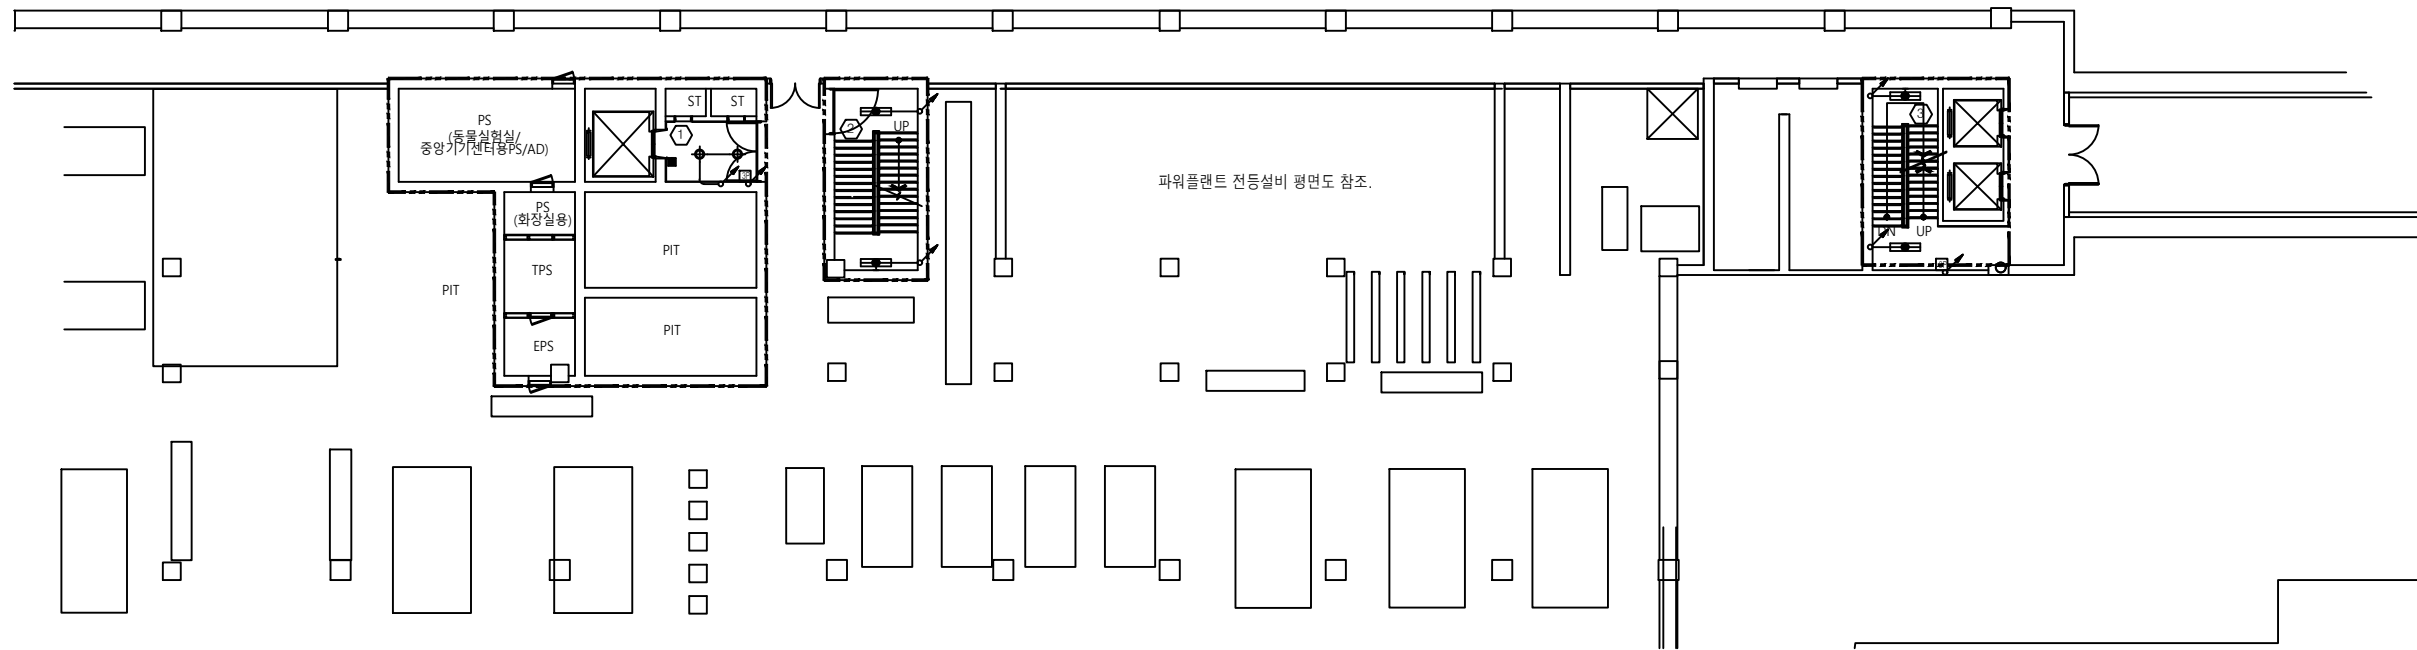
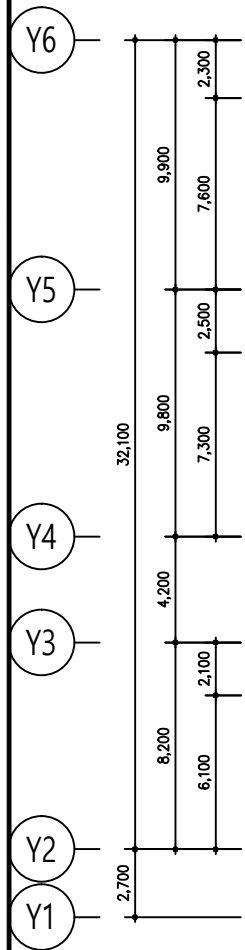
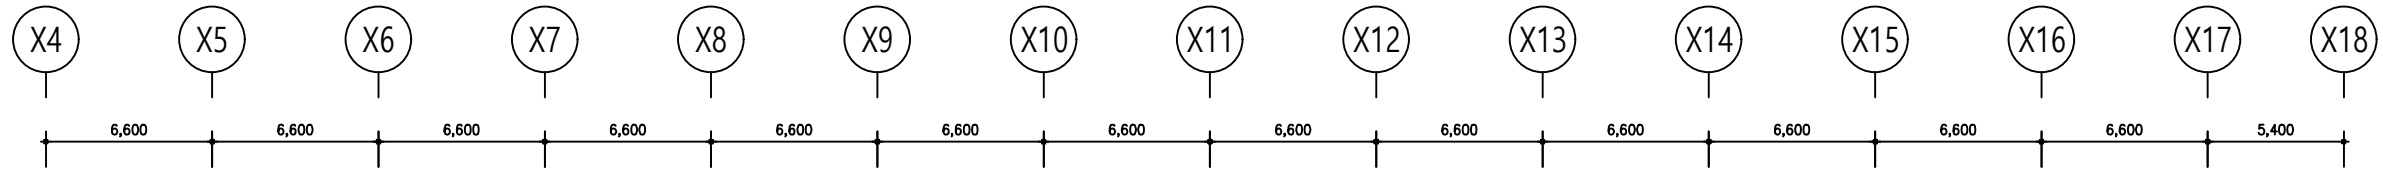


3				
2				
1	14.11.19	실명/호실 수정		
REV	DATE	DESCRIPTION	DRN	CHK

DRAWING TITLE
신물질과학부
지하 2층 전등설비 평면도

APPROVED

CHECKED1

CHECKED2




DRAWN

PROJECT NO.

SCALE	APPROVAL DATE
A1 1/150 A3 1/300	2014.04

DRAWING NO.	REV.
E-11-0701	

신물질과학부 지하2층 전등설비 평면도
축척 A1: 1/150, A3: 1/300

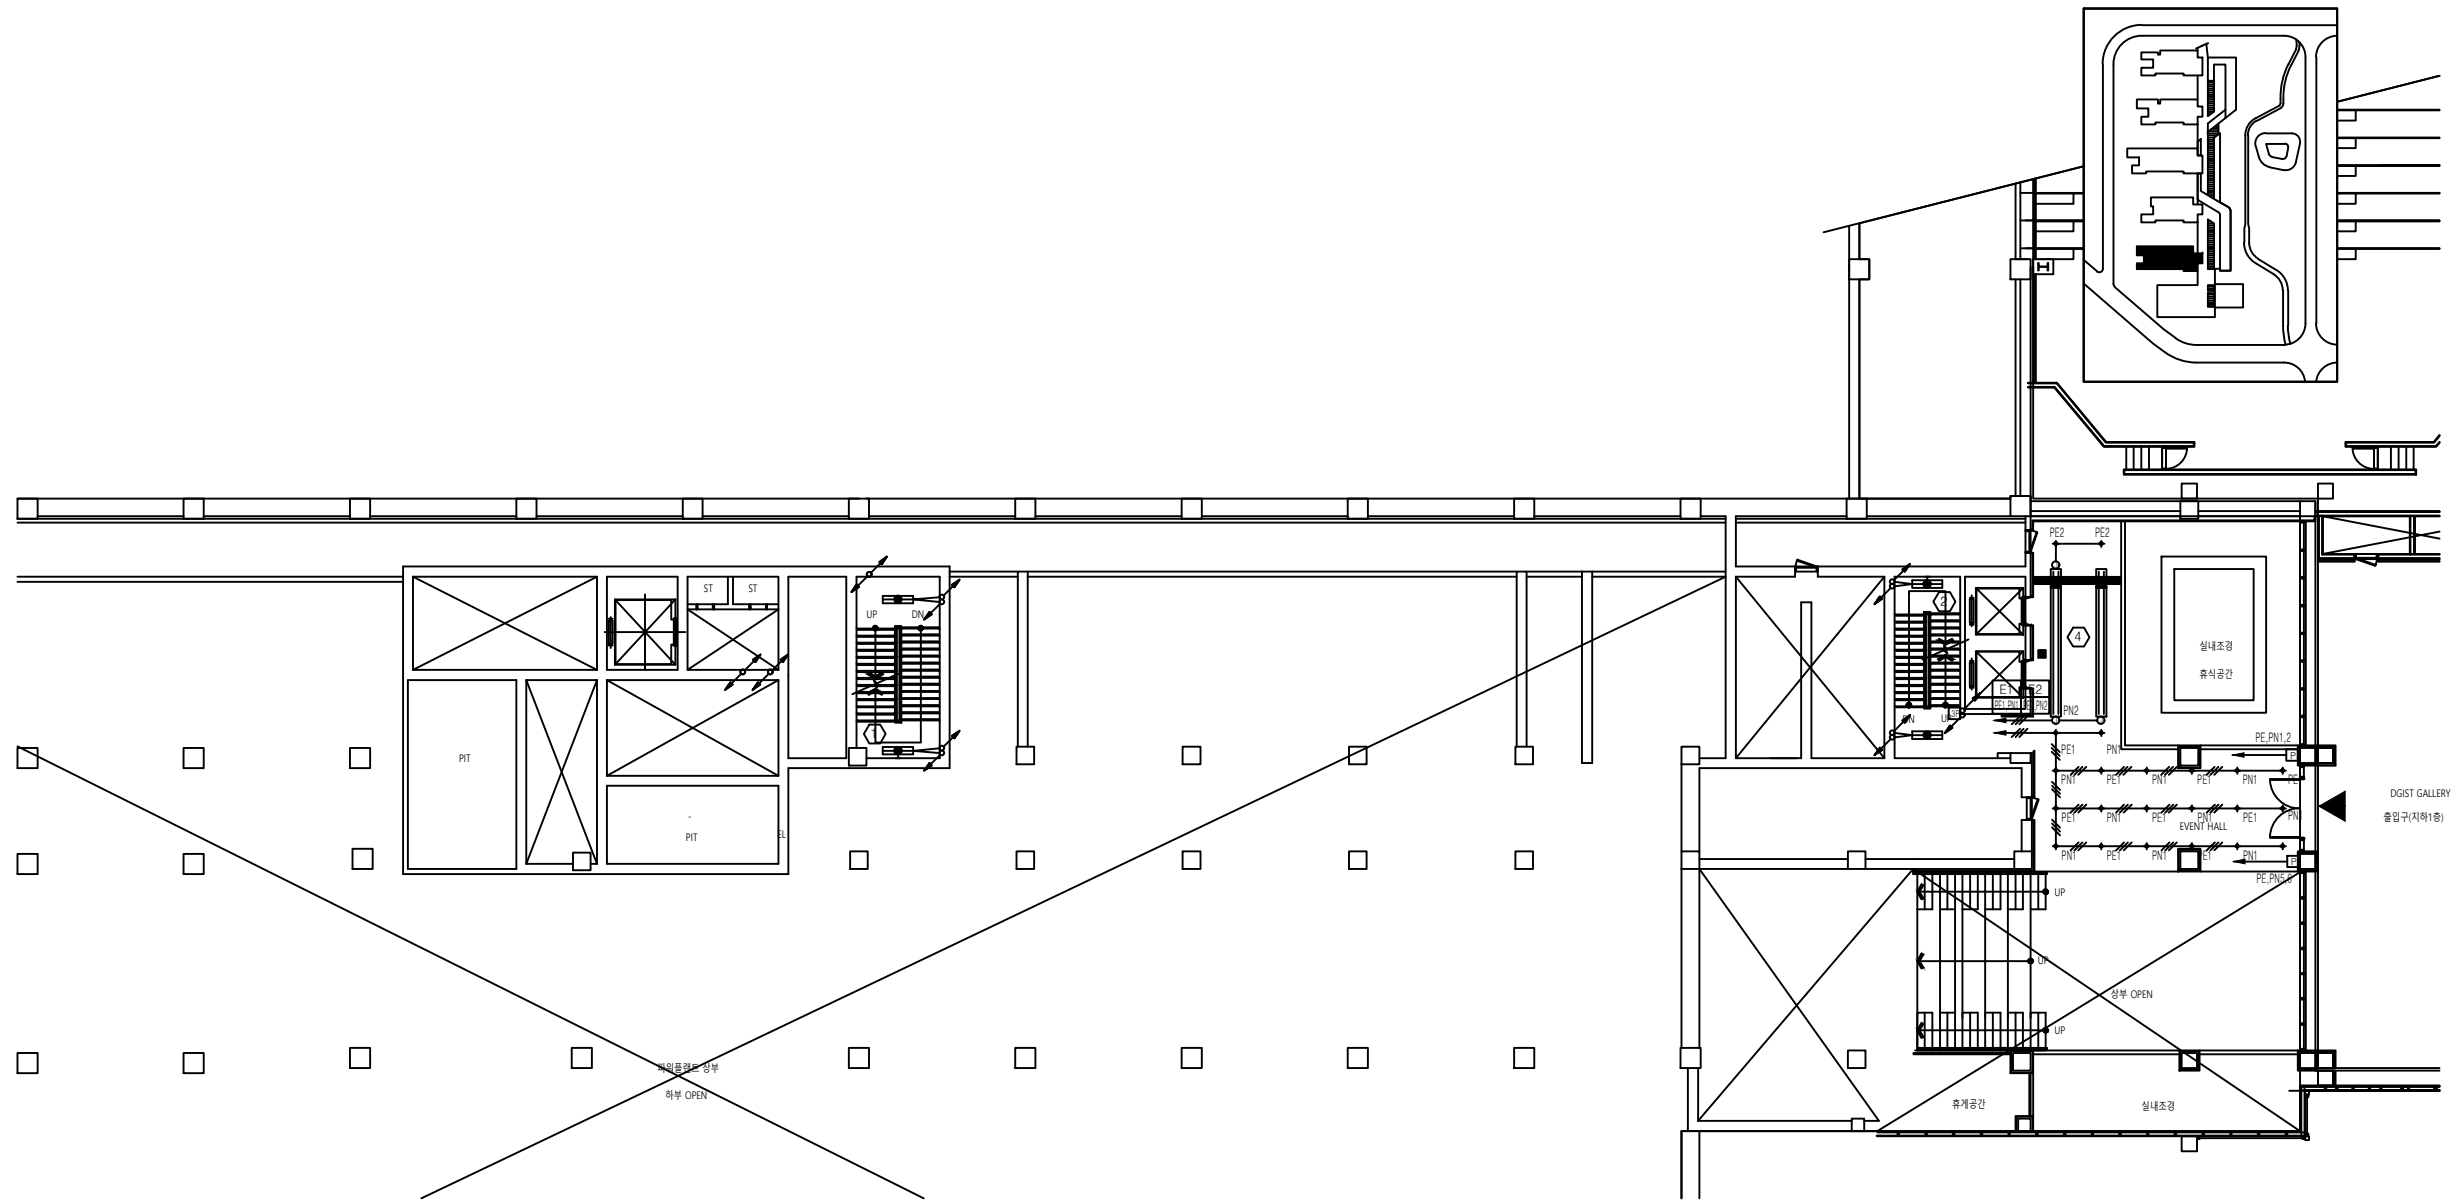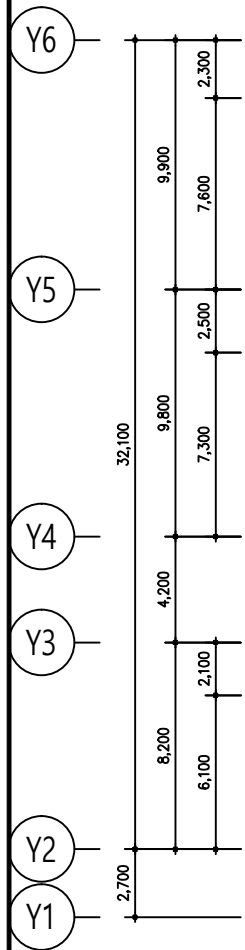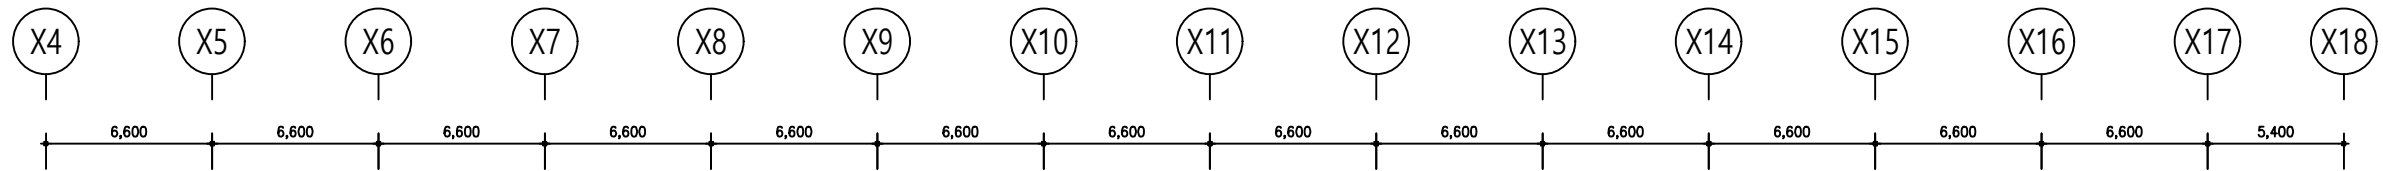

3				
2				
1	14.11.19	실명/호실 수정		
REV	DATE	DESCRIPTION	DRN	CHK

DRAWING TITLE

신물질과학부
지하 1층 전등설비 평면도

APPROVED

CHECKED1

CHECKED2

DRAWN

PROJECT NO.


SCALE

APPROVAL DATE

1/150 1/300 2014.04


DRAWING NO. REV.

E-11-0702

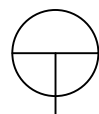



신물질과학부 지하1층 전등설비 평면도

축척 A1: 1/150, A3: 1/300

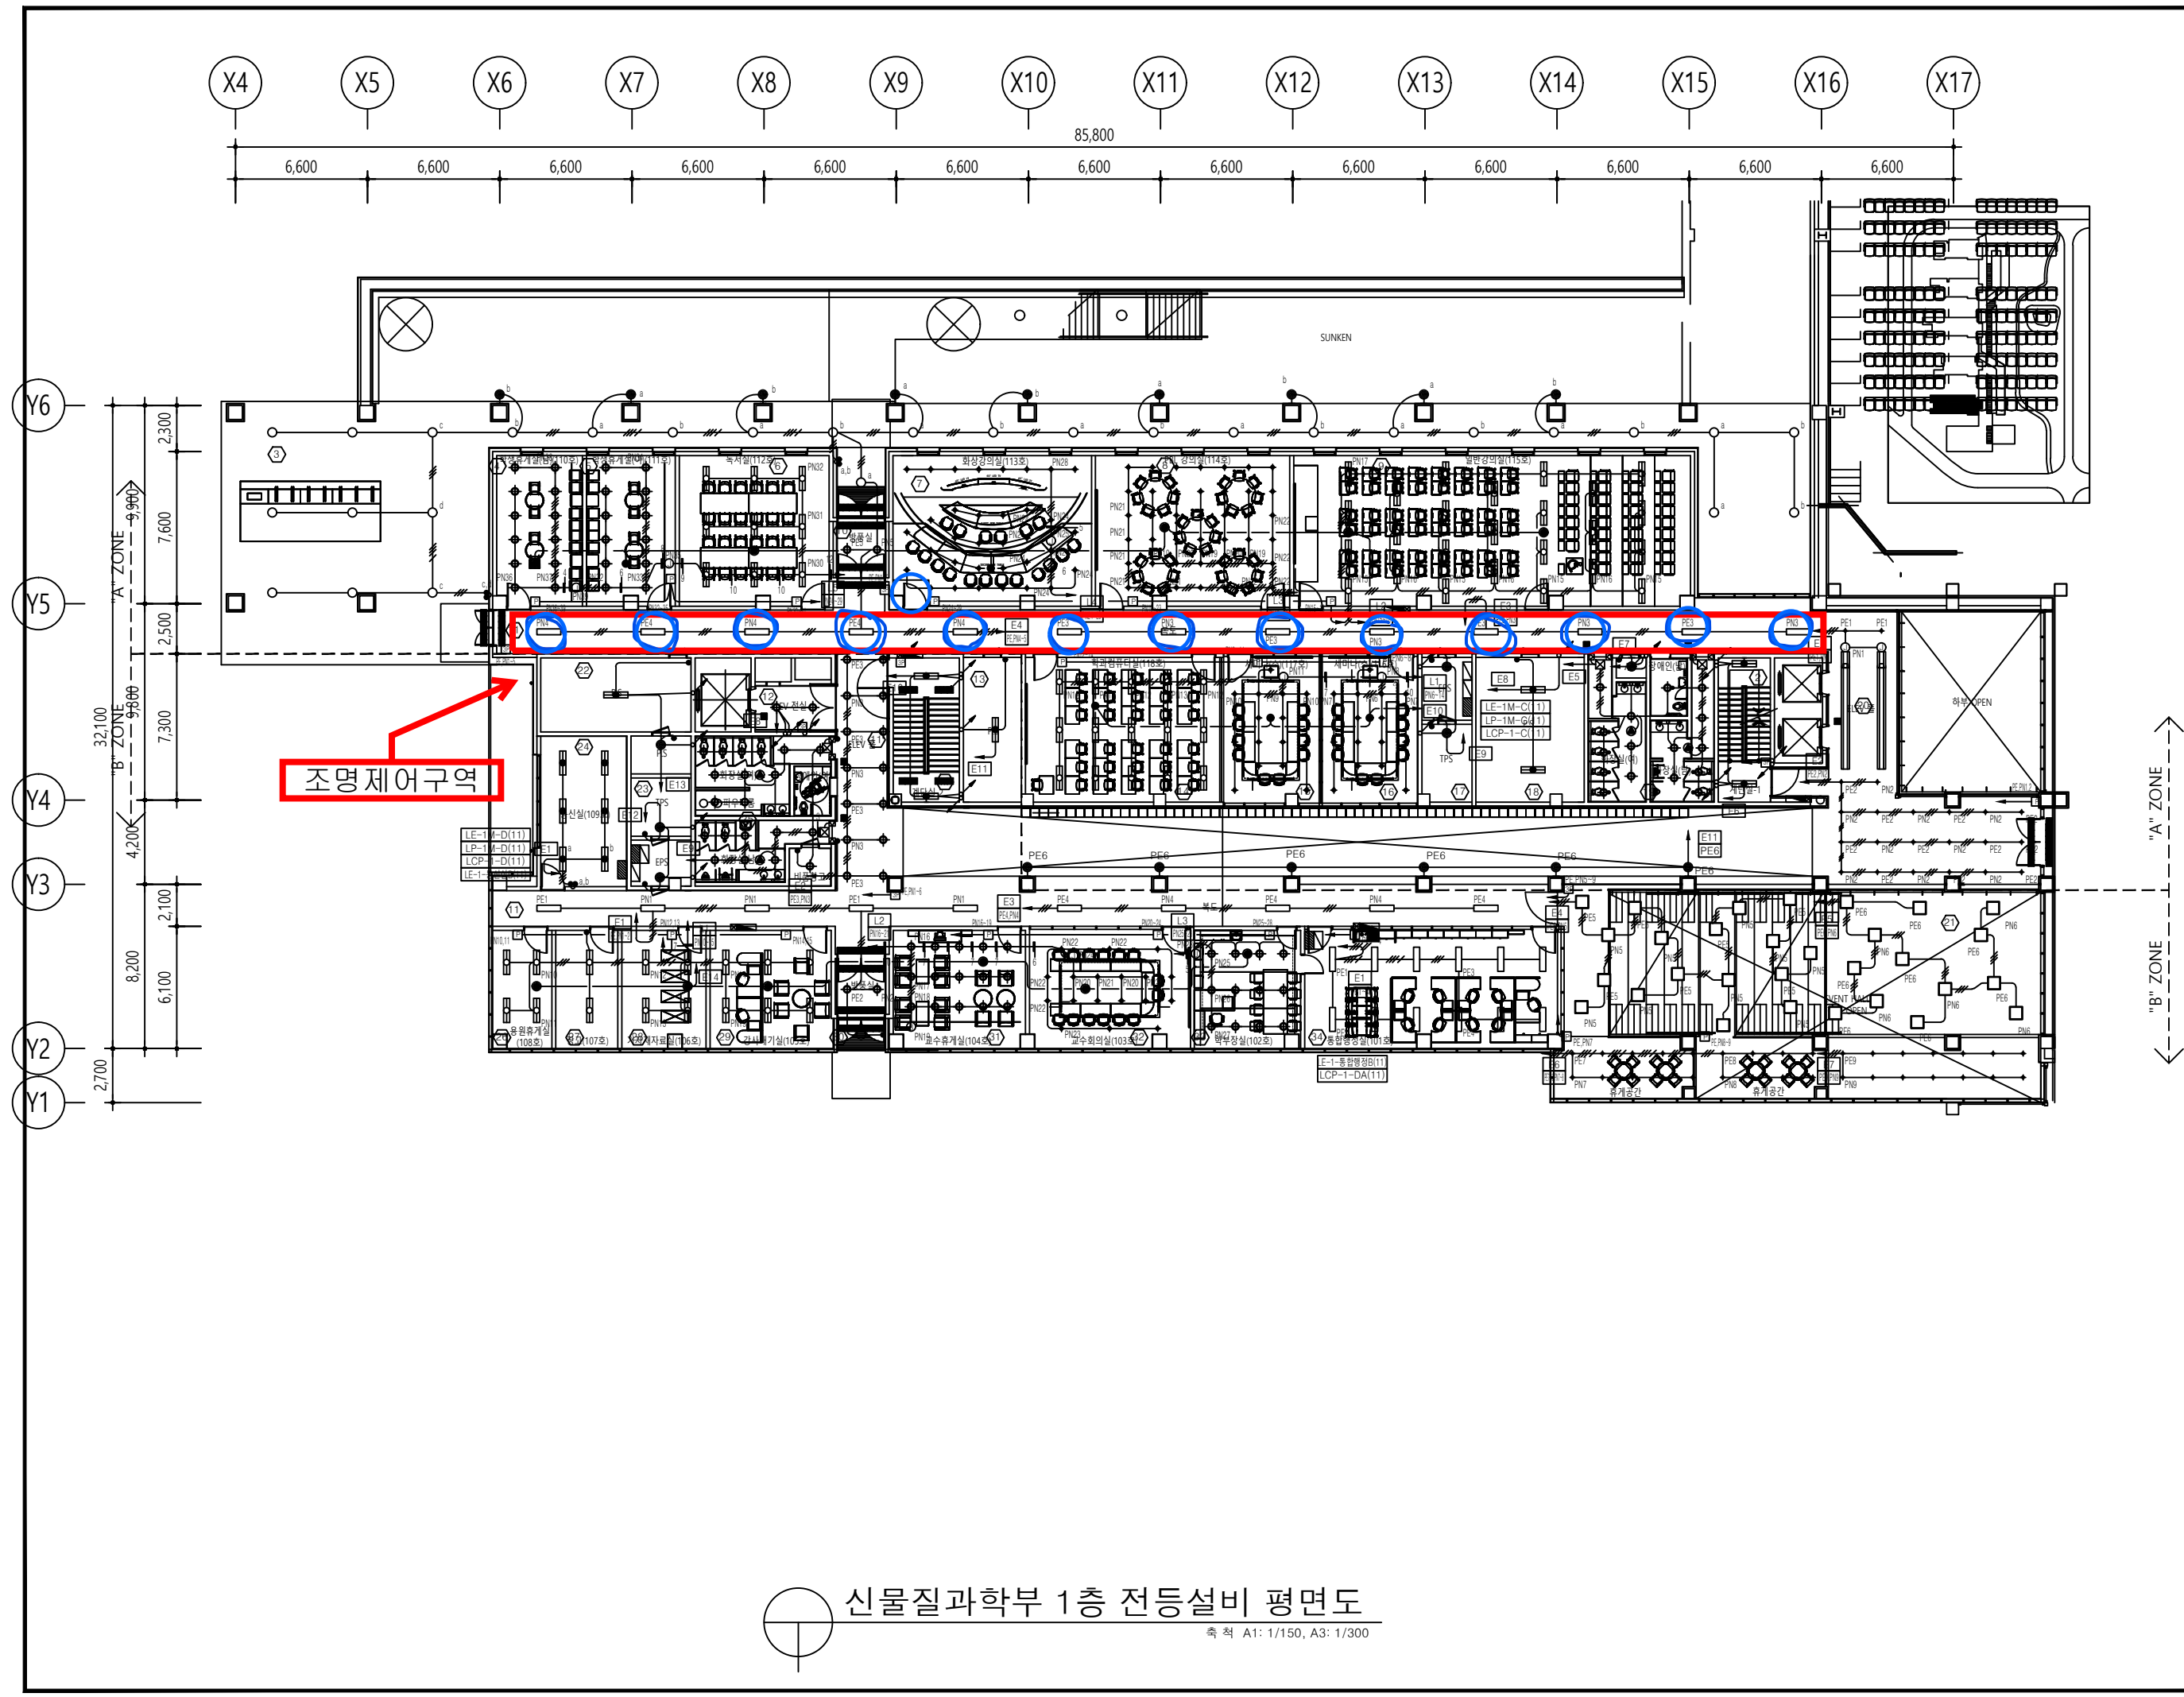


신물질과학부 1층 전등설비 평면도
 축척 A1: 1/150, A3: 1/300

3					
2					
1	14.11.19	실명/호실 수정			
REV	DATE	DESCRIPTION	DRN	CHK	APR
DRAWING TITLE					
신물질과학부 1층 전등설비 평면도					
APPROVED					
CHECKED1					
CHECKED2					
DRAWN					
PROJECT NO.					
SCALE			APPROVAL DATE		
A1	1/150	A3	1/300	2014.04	
DRAWING NO.					REV.
E-11-0703					

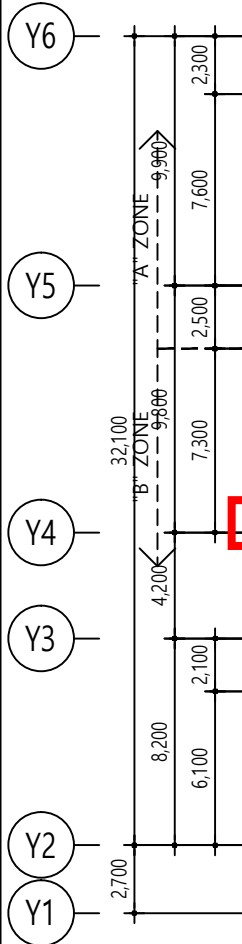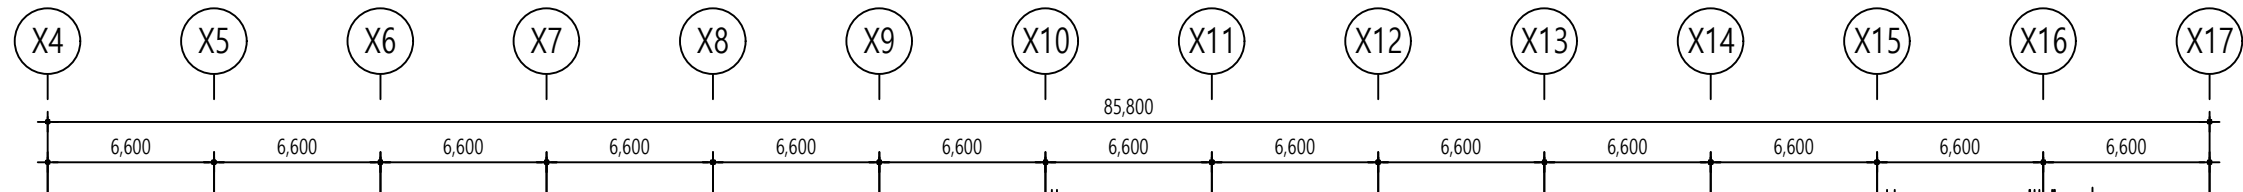


조명제어구역

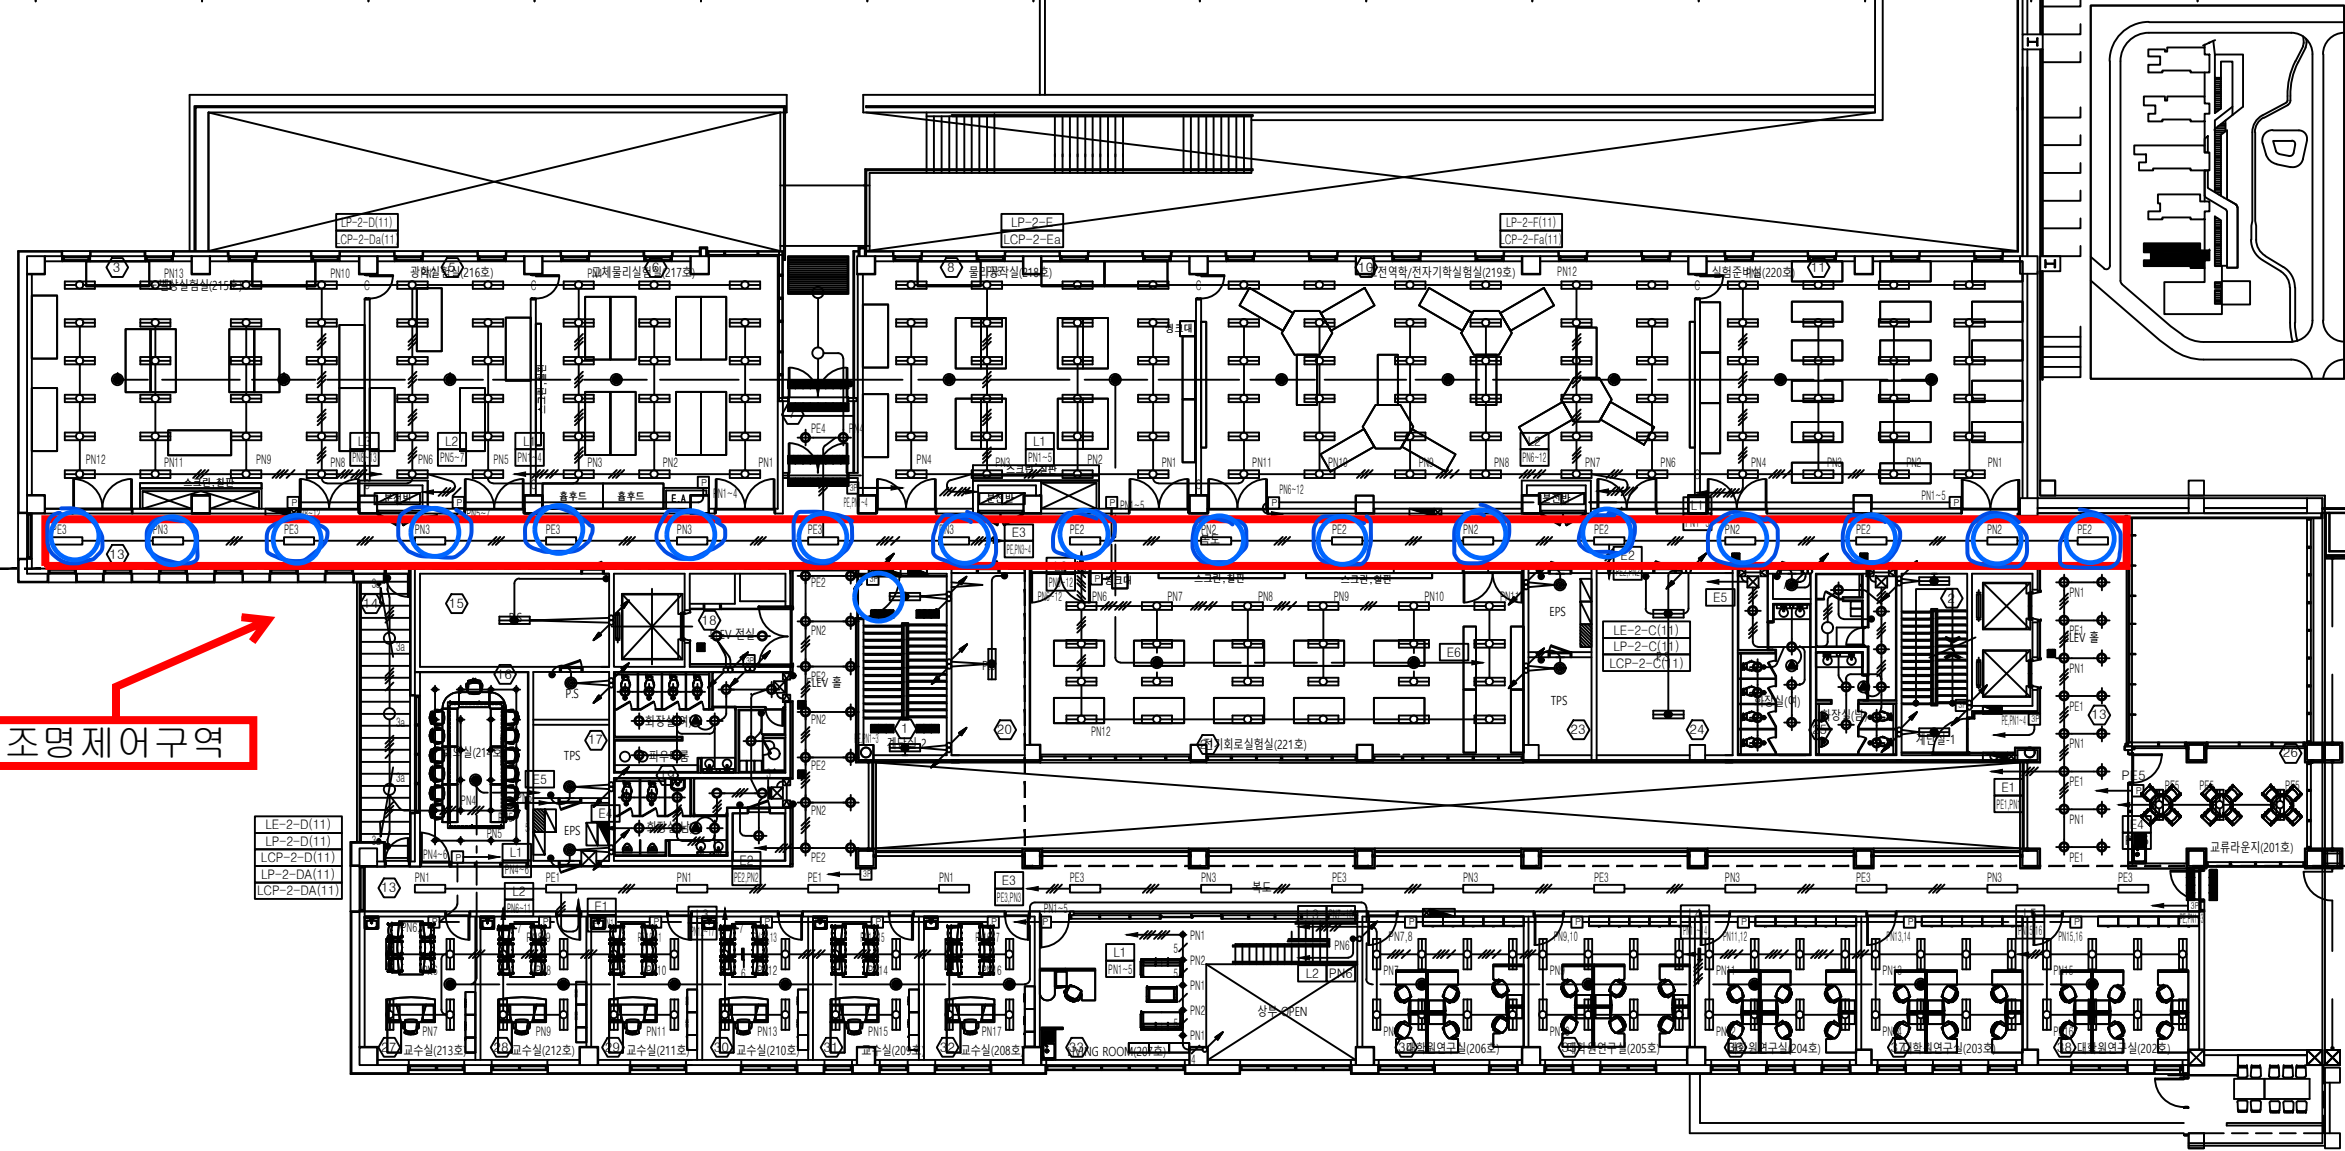


신물질과학부 2층 전등설비 평면도
축척 A1: 1/150, A3: 1/300

3					
2					
1	14.11.19	설명/호실 수정			
REV	DATE	DESCRIPTION	DRN	CHK	APR
DRAWING TITLE					
신물질과학부 2층 전등설비 평면도					
APPROVED					
CHECKED1					
CHECKED2					
DRAWN					
PROJECT NO.					
SCALE			APPROVAL DATE		
A1	1/150	A3	1/300	2014.04	
DRAWING NO.					REV.
E-11-0704					

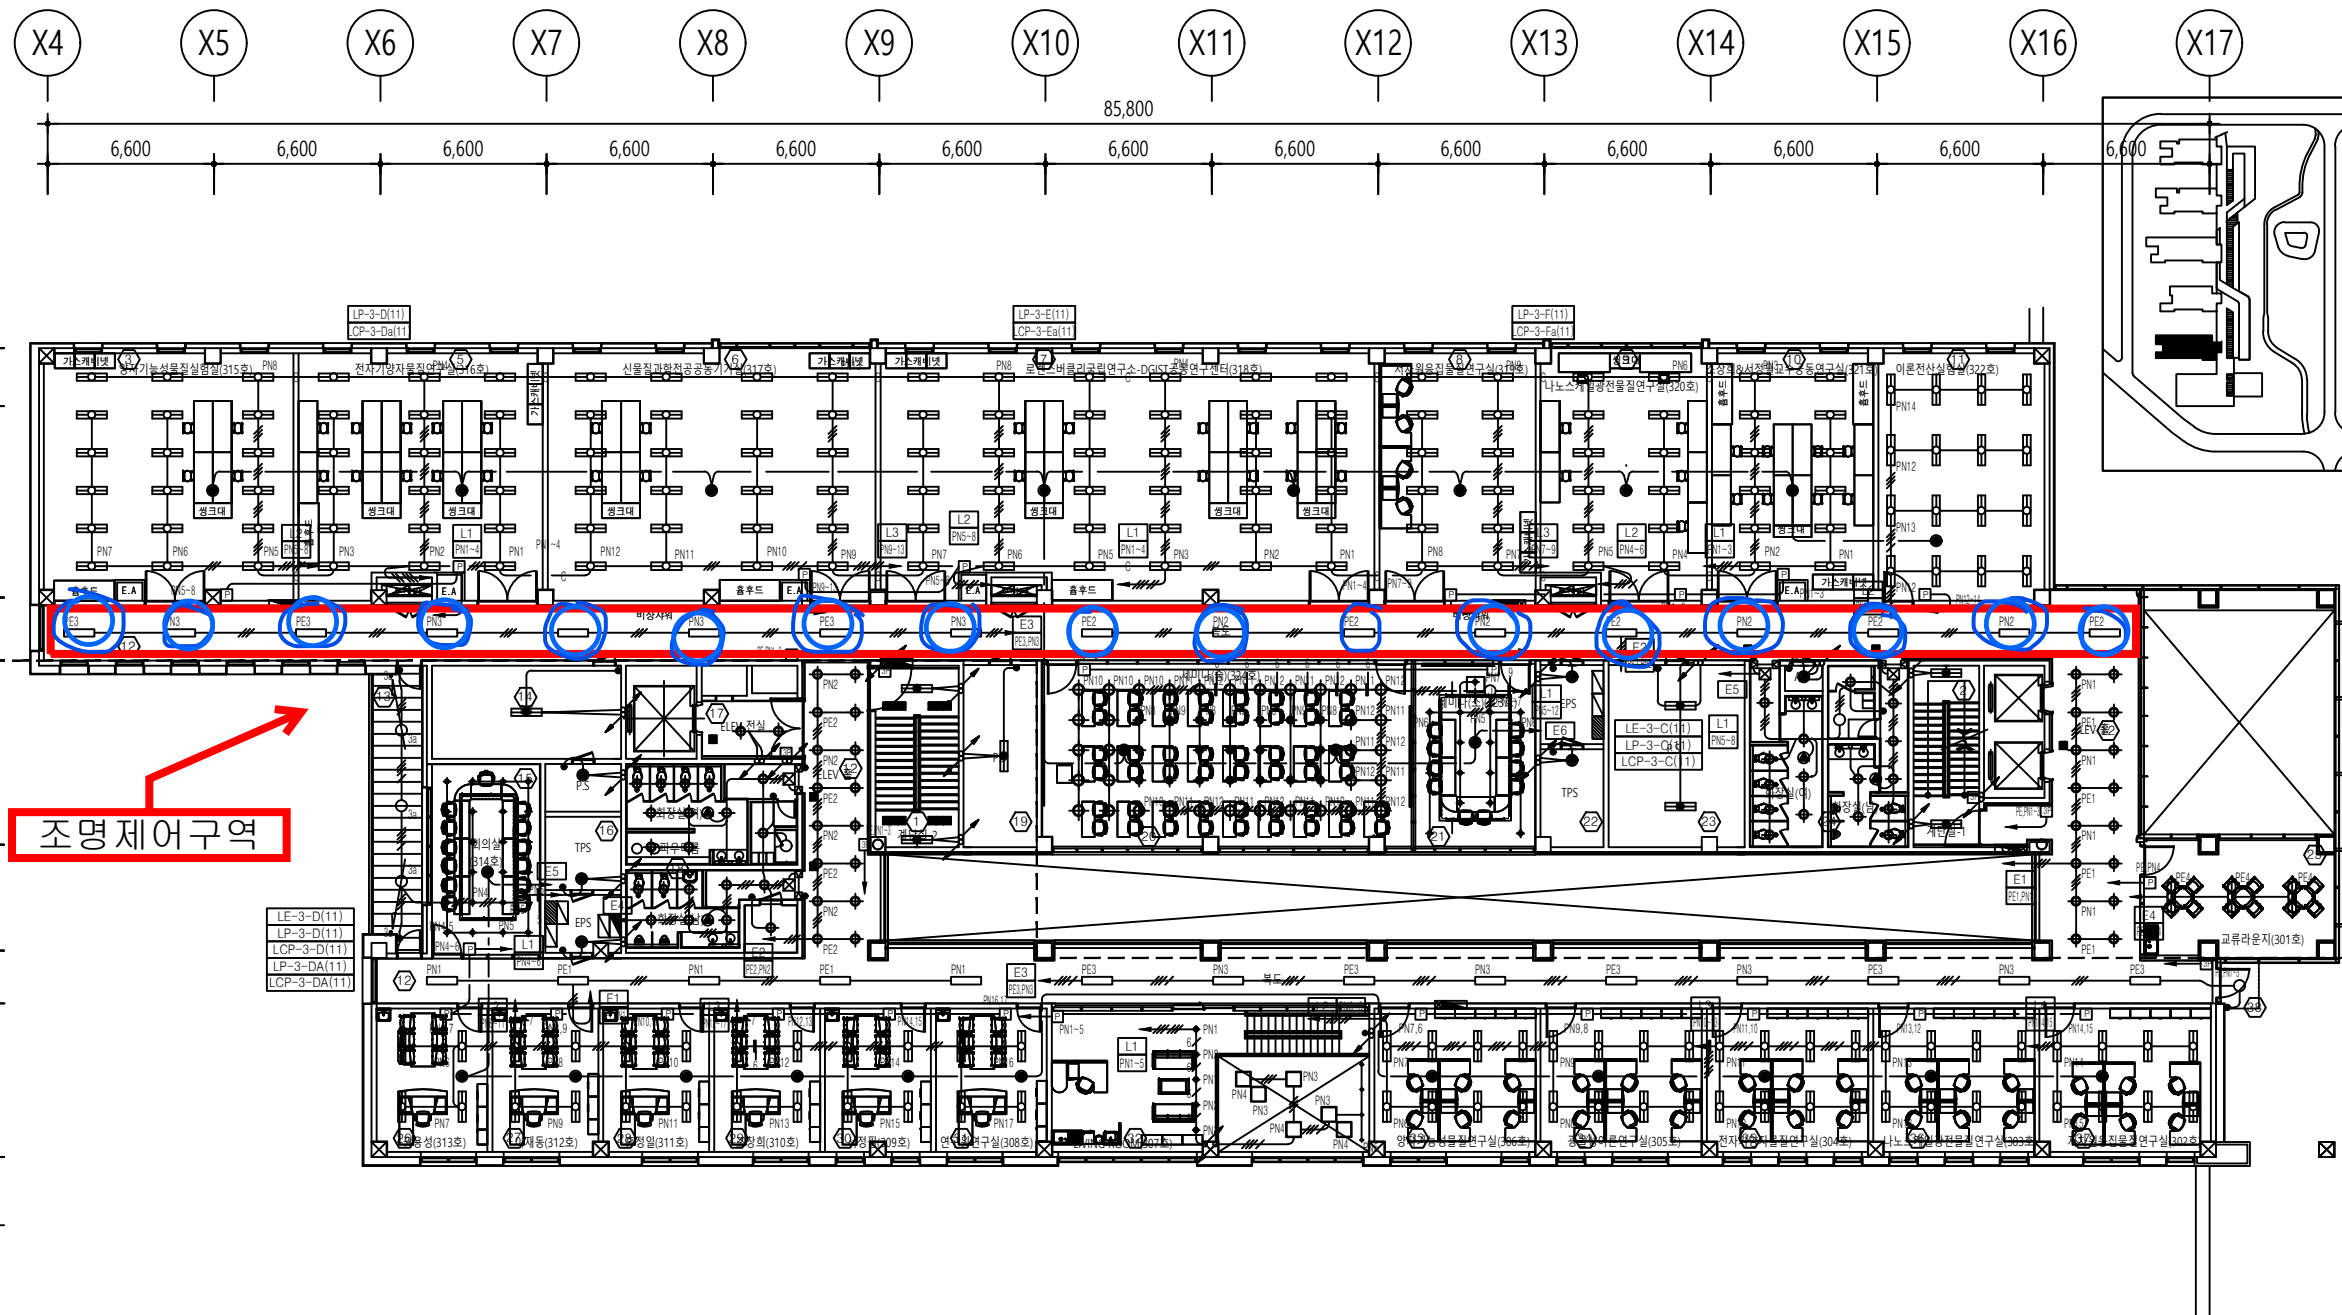

조명제어구역

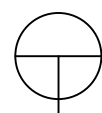

신물질과학부 3층 전등설비 평면도

축척 A1: 1/150, A3: 1/300

학위과정시설 임대형민자사업(BTL)

Construction

現代建設

TEL. 053)615-5093~6 FAX. 053)615-5097

Construction Management

SAMOOO.C.M.
Construction Management

TEL. 053)811-3071 FAX. 053)811-3073

NOTE

1. 시험실내의 전등설비용 공배관 설치.
: EMPTY PIPE (CD 22C)

3					
2					
1	14.11.19	실명/호실 수정			
REV	DATE	DESCRIPTION	DRN	CHK	APR

DRAWING TITLE
신물질과학부
3층 전등설비 평면도

APPROVED

CHECKED1




CHECKED2

DRAWN


PROJECT NO.

SCALE	APPROVAL DATE
1/150 1/300	2014.04

DRAWING NO. E-11-0705

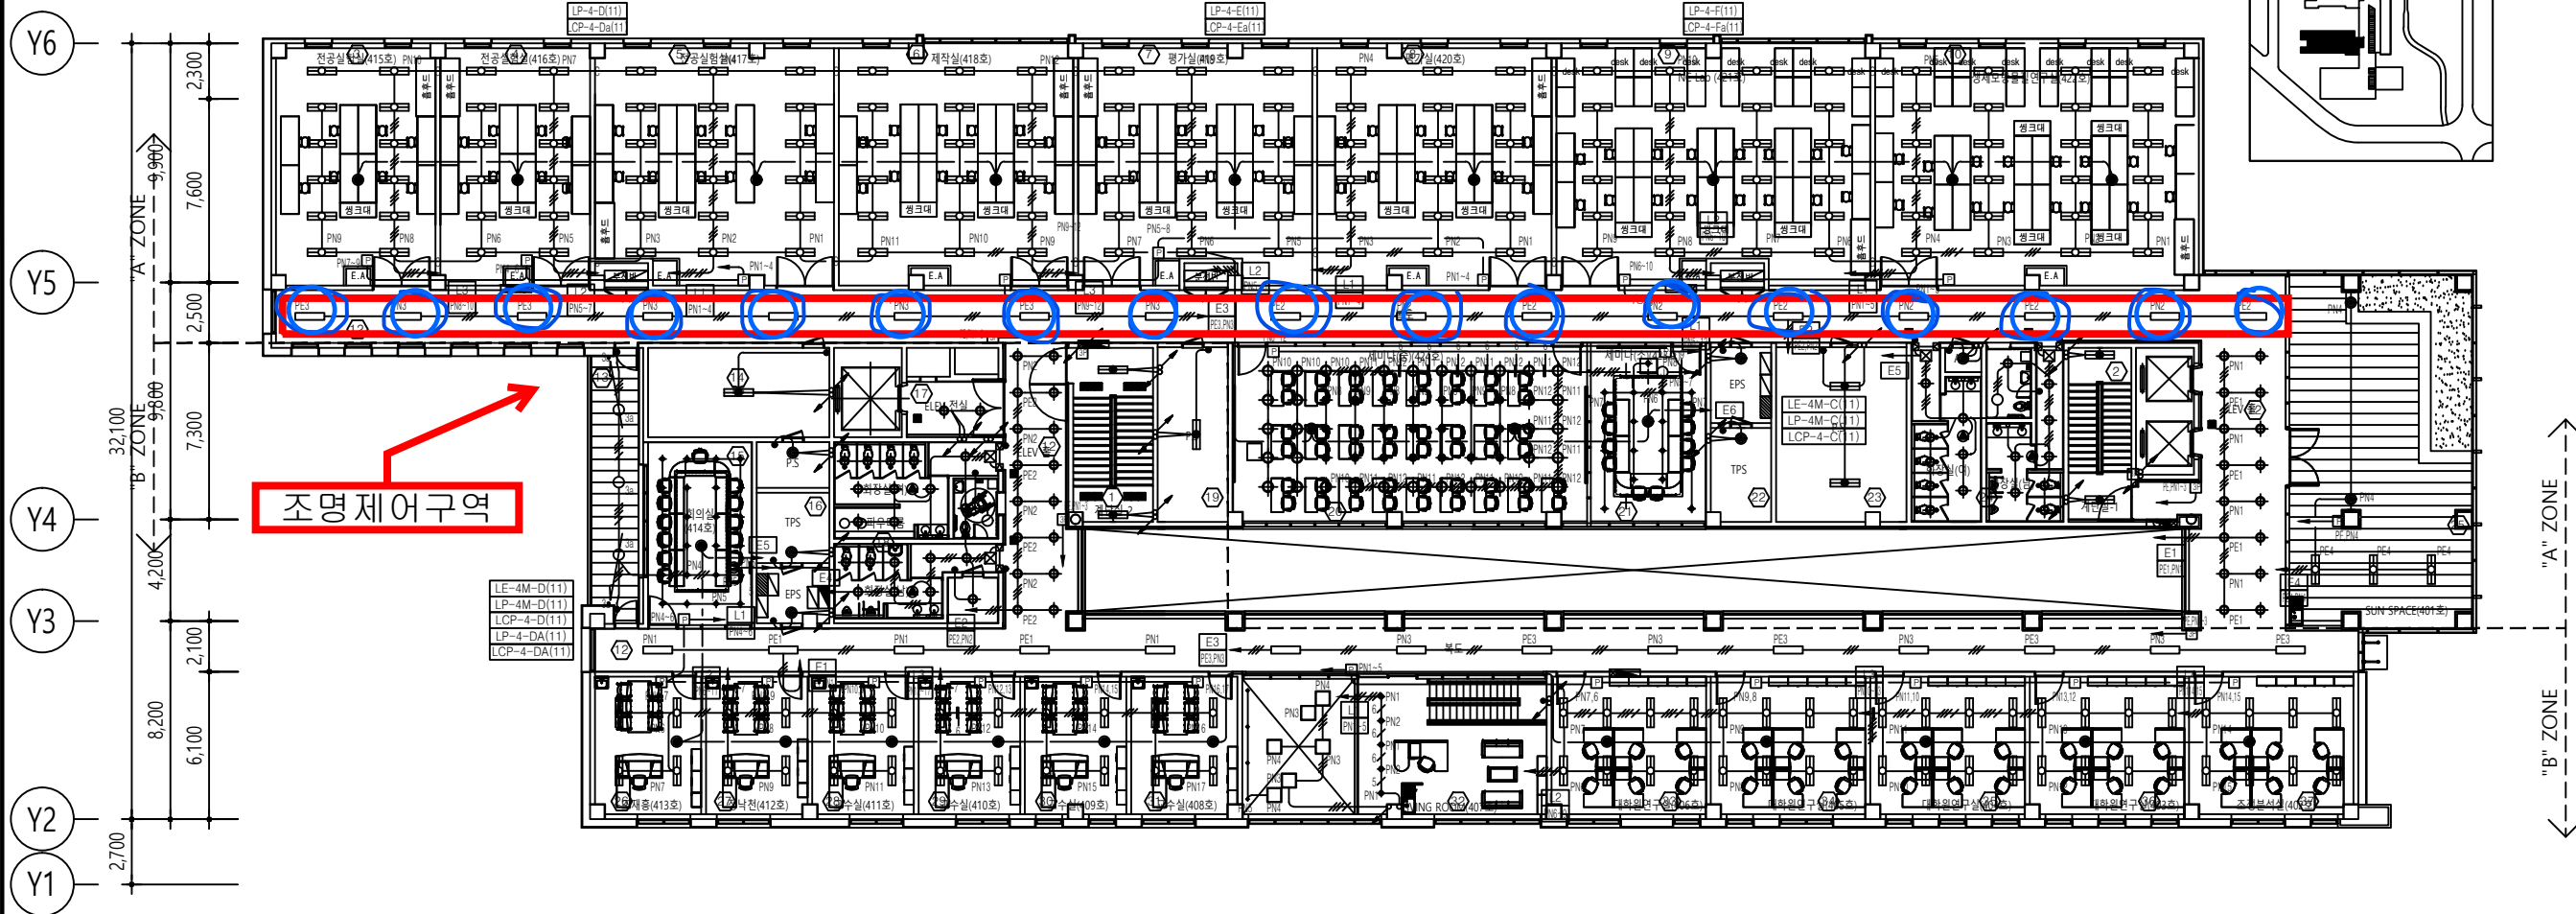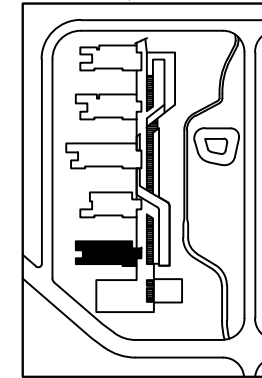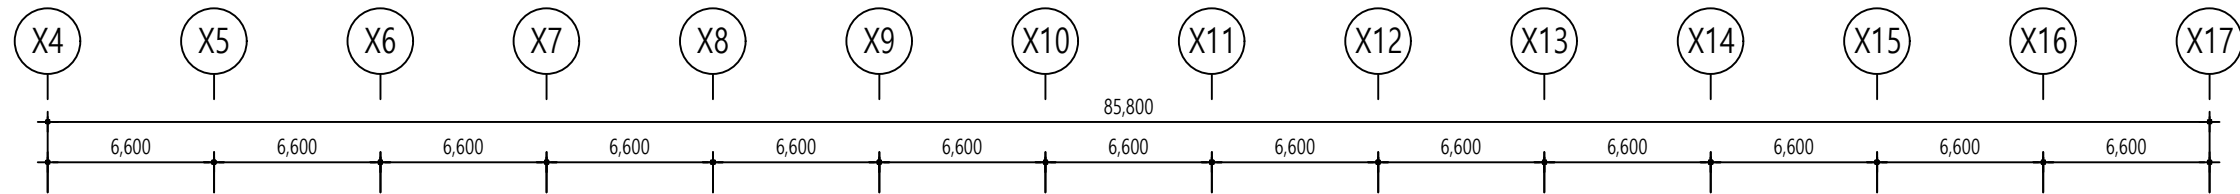

조명제어구역

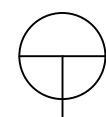

신물질과학부 4층 전등설비 평면도

축척 A1: 1/150, A3: 1/300

3					
2					
1	14.11.19	실명/호실 수정			
REV	DATE	DESCRIPTION	DRN	CHK	APR

DRAWING TITLE
신물질과학부
4층 전등설비 평면도

APPROVED

CHECKED1




CHECKED2

DRAWN




PROJECT NO.

SCALE	APPROVAL DATE
A1 1/150 A3 1/300	2014.04


DRAWING NO. E-11-0706 REV.

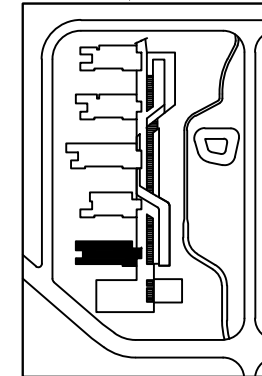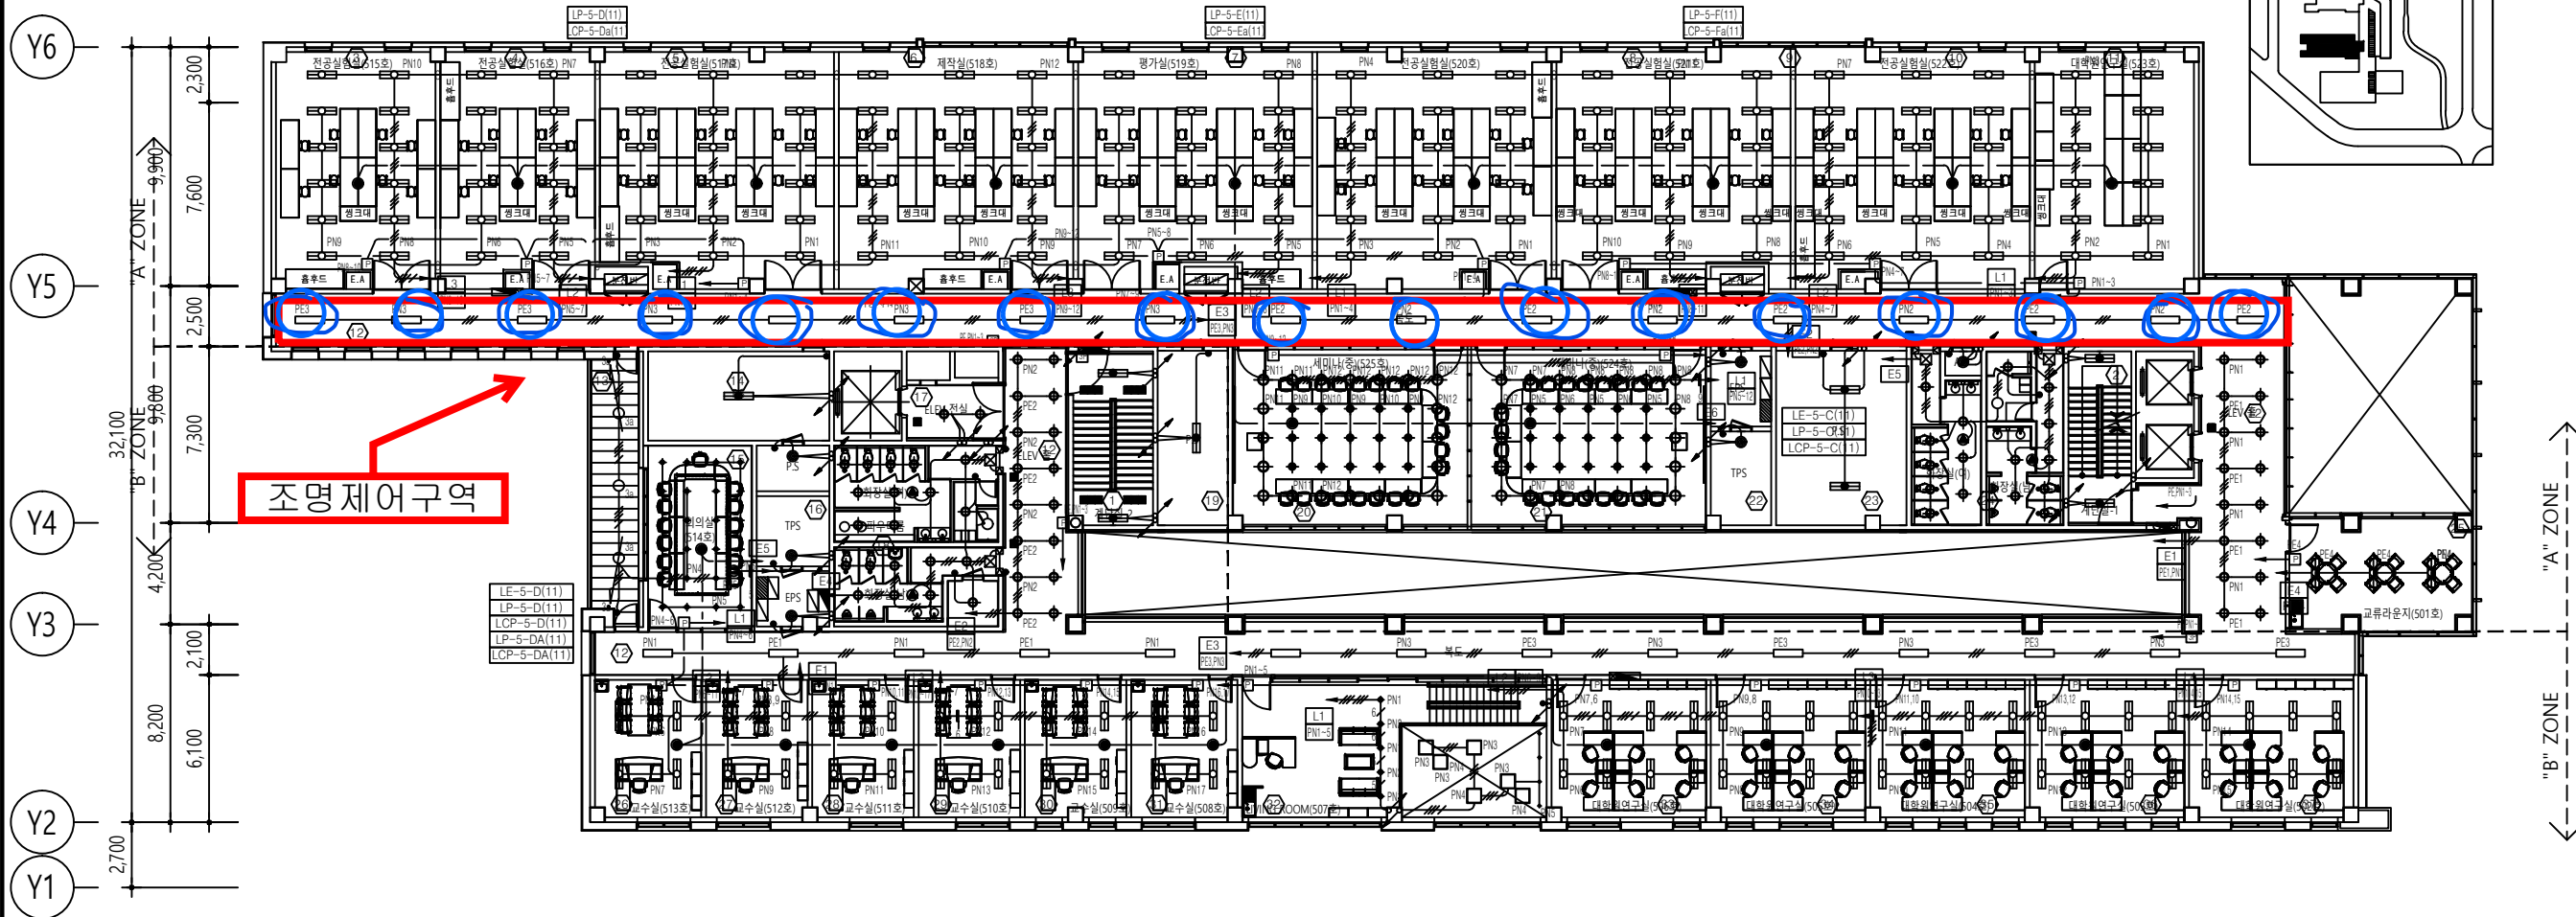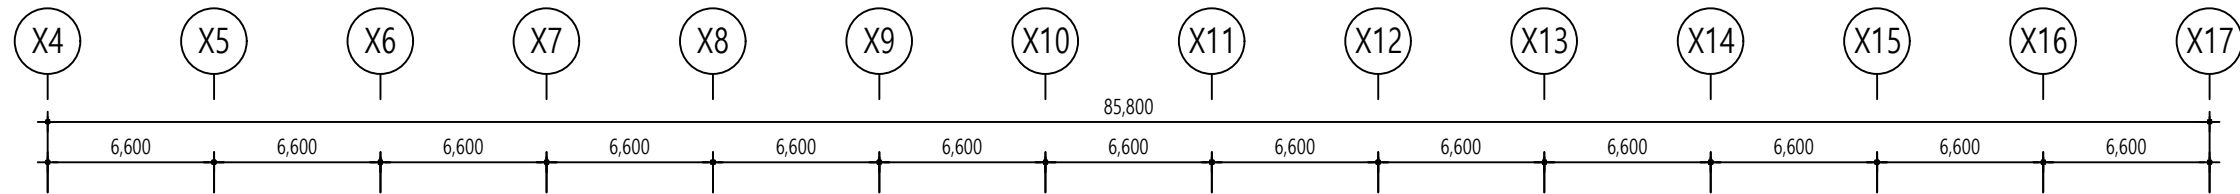

3					
2					
1	14.11.19	실명/호실 수정			
REV	DATE	DESCRIPTION	DRN	CHK	APR
DRAWING TITLE					
신물질과학부 5층 전등설비 평면도					
APPROVED					
CHECKED1					
CHECKED2					
DRAWN					
PROJECT NO.					
SCALE			APPROVAL DATE		
A1	1/150	A3	1/300	2014.04	
DRAWING NO.				REV.	
E-11-0707					

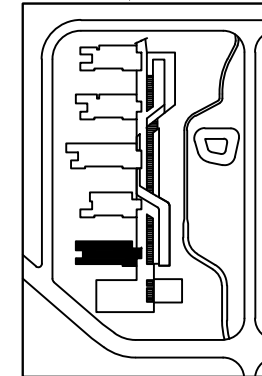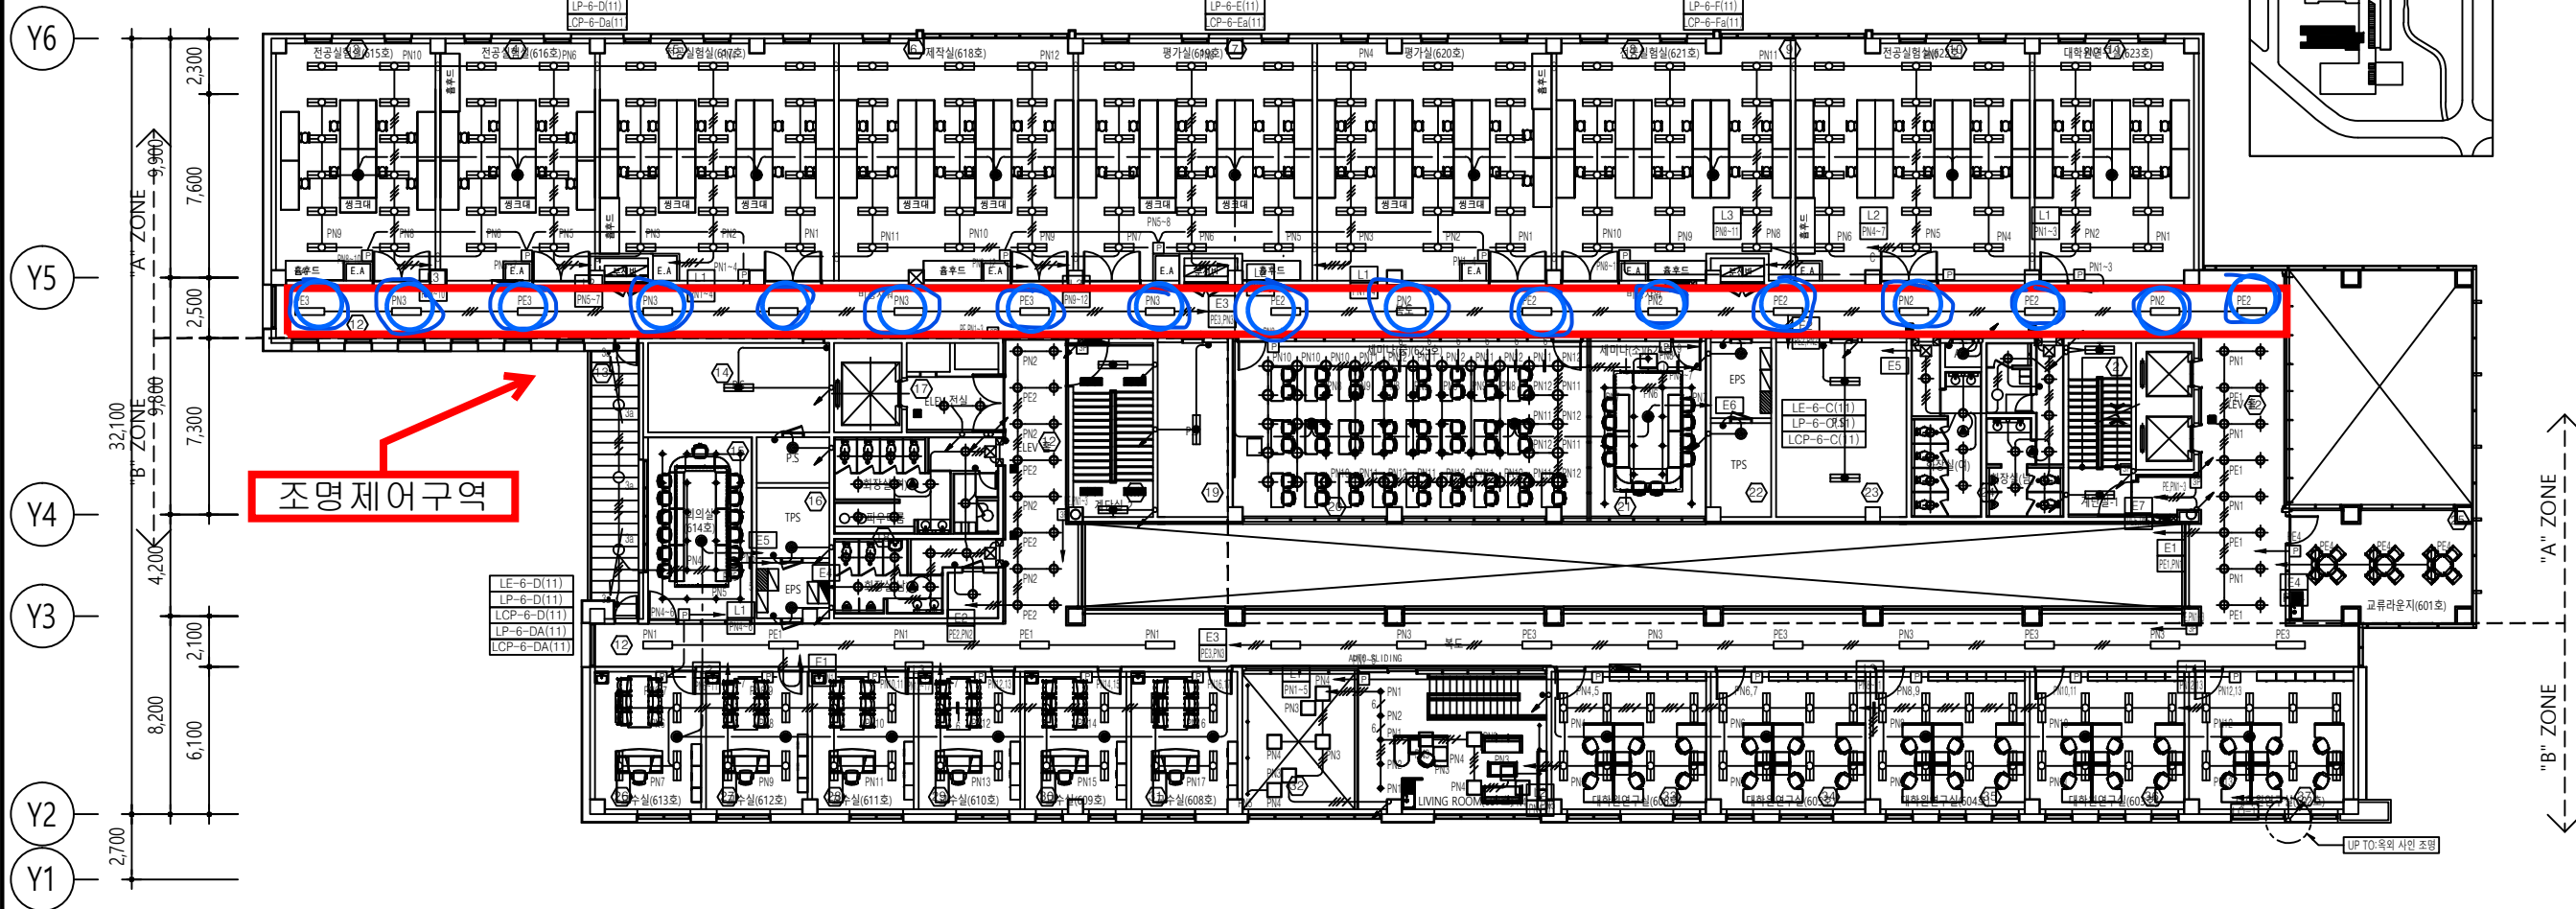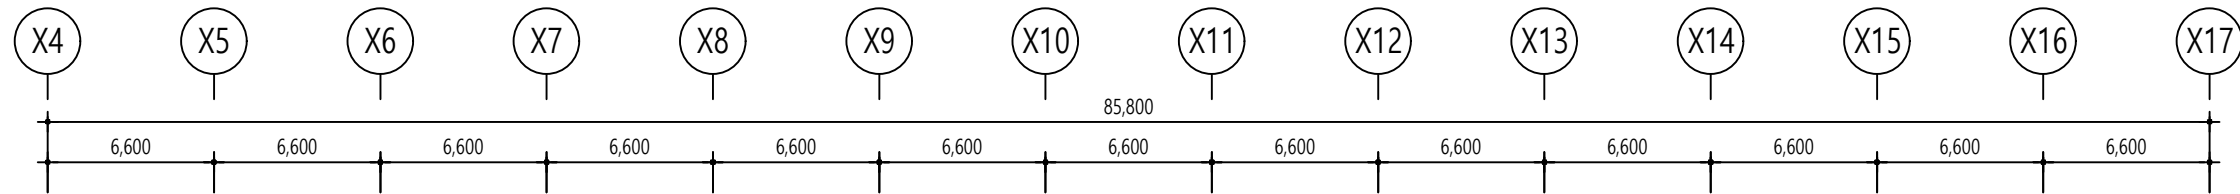

조명 제어구역

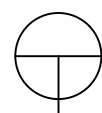

신물질과학부 6층 전등설비 평면도

축척 A1: 1/150, A3: 1/300

3					
2					
1	14.11.19	실명/호실 수정			
REV	DATE	DESCRIPTION	DRN	CHK	APR
DRAWING TITLE					
신물질과학부 6층 전등설비 평면도					
APPROVED					
CHECKED1					
CHECKED2					
DRAWN					
PROJECT NO.					
SCALE			APPROVAL DATE		
A1	1/150	A3	1/300	2014.04	
DRAWING NO.					REV.
E-11-0708					

