
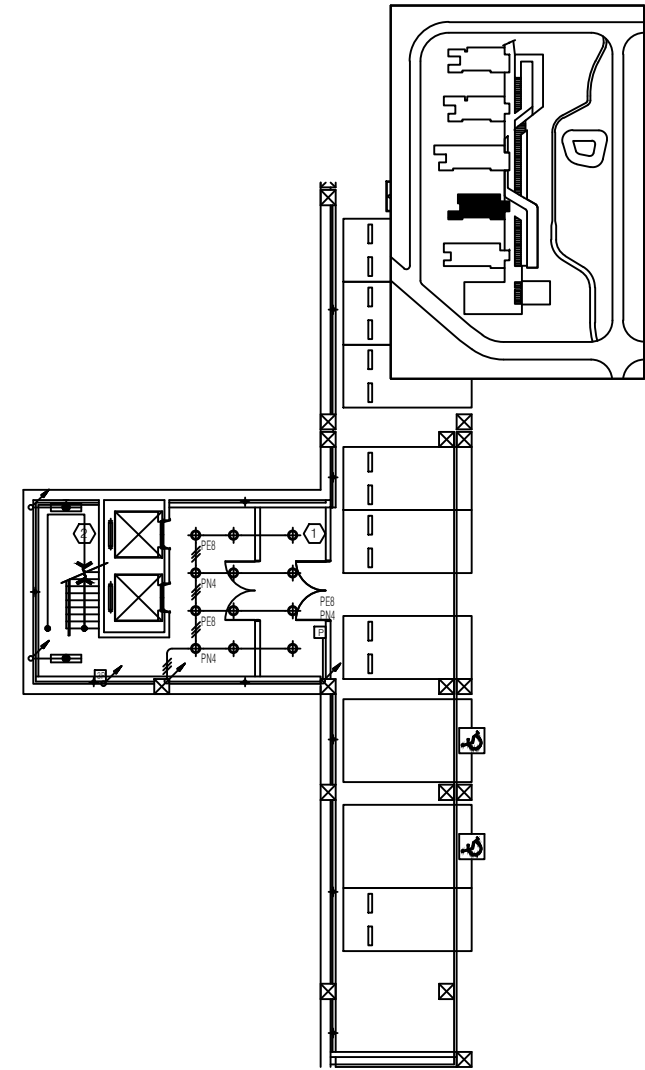
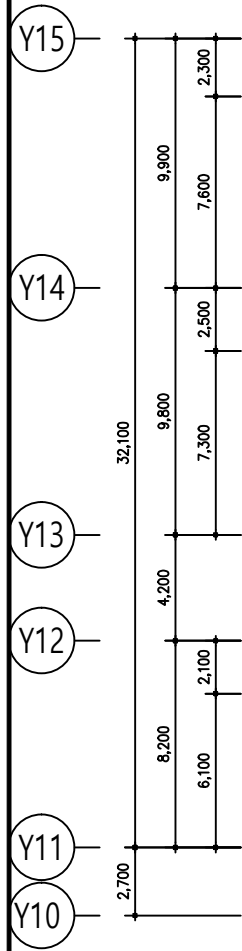


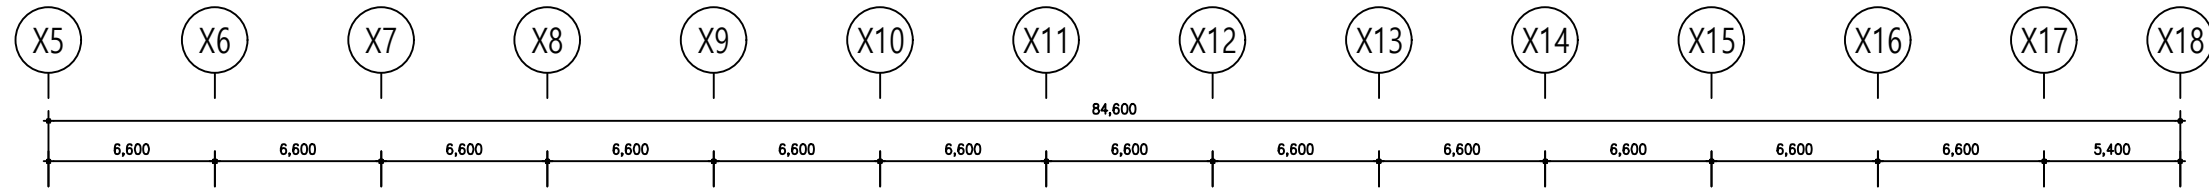

학위과정시설 임대형민자사업(BTL)

Construction

現代建設

TEL. 053)615-5093~6 FAX. 053)615-5097

Construction Management

SAMOOO.C.M.
Construction Management

TEL. 053)611-3071 FAX. 053)611-3073

NOTE

1. 시험실내의 전등설비용 공배관 설치.
— : EMPTY PIPE (CD 22C)

3					
2					
1	14.11.19	실명/호실 수정			
REV	DATE	DESCRIPTION	DRN	CHK	APR

DRAWING TITLE
정보통신융합공학부
지하1층 전등설비 평면도

APPROVED

CHECKED1


CHECKED2

DRAWN

PROJECT NO.


SCALE	APPROVAL DATE
A1 1/150 A3 1/300	2014.04

DRAWING NO. E-12-0701 REV.

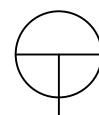

정보통신융합공학부 지하1층 전등설비 평면도

축척 A1: 1/150, A3: 1/300

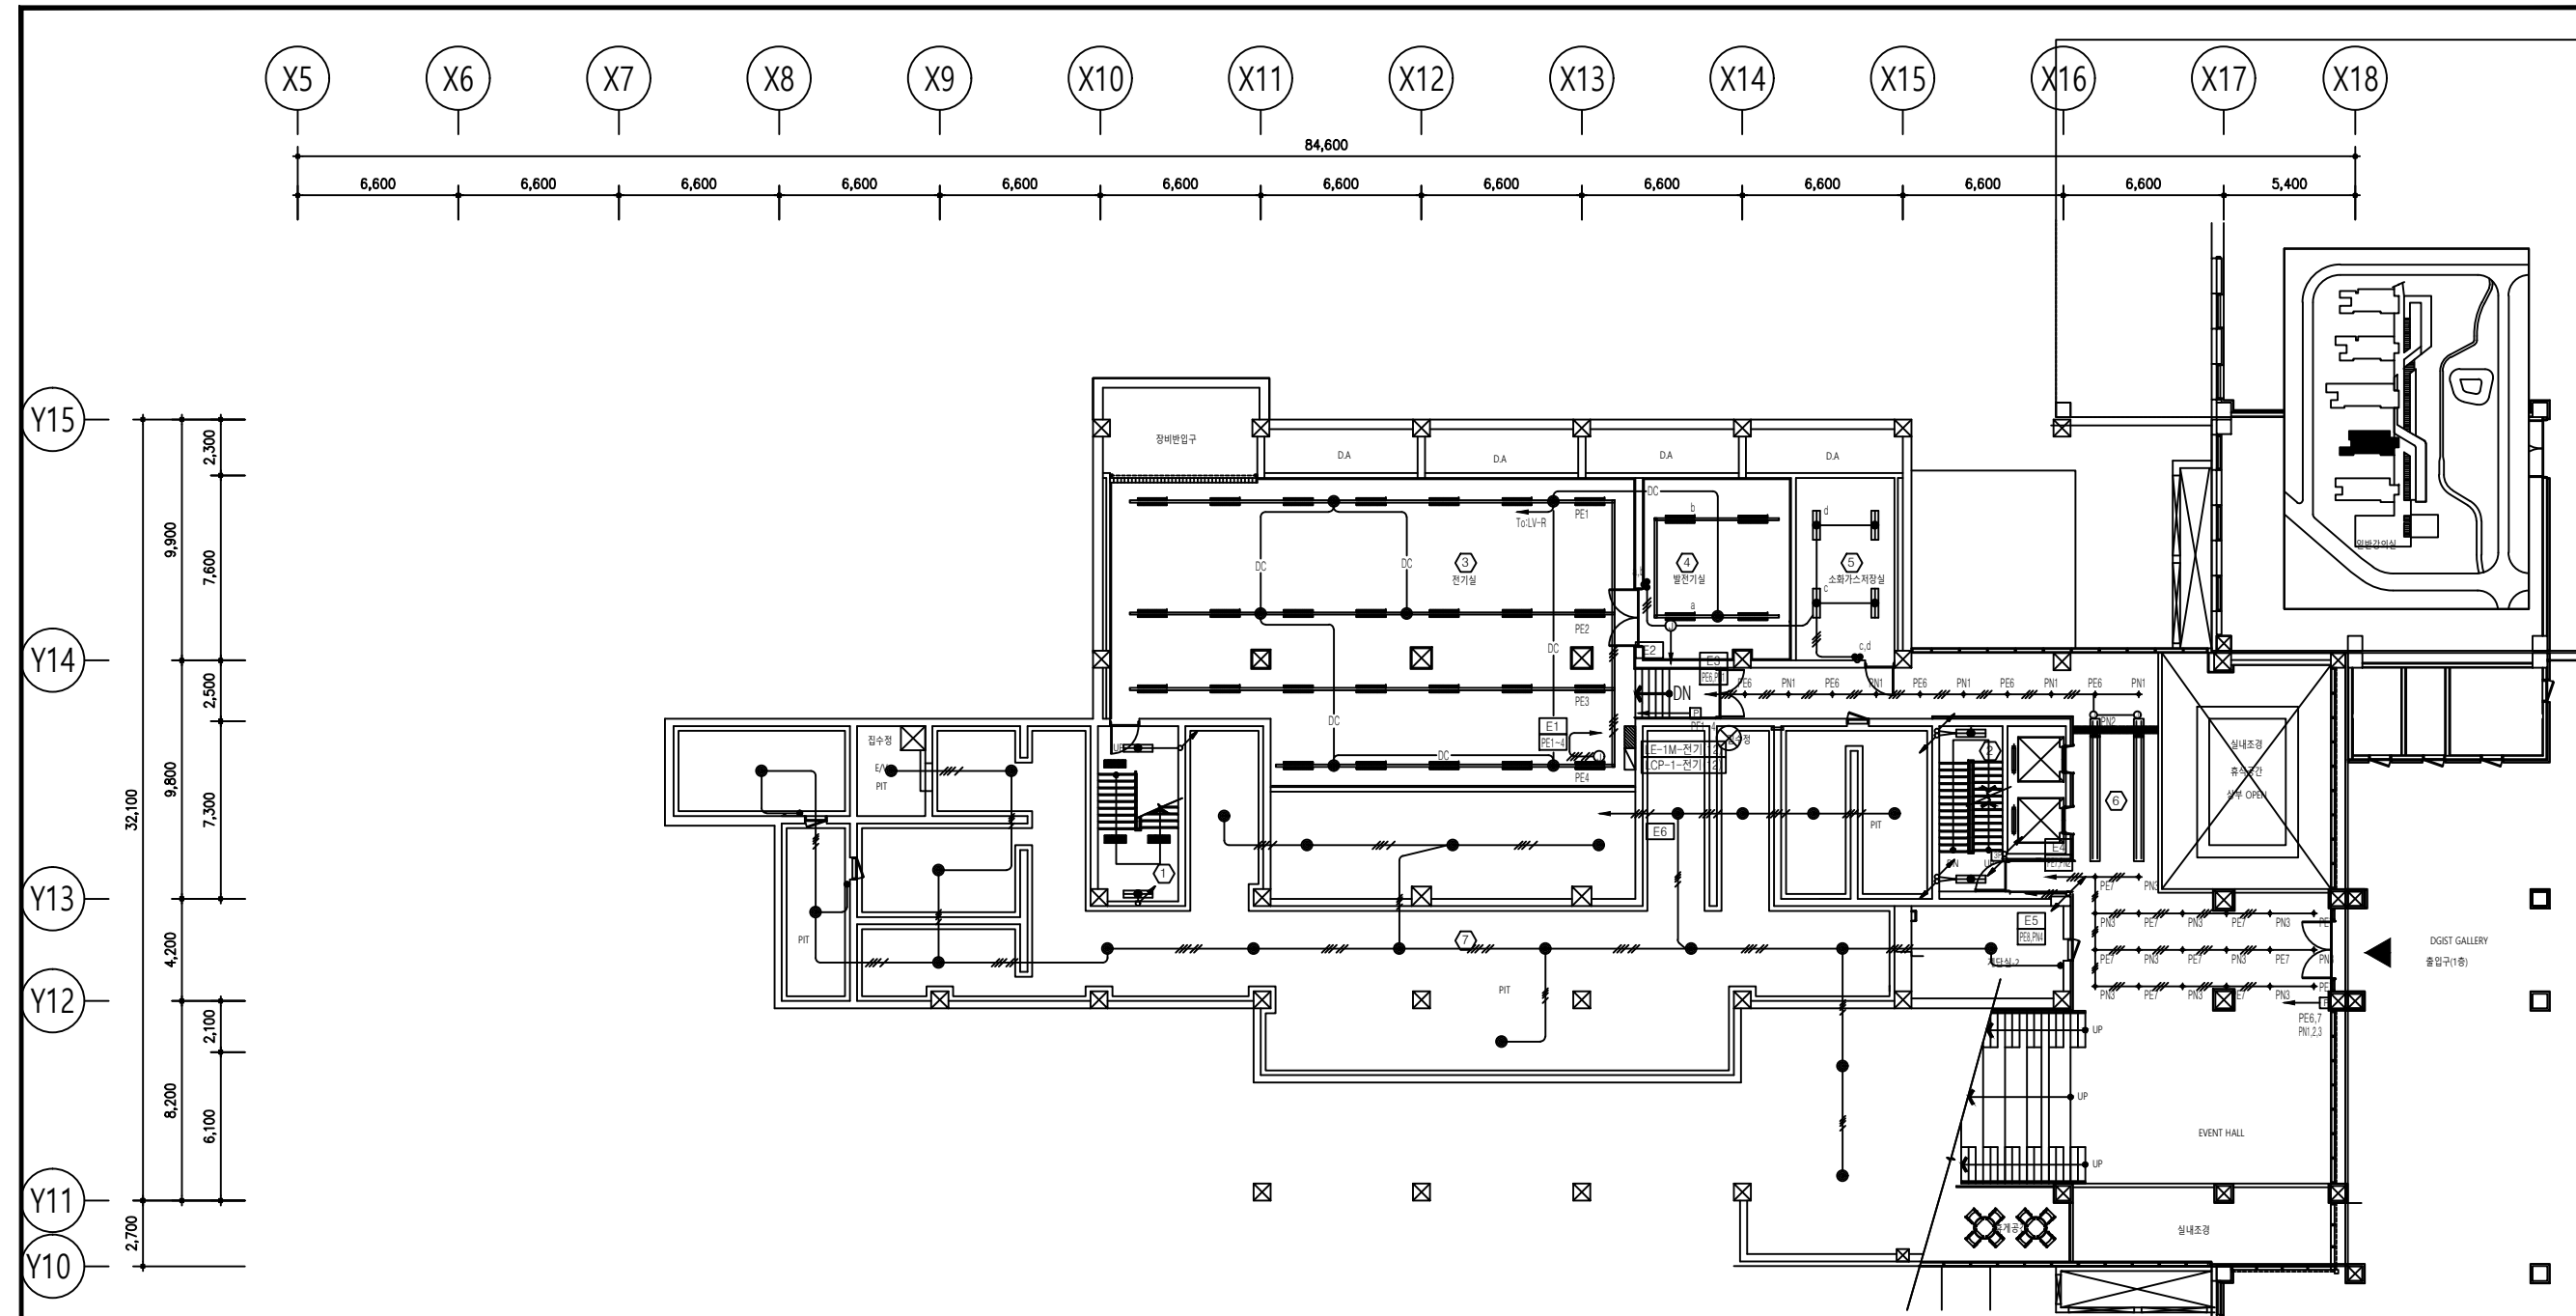

3					
2					
1	14.11.19	실명/호실 수정			
REV	DATE	DESCRIPTION	DRN	CHK	APR

DRAWING TITLE
정보통신융합공학부
1층 전등설비 평면도

APPROVED

CHECKED1

CHECKED2






DRAWN

PROJECT NO.

SCALE
A1 1/150 A3 1/300
APPROVAL DATE
2014.04

DRAWING NO.
E-12-0702
REV.

정보통신융합공학부 1층 전등설비 평면도
축척 A1: 1/150, A3: 1/300

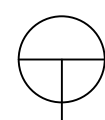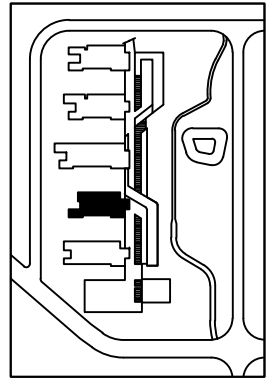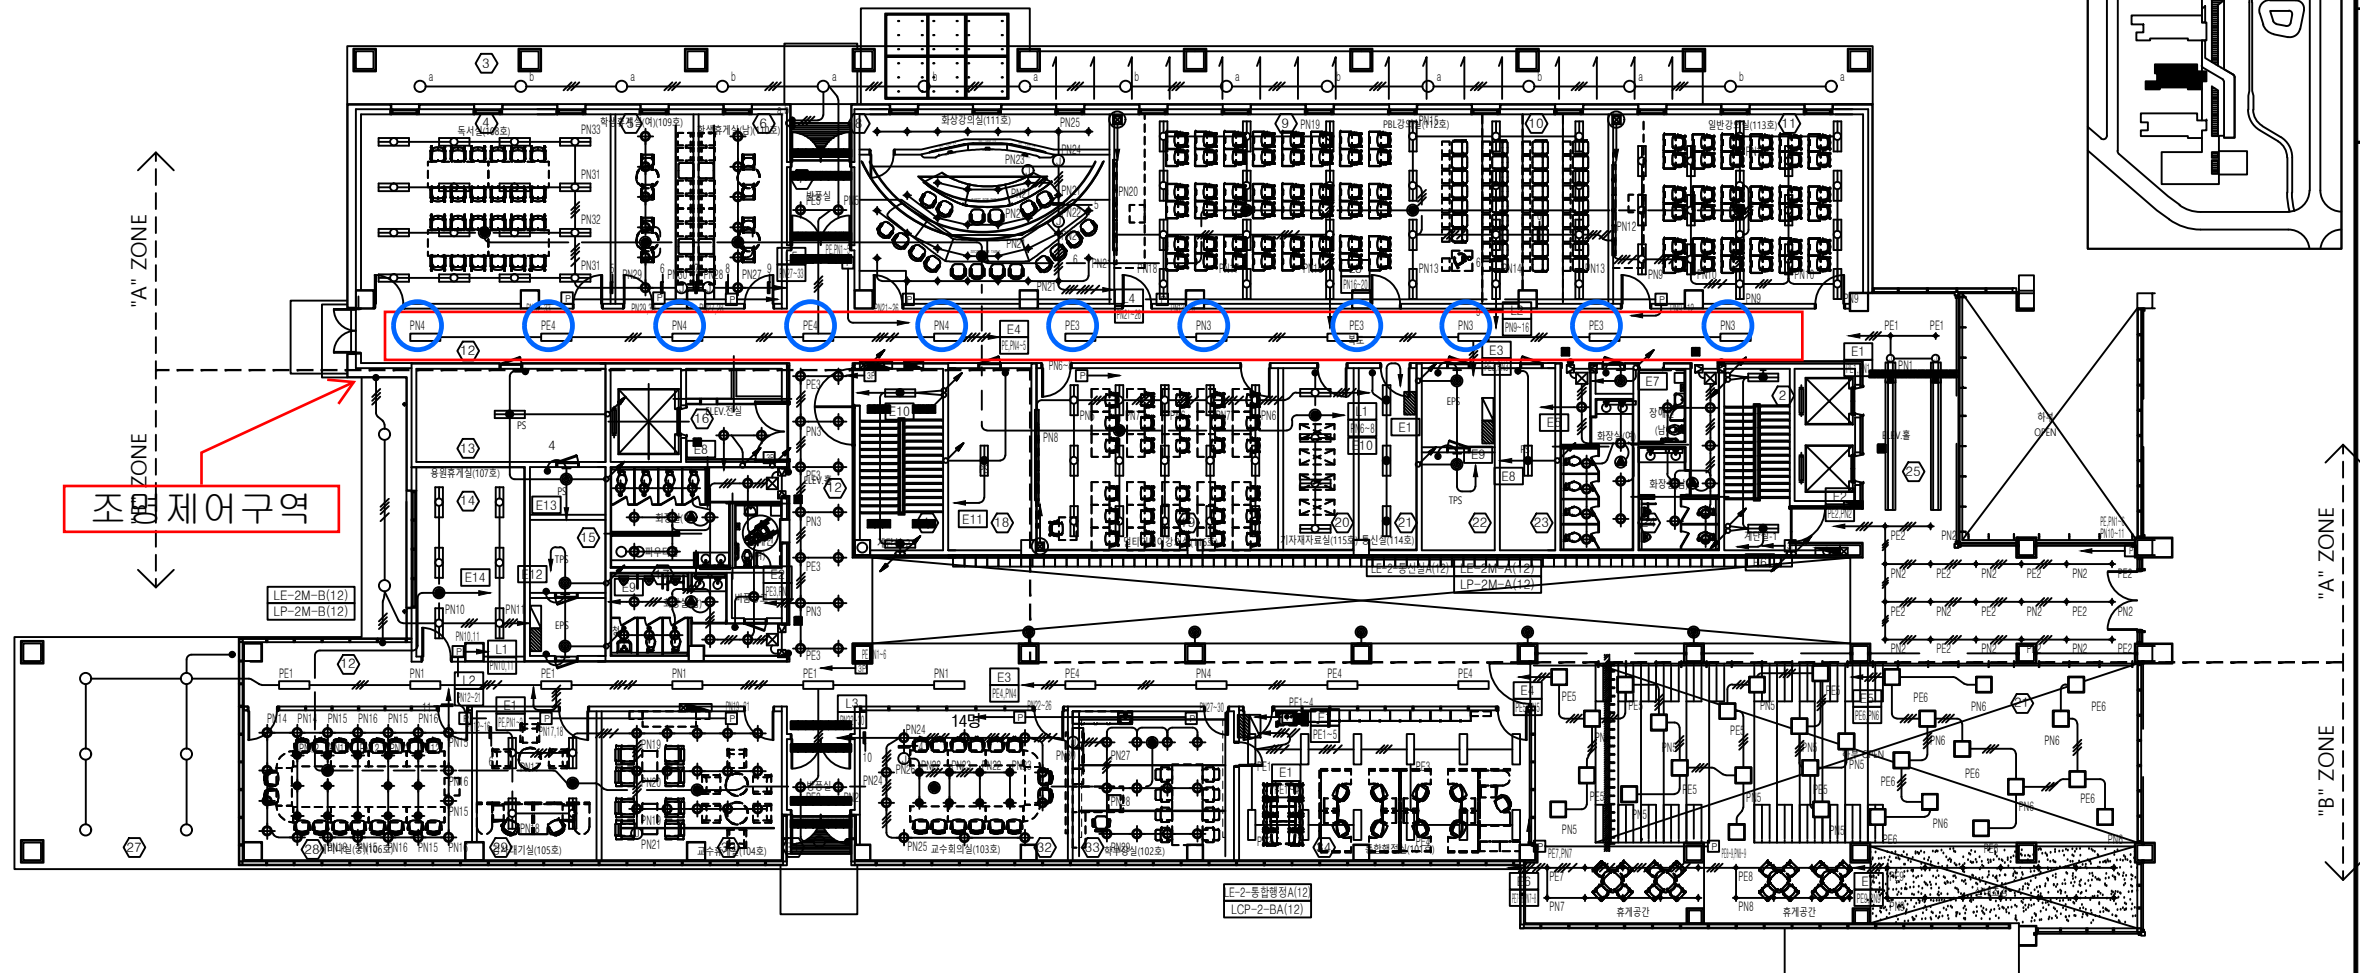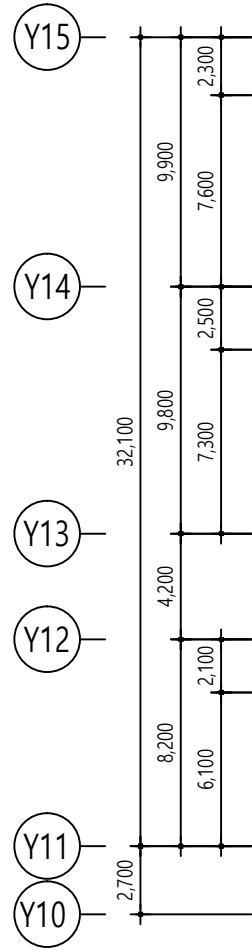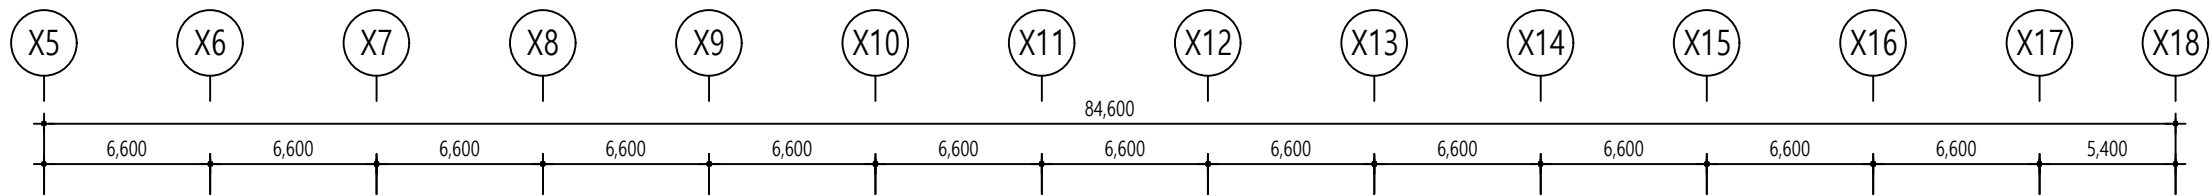

정보통신융합공학부 1층 전등설비 평면도

축척 A1: 1/150, A3: 1/300

3					
2					
1	14.11.19	실명/호실 수정			
REV	DATE	DESCRIPTION	DRN	CHK	APR

DRAWING TITLE

정보통신융합공학부
1층 전등설비 평면도

APPROVED

CHECKED1






CHECKED2

DRAWN

PROJECT NO.

SCALE	APPROVAL DATE
A1 1/150 A3 1/300	2014.04






DRAWING NO.	REV.
E-12-0703	

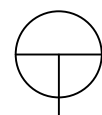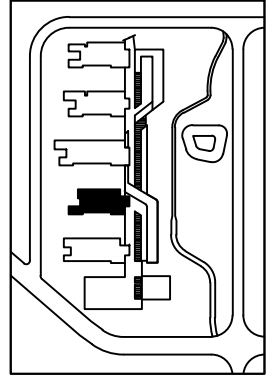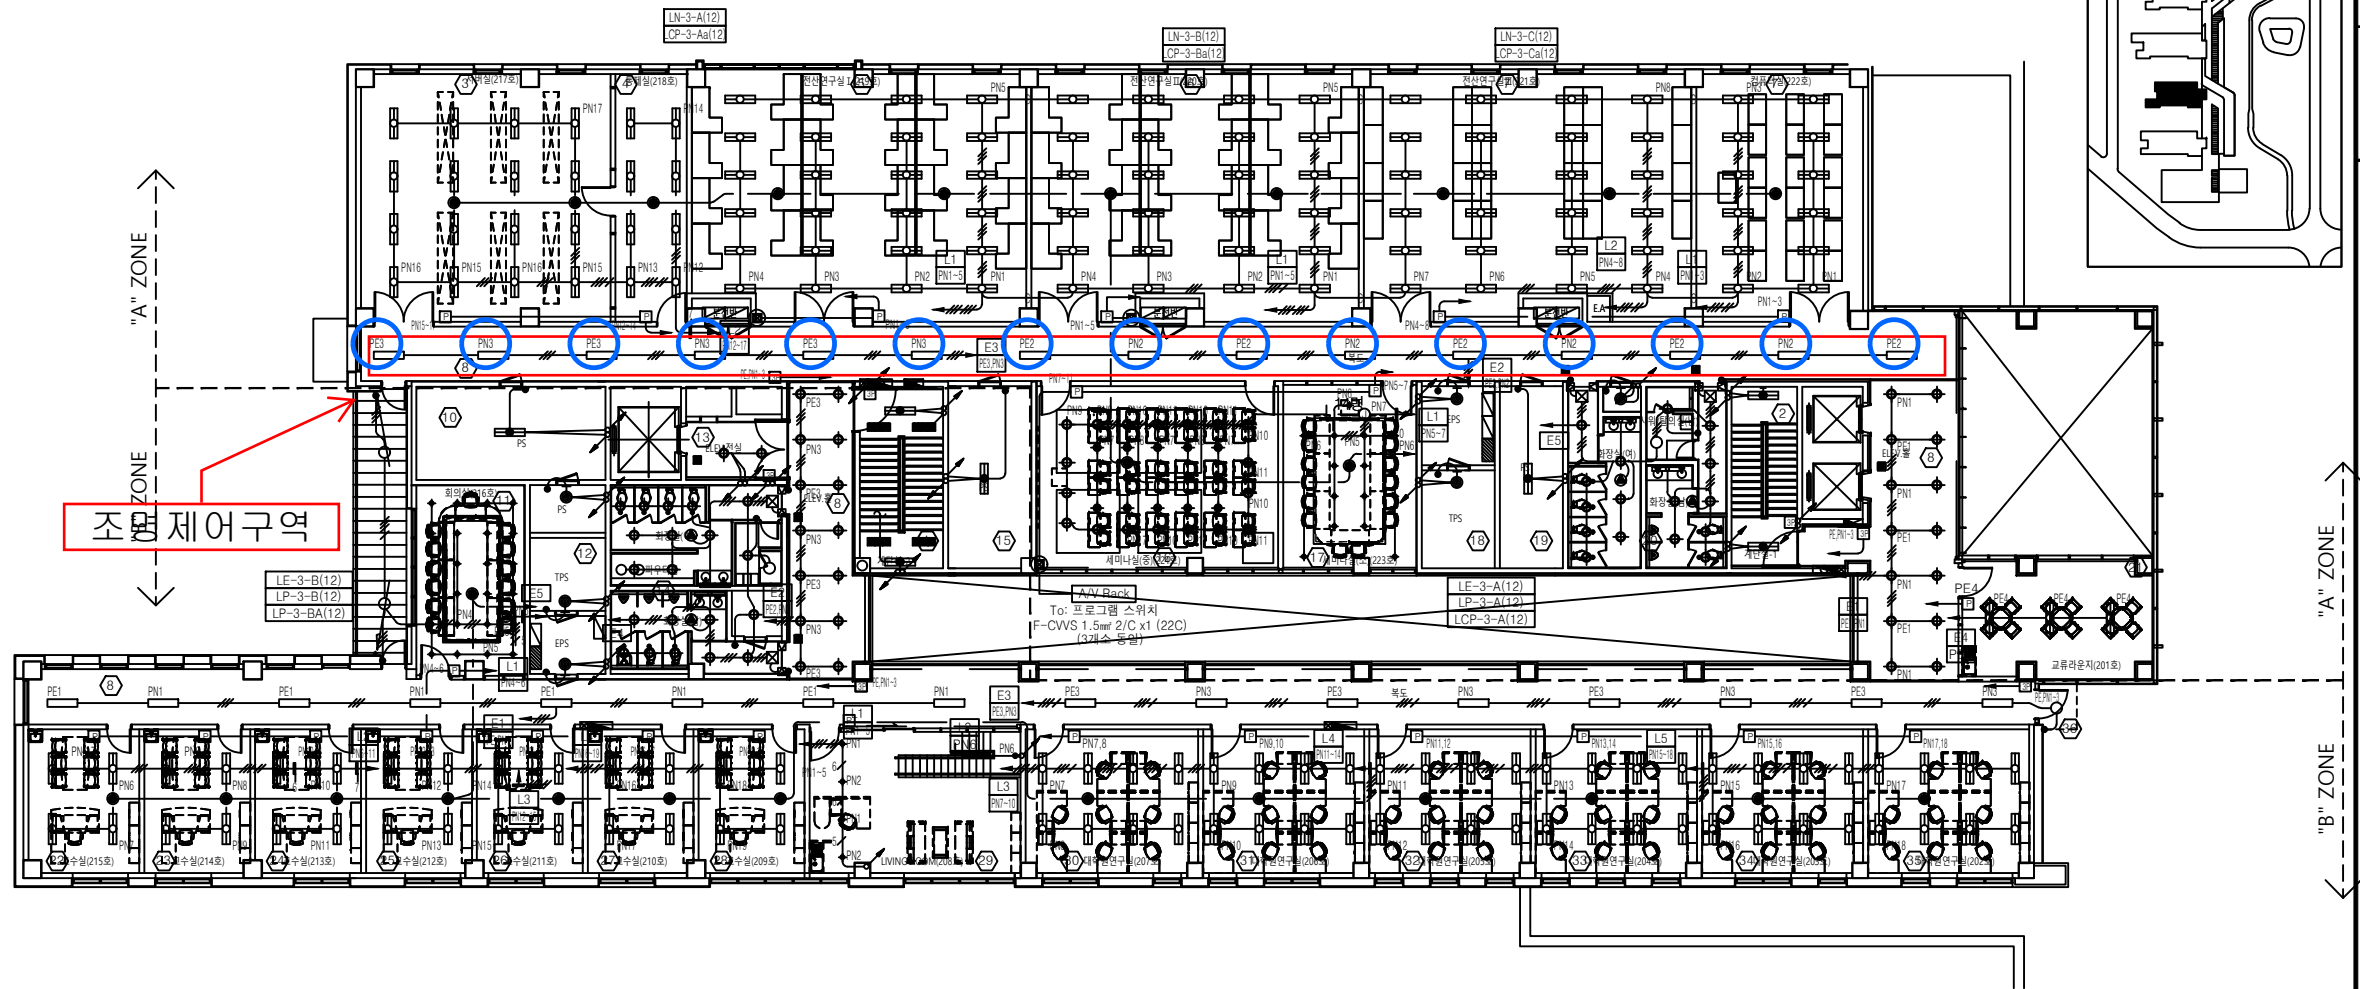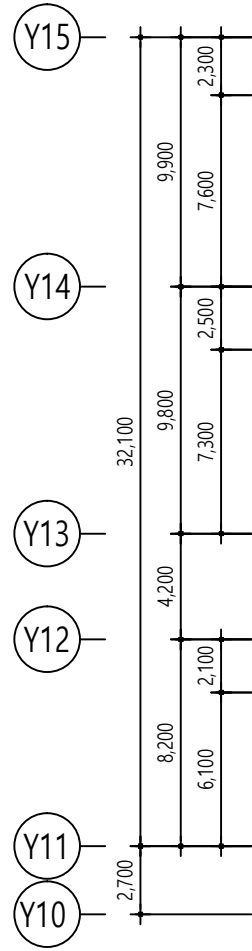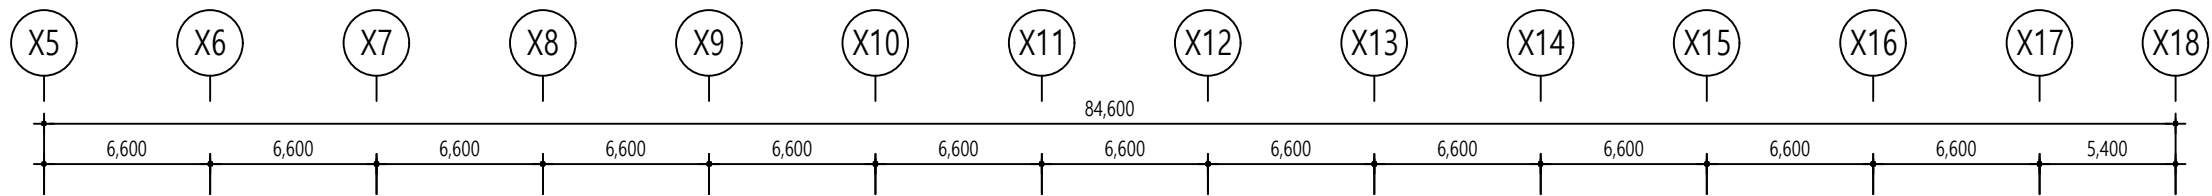

정보통신융합공학부 2층 전등설비 평면도

축척 A1: 1/150, A3: 1/300

3					
2					
1	14.11.19	실명/호실 수정			
REV	DATE	DESCRIPTION	DRN	CHK	APR
DRAWING TITLE					
정보통신융합공학부 2층 전등설비 평면도					
APPROVED					
CHECKED1					
CHECKED2					
DRAWN					
PROJECT NO.					
SCALE			APPROVAL DATE		
A1	1/150	A3	1/300	2014.04	
DRAWING NO.				REV.	
E-12-0704					

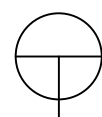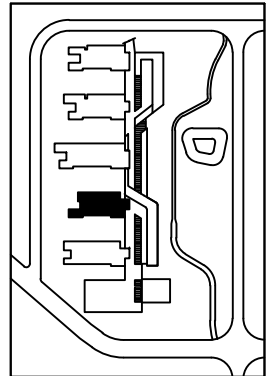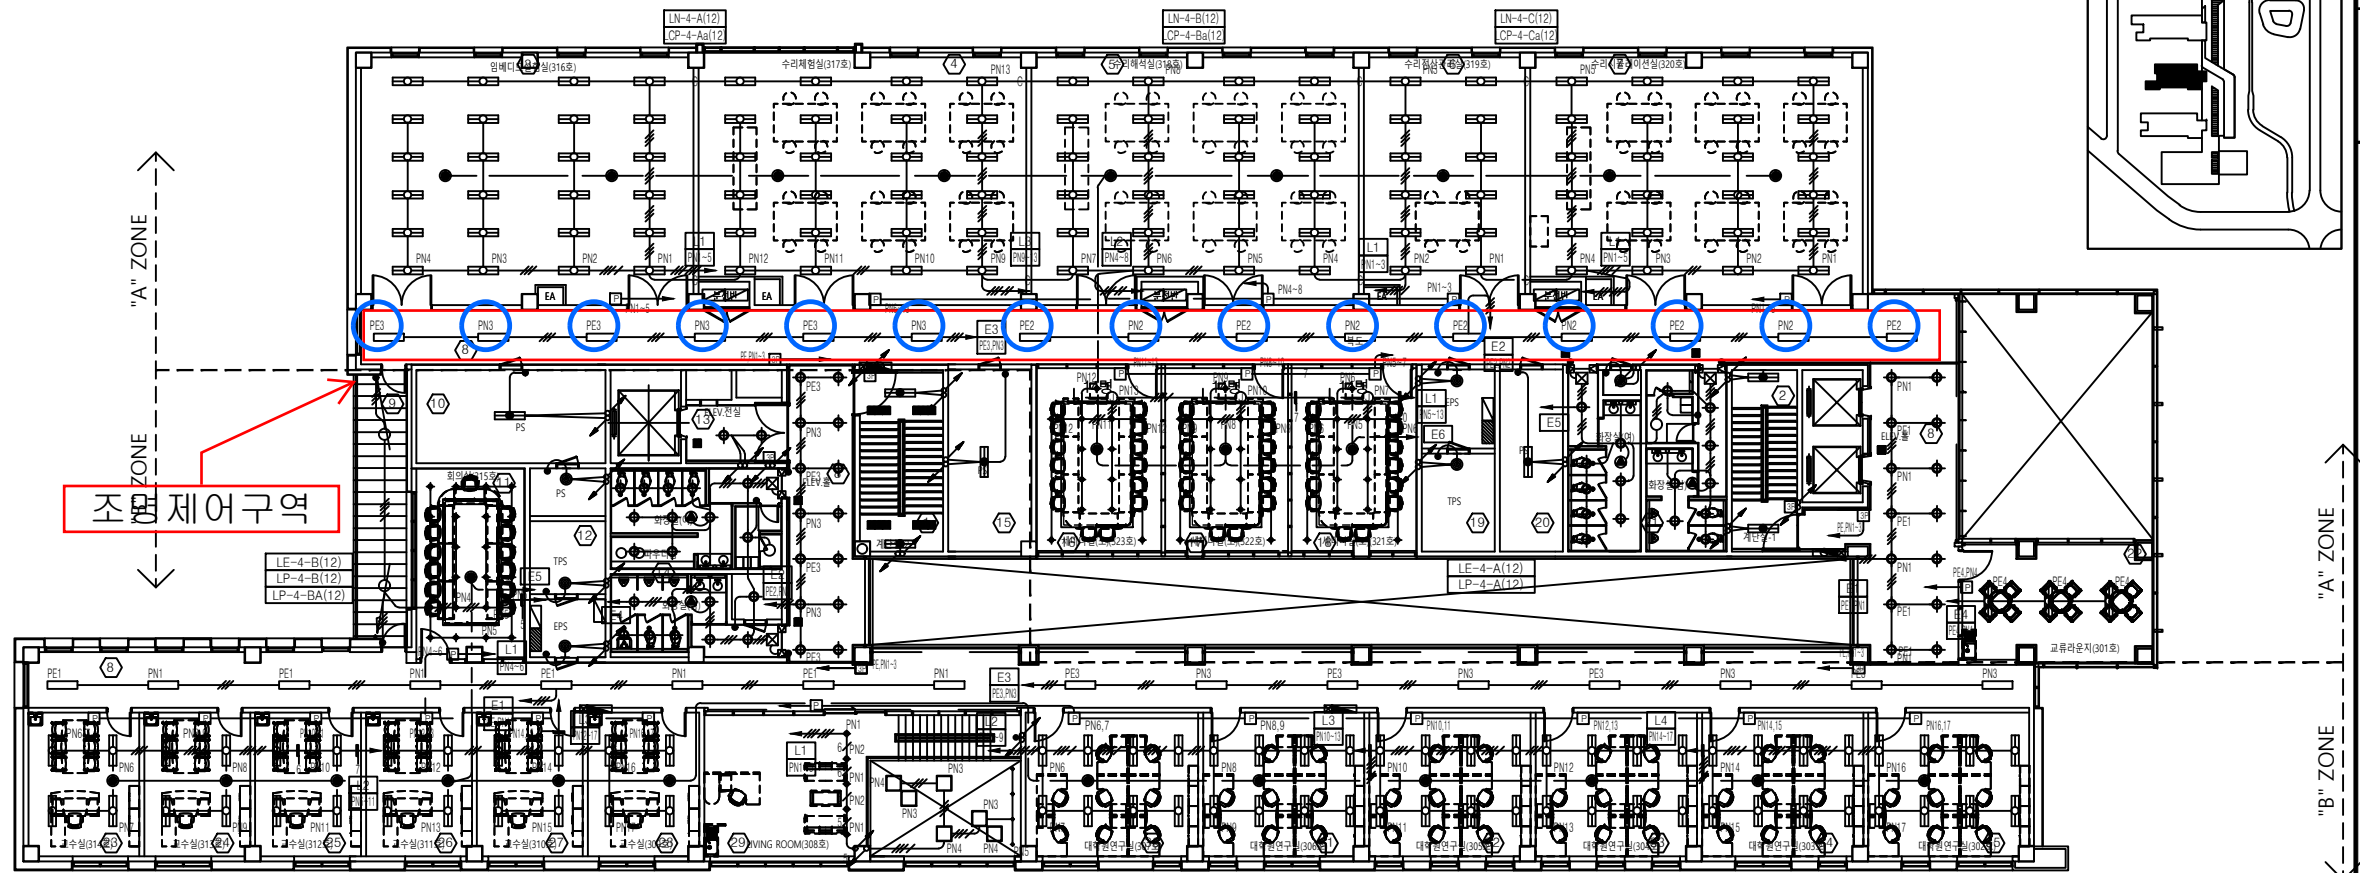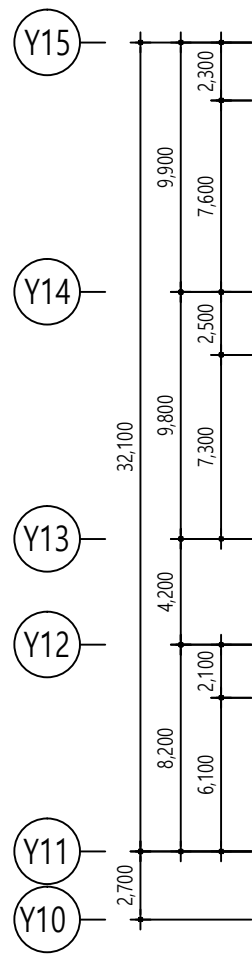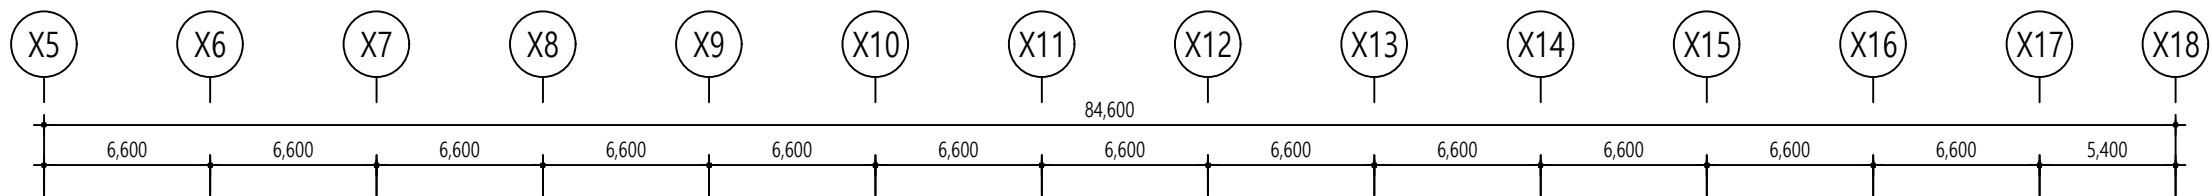

정보통신융합공학부 3층 전등설비 평면도

축척 A1: 1/150, A3: 1/300

3					
2					
1	14.11.19	실명/호실 수정			
REV	DATE	DESCRIPTION	DRN	CHK	APR

DRAWING TITLE

정보통신융합공학부
3층 전등설비 평면도

APPROVED

CHECKED1






CHECKED2

DRAWN

PROJECT NO.

SCALE	APPROVAL DATE
A1 1/150 A3 1/300	2014.04






DRAWING NO. E-12-0705 REV.

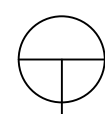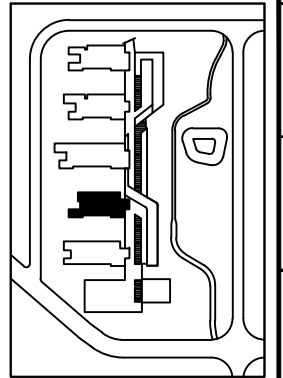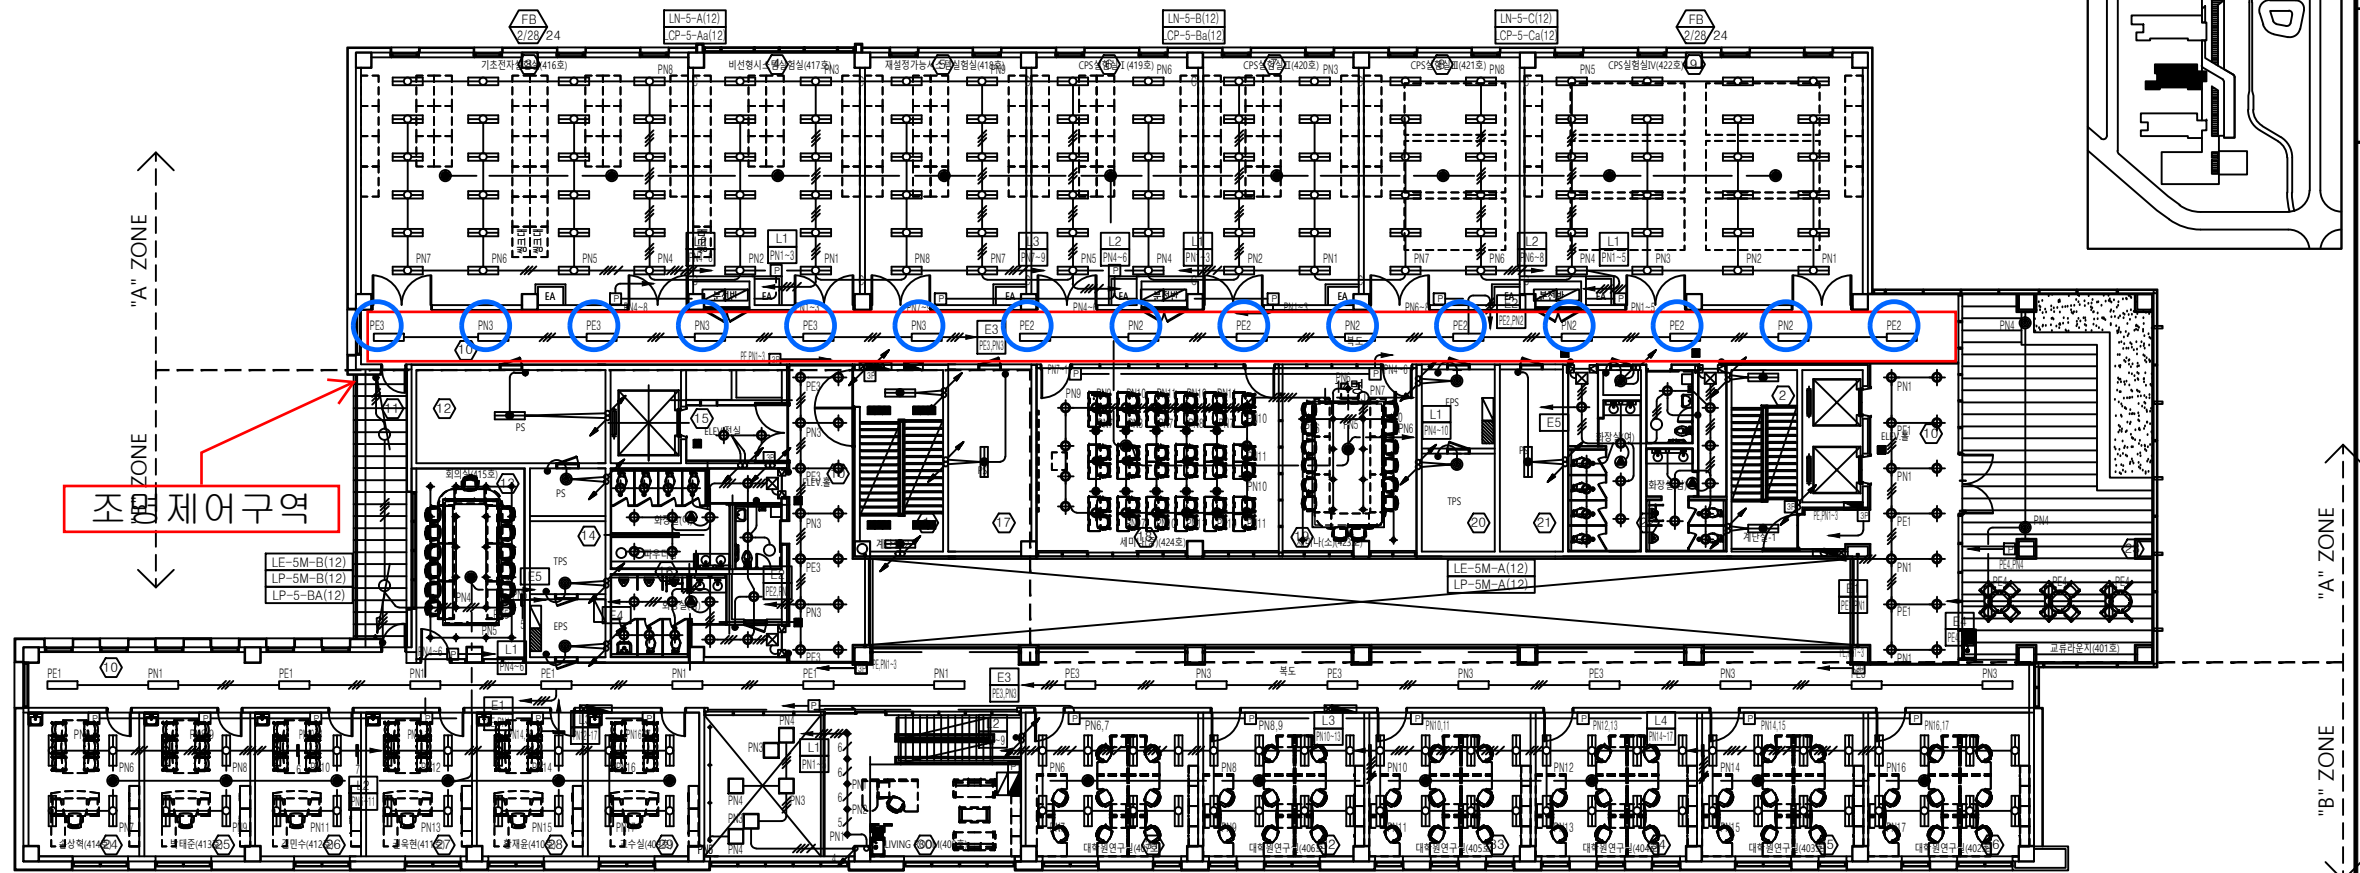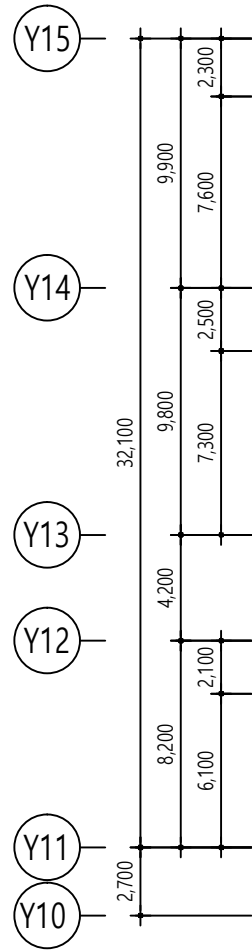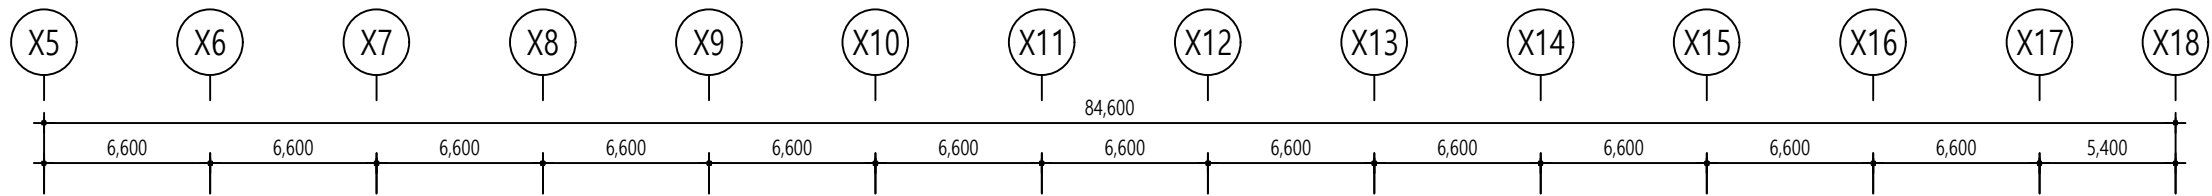

정보통신융합공학부 4층 전등설비 평면도

축척 A1: 1/150, A3: 1/300






3					
2					
1	14.11.19	실명/호실 수정			
REV	DATE	DESCRIPTION	DRN	CHK	APR
DRAWING TITLE					
정보통신융합공학부 4층 전등설비 평면도					
APPROVED					
CHECKED1					
CHECKED2					
DRAWN					
PROJECT NO.					
SCALE					
A1	1/150	A3	1/300	APPROVAL DATE	
				2014.04	
DRAWING NO.					REV.
E-12-0706					

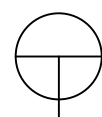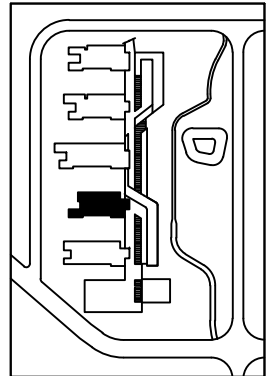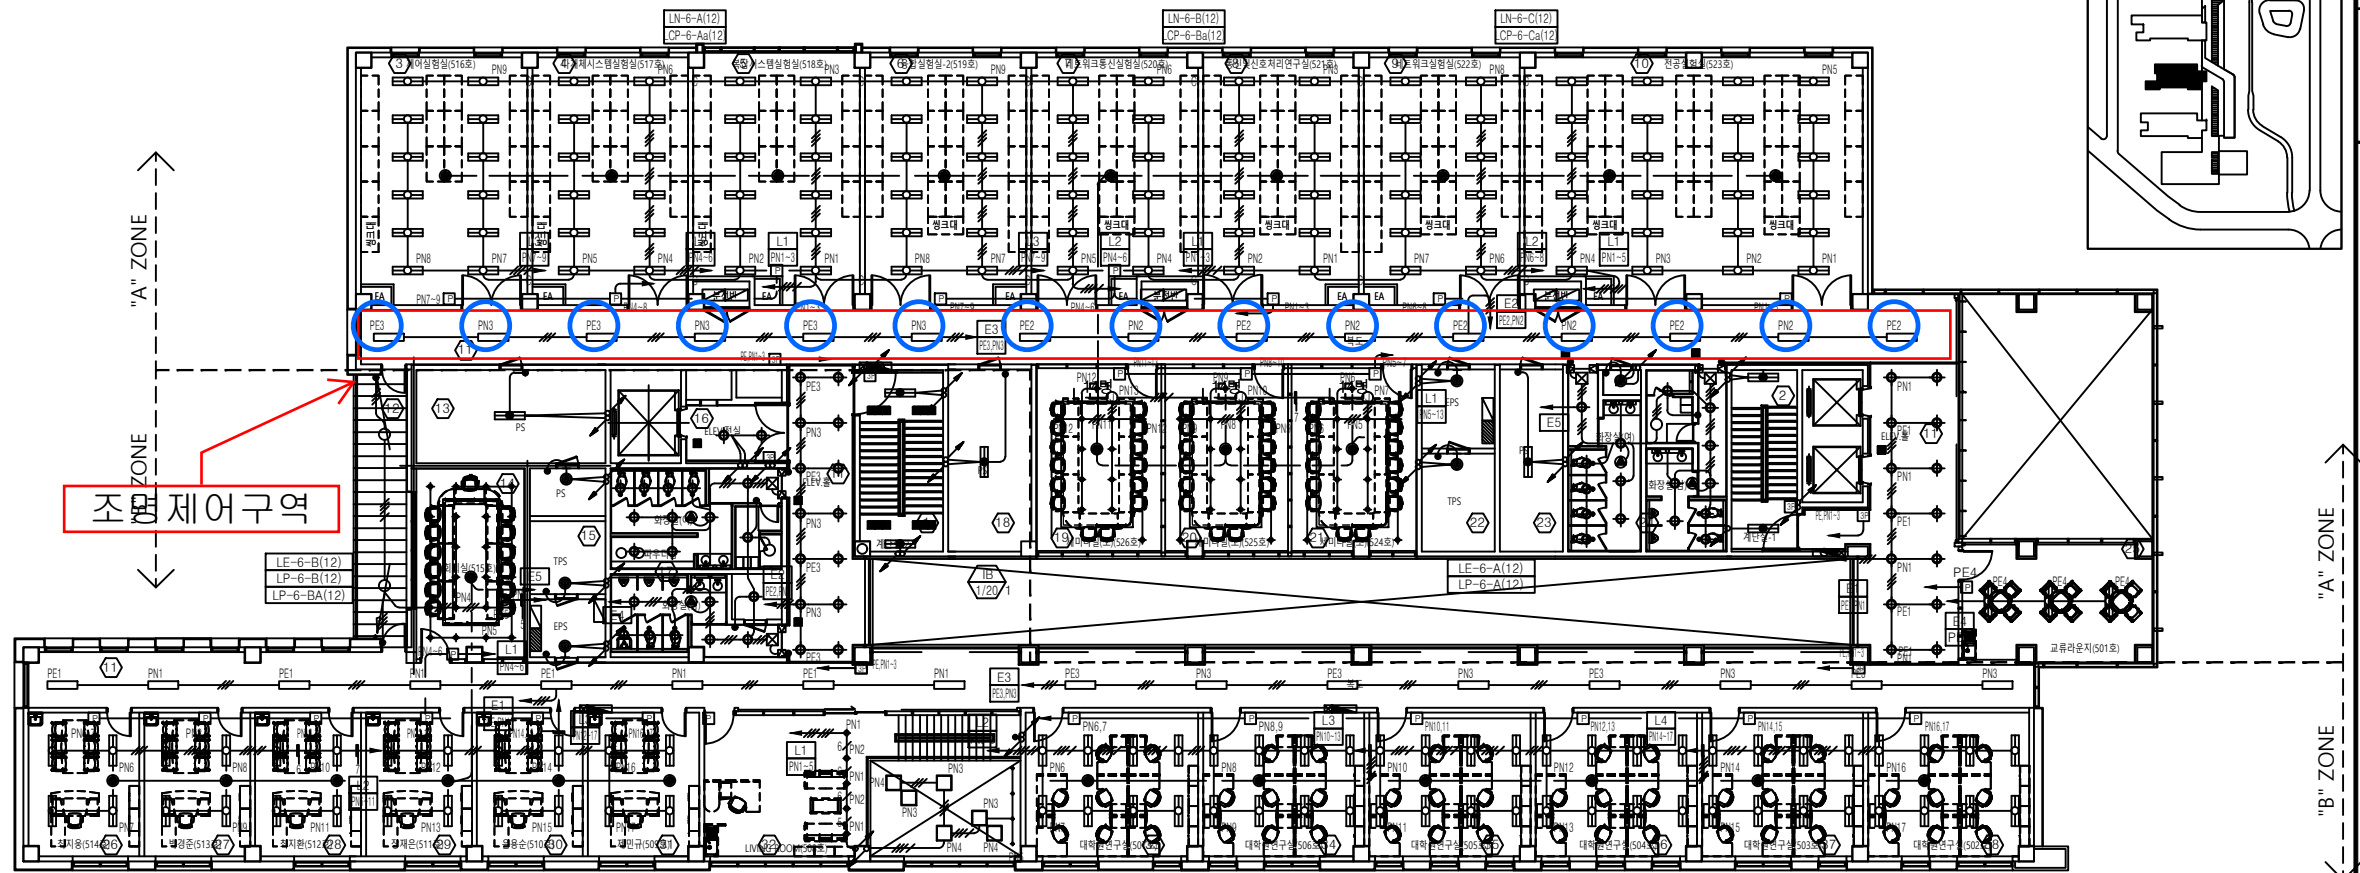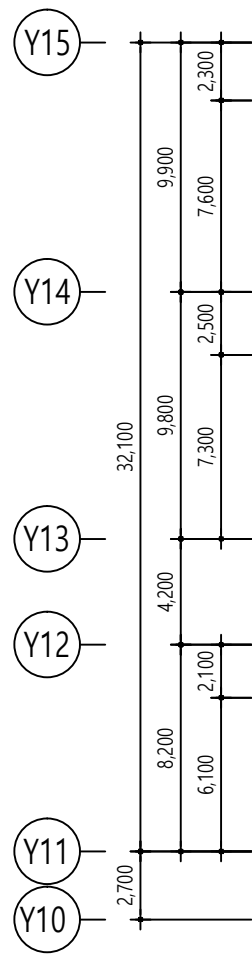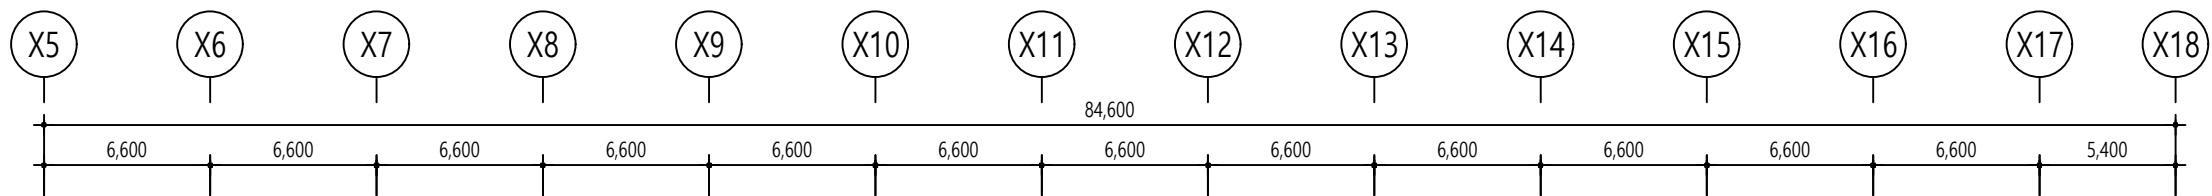

정보통신융합공학부 5층 전등설비 평면도

축척 A1: 1/150, A3: 1/300

3					
2					
1	14.11.19	실명/호실 수정			
REV	DATE	DESCRIPTION	DRN	CHK	APR
DRAWING TITLE					
정보통신융합공학부 5층 전등설비 평면도					
APPROVED					
CHECKED1					
CHECKED2					
DRAWN					
PROJECT NO.					
SCALE			APPROVAL DATE		
A1	1/150	A3	1/300	2014.04	
DRAWING NO.					REV.
E-12-0707					

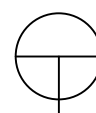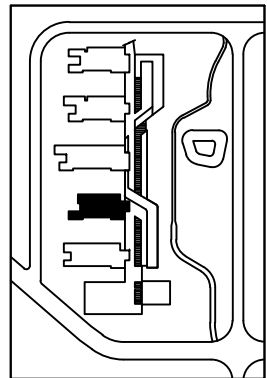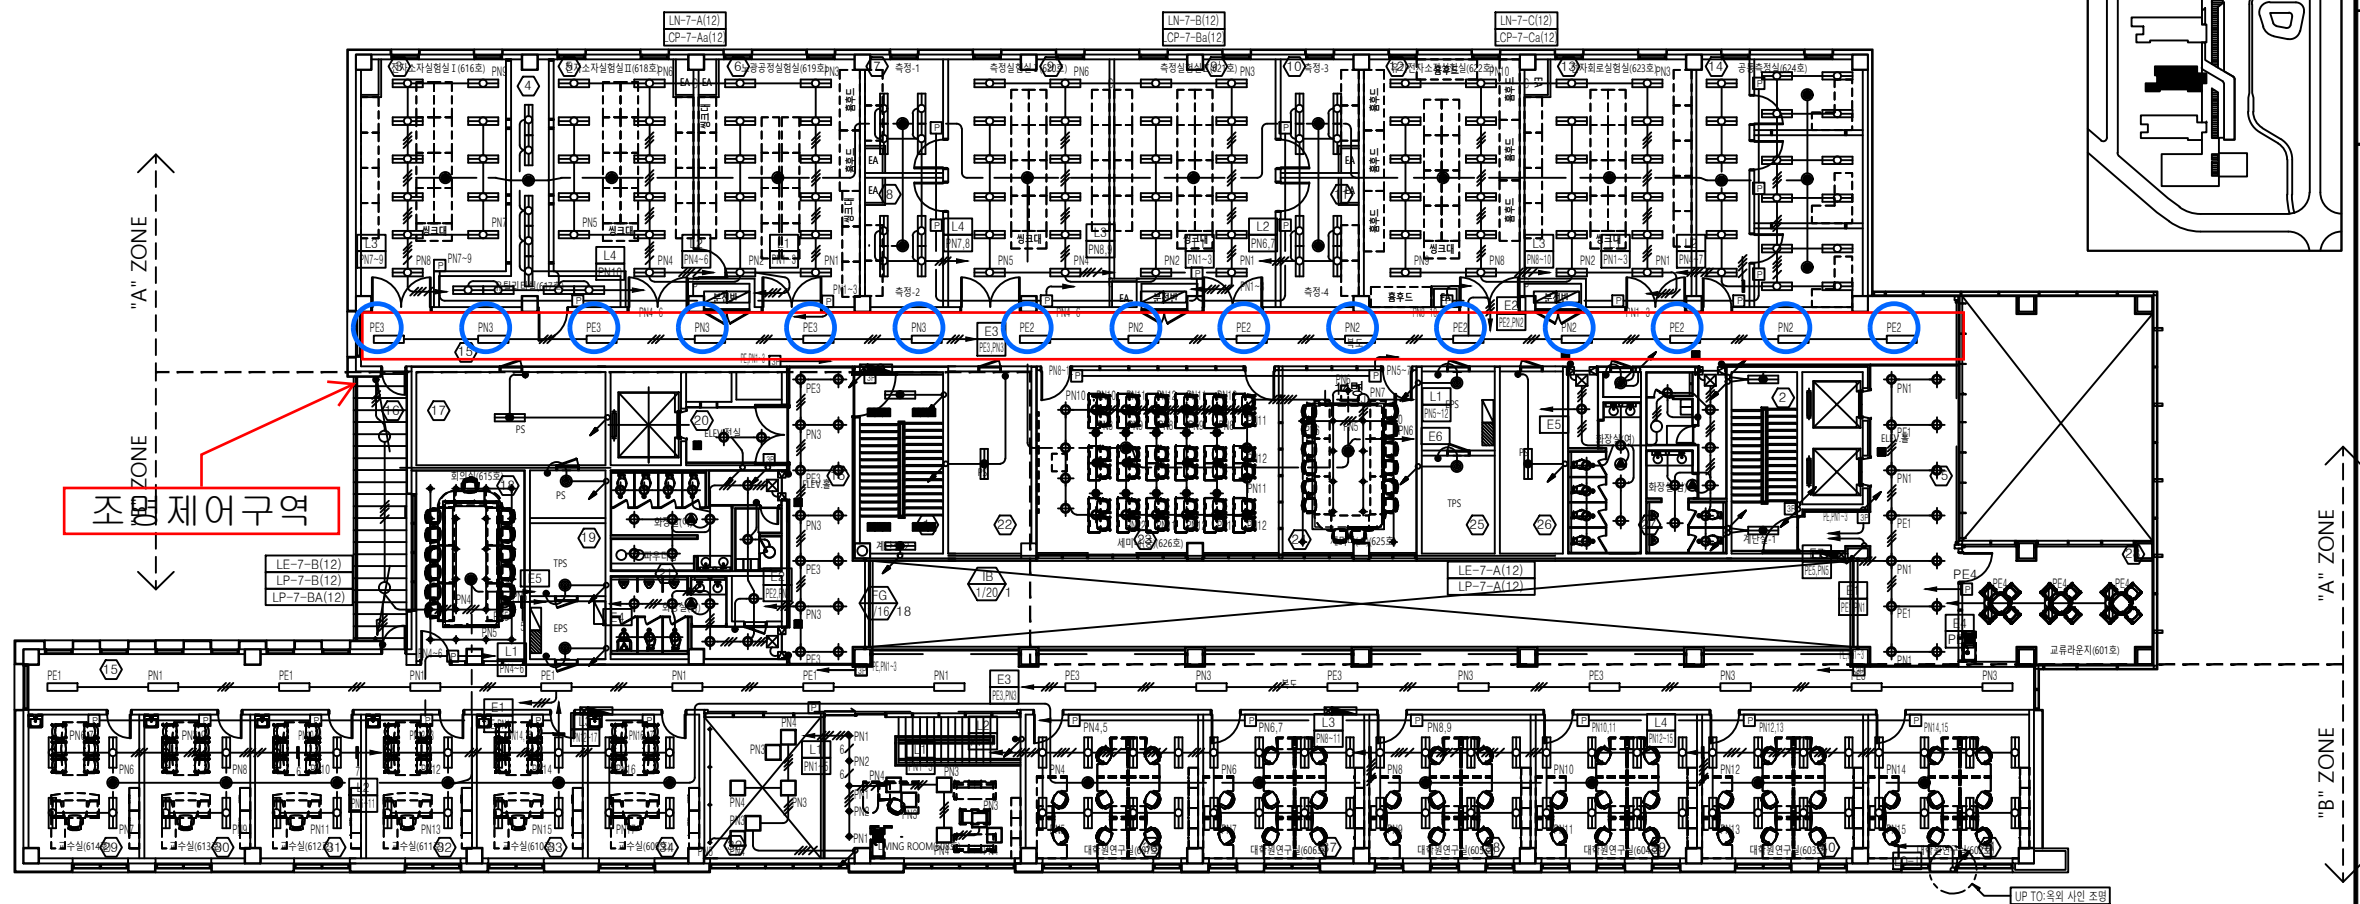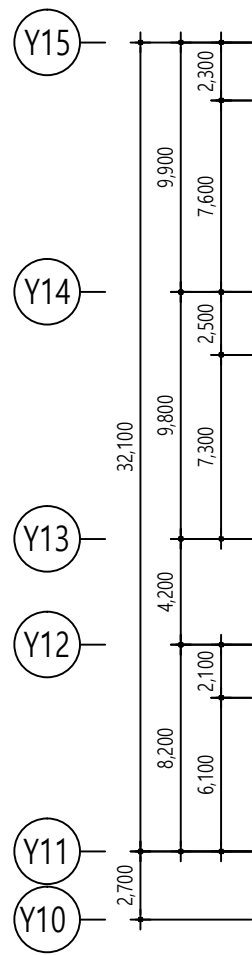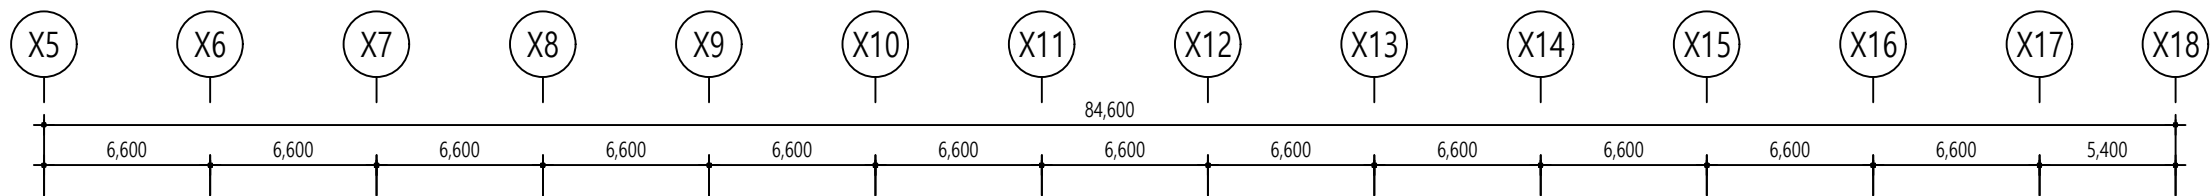

정보통신융합공학부 6층 전등설비 평면도

축척 A1: 1/150, A3: 1/300

3					
2					
1	14.11.19	실명/호실 수정			
REV	DATE	DESCRIPTION	DRN	CHK	APR
DRAWING TITLE					
정보통신융합공학부 6층 전등설비 평면도					
APPROVED					
CHECKED1					
CHECKED2					
DRAWN					
PROJECT NO.					
SCALE			APPROVAL DATE		
A1	1/150	A3	1/300	2014.04	
DRAWING NO.					REV.
E-12-0708					

