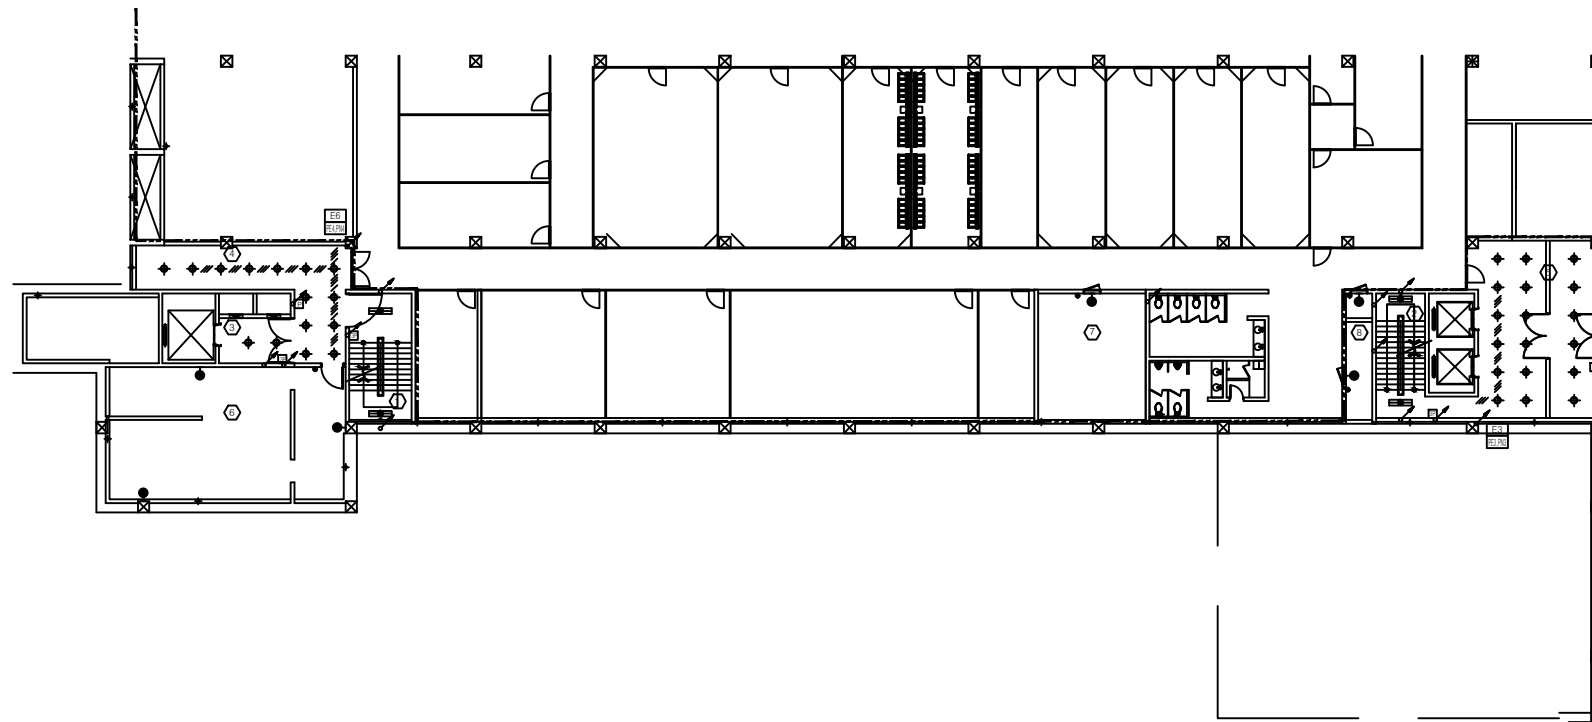
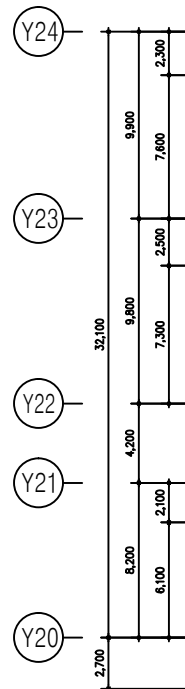
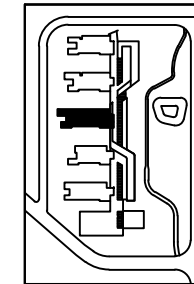
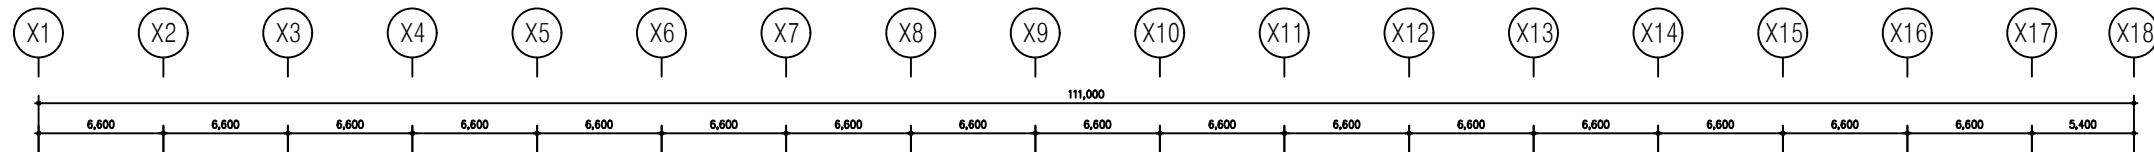


뇌과학부 지하2층 전등설비 평면도

축척 A1: 1/200, A3: 1/400

학위과정시설 임대형민자사업(BTL)

Construction

現代建設

TEL. 053)615-5093~6 FAX. 053)615-5097

Construction Management

SAMOOO.C.M.
Construction Management

TEL. 053)611-3071 FAX. 053)611-3073

NOTE

1. 시험실내의 전등설비용 공배관 설치.
— C — : EMPTY PIPE (CD 22C)

3					
2					
1	14.11.18	실명/호실 수정			
REV	DATE	DESCRIPTION	DRN	CHK	APR

DRAWING TITLE

뇌과학부
지하2층 전등설비 평면도

APPROVED




CHECKED1

CHECKED2

DRAWN

PROJECT NO.

SCALE	A3	APPROVAL DATE
1/200	1/400	2014.04
DRAWING NO.	E-13-0701	REV.

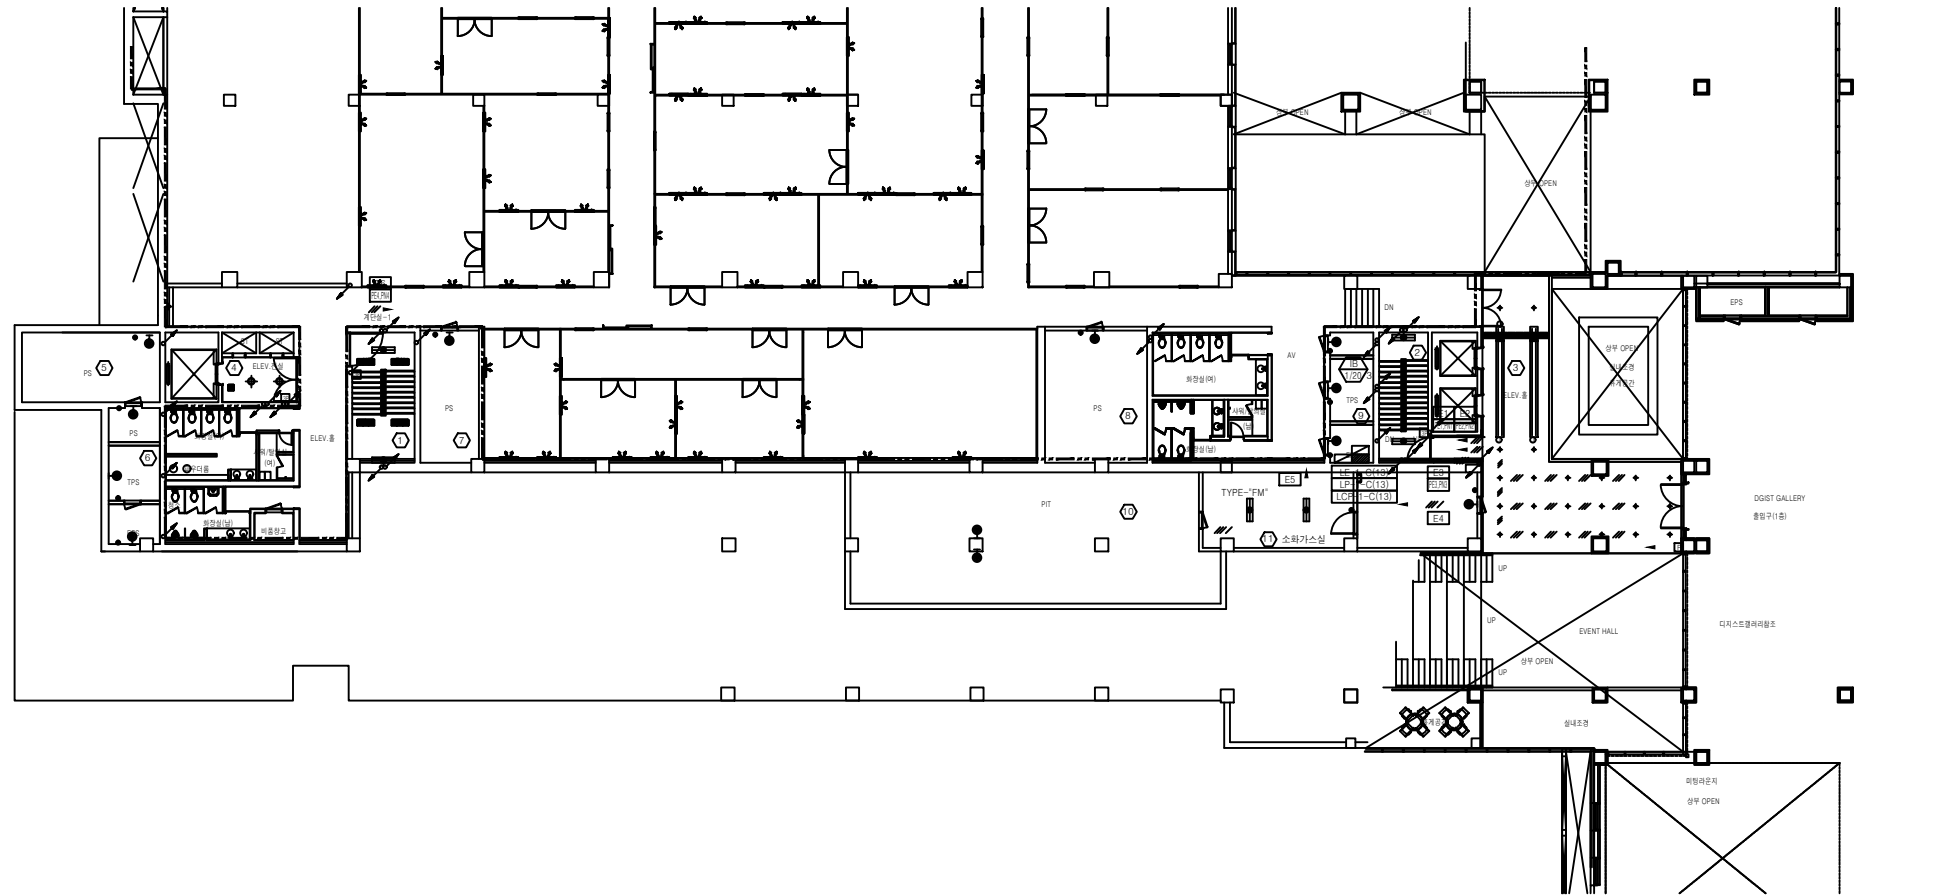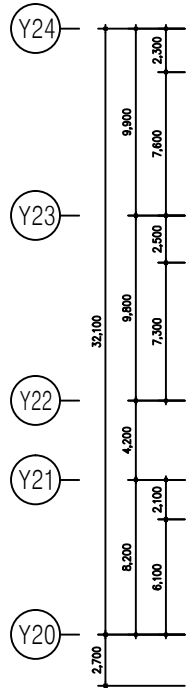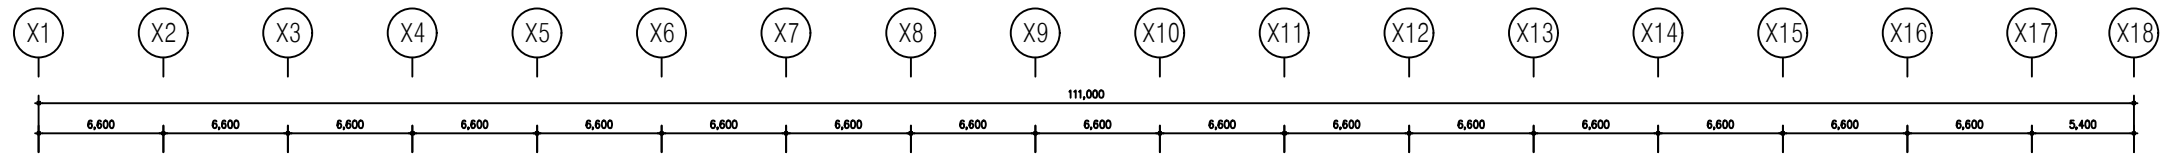

학위과정시설 임대형민자사업(BTL)

Construction

現代建設

TEL. 053)615-5093~6 FAX. 053)615-5097

Construction Management

SAMOOO.C.M.
Construction Management

TEL. 053)611-3071 FAX. 053)611-3073

NOTE

1. 실험실내의 전등설비용 공배관 설치.
— C — : EMPTY PIPE (CD 22C)

3					
2					
1	14.11.18	실험/호실 수정			
REV	DATE	DESCRIPTION	DRN	CHK	APR

DRAWING TITLE

뇌과학부
지하1층 전등설비 평면도

APPROVED

CHECKED1

CHECKED2



DRAWN

PROJECT NO.

SCALE
A1 1/200 A3 1/400
APPROVAL DATE
2014.04

DRAWING NO.
E-13-0702
REV.

뇌과학부 지하1층 전등설비 평면도
축척 A1: 1/200, A3: 1/400

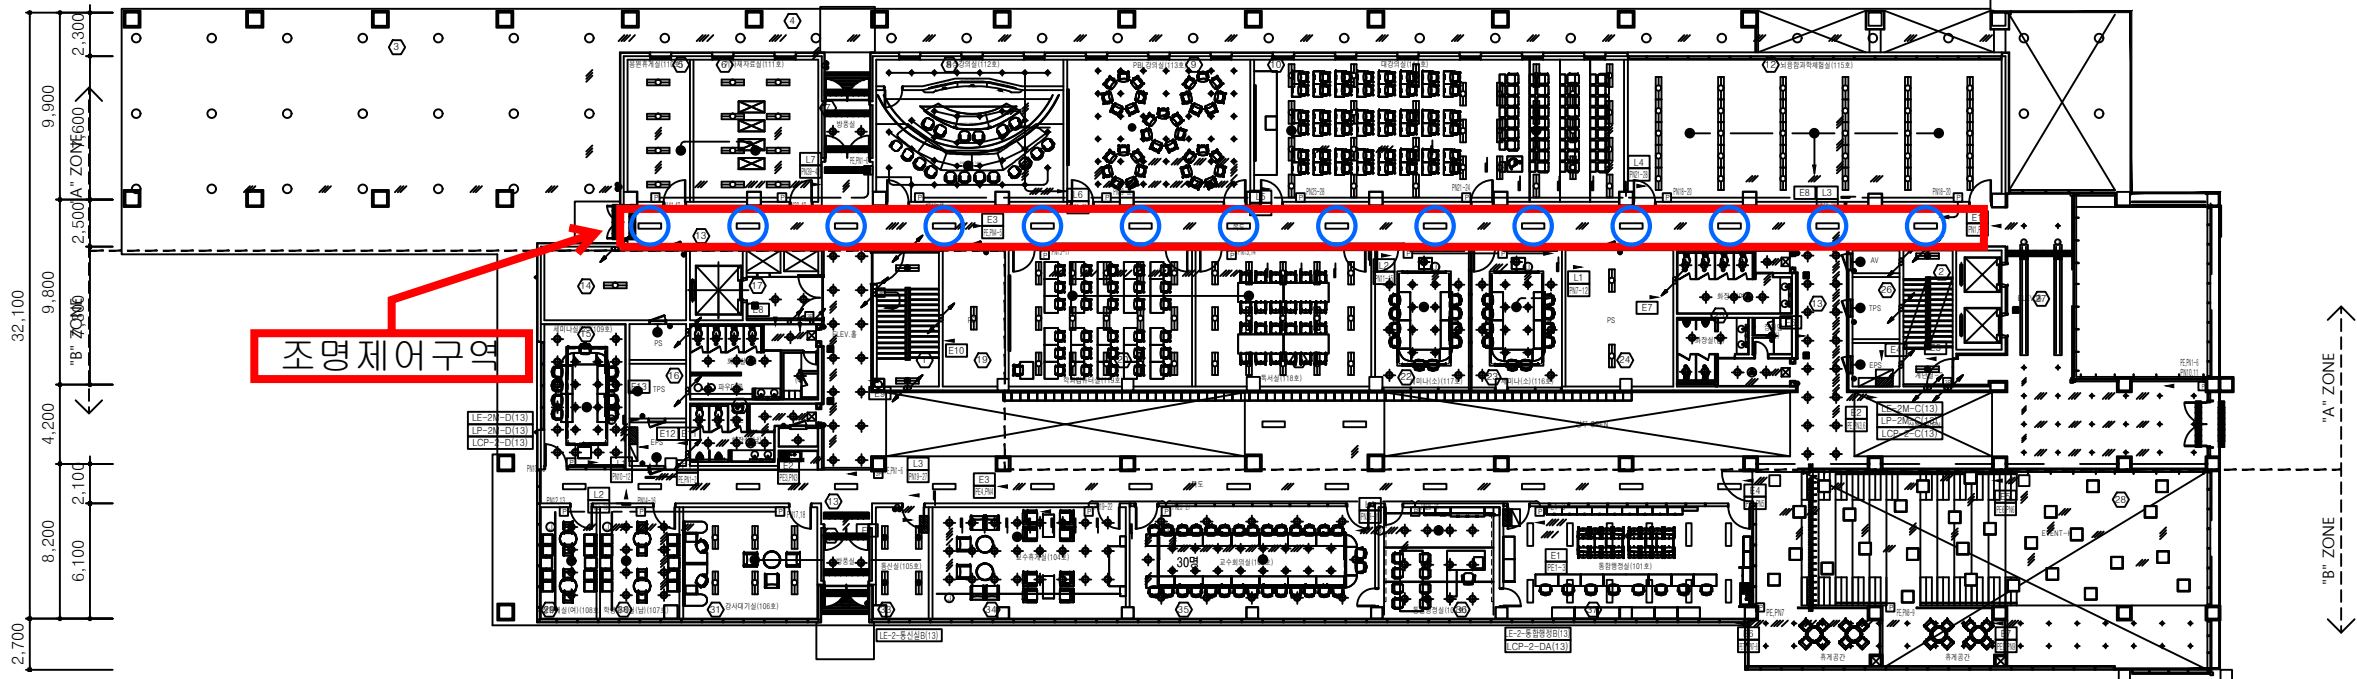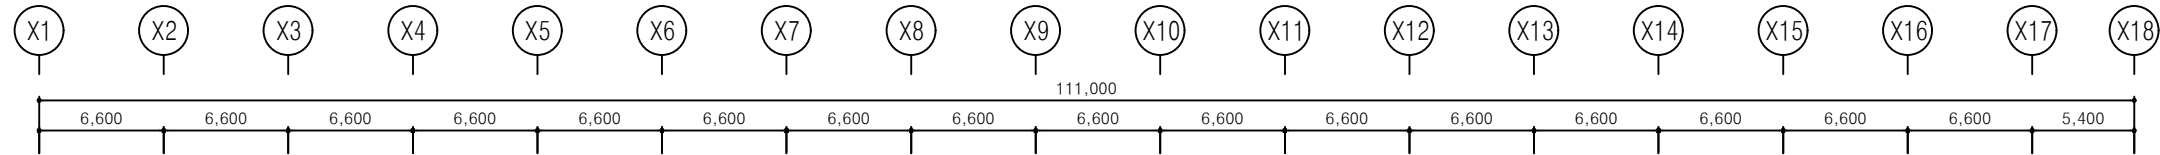

뇌과학부 1층 전등설비 평면도
축척 A1: 1/200, A3: 1/400

3					
2					
1	14.11.18	실명/호실 수정			
REV	DATE	DESCRIPTION	DRN	CHK	APR

DRAWING TITLE

뇌과학부
1층 전등설비 평면도

APPROVED

CHECKED1



CHECKED2


DRAWN

PROJECT NO.




SCALE	APPROVAL DATE
A1: 1/200 A3: 1/400	2014.04

DRAWING NO.	REV.
E-13-0703	

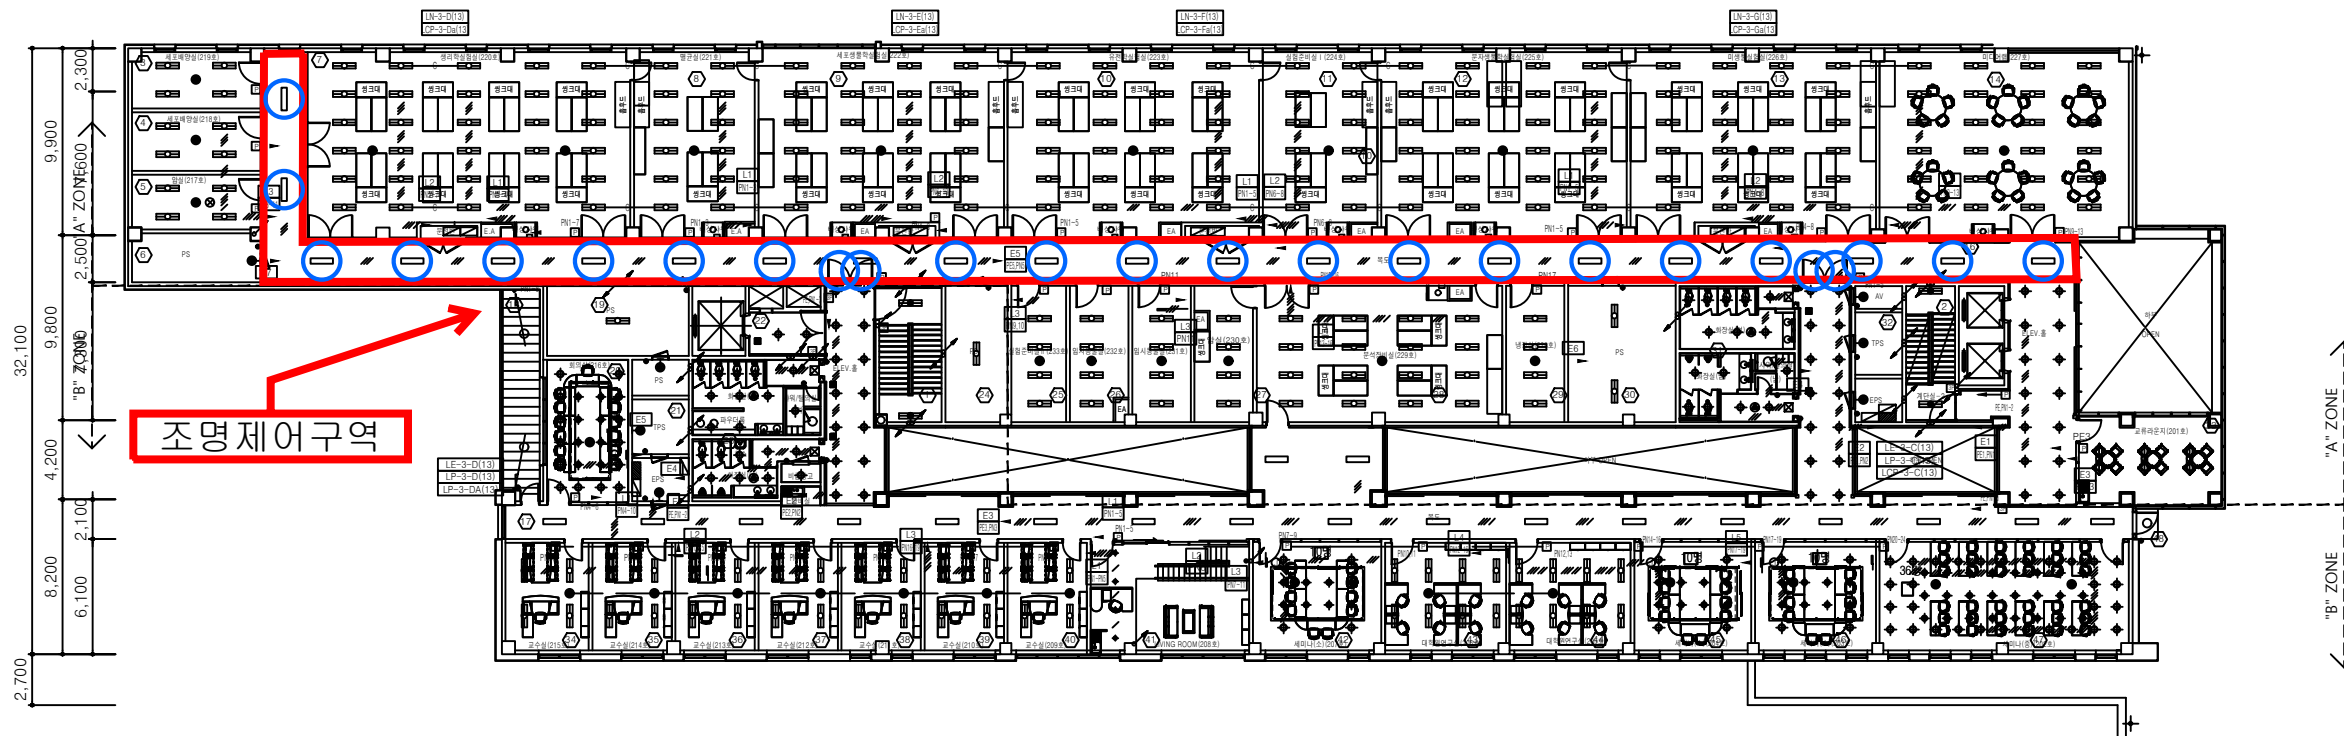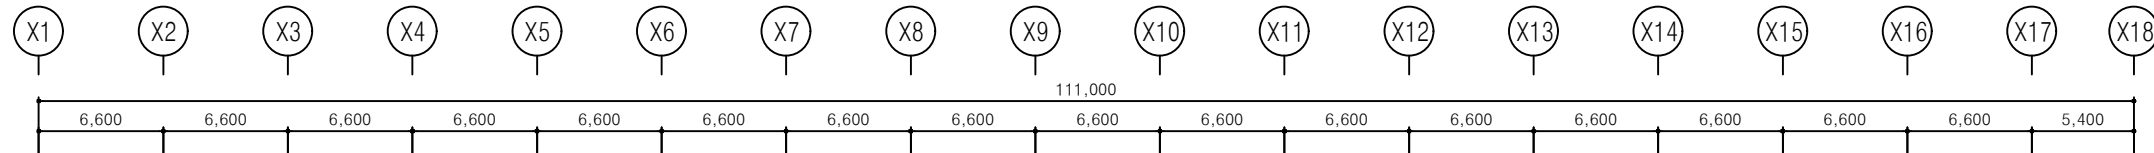

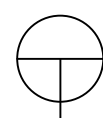
뇌과학부 2층 전등설비 평면도
 축척 A1: 1/200, A3: 1/400

3					
2					
1	14.11.18	시험/호실 수정			
REV	DATE	DESCRIPTION	DRN	CHK	APR
DRAWING TITLE					
뇌과학부 2층 전등설비 평면도					
APPROVED					
CHECKED1					
CHECKED2					
DRAWN					
PROJECT NO.					
SCALE					
A1	A3	APPROVAL DATE			
1/200	1/400	2014.04			
DRAWING NO.					REV.
E-13-0704					

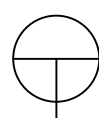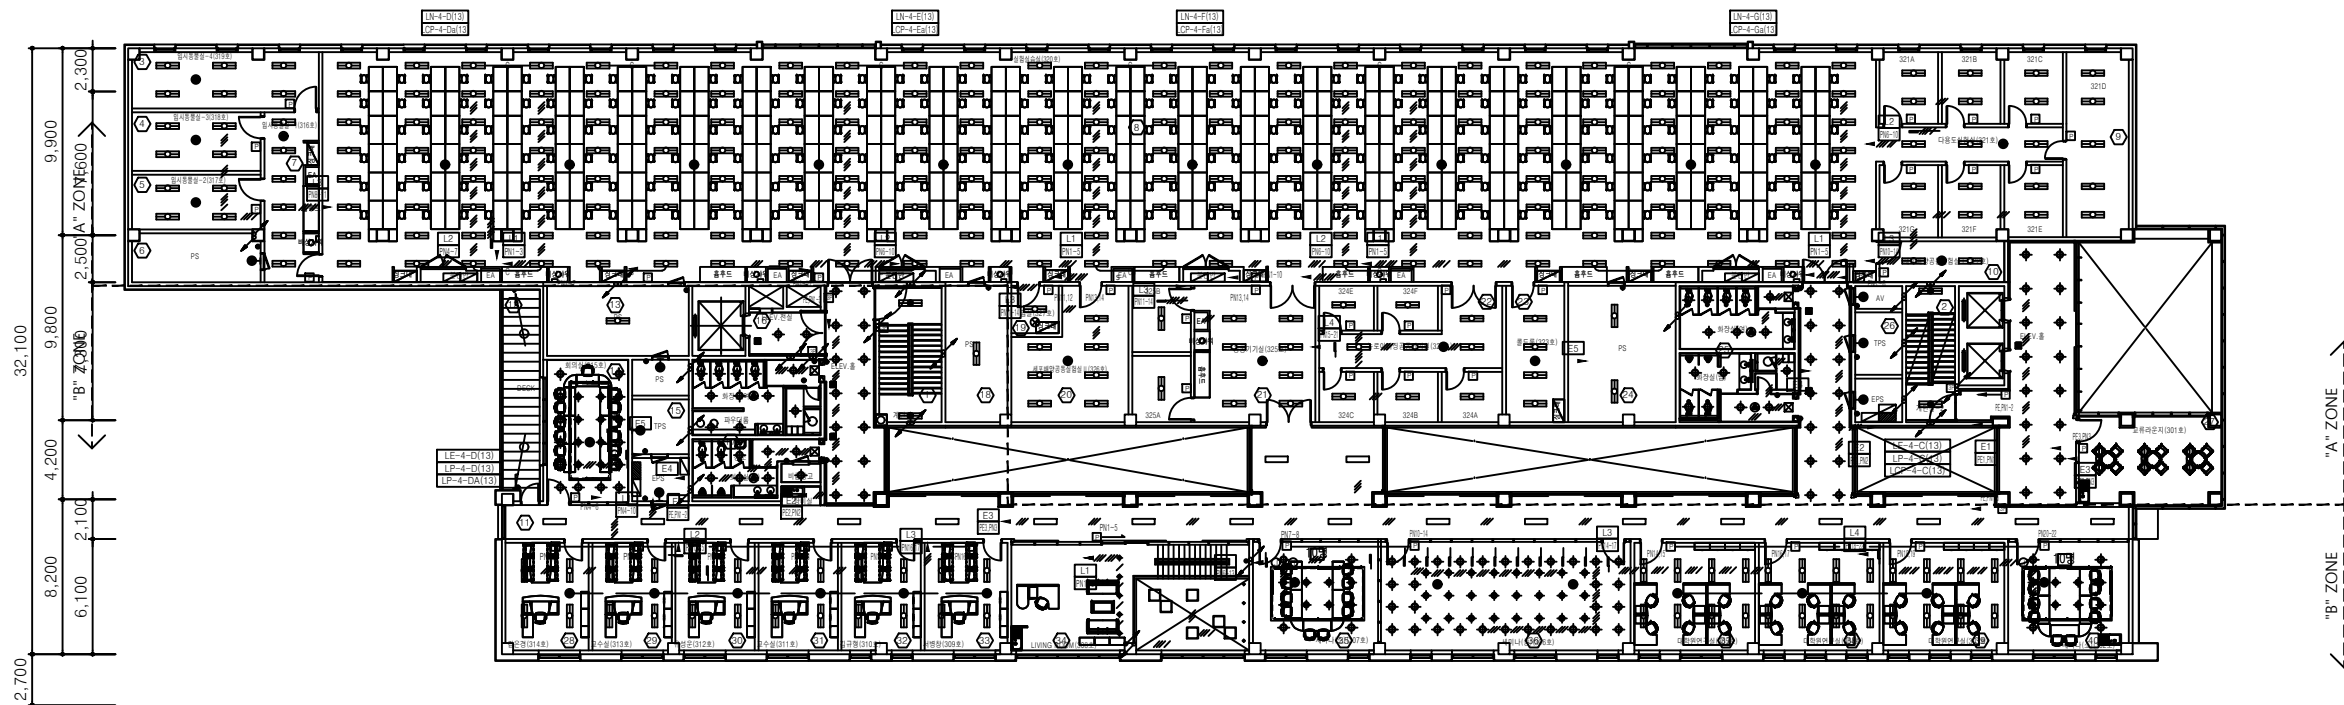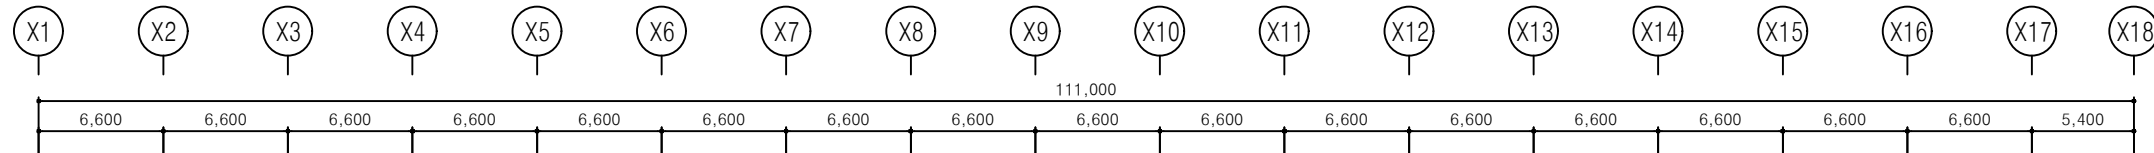

뇌과학부 3층 전등설비 평면도

축척 A1: 1/200, A3: 1/400

학위과정시설 임대형민자사업(BTL)

Construction

現代建設

TEL. 053)615-5093~6 FAX. 053)615-5097

Construction Management




SAMOOO.C.M.
Construction Management

TEL. 053)611-3071 FAX. 053)611-3073

NOTE

1. 실험실내의 전등설비용 공배관 설치.
— C — : EMPTY PIPE (CD 22C)

3					
2					
1	14.11.18	실험/호실 수정			
REV	DATE	DESCRIPTION	DRN	CHK	APR
DRAWING TITLE					
뇌과학부 3층 전등설비 평면도					
APPROVED					
CHECKED1					
CHECKED2					
DRAWN					
PROJECT NO.					
SCALE		APPROVAL DATE			
A1	A3	2014.04			
1/200	1/400				
DRAWING NO. E-13-0705					REV.

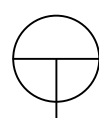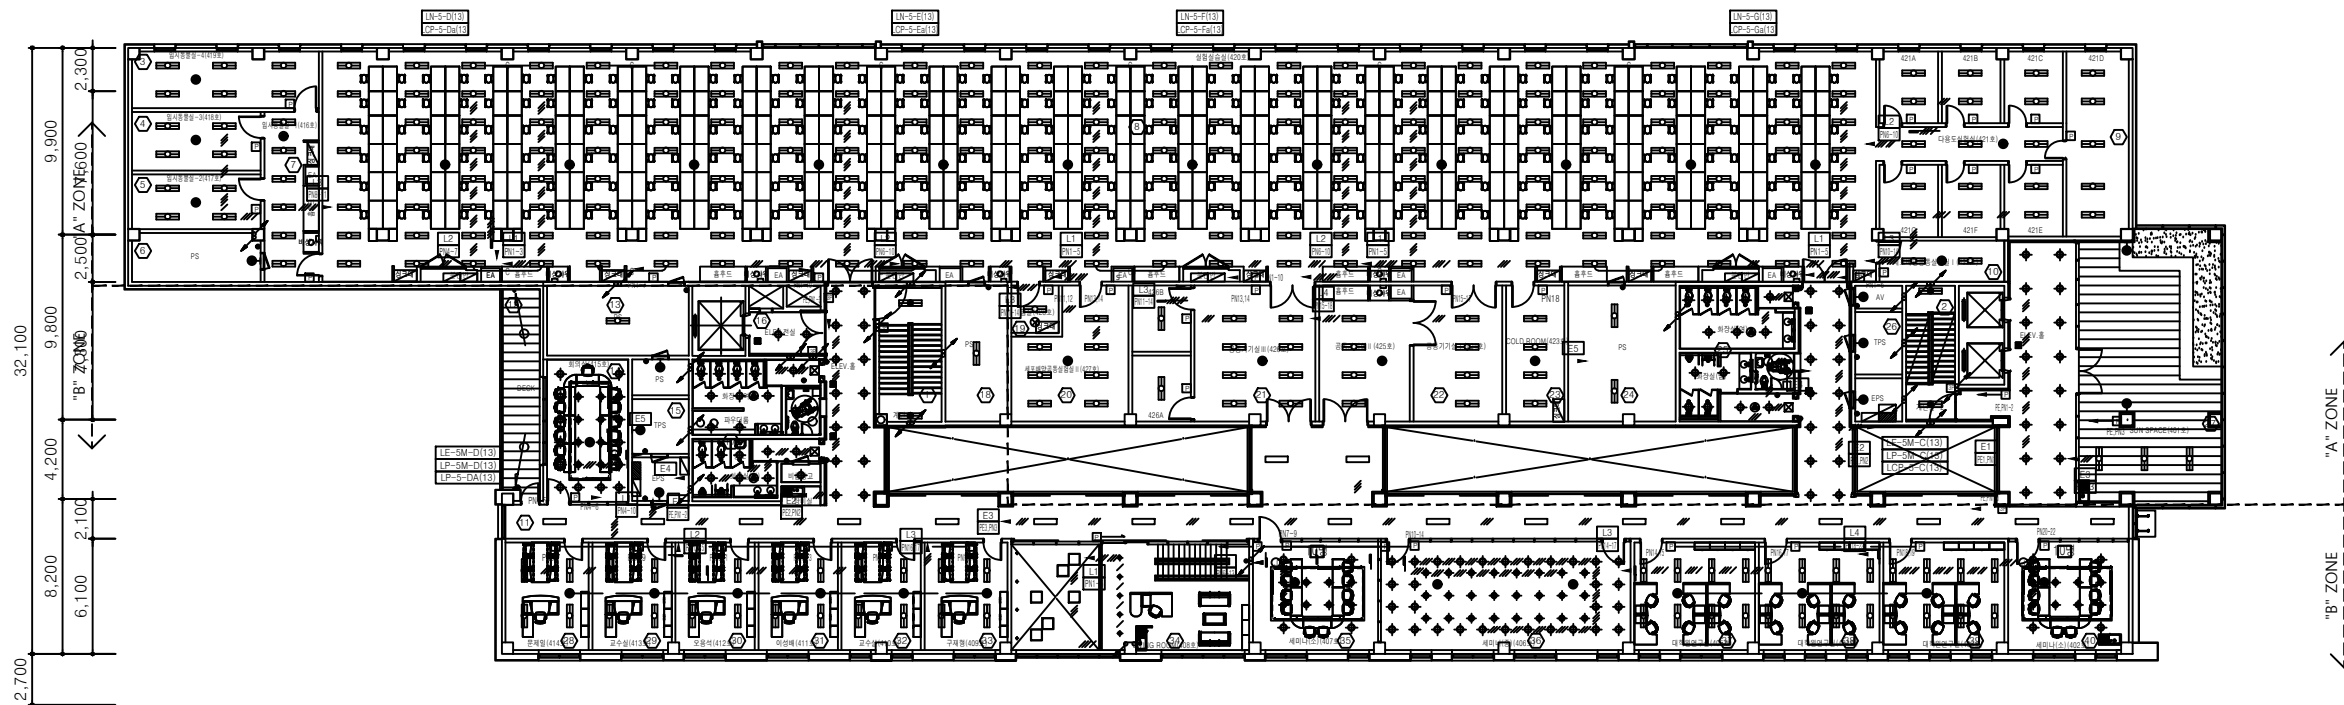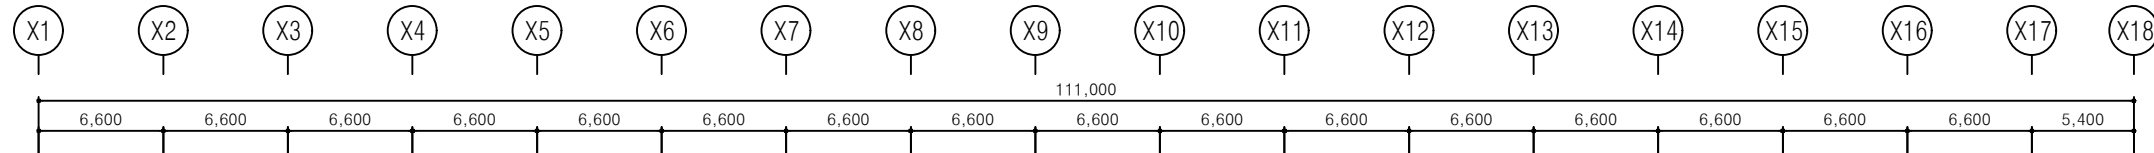

뇌과학부 4층 전등설비 평면도

축척 A1: 1/200, A3: 1/400

학위과정시설 임대형민자사업(BTL)

Construction



TEL. 053)615-5093~6 FAX. 053)615-5097

Construction Management



TEL. 053)611-3071 FAX. 053)611-3073

NOTE

1. 시험실내의 전등설비용 공배관 설치.
: EMPTY PIPE (CD 22C)

3				
2				
1	14.11.18	실명/호실 수정		
REV	DATE	DESCRIPTION	DRN	CHK
APR				

DRAWING TITLE

뇌과학부
4층 전등설비 평면도

APPROVED

CHECKED1




CHECKED2

DRAWN

PROJECT NO.

SCALE	APPROVAL DATE
A1 1/200	2014.04
A3 1/400	

DRAWING NO.	REV.
E-13-0706	

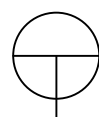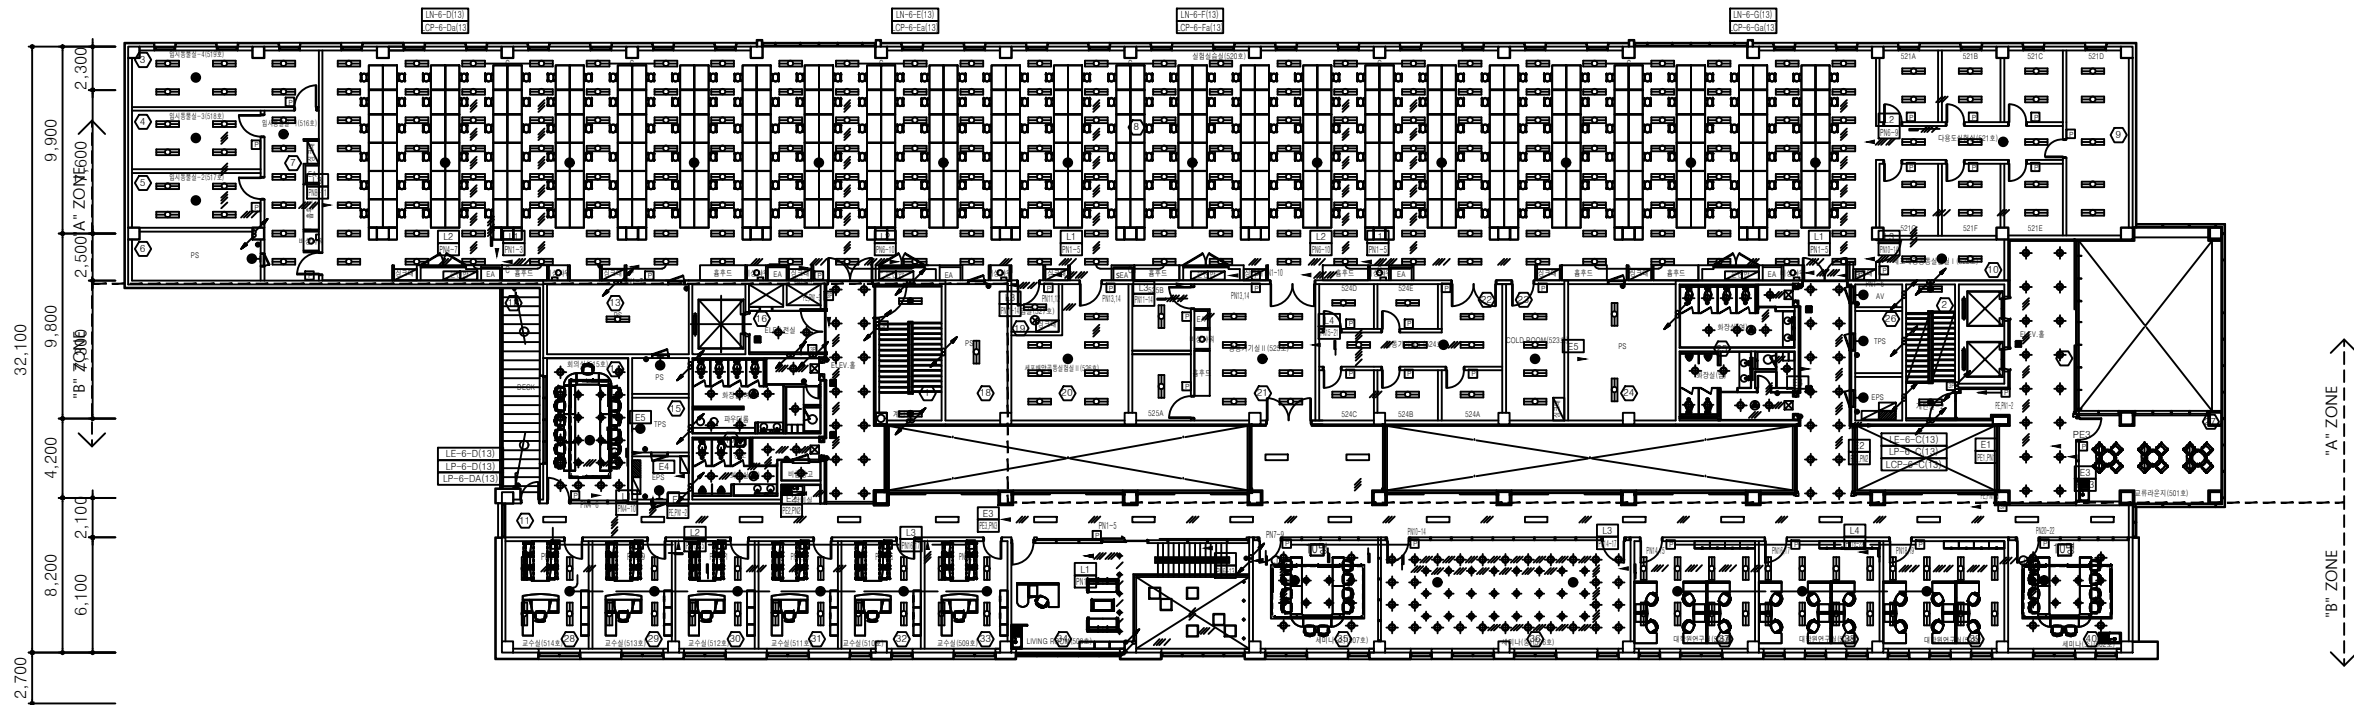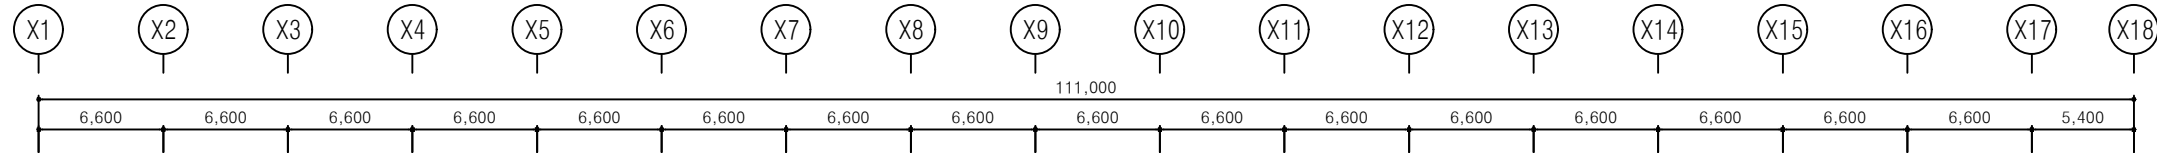

뇌과학부 5층 전등설비 평면도

축척 A1: 1/200, A3: 1/400

학위과정시설 임대형민자사업(BTL)

Construction

現代建設

TEL. 053)615-5093~6 FAX. 053)615-5097

Construction Management




SAMOOO.C.M.
Construction Management

TEL. 053)611-3071 FAX. 053)611-3073

NOTE

- 실점실내의 전등설비용 공배관 설치.
— C — : EMPTY PIPE (CD 22C)

3					
2					
1	14.11.18	실명/호실 수정			
REV	DATE	DESCRIPTION	DRN	CHK	APR
DRAWING TITLE					
뇌과학부 5층 전등설비 평면도					
APPROVED					
CHECKED1					
CHECKED2					
DRAWN					
PROJECT NO.					
SCALE			APPROVAL DATE		
A1	A3		2014.04		
1/200	1/400				
DRAWING NO.				REV.	
E-13-0707					

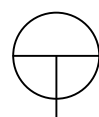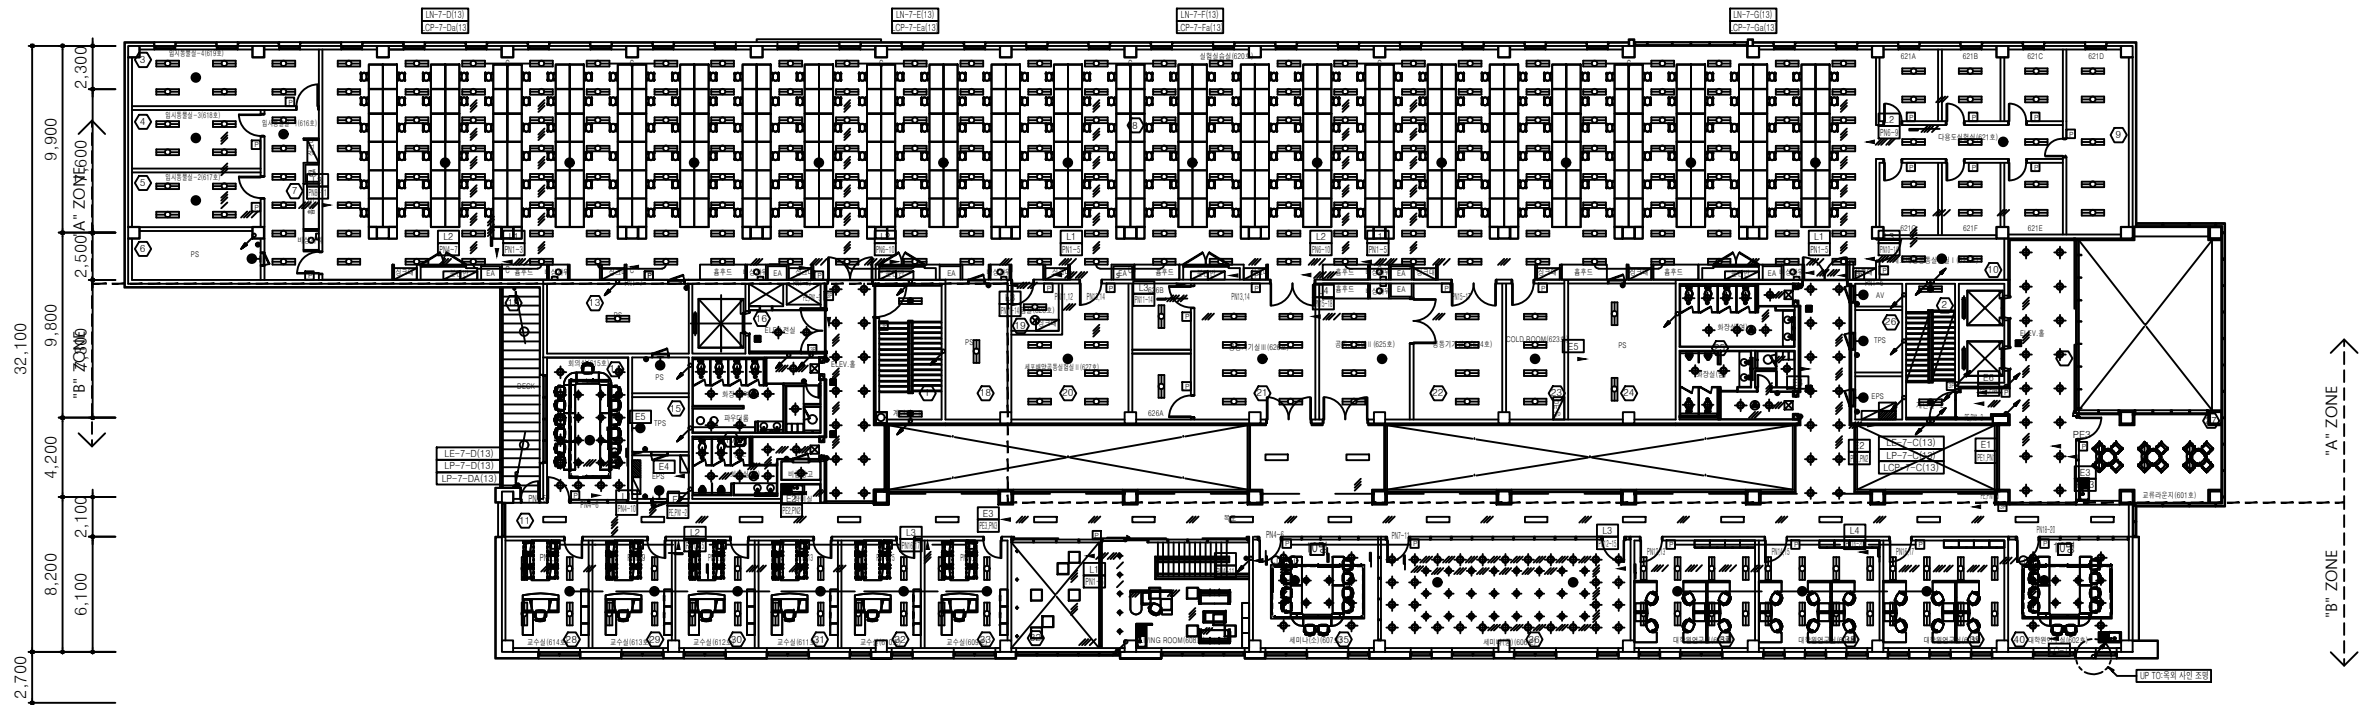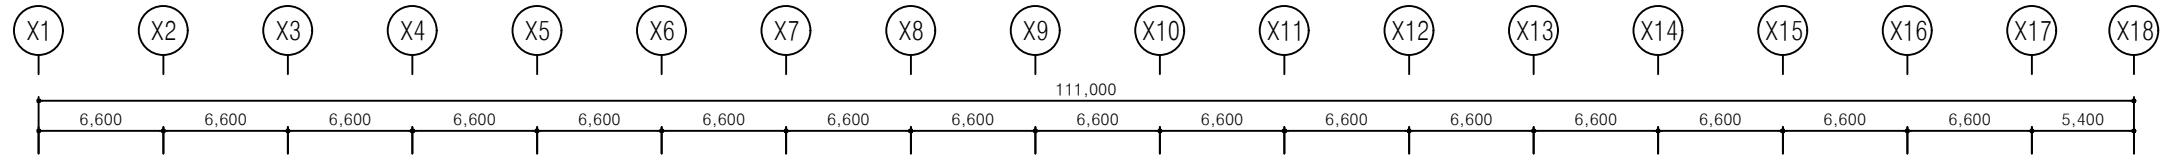

뇌과학부 6층 전등설비 평면도

축척 A1: 1/200, A3: 1/400

학위과정시설 임대형민자사업(BTL)

Construction

現代建設

TEL. 053)615-5093~6 FAX. 053)615-5097

Construction Management





SAMOOO.C.M.
Construction Management

TEL. 053)611-3071 FAX. 053)611-3073

NOTE

1. 실험실내의 전등설비용 공배관 설치.
— C — : EMPTY PIPE (CD 22C)

3					
2					
1	14.11.19	실험/호실 수정			
REV	DATE	DESCRIPTION	DRN	CHK	APR
DRAWING TITLE					
뇌과학부 6층 전등설비 평면도					
APPROVED					
CHECKED1					
CHECKED2					
DRAWN					
PROJECT NO.					
SCALE		APPROVAL DATE			
A1	A3	2014.04			
1/200	1/400				
DRAWING NO.					REV.
E-13-0708					

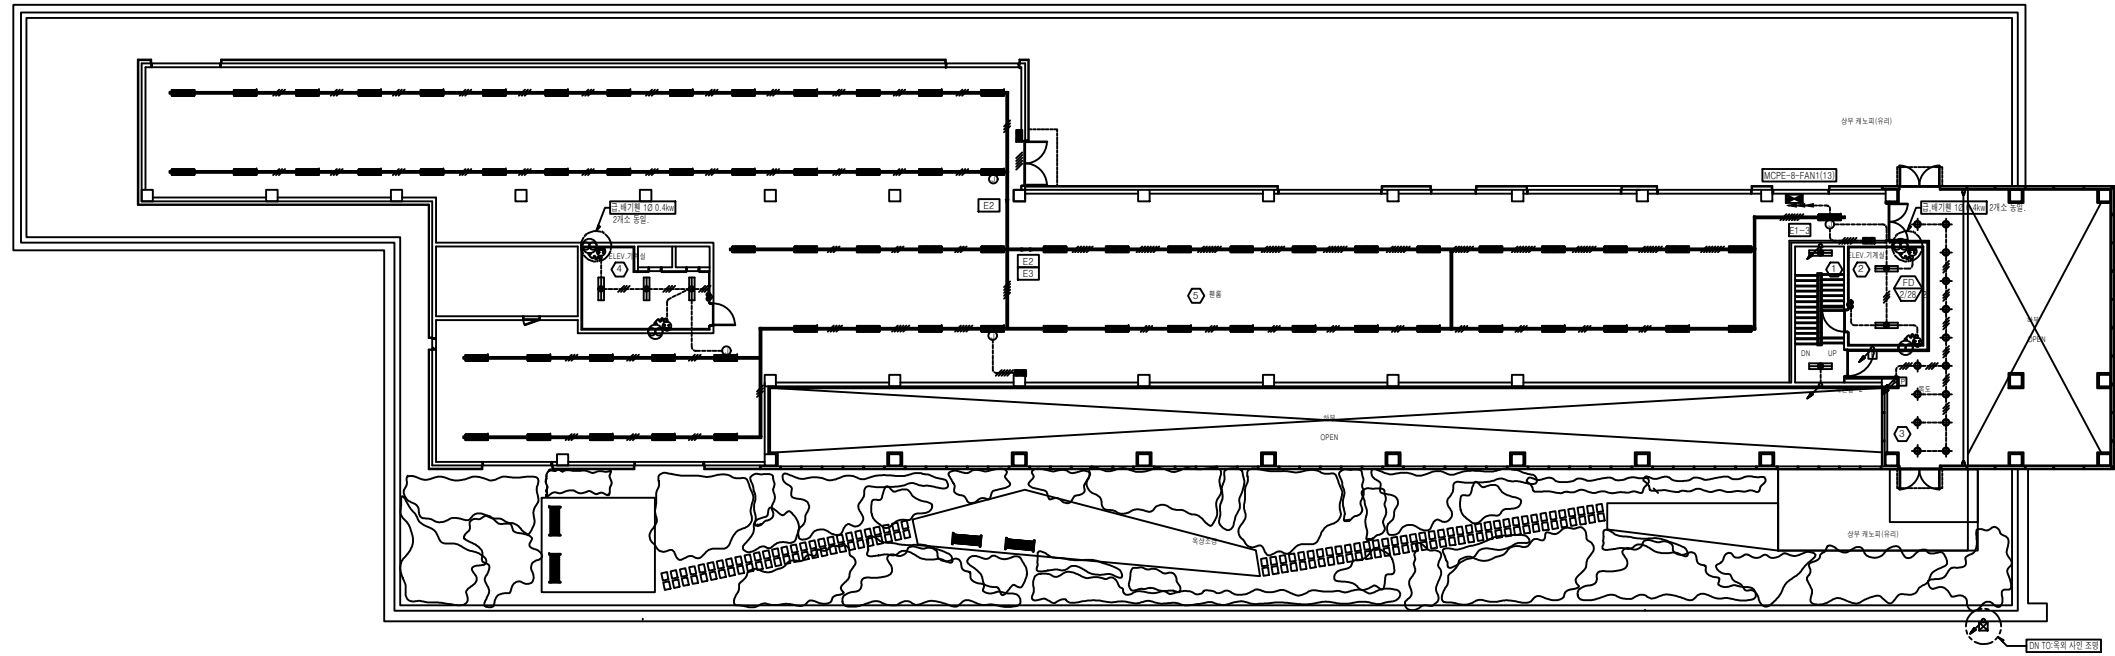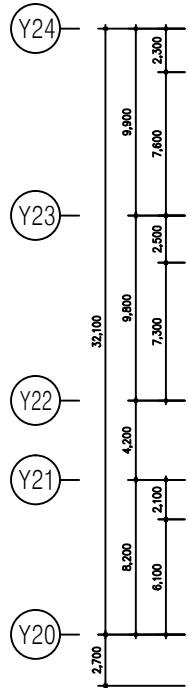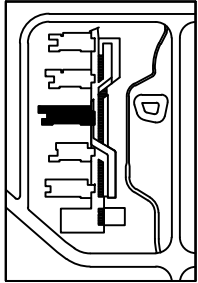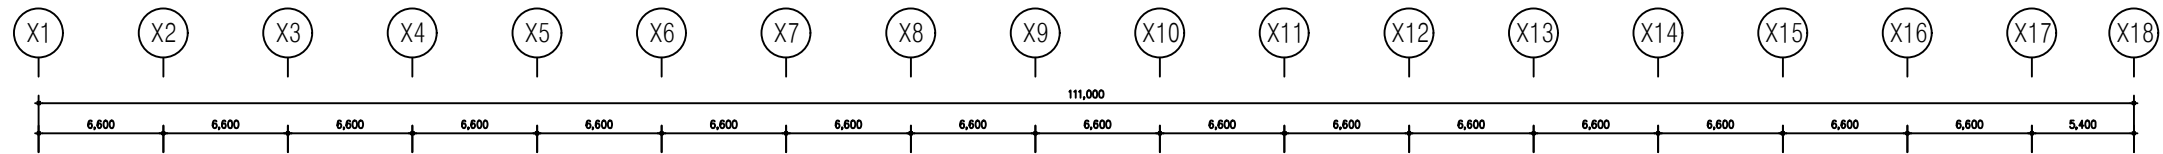

1. 시험실내의 전등설비용 공배관 설치.
— C — : EMPTY PIPE (CD 22C)

3					
2					
1	14.11.18	시험/호실 수정			
REV	DATE	DESCRIPTION	DRN	CHK	APR

DRAWING TITLE

뇌과학부
7층 전등설비 평면도

APPROVED

CHECKED1

CHECKED2

DRAWN

PROJECT NO.

SCALE	APPROVAL DATE
A1 1/200	A3 1/400
	2014.04

DRAWING NO.	REV.
E-13-0709	

뇌과학부 7층 전등설비 평면도
축척 A1: 1/200, A3: 1/400