
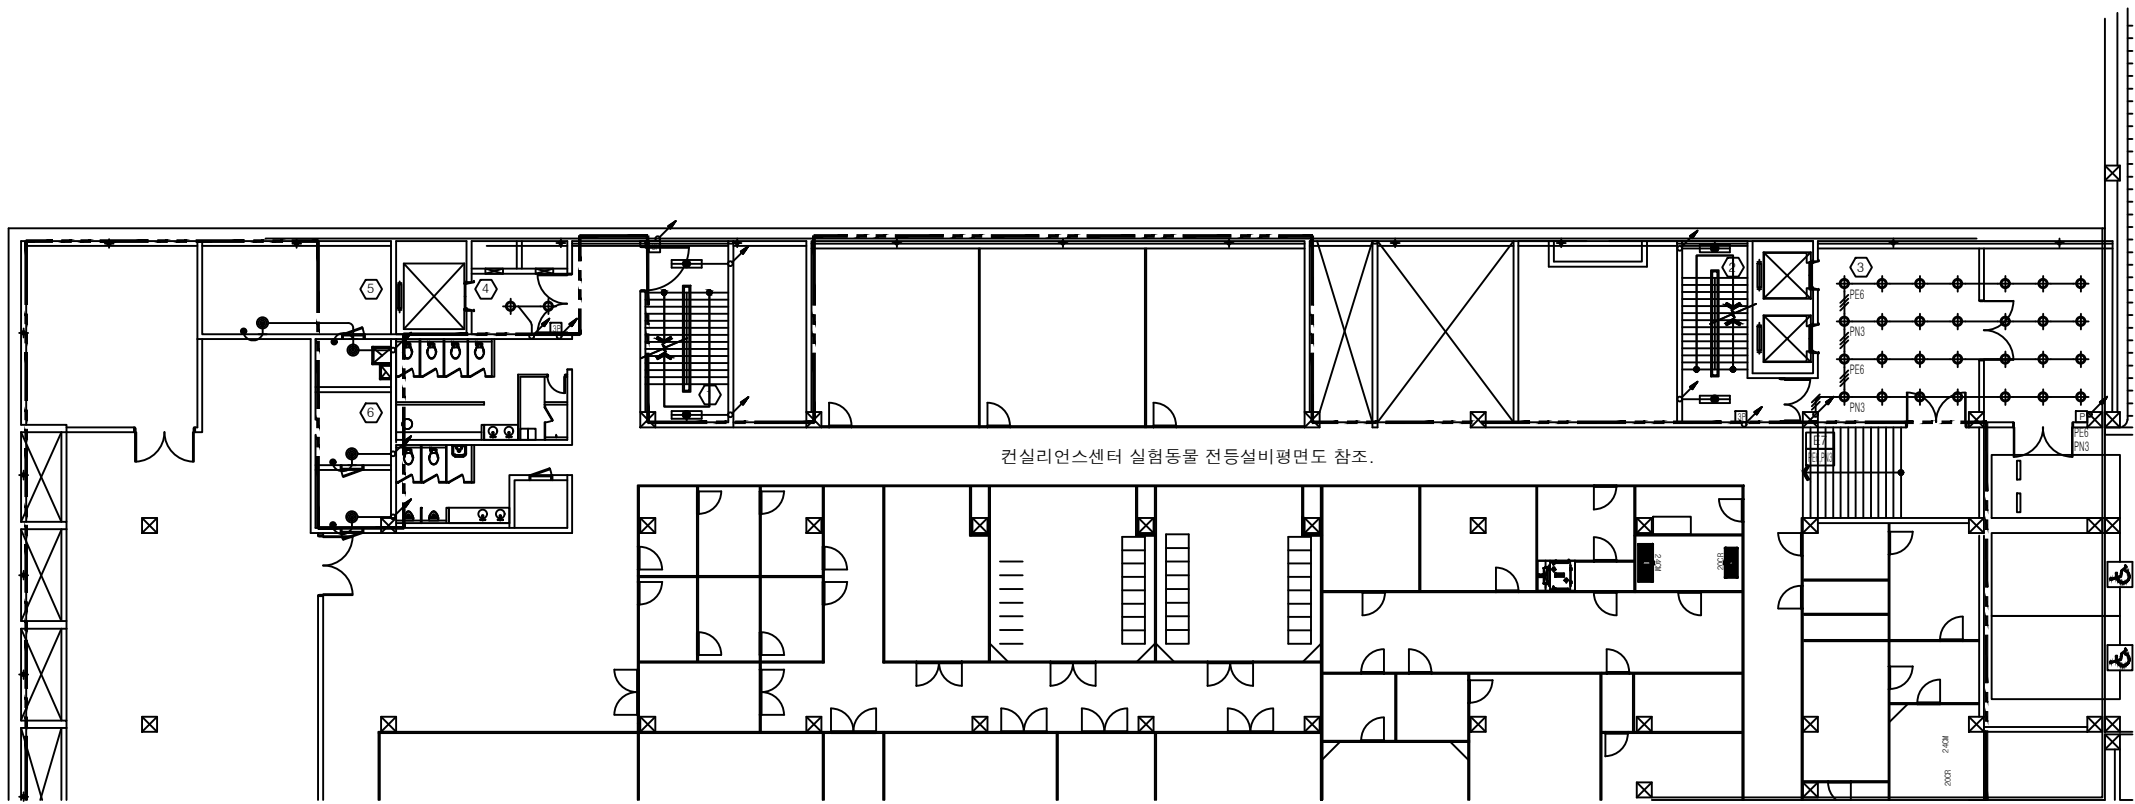
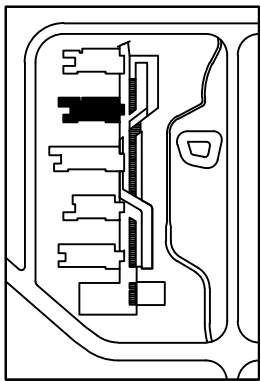
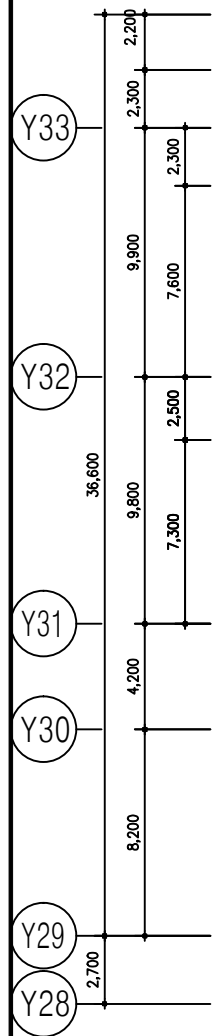


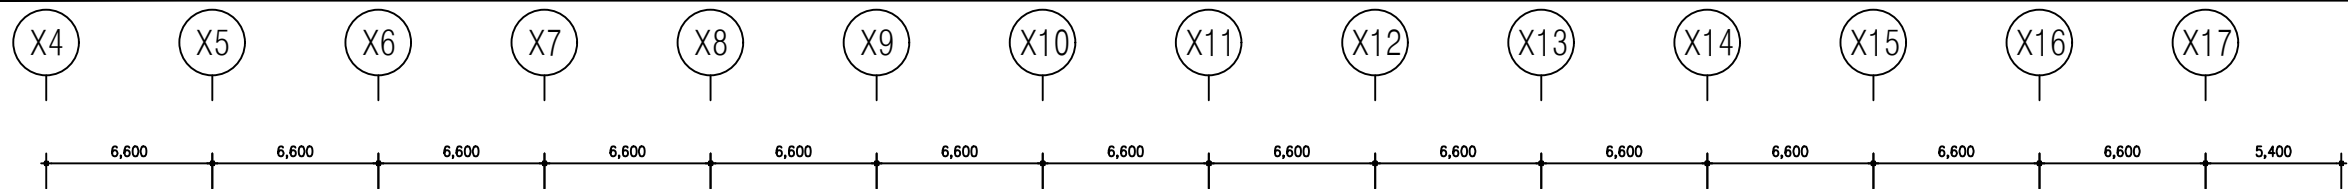

로봇공학부 지하 1층 전등설비 평면도
축척 A1: 1/150, A3: 1/300

1. 실험실내의 전등설비용 공배관 설치.
: EMPTY PIPE (CD 22C)

3					
2					
1	14.11.18	실명/호실 수정			
REV	DATE	DESCRIPTION	DRN	CHK	APR

DRAWING TITLE

로봇공학부
지하 1층 전등설비 평면도

APPROVED

CHECKED1

CHECKED2

DRAWN

PROJECT NO.

SCALE

A1 1/150 A3 1/300



APPROVAL DATE

2014.04

DRAWING NO.

E-14-0701



REV.

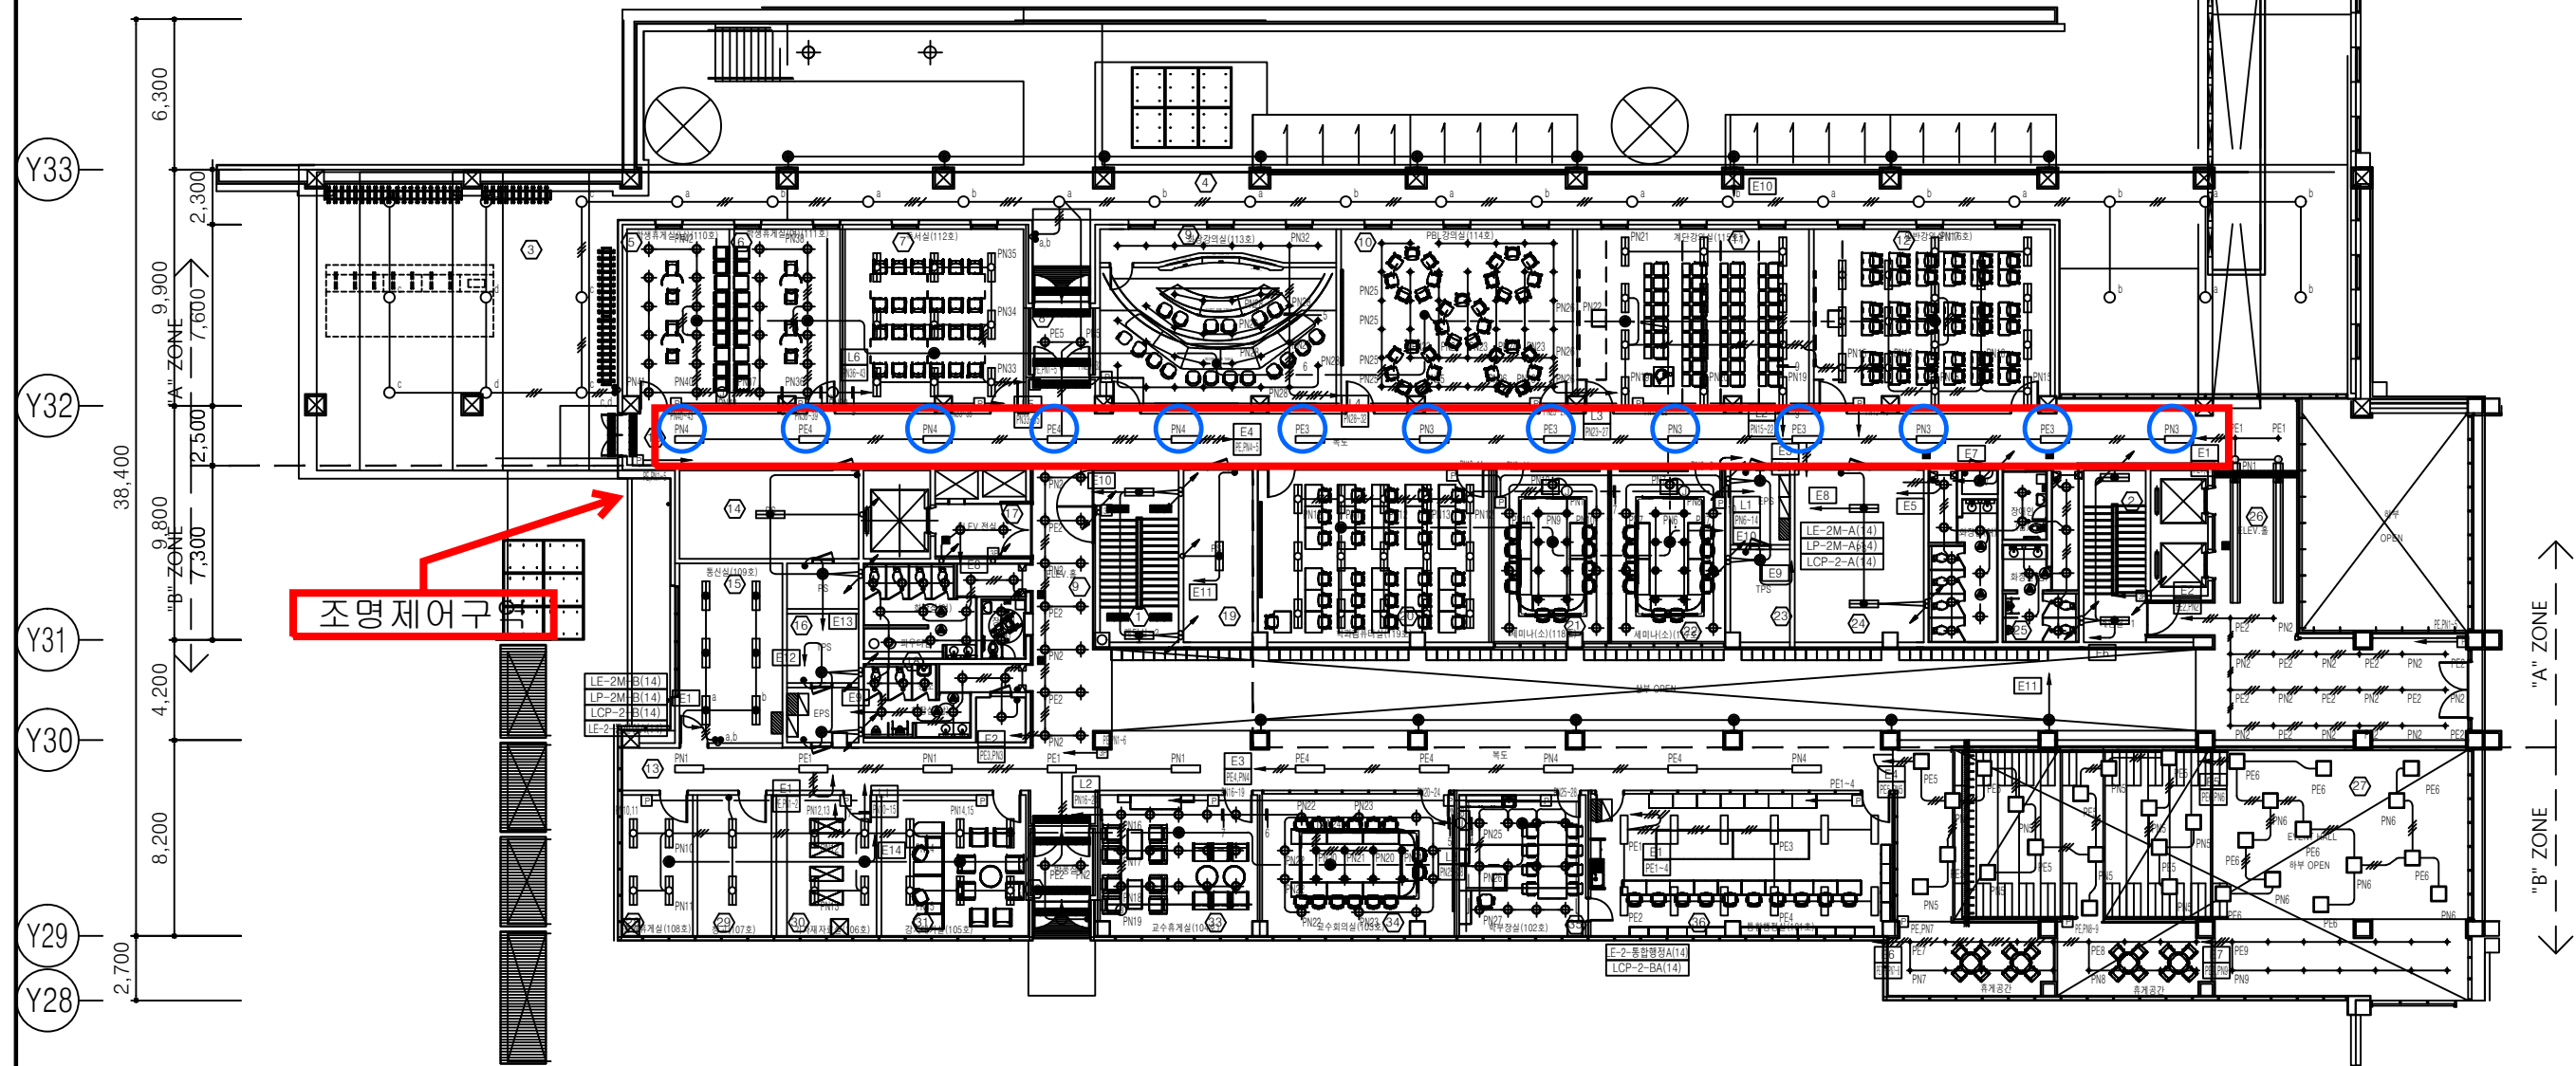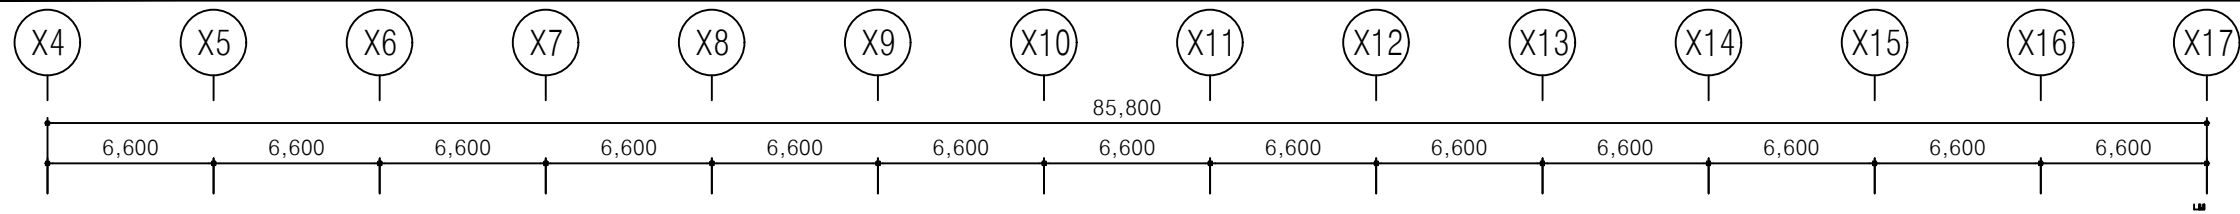

조명 제어구역

로봇공학부 1층 전등설비 평면도
축척 A1: 1/150, A3: 1/300

3					
2					
1	14.11.18	실명/호실 수정			
REV	DATE	DESCRIPTION	DRN	CHK	APR
DRAWING TITLE					
로봇공학부 1층 전등설비 평면도					
APPROVED					
CHECKED1					
CHECKED2					
DRAWN					
PROJECT NO.					
SCALE					
A1	A3	APPROVAL DATE			
1/150	1/300	2014.04			
DRAWING NO.					REV.
E-14-0703					

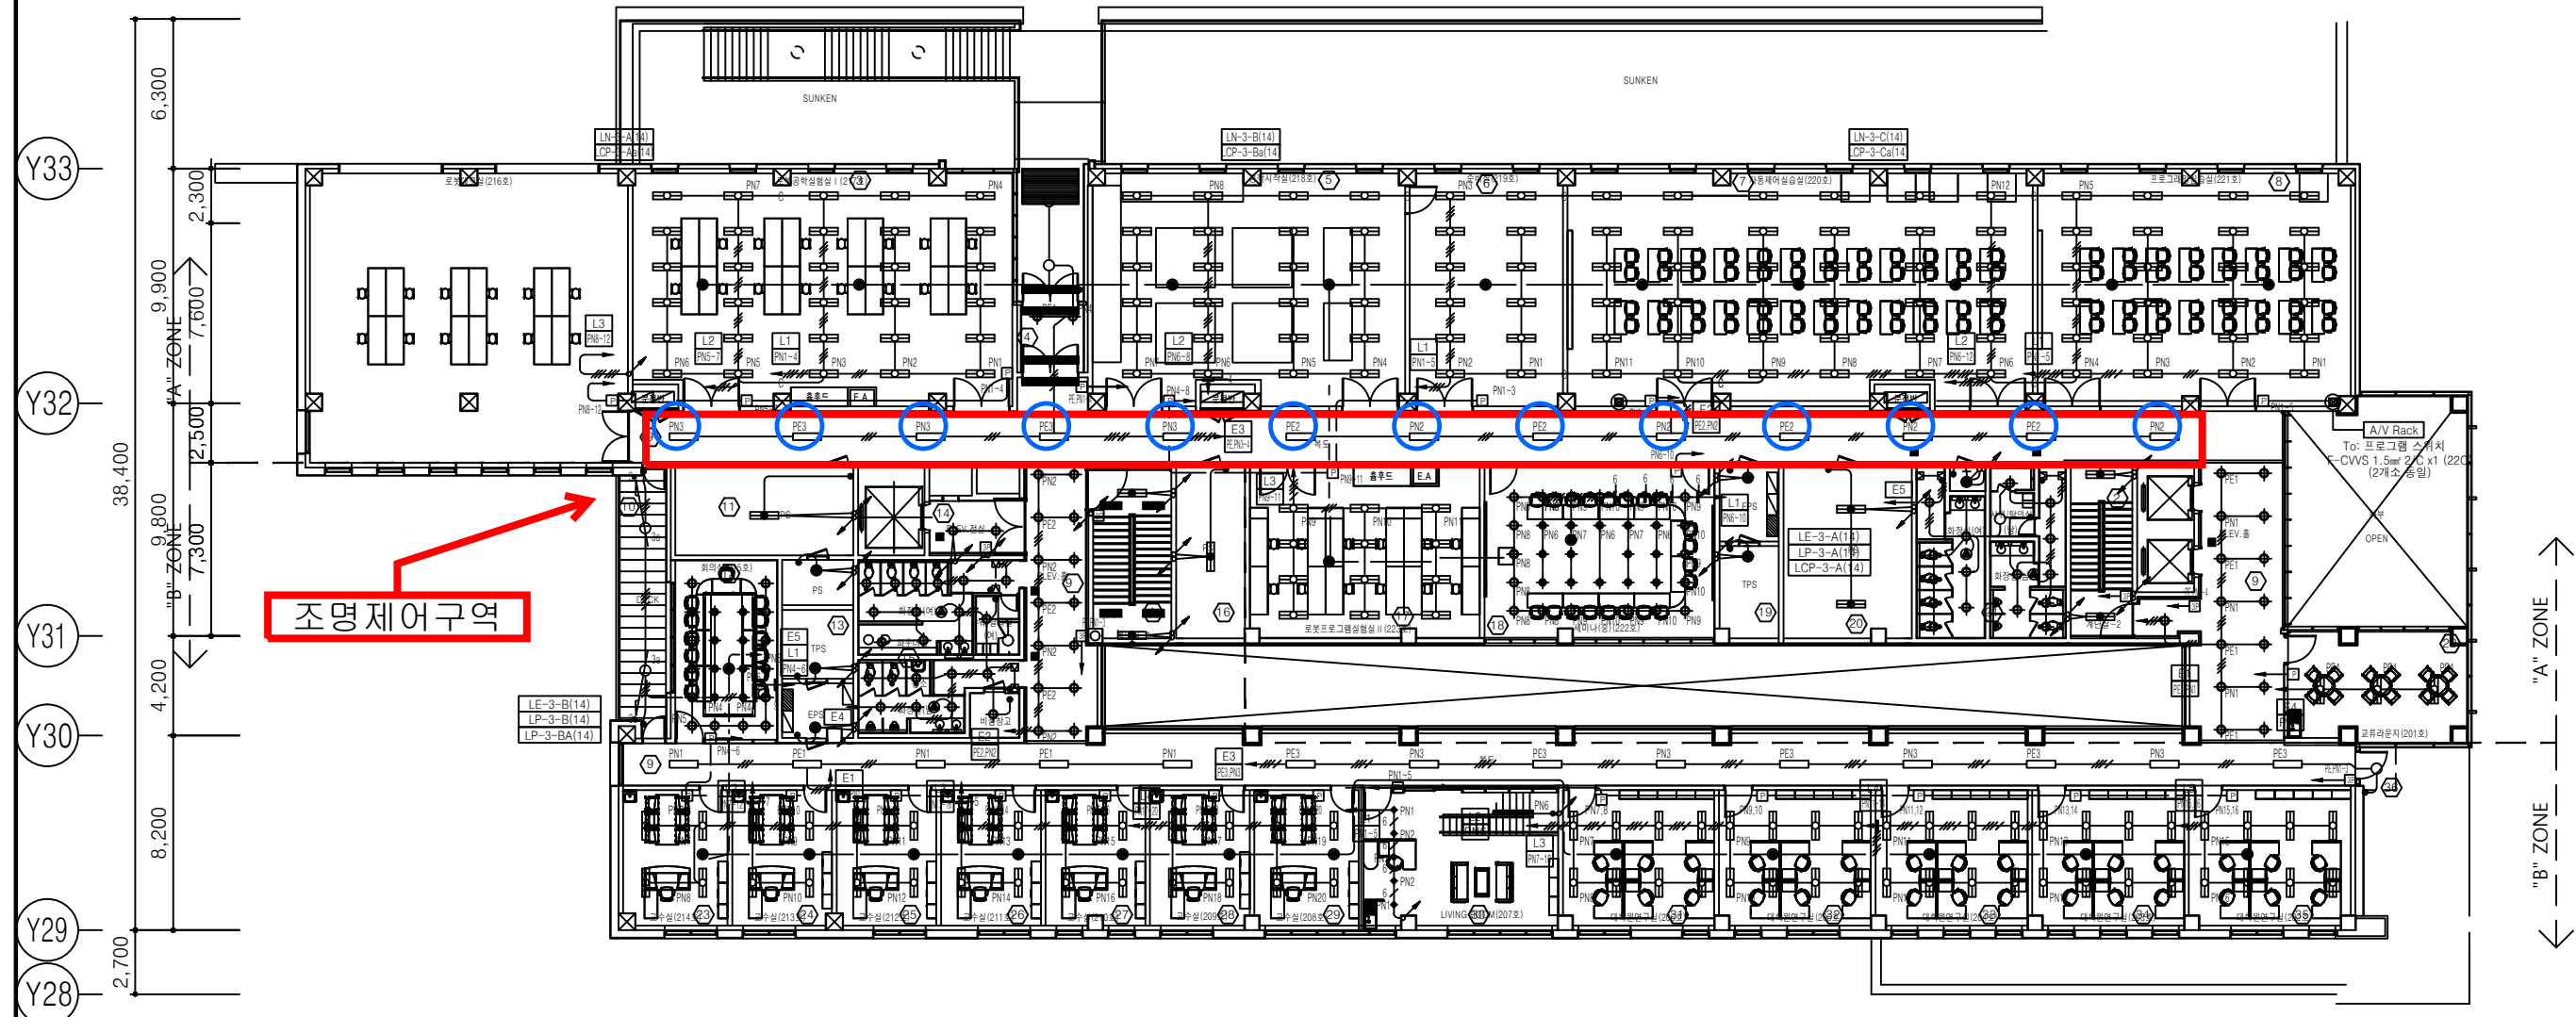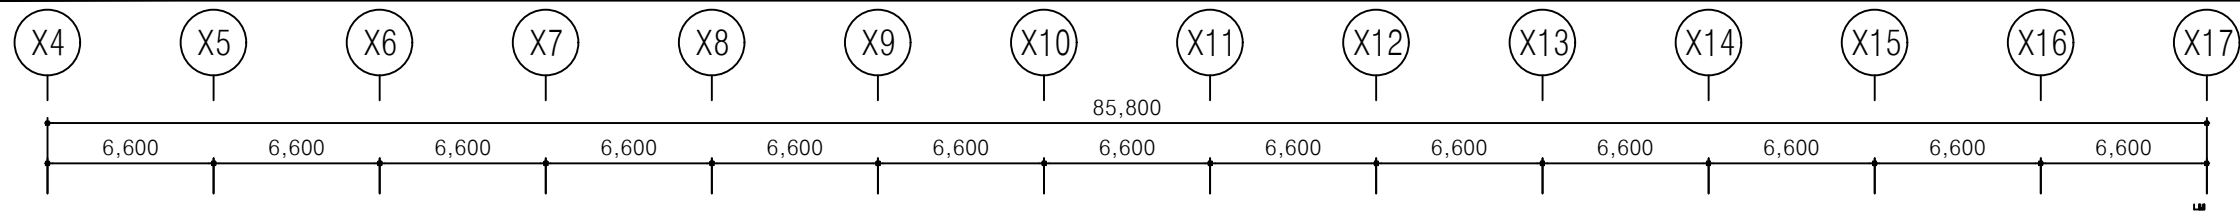

조명제어구역

로봇공학부 2층 전등설비 평면도
축척 A1: 1/150, A3: 1/300

학위과정시설 임대형민자사업(BTL)

Construction

現代建設

TEL. 053)615-5093~6 FAX. 053)615-5097

Construction Management




SAMOOO.C.M.
Construction Management

TEL. 053)611-3071 FAX. 053)611-3073

NOTE

1. 실험실내의 전등설비용 공배관 설치.
— : EMPTY PIPE (CD 22C)




3					
2					
1	14.11.18	실명/호실 수정			
REV	DATE	DESCRIPTION	DRN	CHK	APR
DRAWING TITLE					
로봇공학부 2층 전등설비 평면도					
APPROVED					
CHECKED1					
CHECKED2					
DRAWN					
PROJECT NO.					
SCALE					
A1	A3	APPROVAL DATE			
1/150	1/300	2014.04			
DRAWING NO.					REV.
E-14-0704					

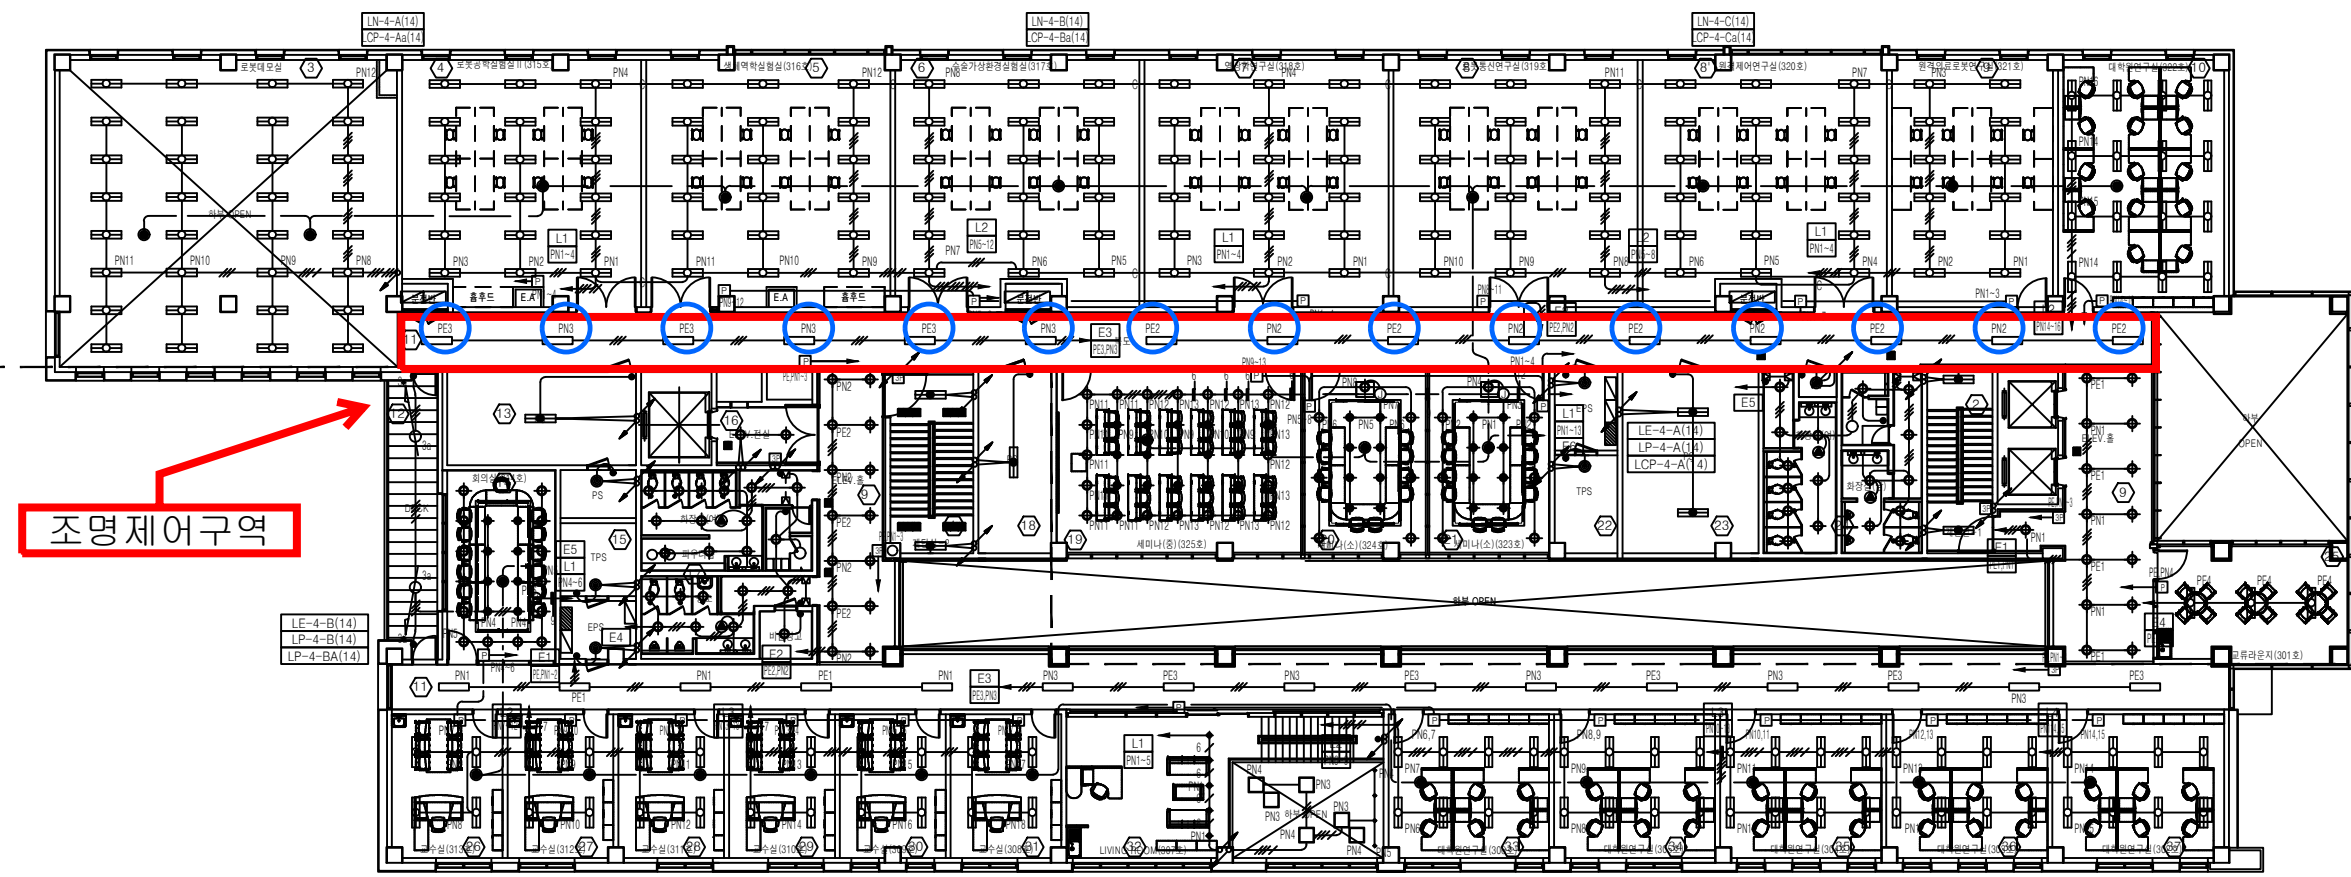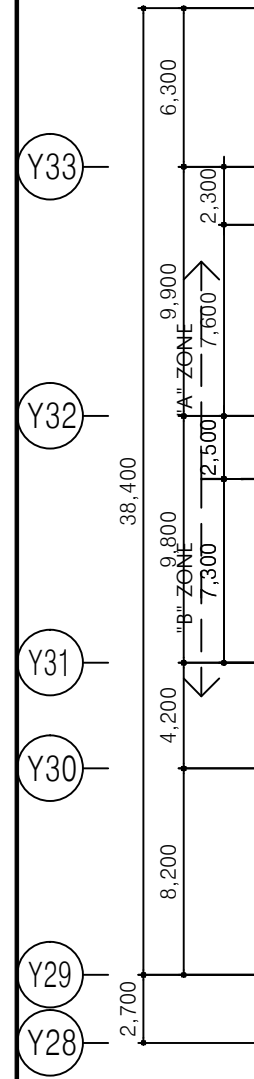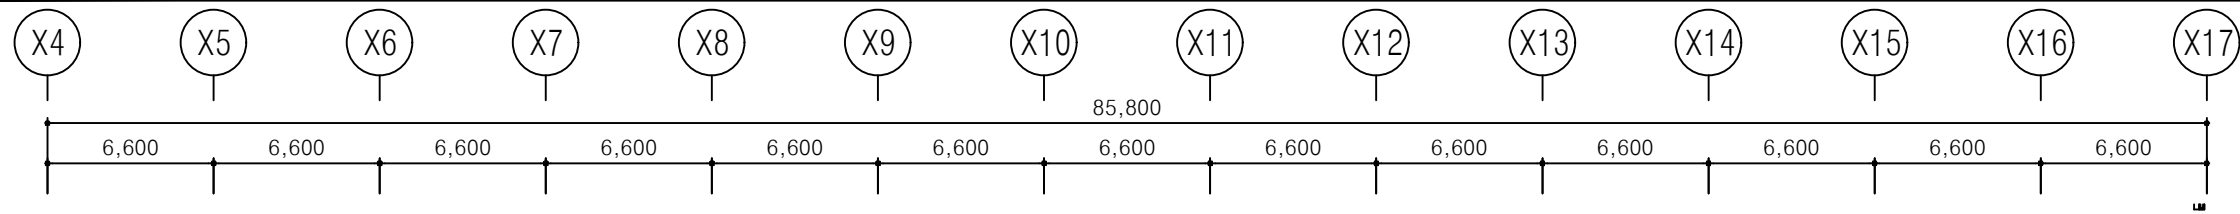

조명 제어구역

로봇공학부 3층 전등설비 평면도
축척 A1: 1/150, A3: 1/300




3					
2					
1	14.11.18	실명/호실 수정			
REV	DATE	DESCRIPTION	DRN	CHK	APR
DRAWING TITLE					
로봇공학부 3층 전등설비 평면도					
APPROVED					
CHECKED1					
CHECKED2					
DRAWN					
PROJECT NO.					
SCALE			APPROVAL DATE		
A1	A3		2014.04		
1/150	1/300				
DRAWING NO.				REV.	
E-14-0705				01	

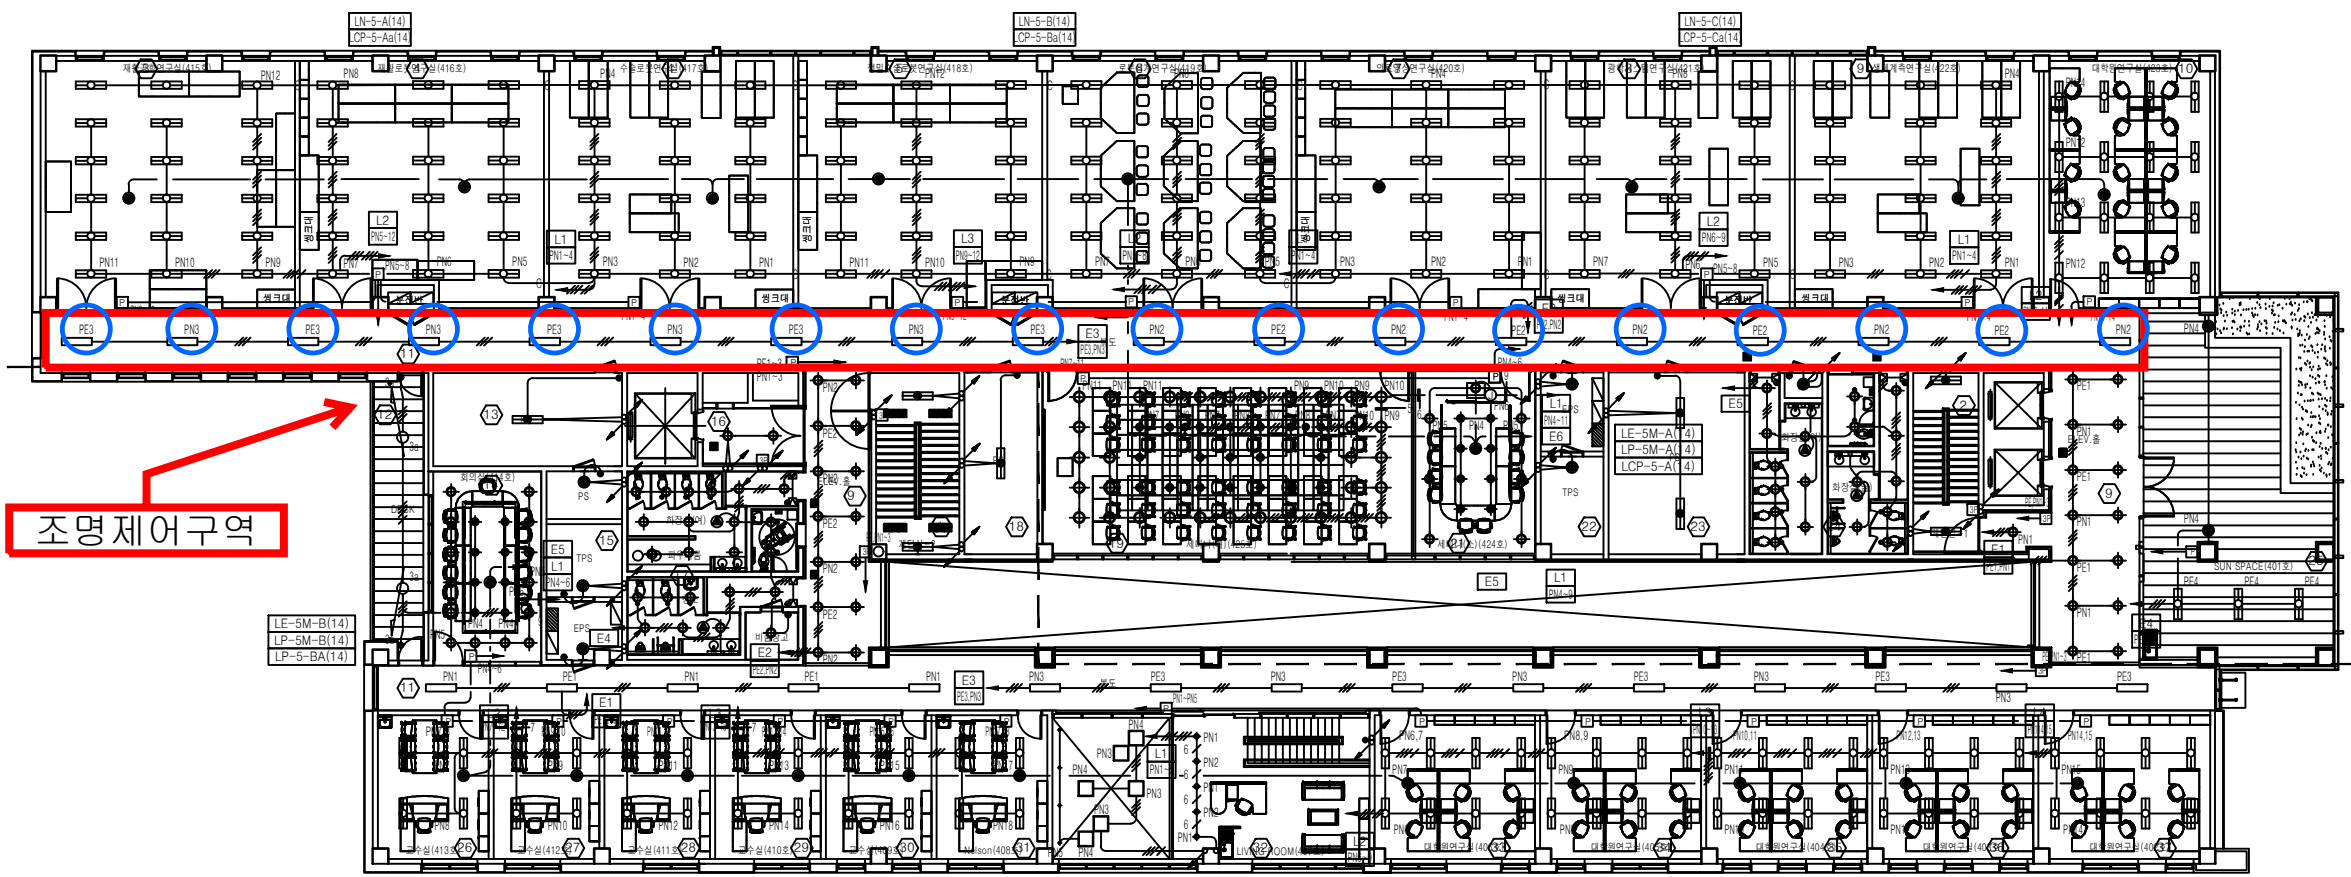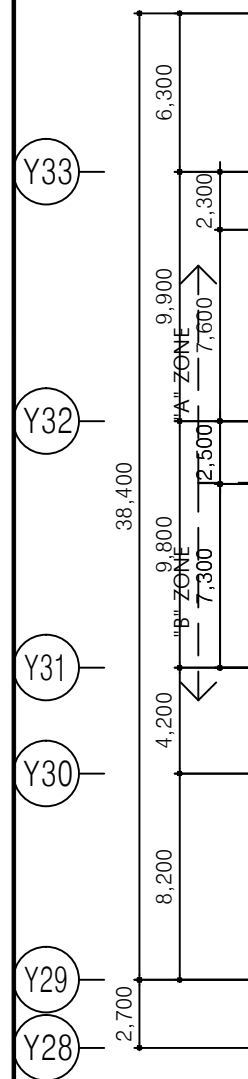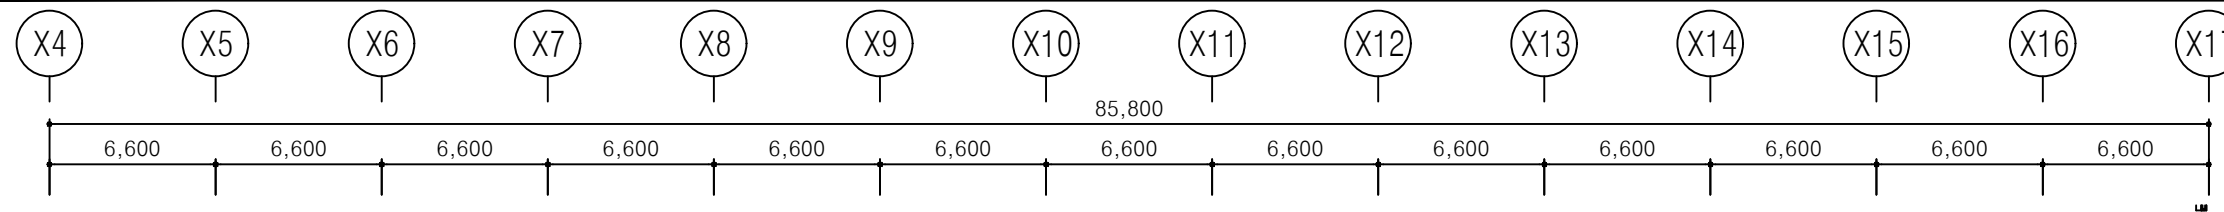

조명 제어구역

로봇공학부 4층 전등설비 평면도
축척 A1: 1/150, A3: 1/300




3					
2					
1	14.11.18	실명/호실 수정			
REV	DATE	DESCRIPTION	DRN	CHK	APR
DRAWING TITLE					
로봇공학부 4층 전등설비 평면도					
APPROVED					
CHECKED1					
CHECKED2					
DRAWN					
PROJECT NO.					
SCALE					
A1	1/150	A3	1/300	APPROVAL DATE	
				2014.04	
DRAWING NO.				REV.	
E-14-0706					

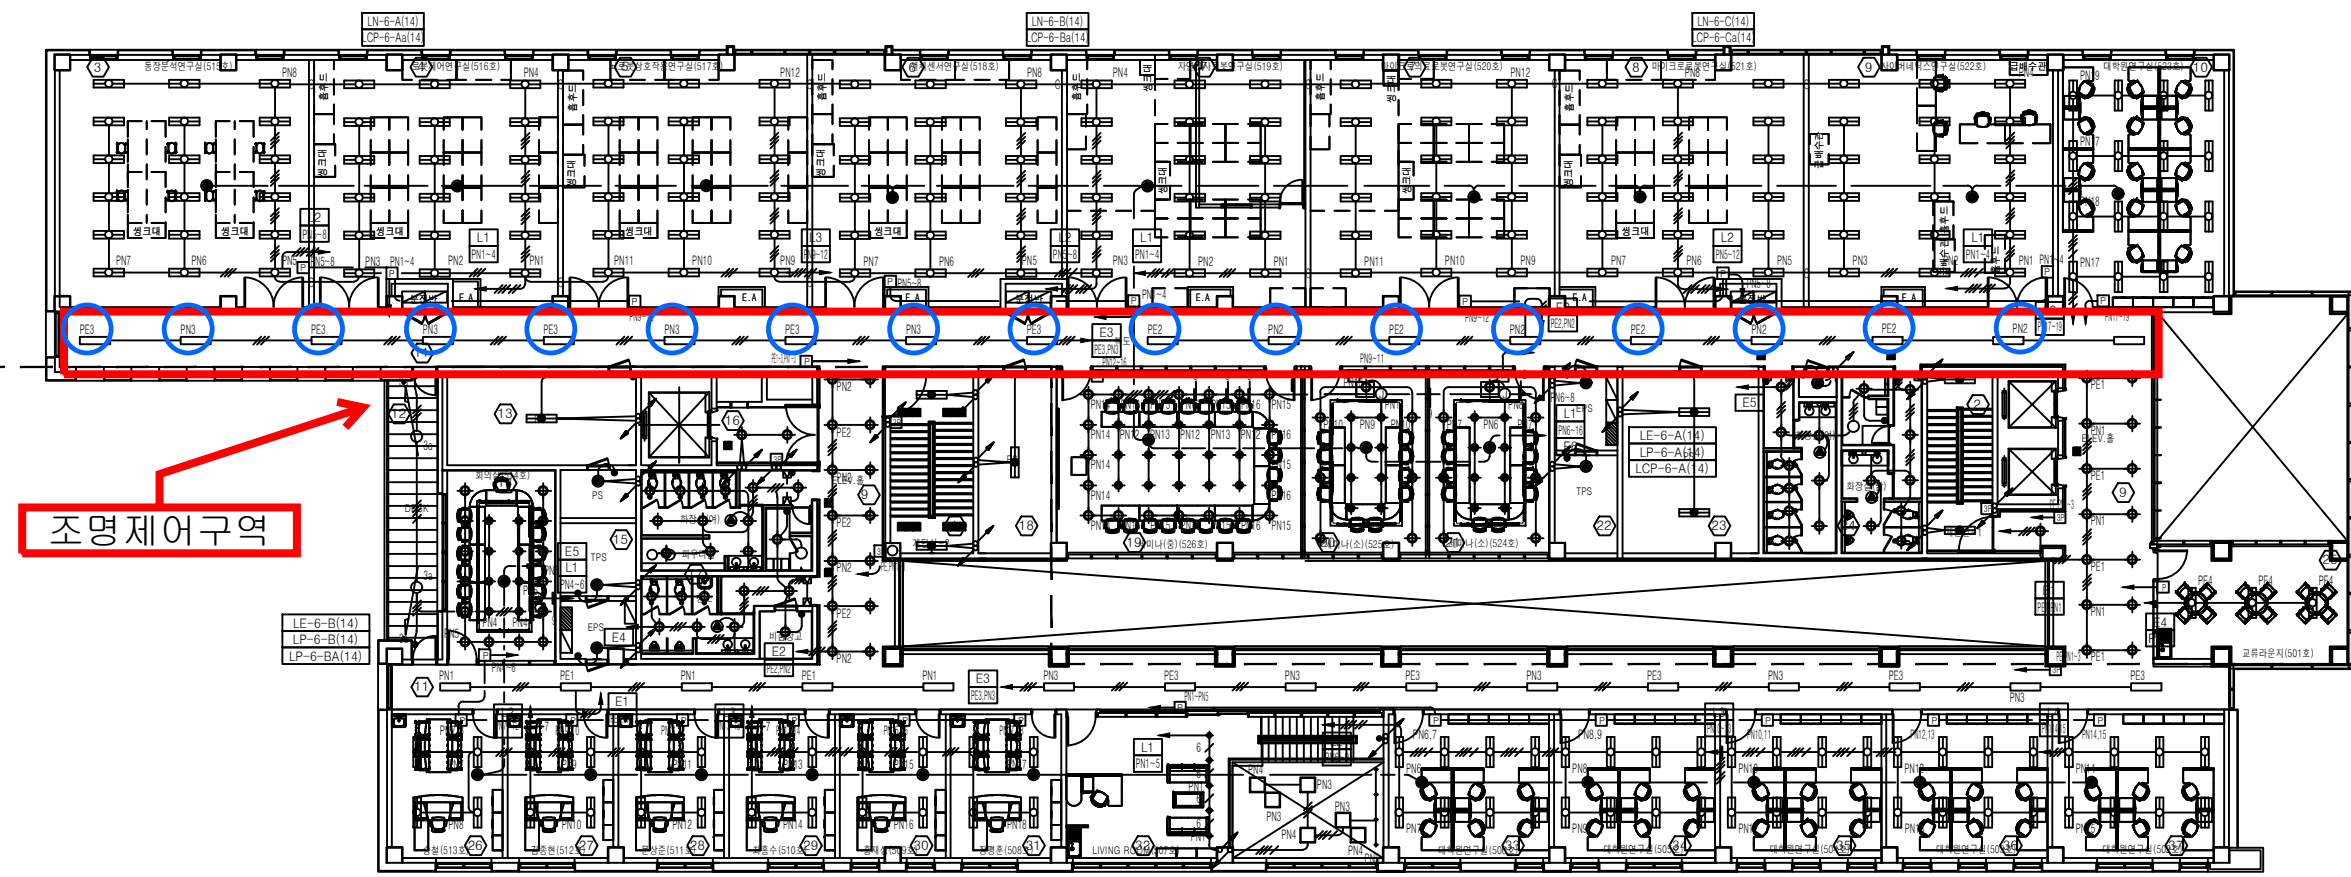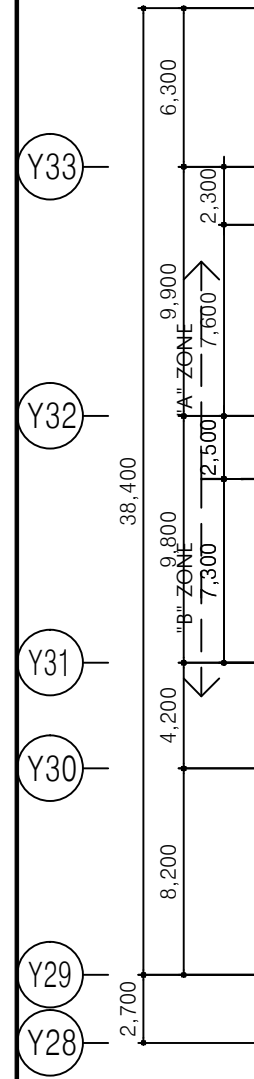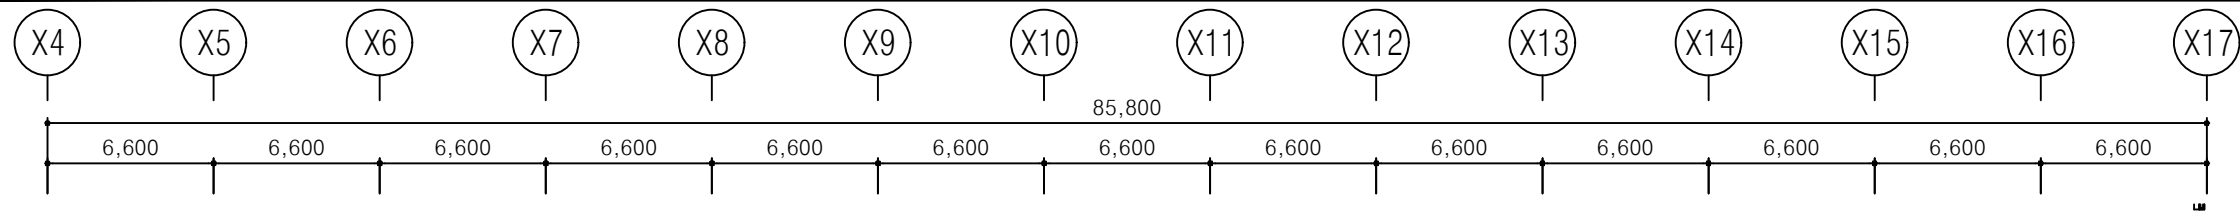

조명 제어구역

로봇공학부 5층 전등설비 평면도
축척 A1: 1/150, A3: 1/300

3					
2					
1	14.11.18	실명/호실 수정			
REV	DATE	DESCRIPTION	DRN	CHK	APR
DRAWING TITLE					
로봇공학부 5층 전등설비 평면도					
APPROVED					
CHECKED1					
CHECKED2					
DRAWN					
PROJECT NO.					
SCALE					
A1	1/150	A3	1/300	APPROVAL DATE	
				2014.04	
DRAWING NO.					REV.
E-14-0707					


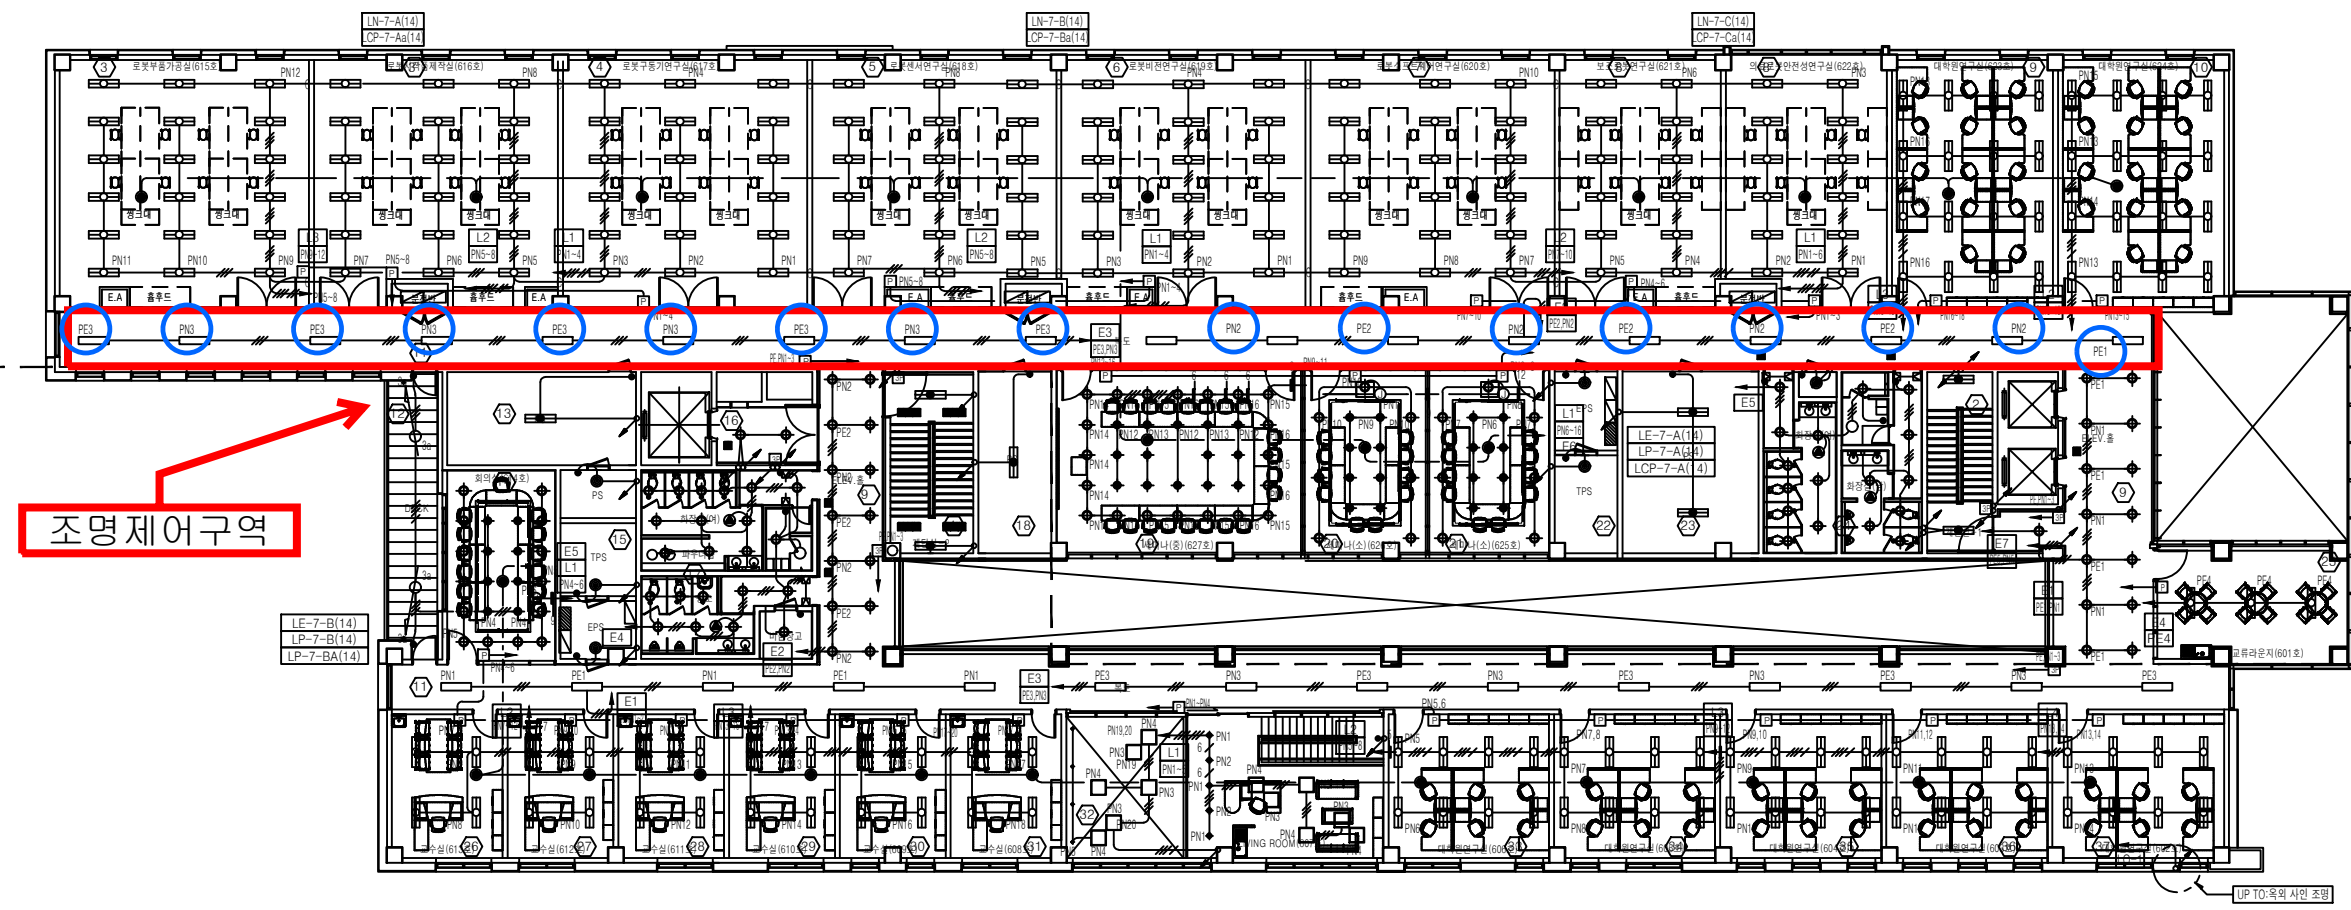
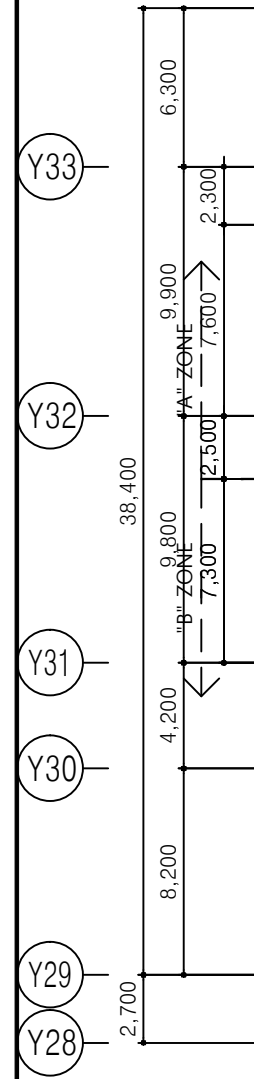
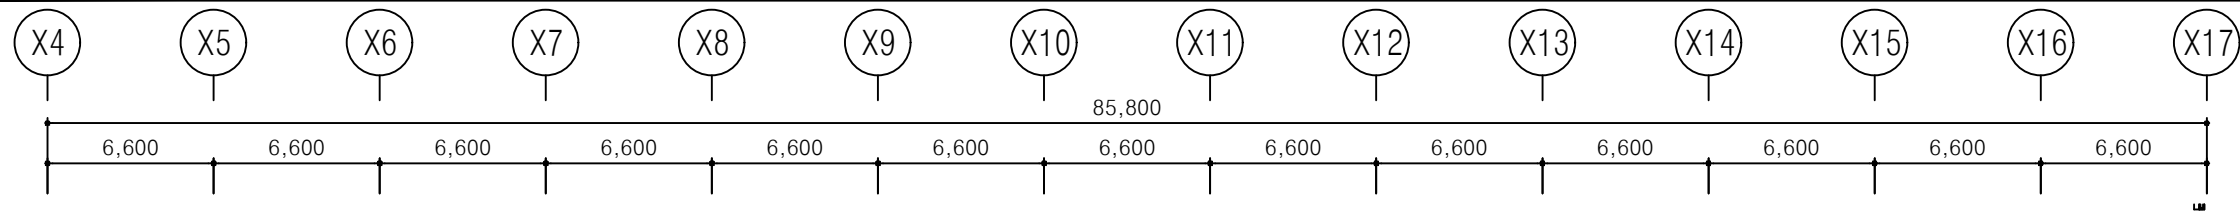


조명 제어구역

로봇공학부 6층 전등설비 평면도
축척 A1: 1/150, A3: 1/300

1. 실험실내의 전등설비용 공배관 설치.
: EMPTY PIPE (CD 22C)

3					
2					
1	14.11.18	실명/호실 수정			
REV	DATE	DESCRIPTION	DRN	CHK	APR
DRAWING TITLE					
로봇공학부 6층 전등설비 평면도					
APPROVED					
CHECKED1					
CHECKED2					
DRAWN					
PROJECT NO.					
SCALE					
A1	1/150	A3	1/300	APPROVAL DATE	
				2014.04	
DRAWING NO.				REV.	
E-14-0708					

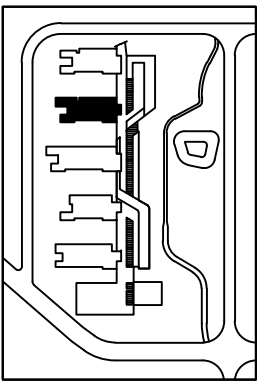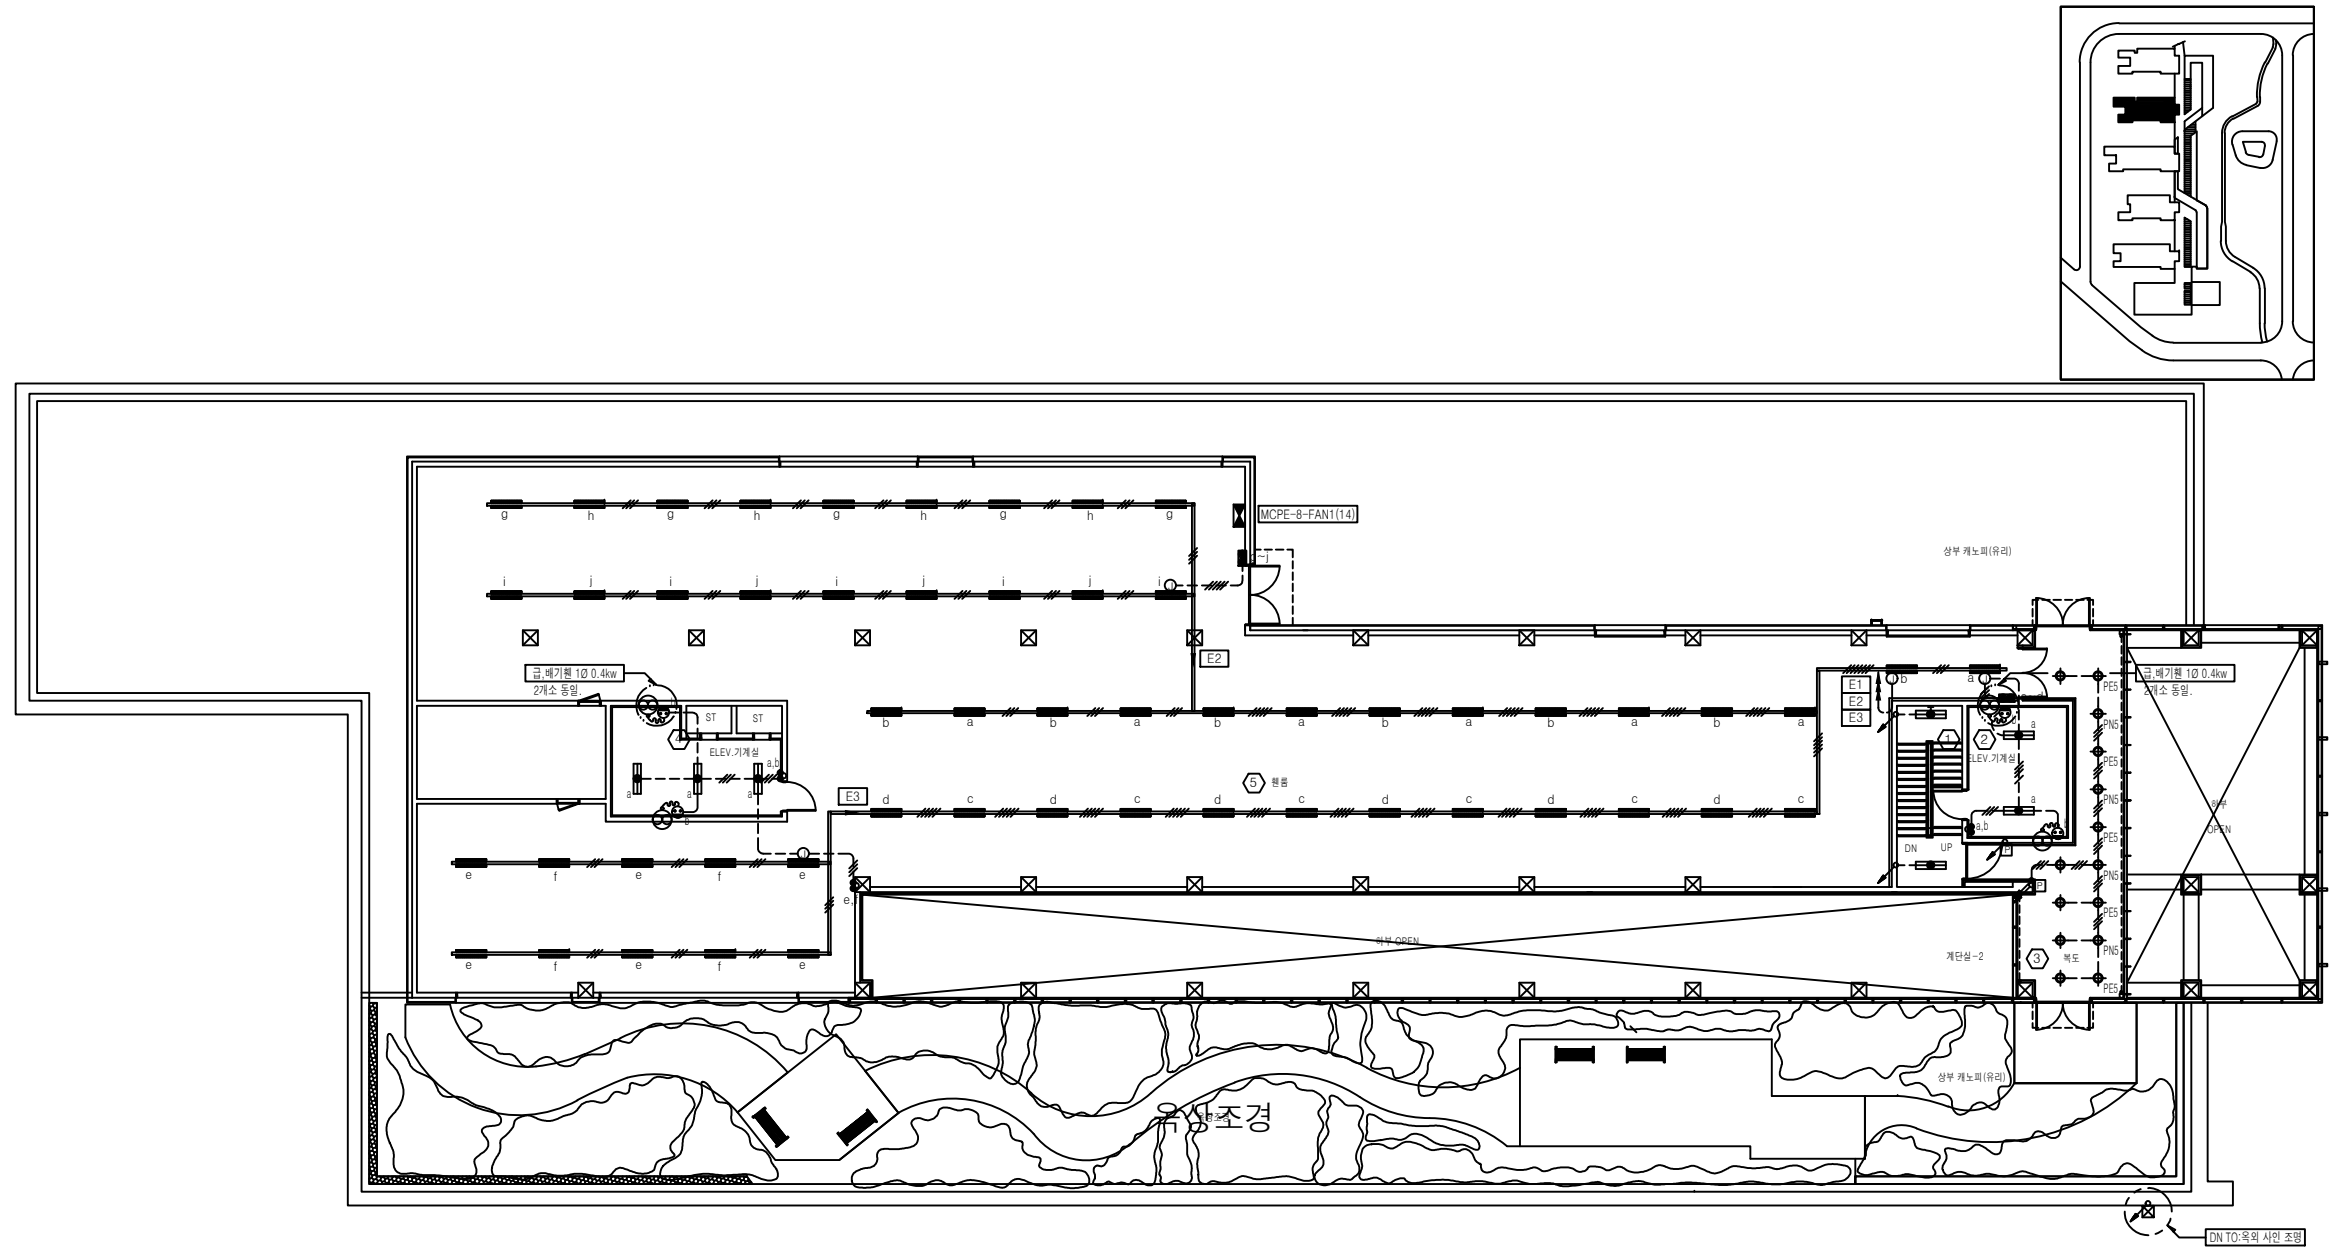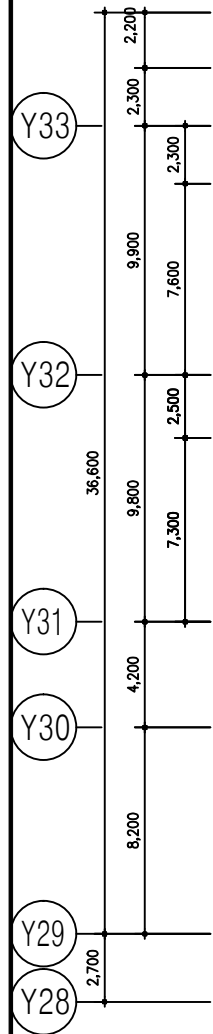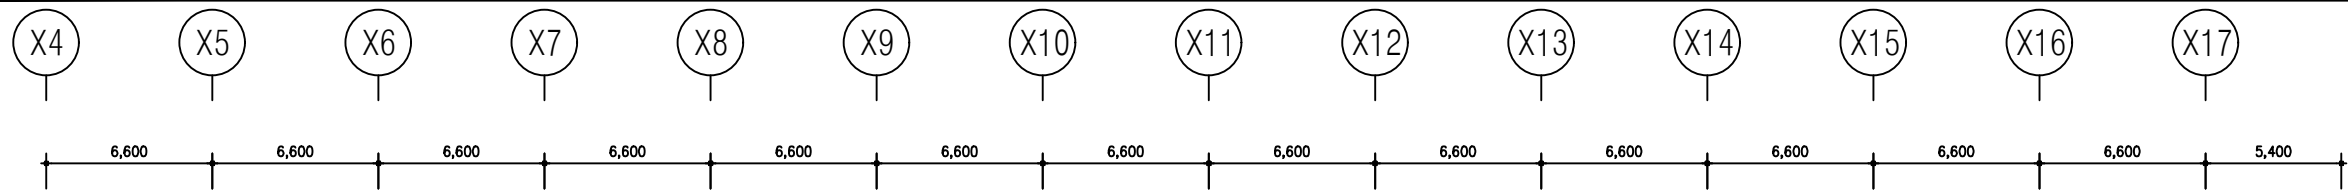

3					
2					
1	14.11.18	실명/호실 수정			
REV	DATE	DESCRIPTION	DRN	CHK	APR

DRAWING TITLE

로봇공학부
7층 전등설비 평면도

APPROVED

CHECKED1

CHECKED2

DRAWN

PROJECT NO.

SCALE	A3	APPROVAL DATE
1/150	1/300	2014.04

DRAWING NO.	REV.
E-14-0709	

로봇공학부 7층 전등설비 평면도
축척 A1: 1/150, A3: 1/300