
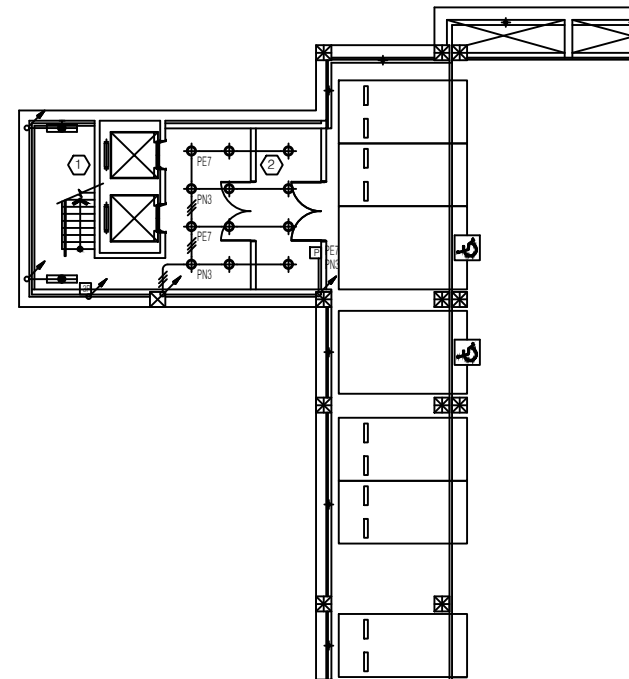
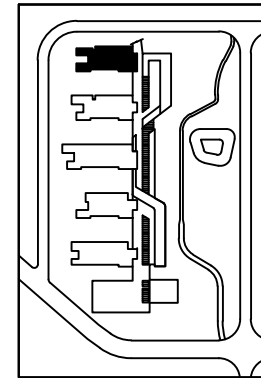
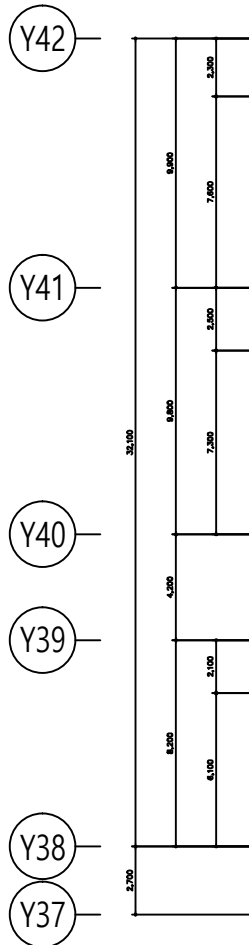


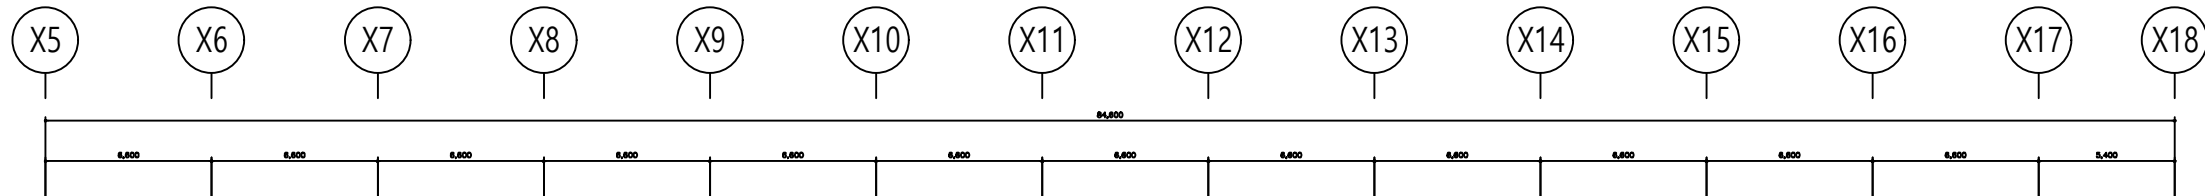

에너지시스템공학부 지하2층 전등설비 평면도
축척 A1: 1/150, A3: 1/300

3					
2					
1	14.11.18	실명/호실 수정			
REV	DATE	DESCRIPTION	DRN	CHK	APR

DRAWING TITLE

에너지시스템공학부
지하2층 전등설비 평면도

APPROVED

CHECKED1




CHECKED2

DRAWN

PROJECT NO.


SCALE	A3	APPROVAL DATE
1/150	1/300	2014.04

DRAWING NO.	REV.
E-15-0701	

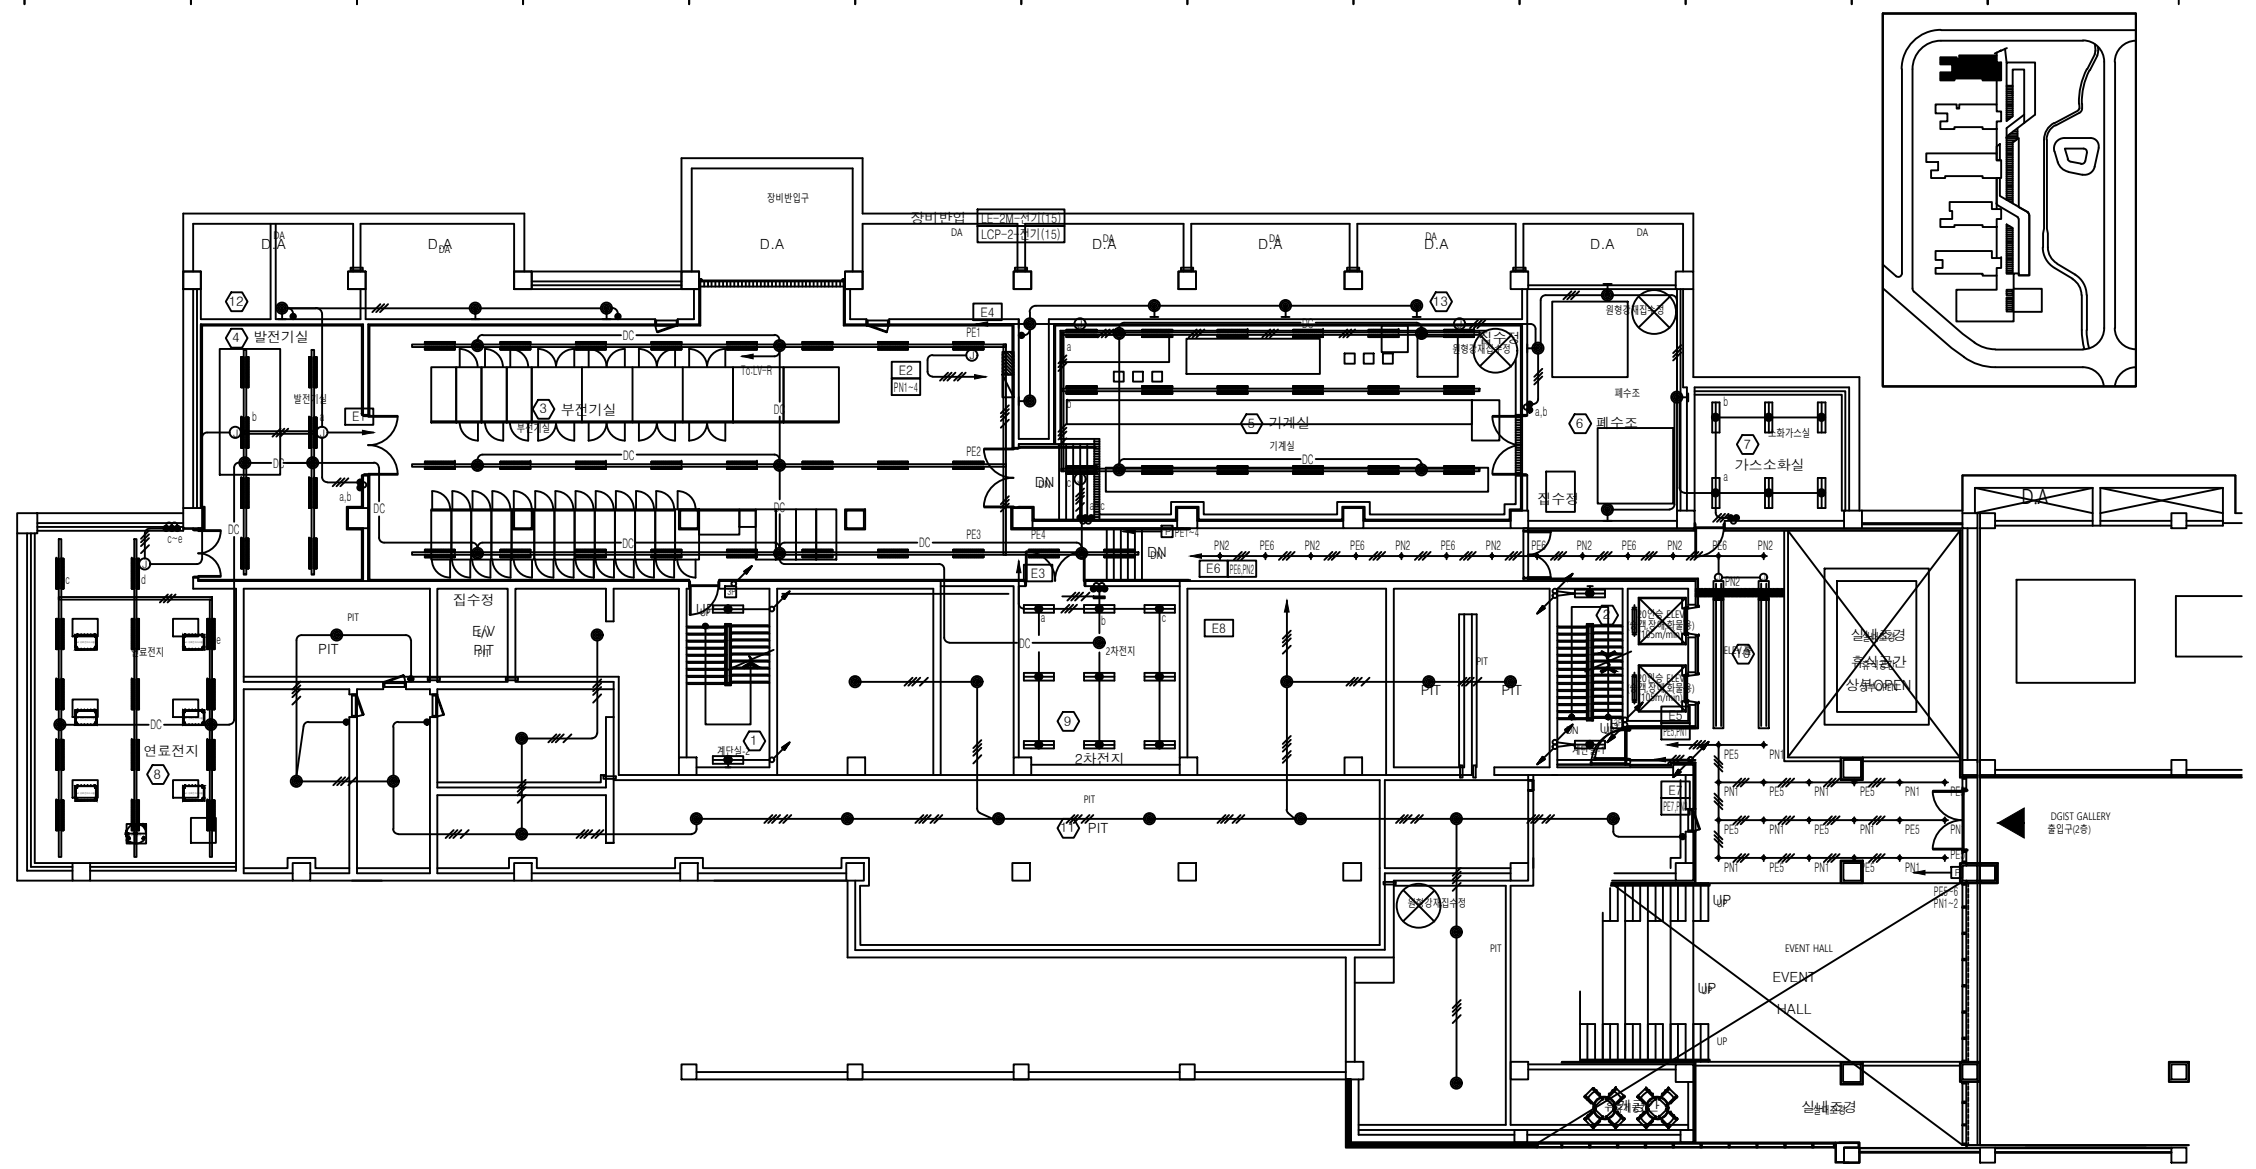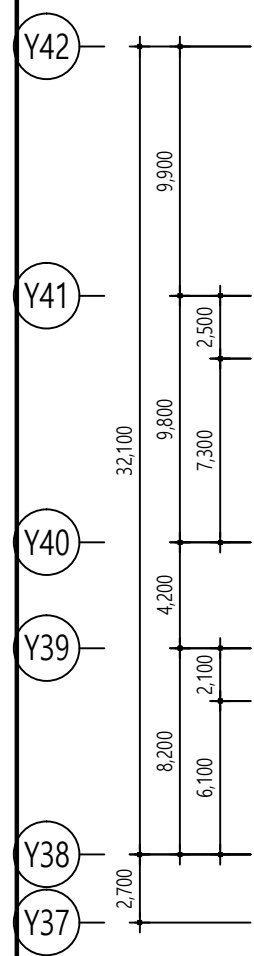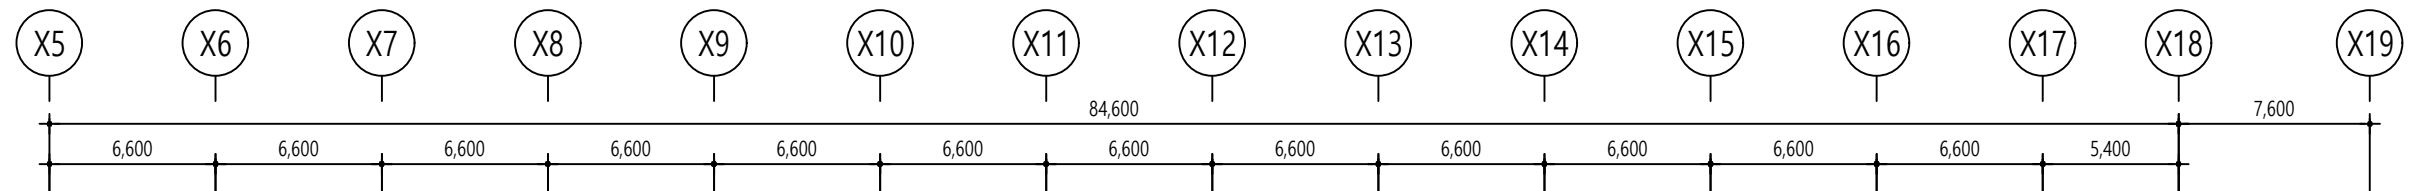

에너지시스템공학부 지하1층 전등설비 평면도
축척 A1: 1/150, A3: 1/300

3					
2					
1	14.11.18	설명/호실 수정			
REV	DATE	DESCRIPTION	DRN	CHK	APR
DRAWING TITLE					
에너지시스템공학부 지하1층 전등설비 평면도					
APPROVED					
CHECKED1					
CHECKED2					
DRAWN					
PROJECT NO.					
SCALE			APPROVAL DATE		
A1	1/150	A3	1/300	2014.04	
DRAWING NO.				REV.	
E-15-0702					

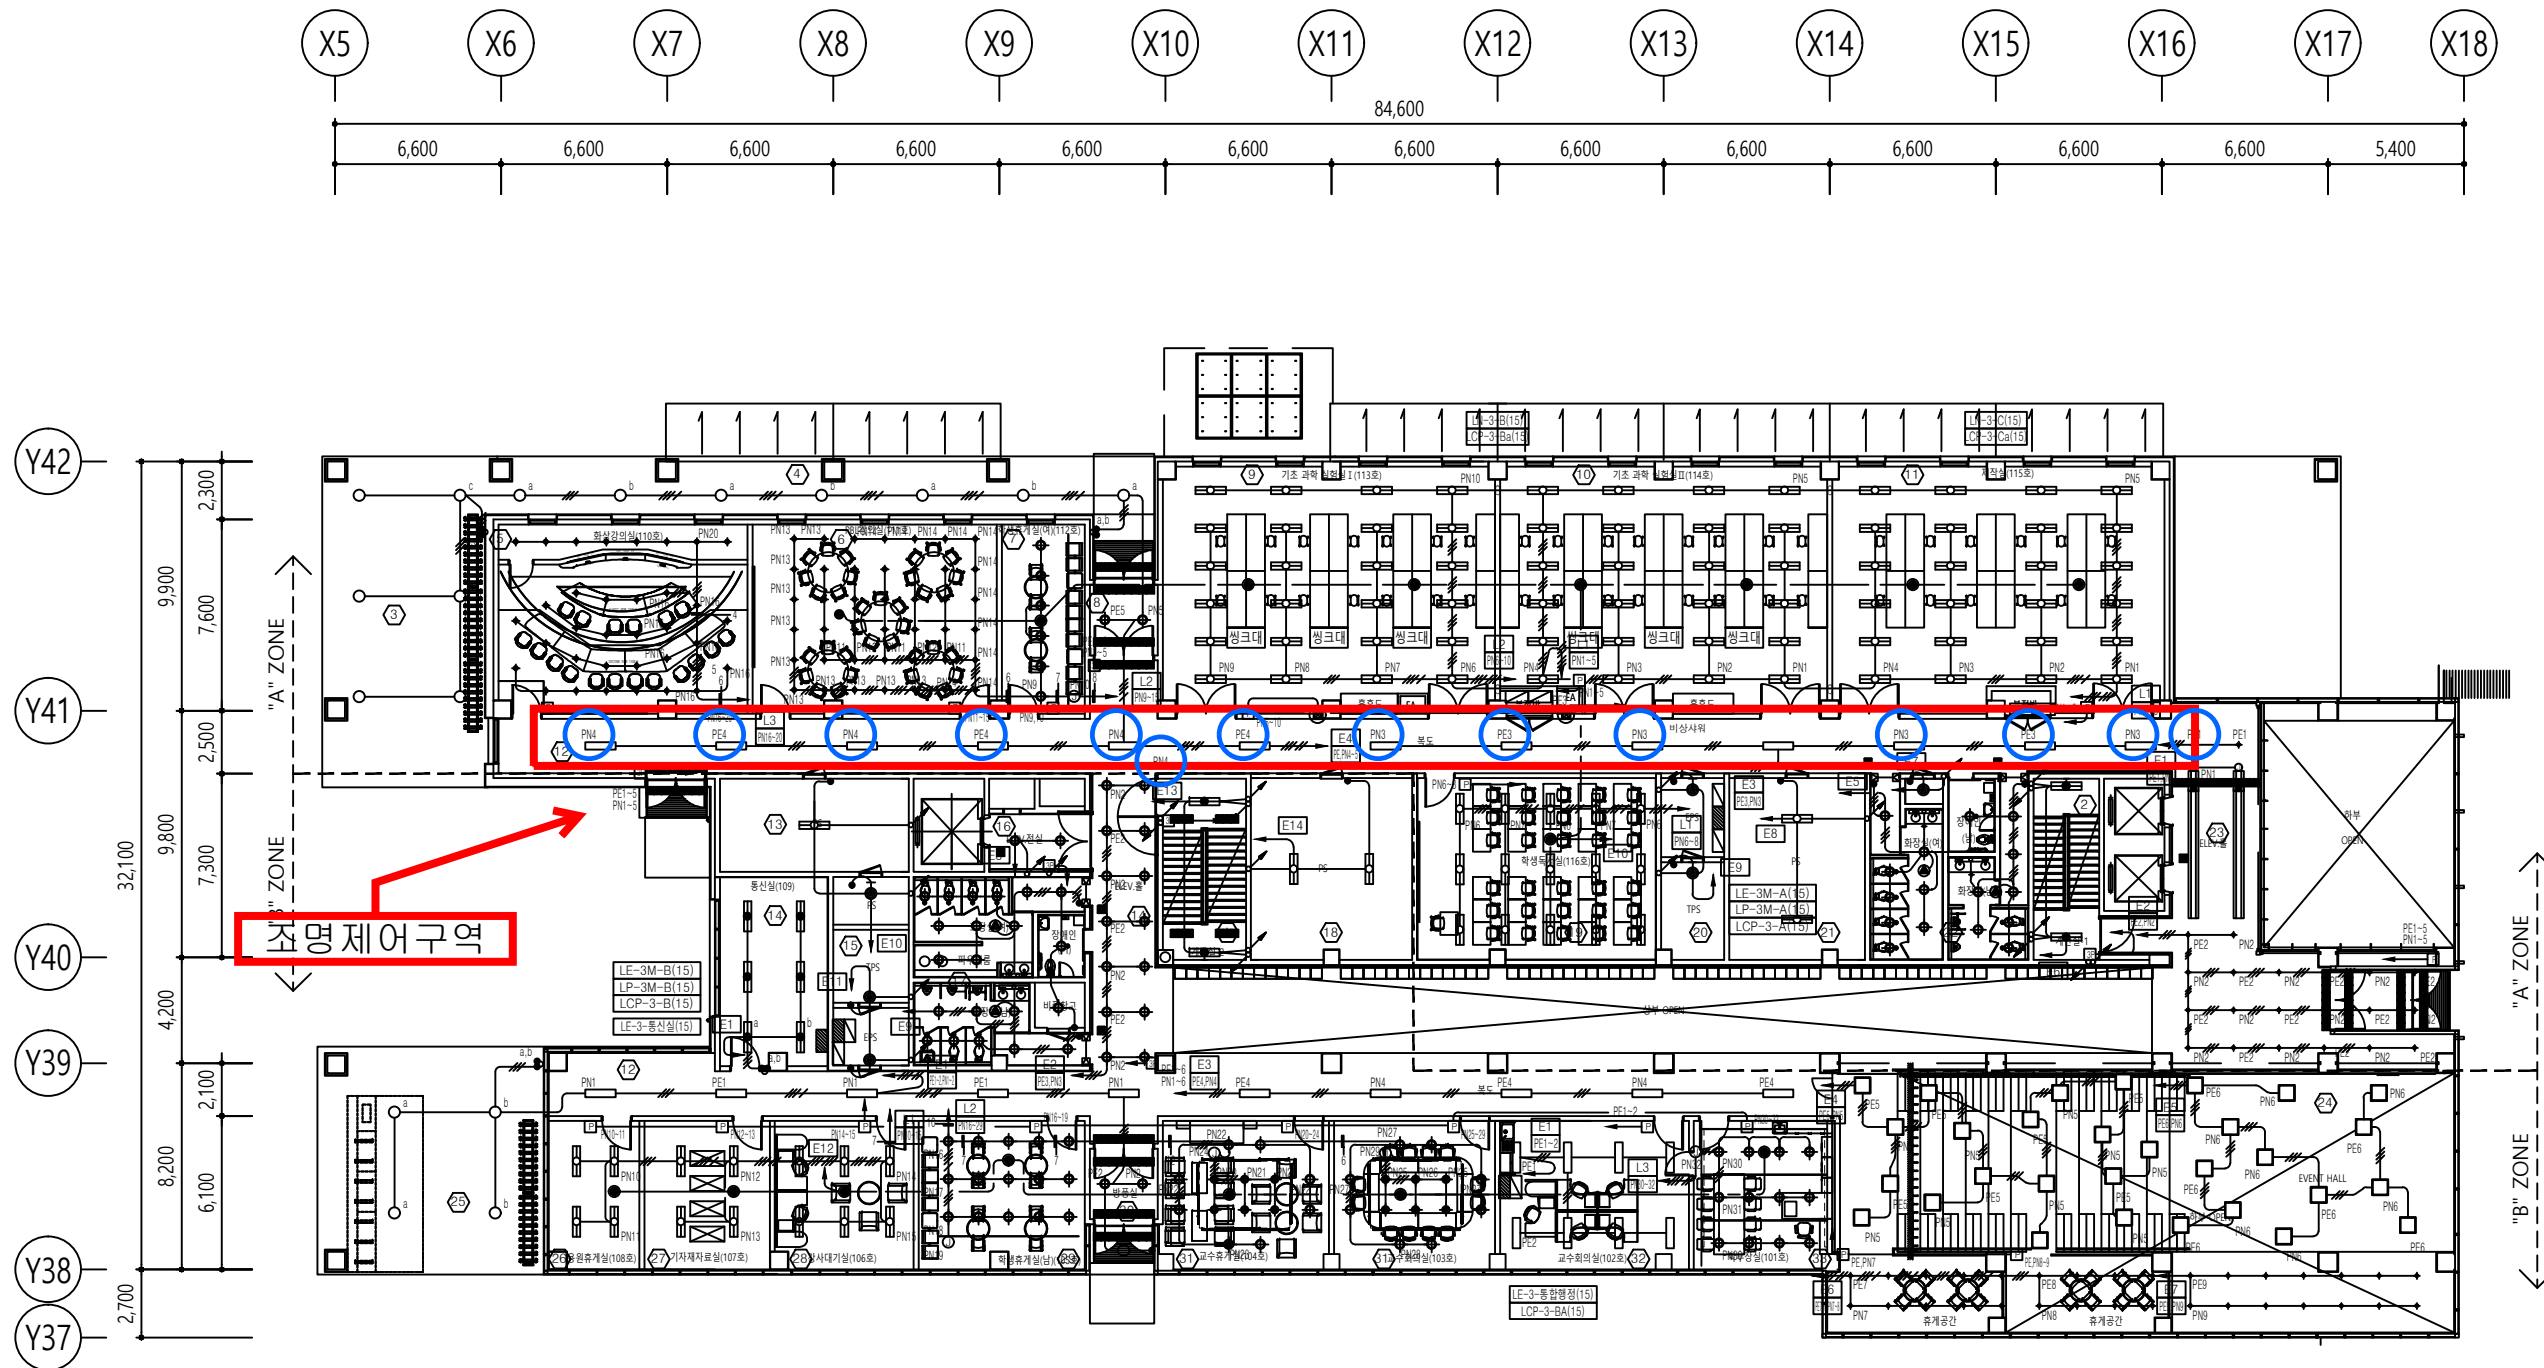

에너지시스템공학부 1층 전등설비 평면도
축척 A1: 1/150, A3: 1/300

3					
2					
1	14.11.18	실명/호실 수정			
REV	DATE	DESCRIPTION	DRN	CHK	APR

DRAWING TITLE
에너지시스템공학부
1층 전등설비 평면도

APPROVED

CHECKED1



CHECKED2

DRAWN

PROJECT NO.


SCALE	APPROVAL DATE
A1 1/150 A3 1/300	2014.04

DRAWING NO. E-15-0703 REV.

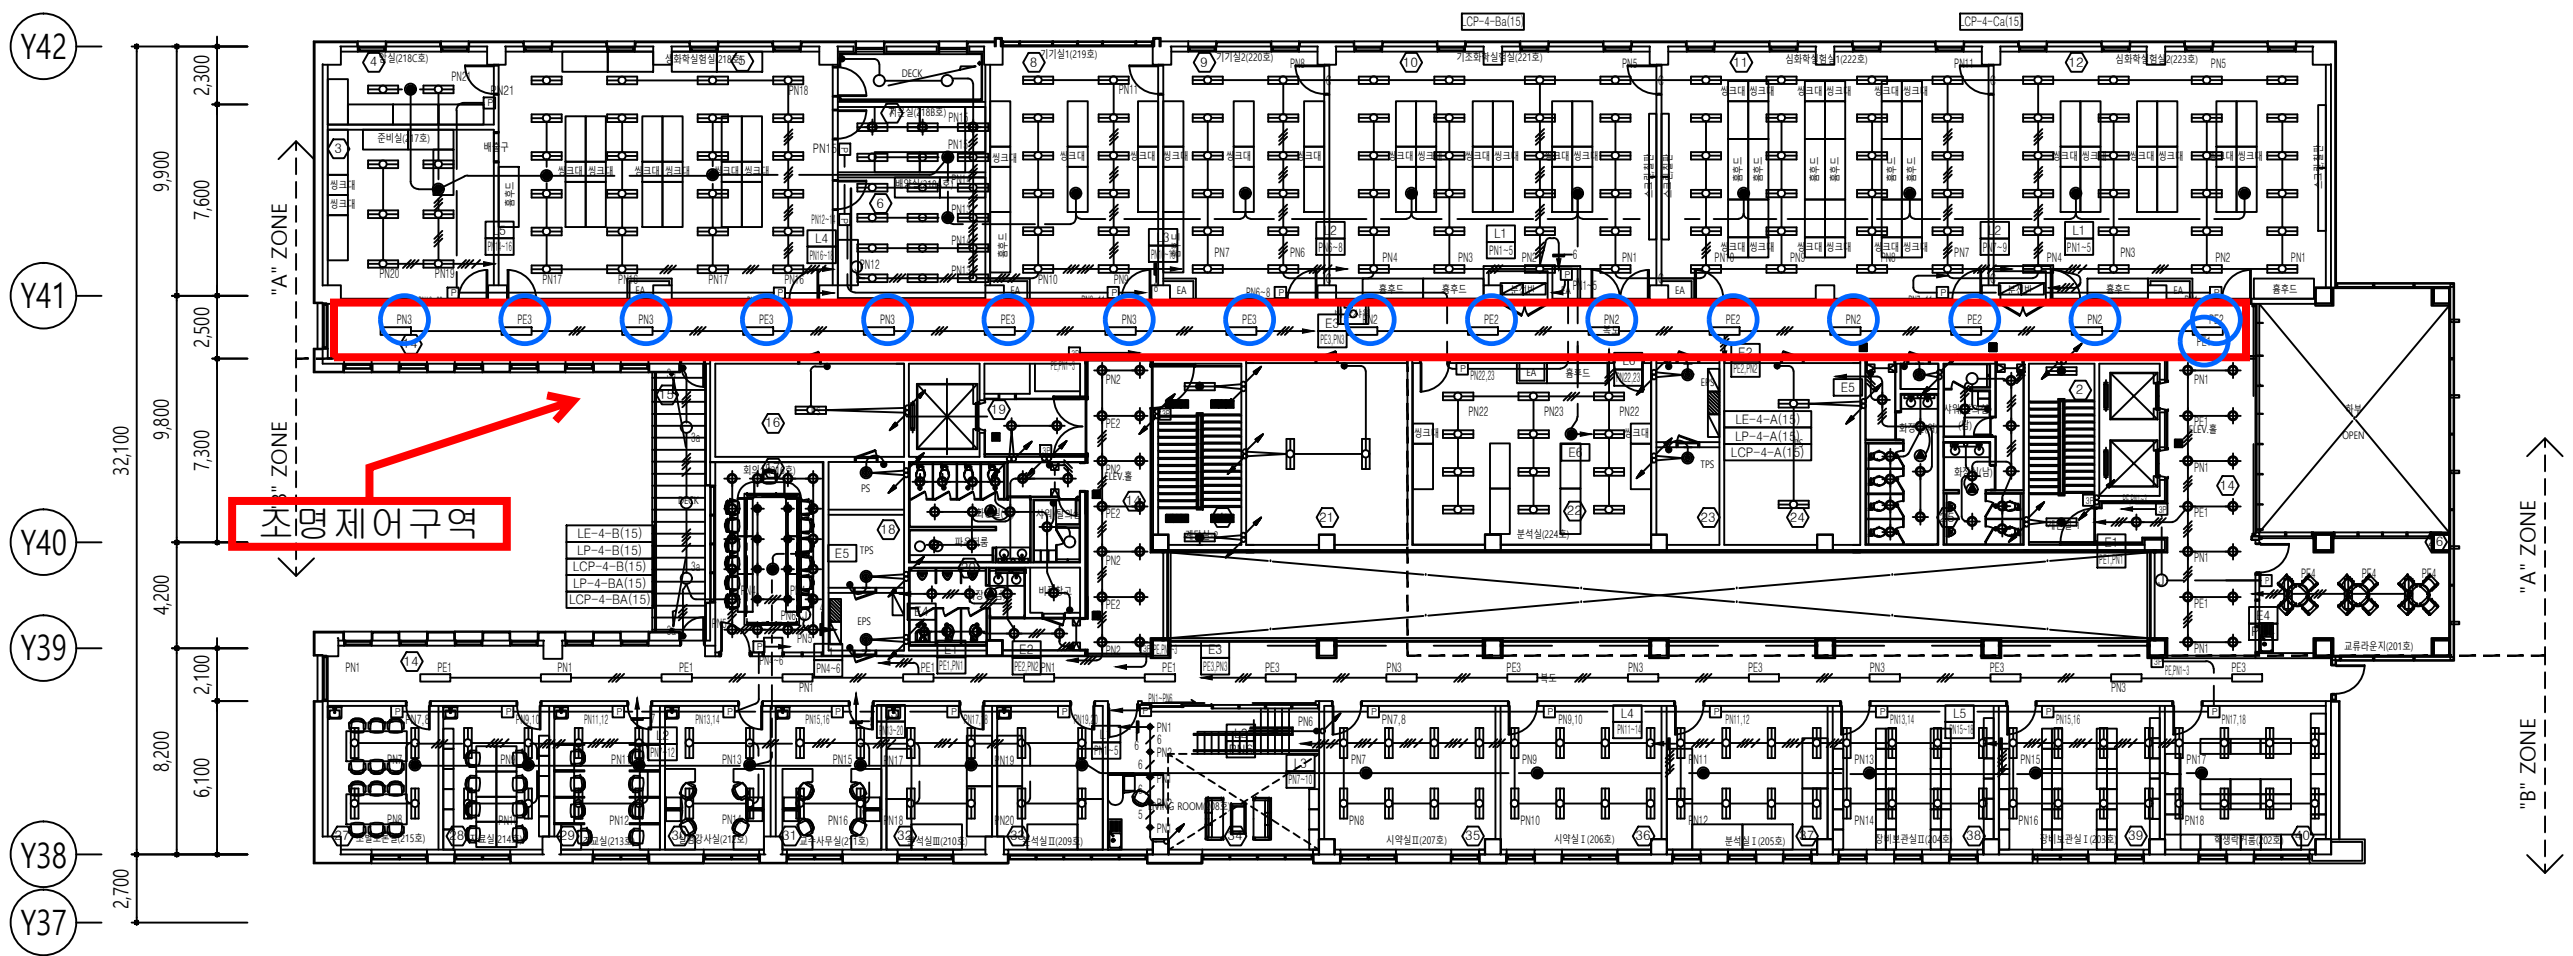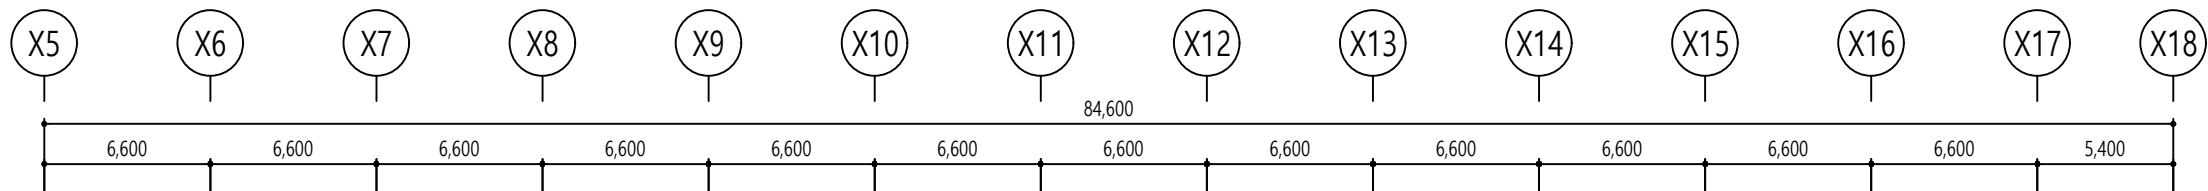



에너지시스템공학부 2층 전등설비 평면도
축척 A1: 1/150, A3: 1/300

3					
2					
1	14.11.18	실명/호실 수정			
REV	DATE	DESCRIPTION	DRN	CHK	APR
DRAWING TITLE					
에너지시스템공학부 2층 전등설비 평면도					
APPROVED					
CHECKED1					
CHECKED2					
DRAWN					
PROJECT NO.					
SCALE					
A1	1/150	A3	1/300	APPROVAL DATE	
				2014.04	
DRAWING NO.				REV.	
E-15-0704					

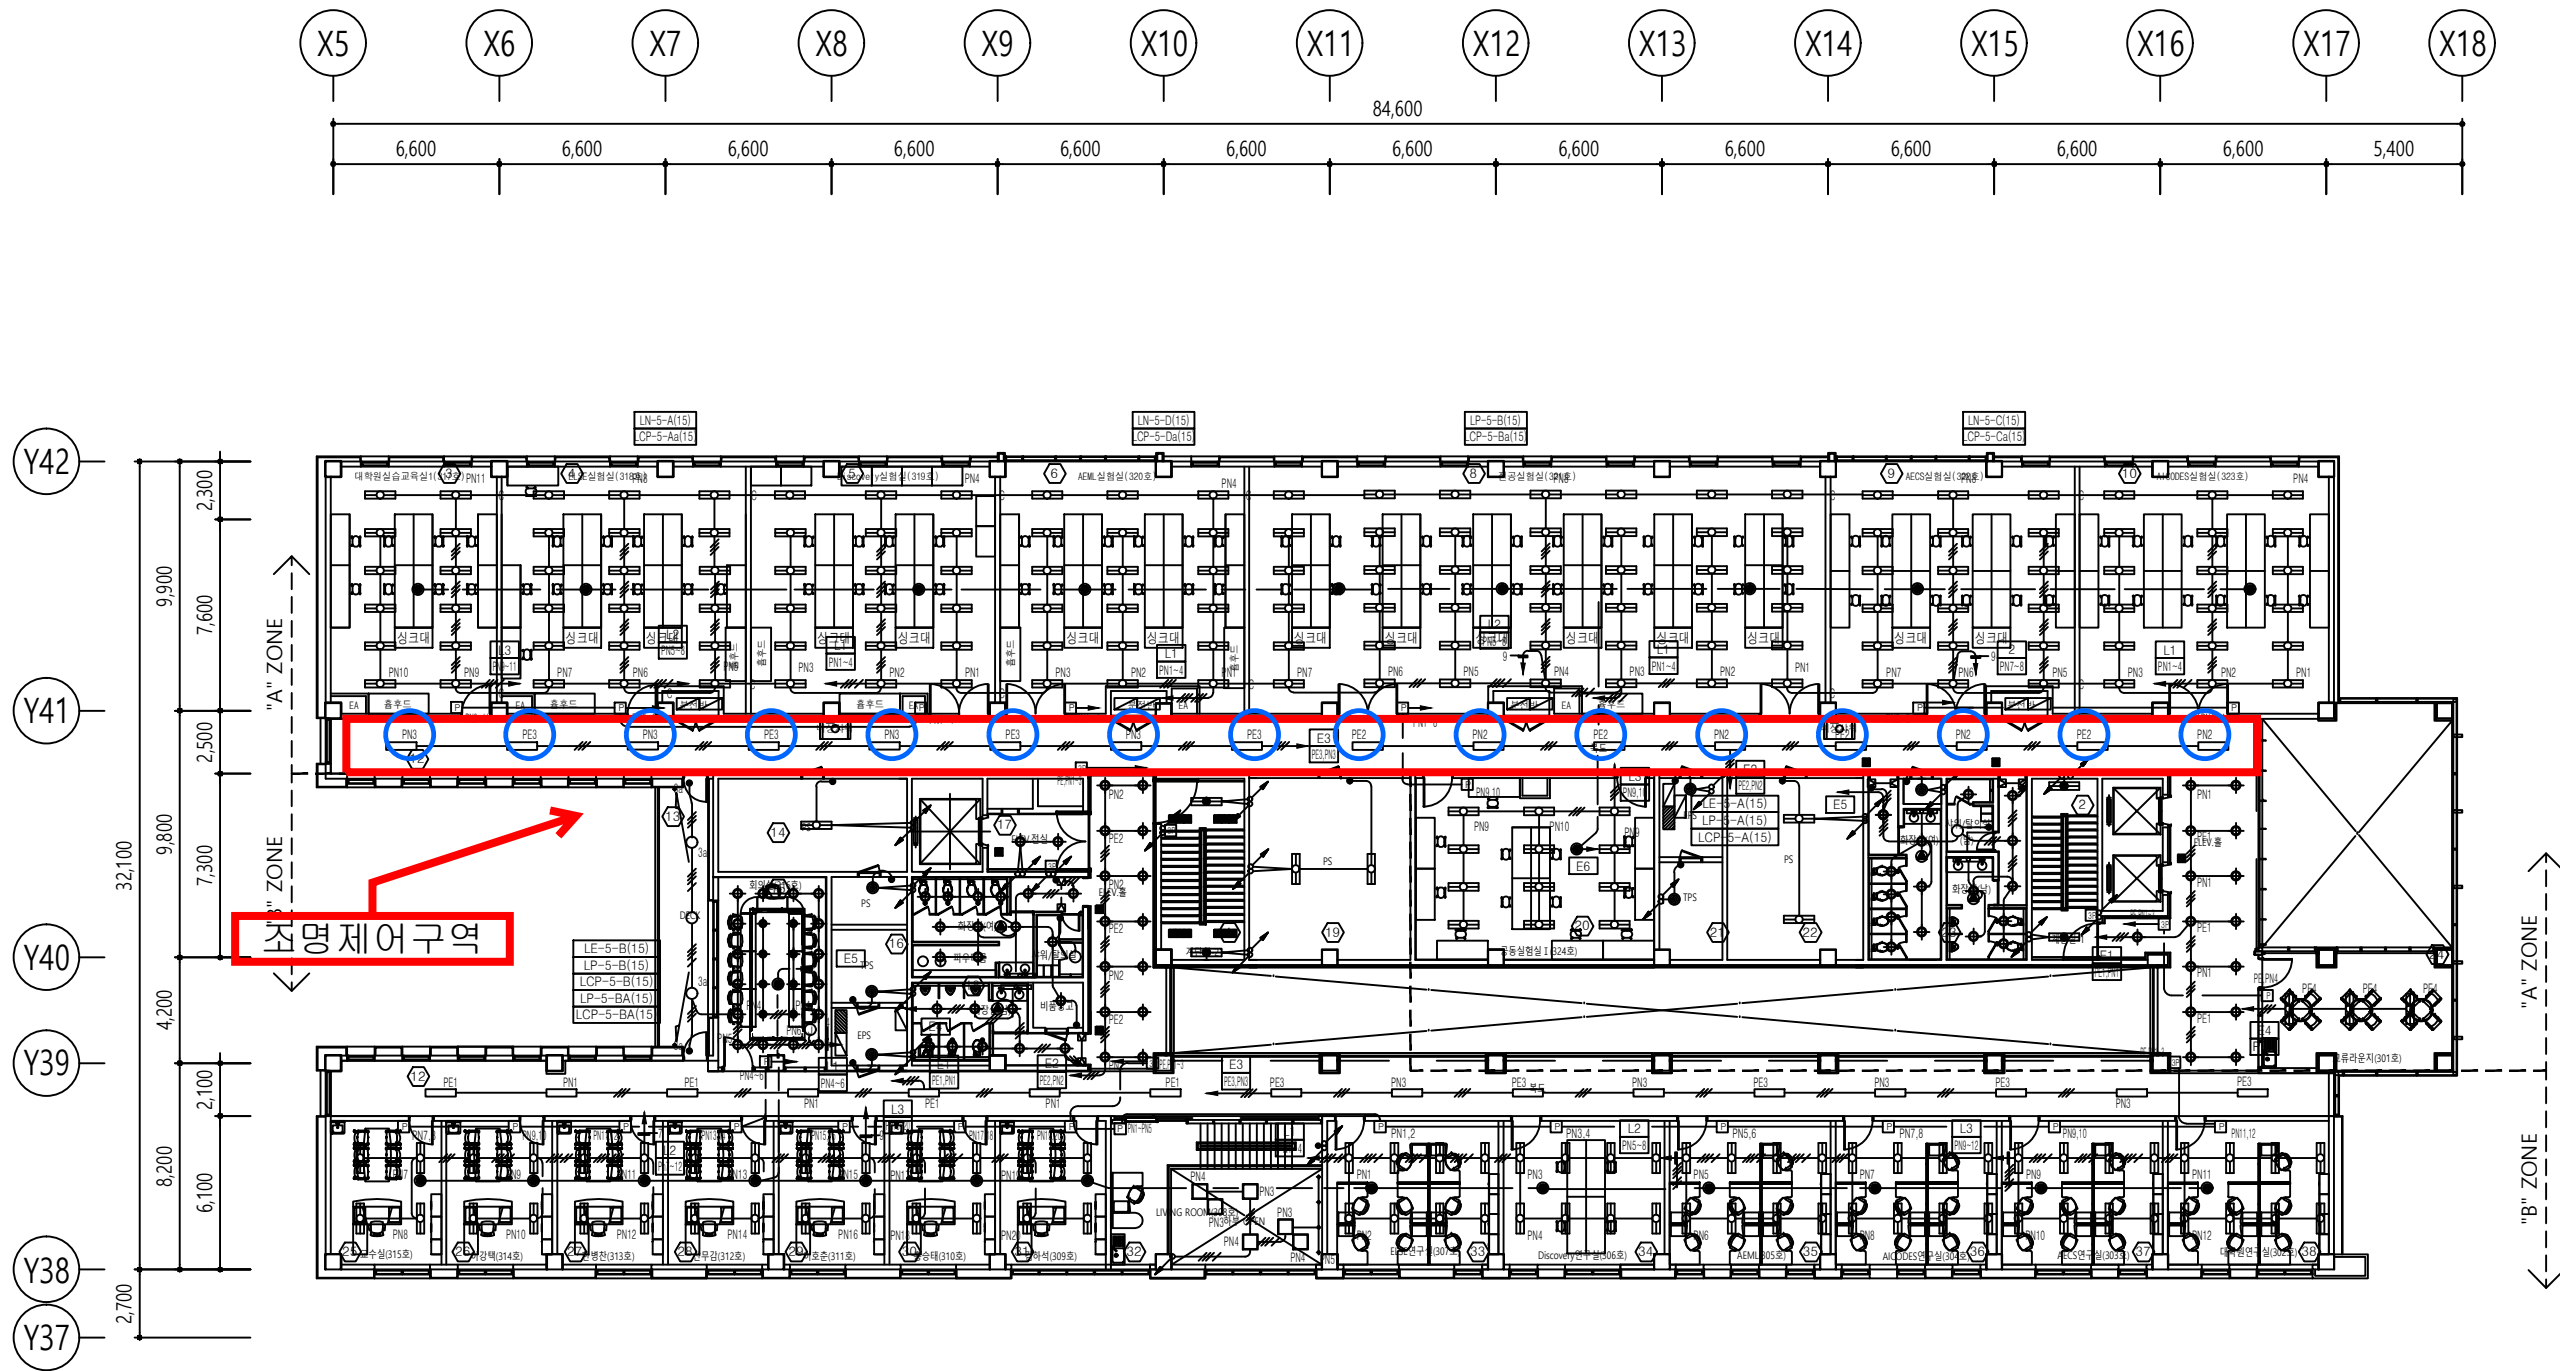



에너지시스템공학부 3층 전등설비 평면도
축척 A1: 1/150, A3: 1/300

3					
2					
1	14.11.18	실명/호실 수정			
REV	DATE	DESCRIPTION	DRN	CHK	APR
DRAWING TITLE					
에너지시스템공학부 3층 전등설비 평면도					
APPROVED					
CHECKED1					
CHECKED2					
DRAWN					
PROJECT NO.					
SCALE			APPROVAL DATE		
A1	A3		2014.04		
1/150	1/300				
DRAWING NO.					REV.
E-15-0705					

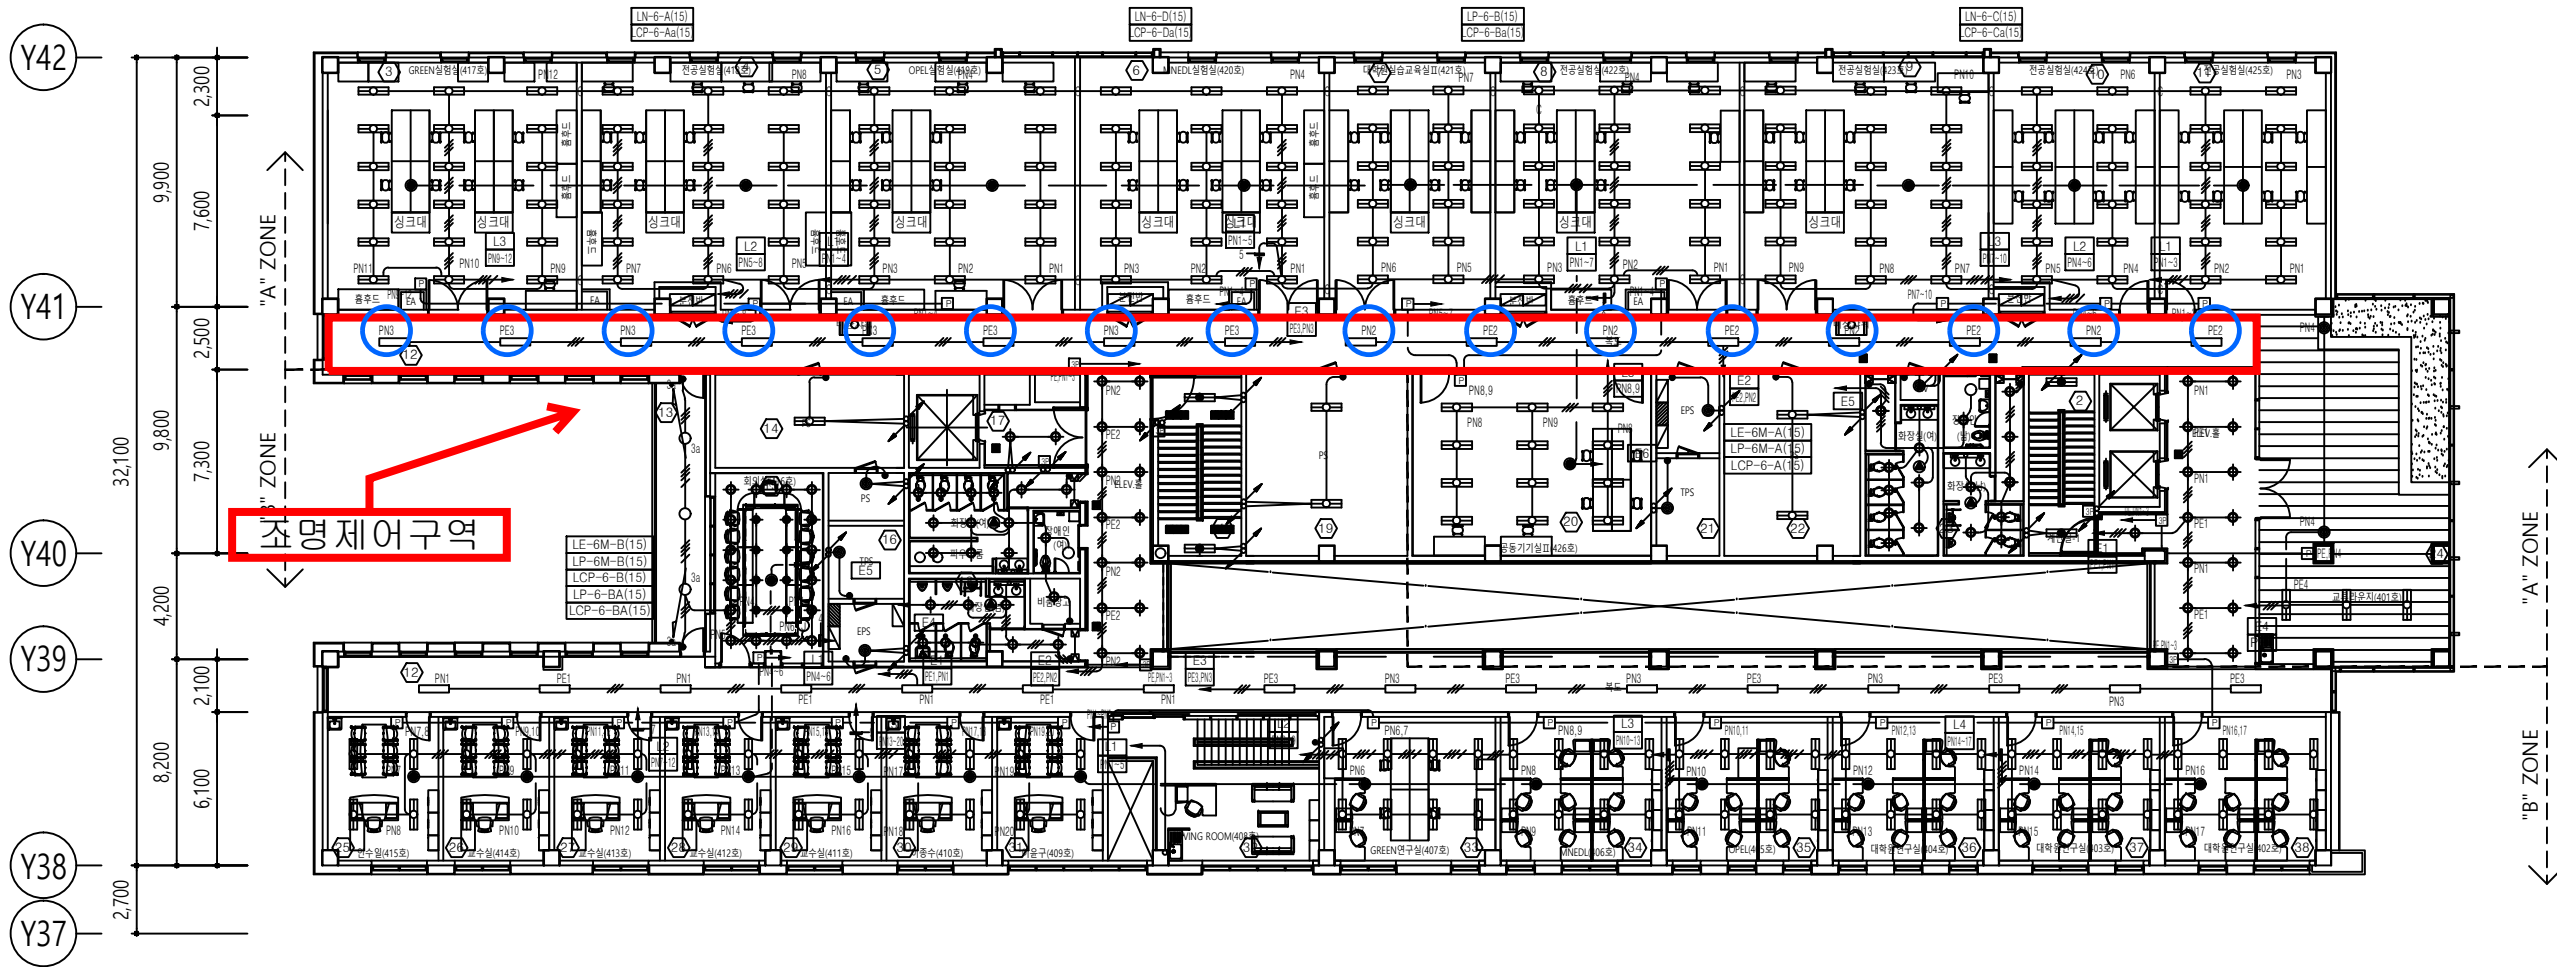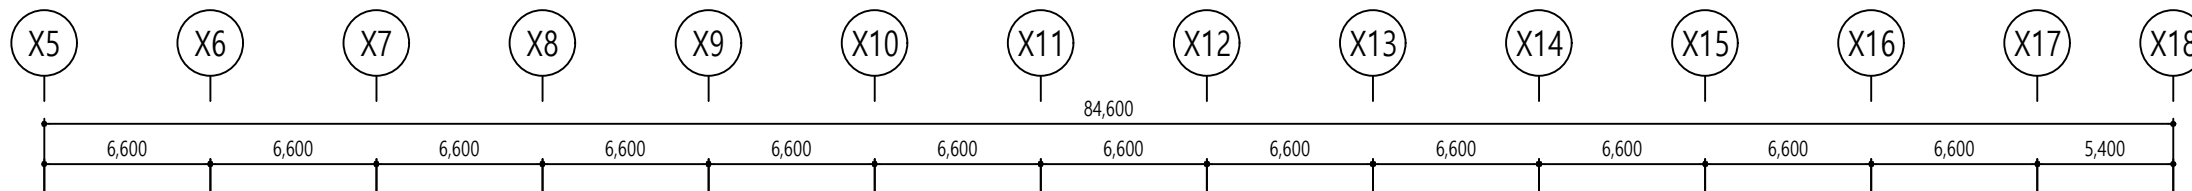


에너지시스템공학부 4층 전등설비 평면도
축척 A1: 1/150, A3: 1/300

3					
2					
1	14.11.18	설명/호설 수정			
REV	DATE	DESCRIPTION	DRN	CHK	APR
DRAWING TITLE					
에너지시스템공학부 4층 전등설비 평면도					
APPROVED					
CHECKED1					
CHECKED2					
DRAWN					
PROJECT NO.					
SCALE			APPROVAL DATE		
A1	1/150	A3	1/300	2014.04	
DRAWING NO.					REV.
E-15-0706					

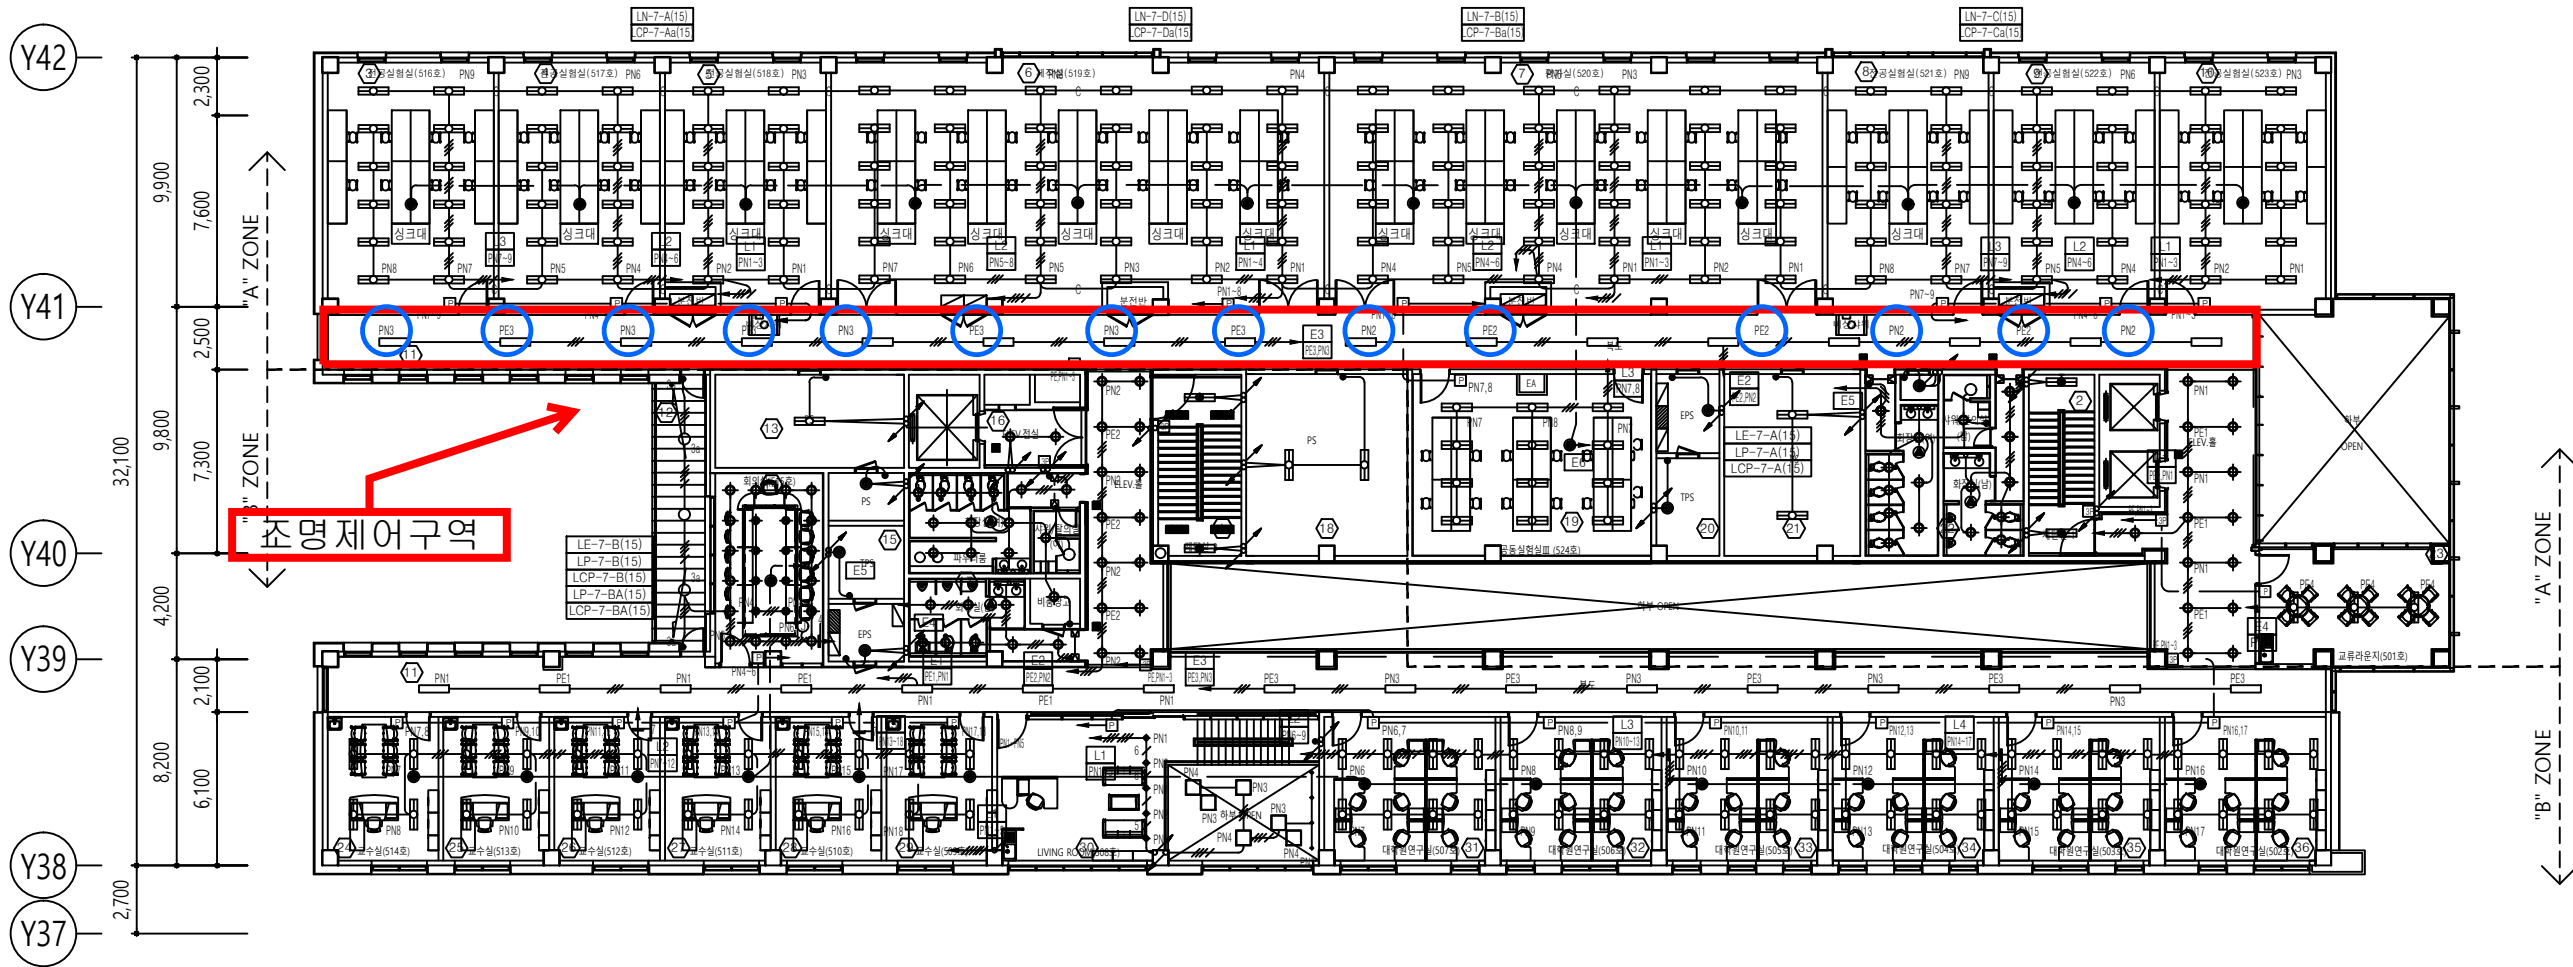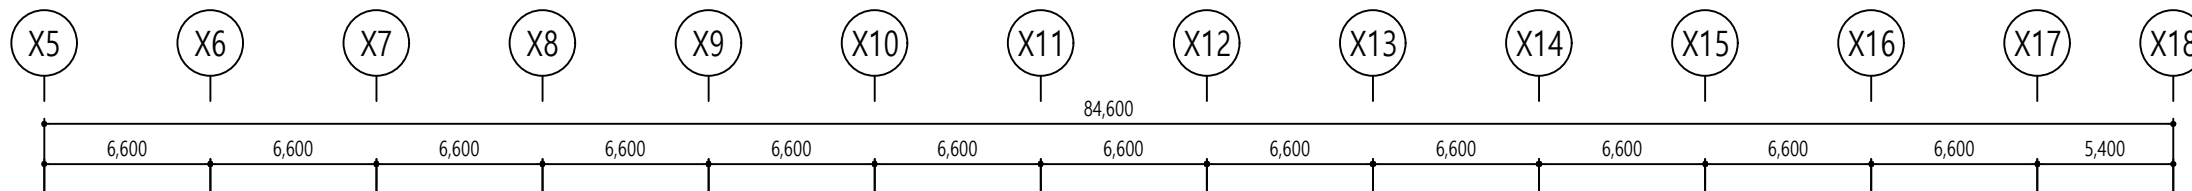

에너지시스템공학부 5층 전등설비 평면도
축척 A1: 1/150, A3: 1/300




3					
2					
1	14.11.18	실명/호실 수정			
REV	DATE	DESCRIPTION	DRN	CHK	APR
DRAWING TITLE					
에너지시스템공학부 5층 전등설비 평면도					
APPROVED					
CHECKED1					
CHECKED2					
DRAWN					
PROJECT NO.					
SCALE			APPROVAL DATE		
A1	A3		2014.04		
1/150	1/300				
DRAWING NO.					REV.
E-15-0707					

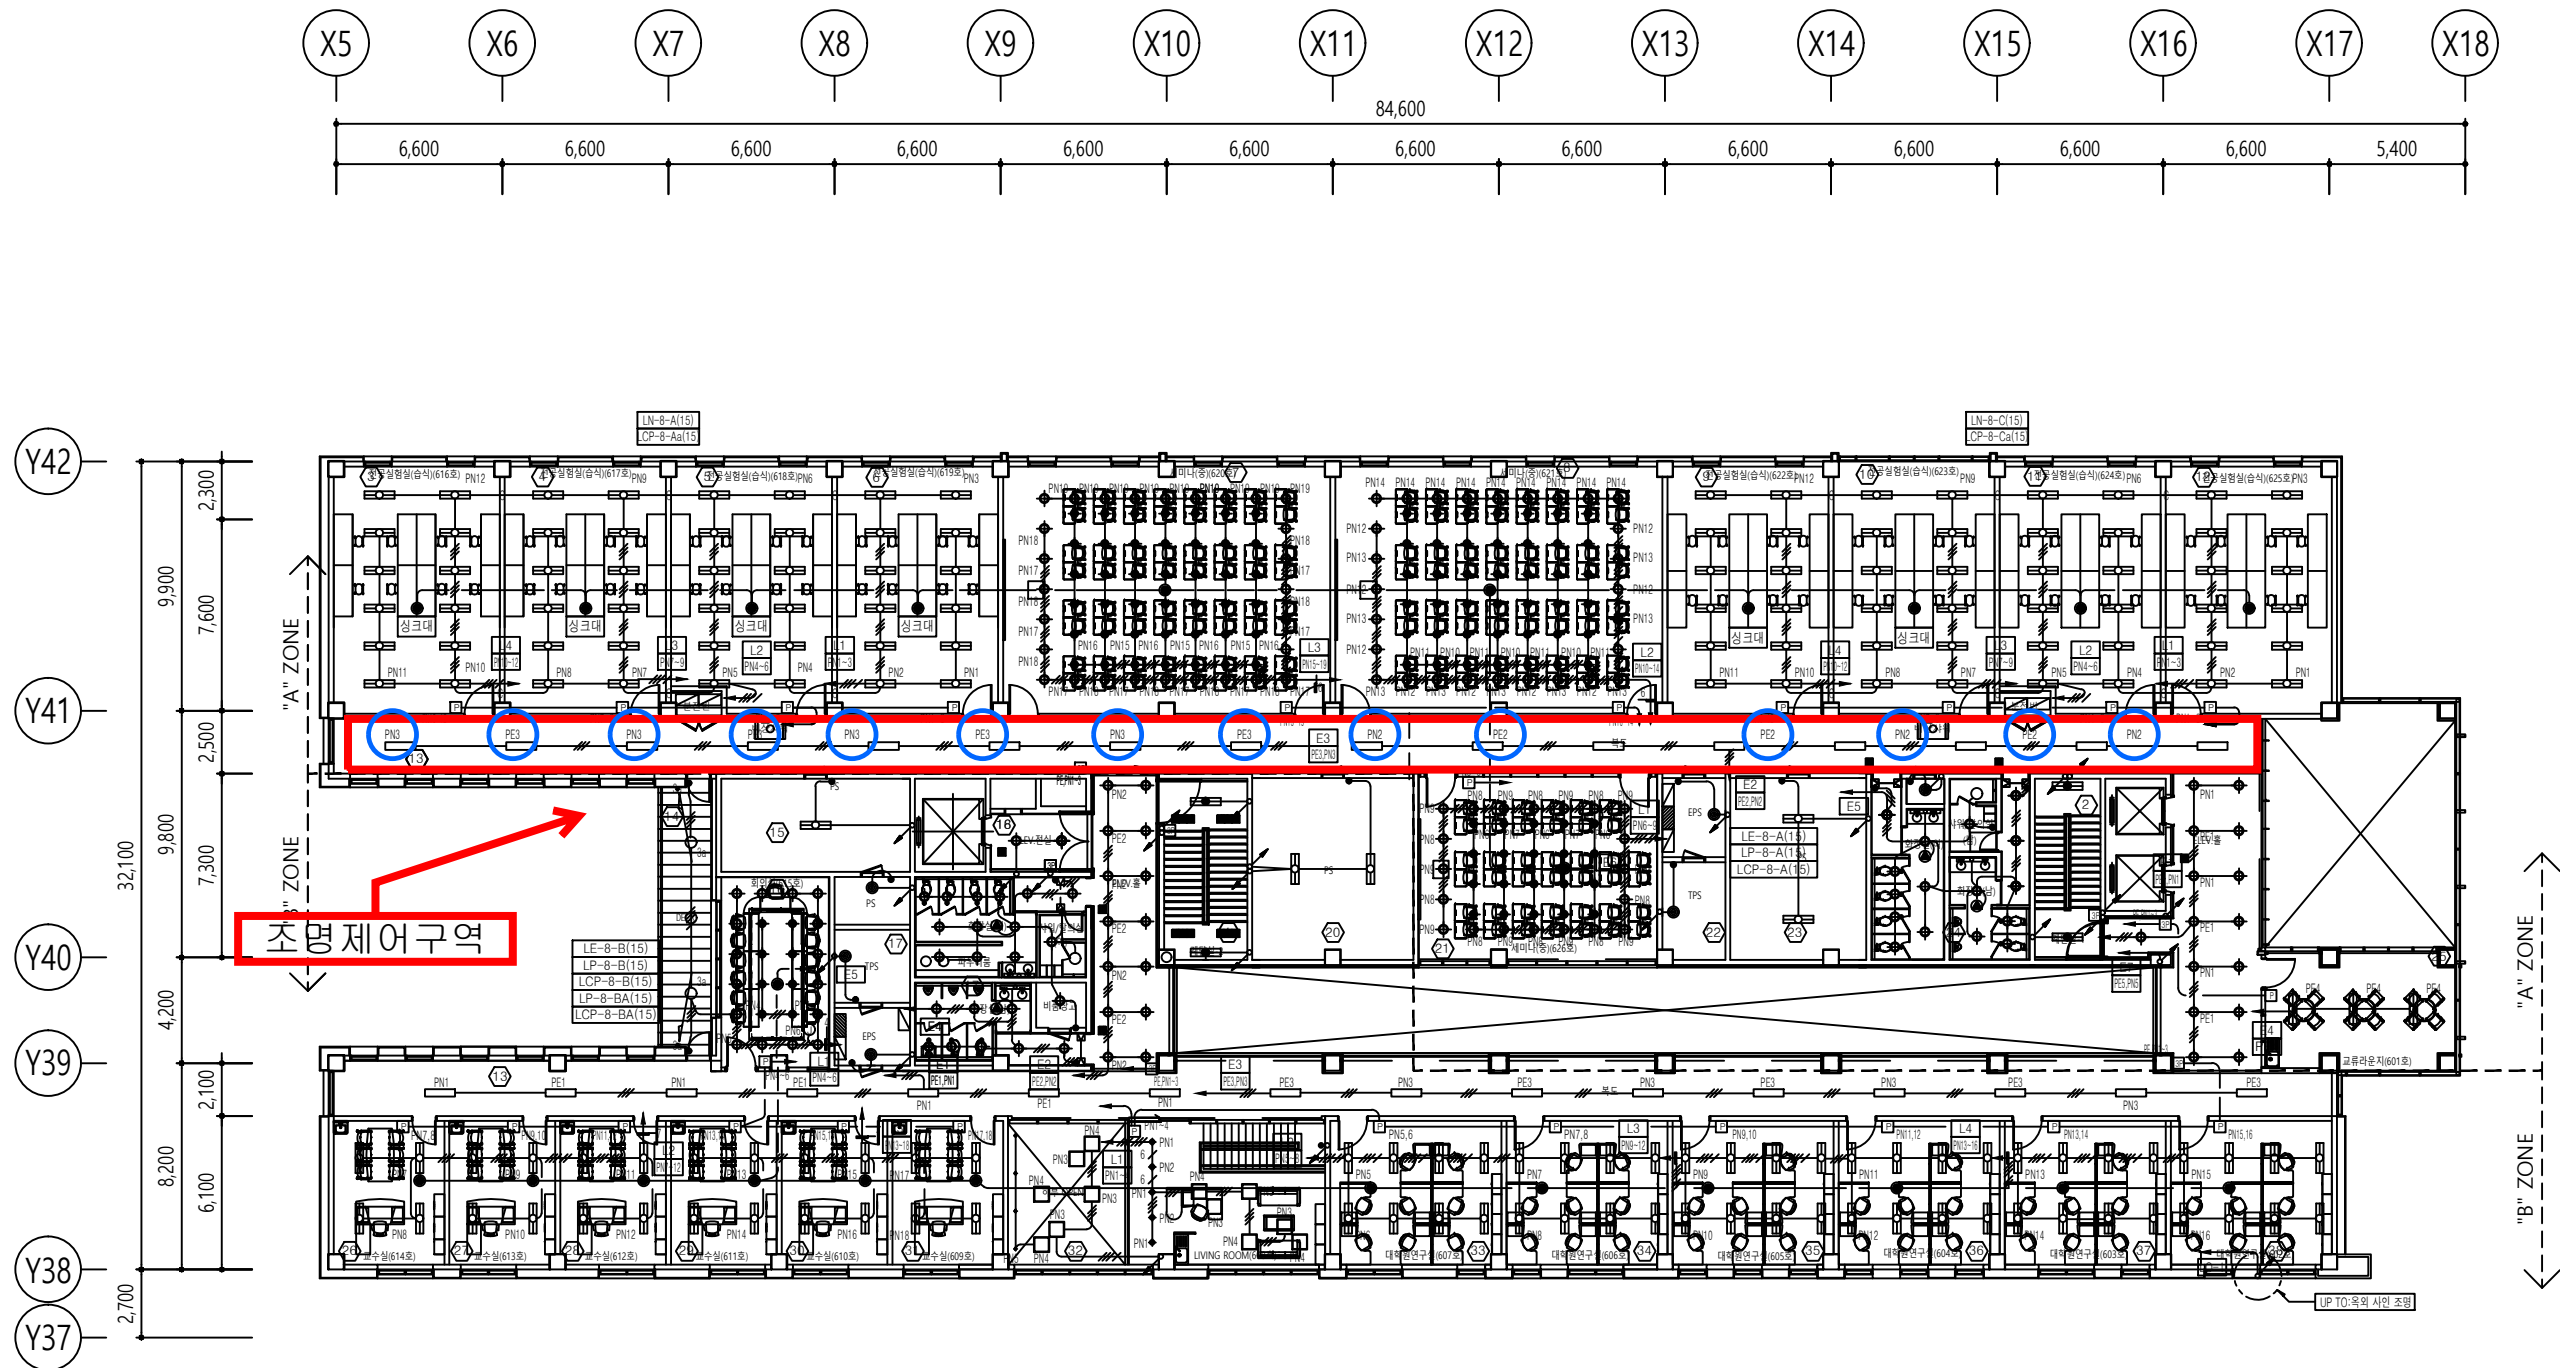

에너지시스템공학부 6층 전등설비 평면도
축척 A1: 1/150, A3: 1/300

1. 시험실내의 전등설비용 공배관 설치.
← : EMPTY PIPE (CD 22C)

3					
2					
1	14.11.18	실명/호실 수정			
REV	DATE	DESCRIPTION	DRN	CHK	APR
DRAWING TITLE					
에너지시스템공학부 6층 전등설비 평면도					
APPROVED					
CHECKED1					
CHECKED2					
DRAWN					
PROJECT NO.					
SCALE					
A1	A3	APPROVAL DATE			
1/150	1/300	2014.04			
DRAWING NO.					REV.
E-15-0708					

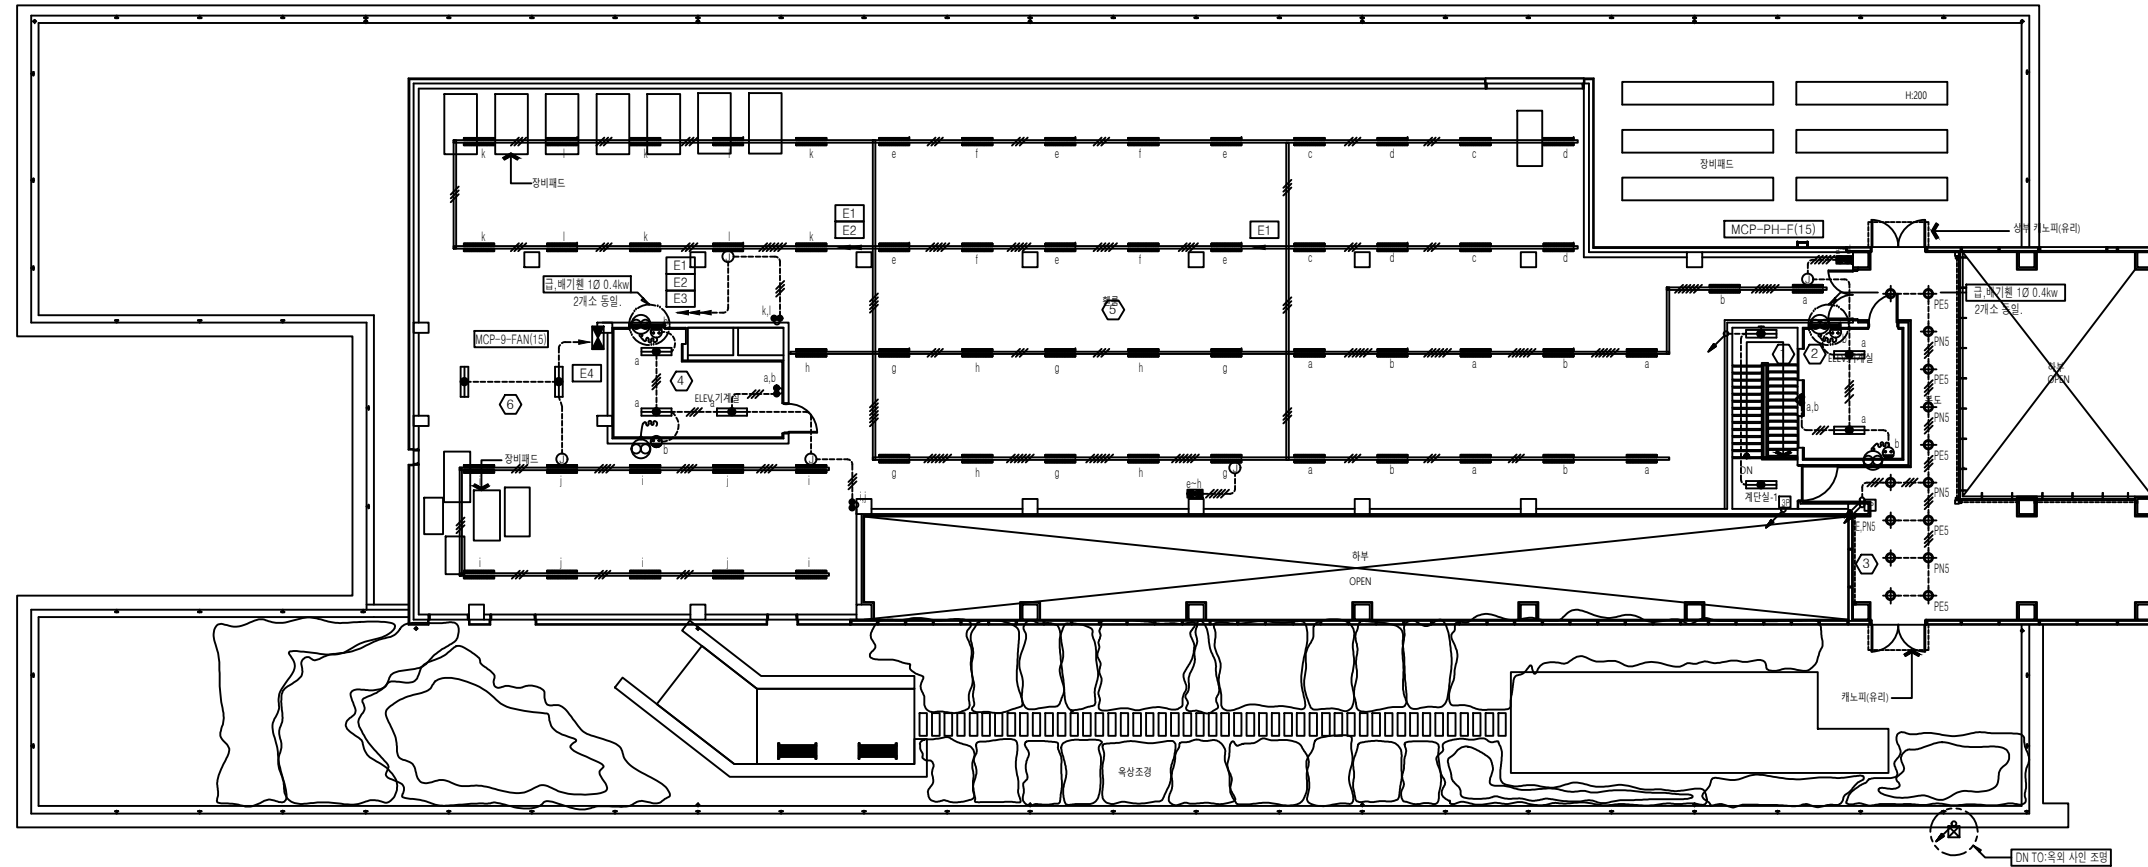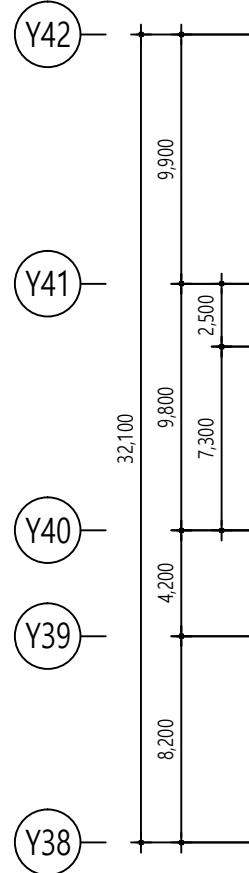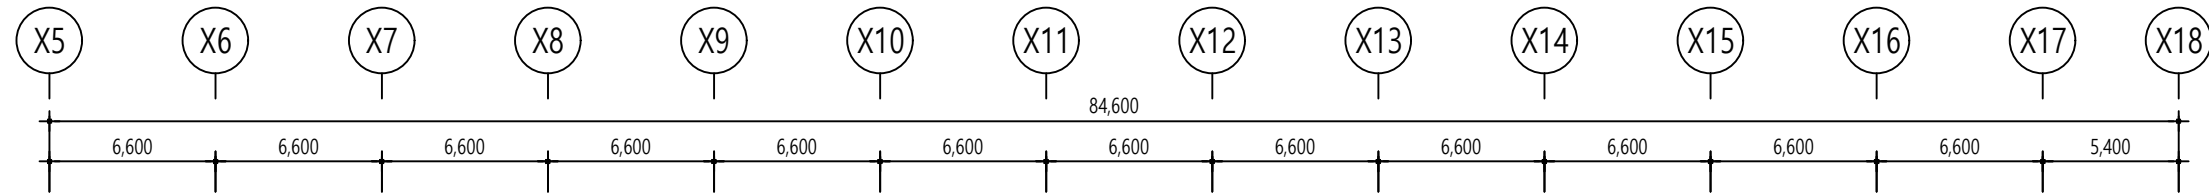

에너지시스템공학부 7층 전등설비 평면도
축척 A1: 1/150, A3: 1/300

3					
2					
1	14.11.18	실명/호실 수정			
REV	DATE	DESCRIPTION	DRN	CHK	APR

DRAWING TITLE
에너지시스템공학부
7층 전등설비 평면도

APPROVED

CHECKED1

CHECKED2

DRAWN

PROJECT NO.

SCALE	APPROVAL DATE
A1 1/150 A3 1/300	2014.04

DRAWING NO.	REV.
E-15-0709	