


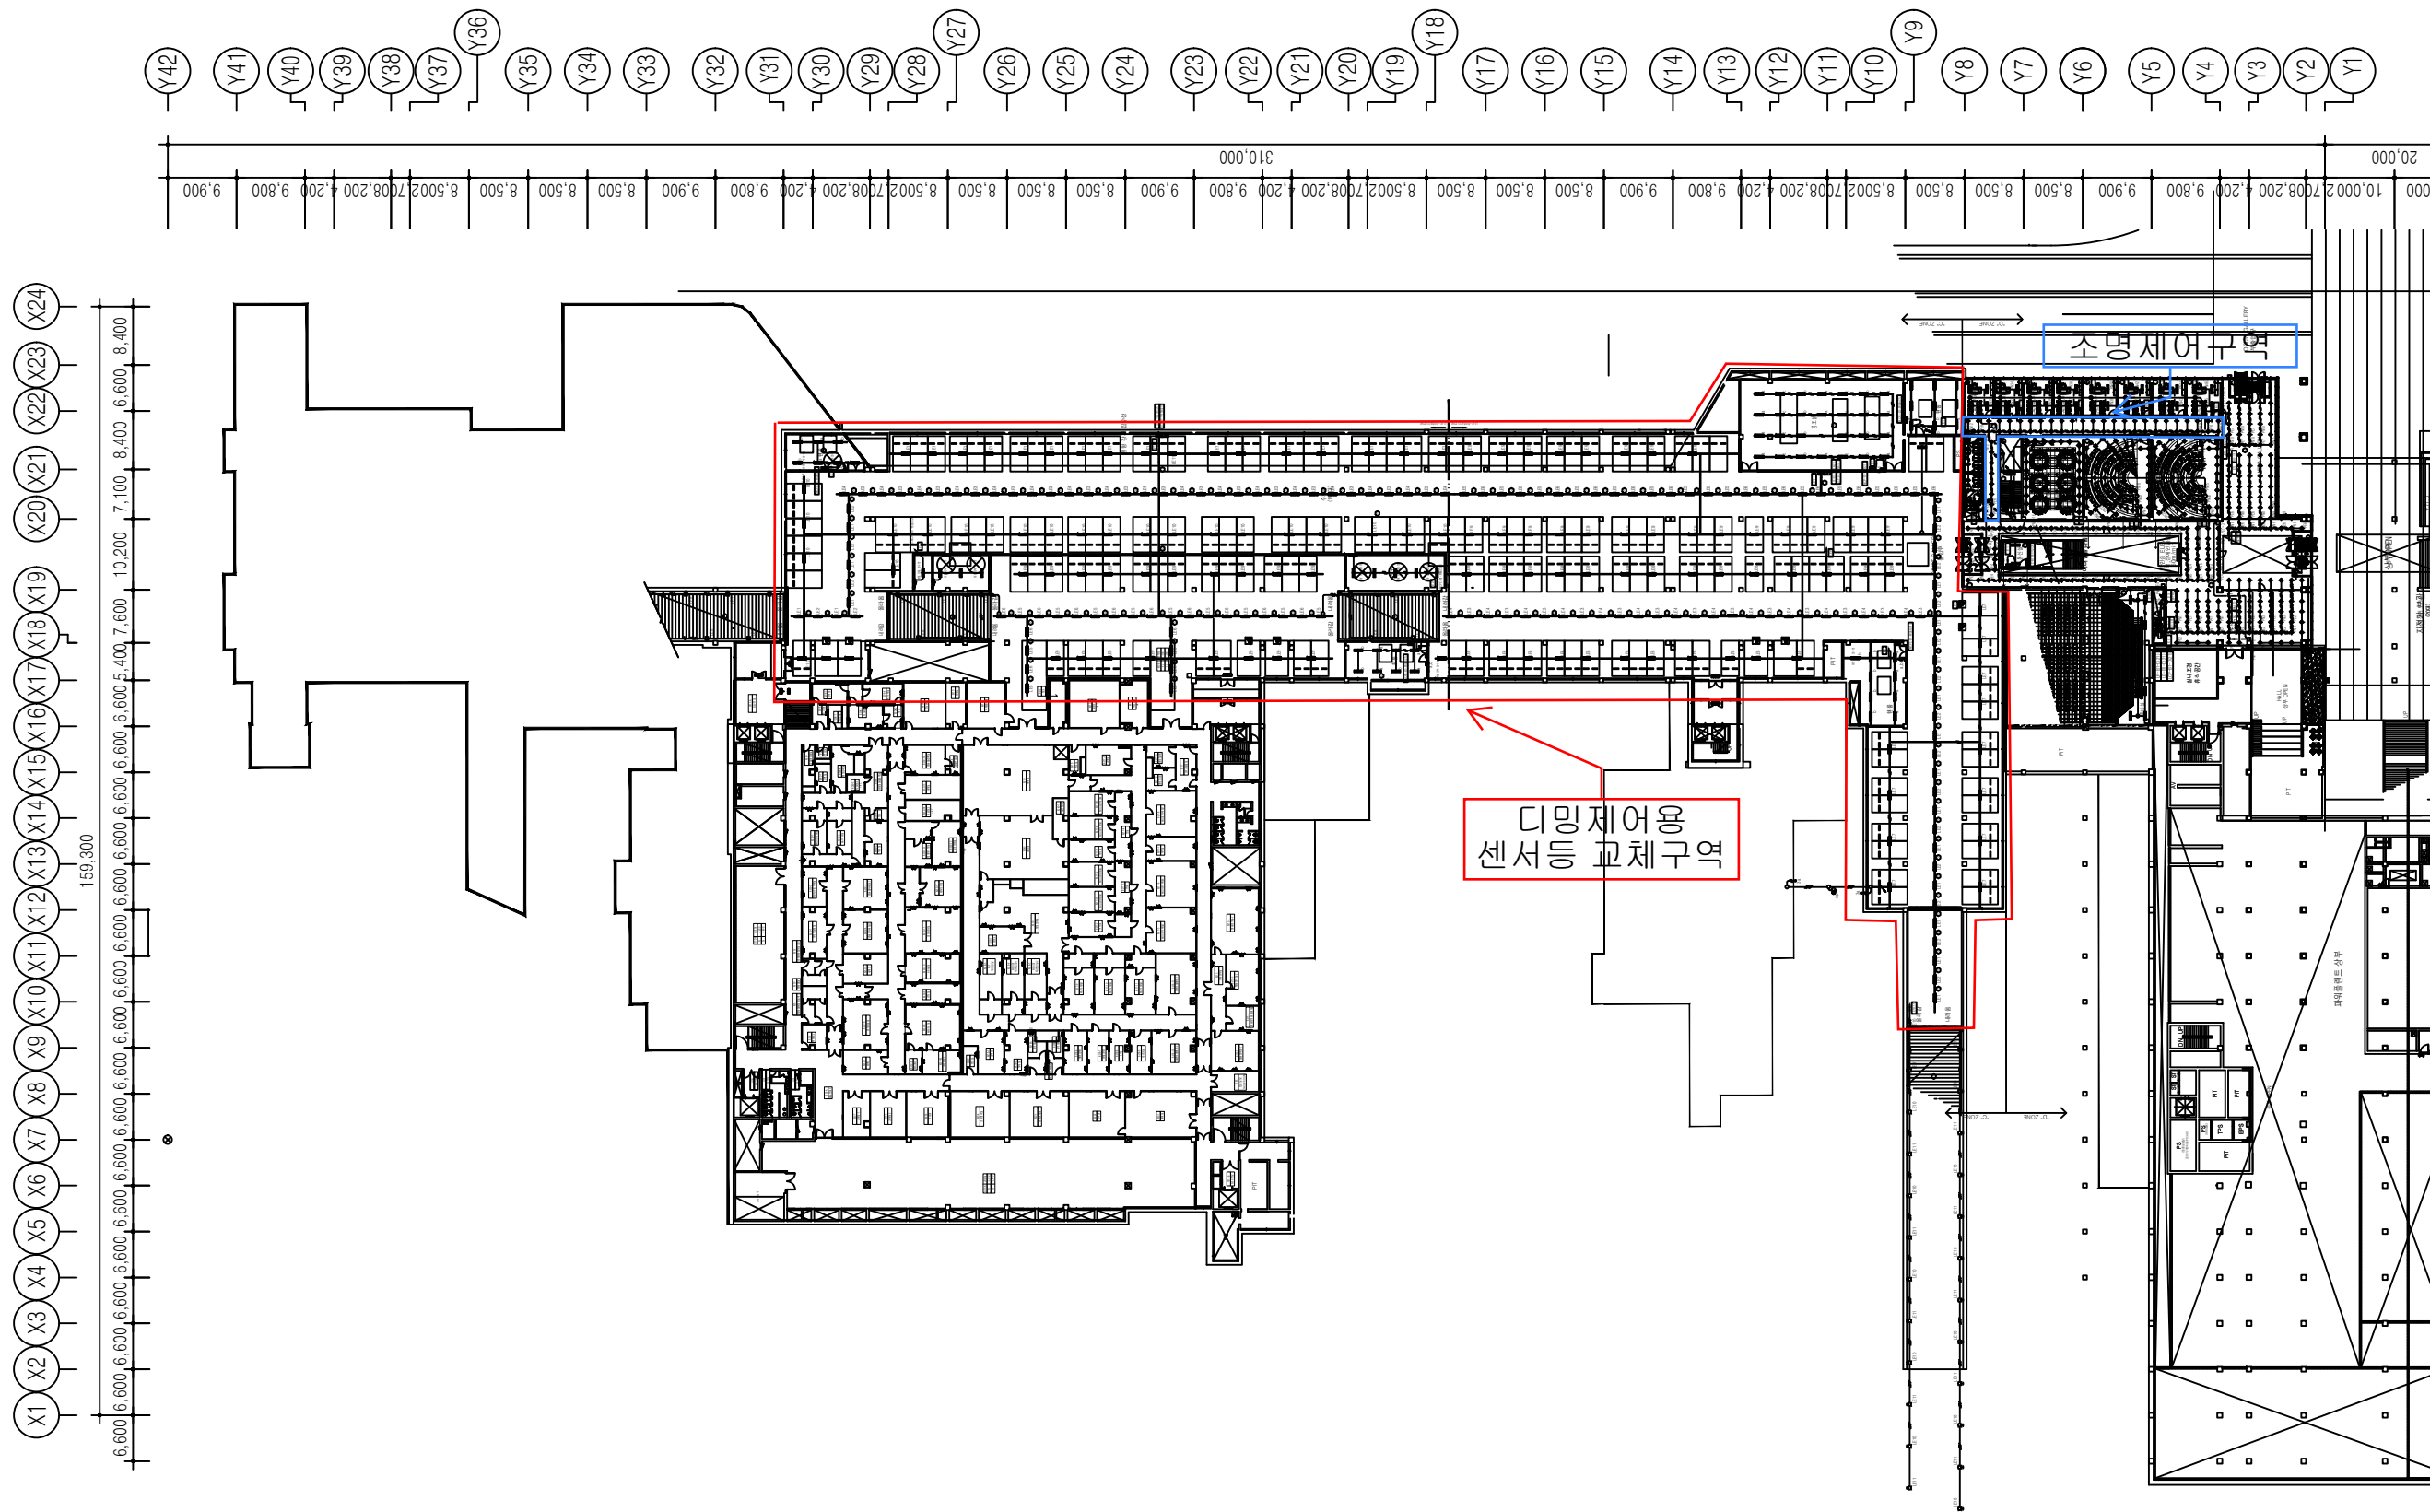

컨실리언스센터 지하1층 전등설비 평면도
축척 A1: 1/500, A3: 1/1000

3					
2					
1	14.12.04	실명/호실 수정			
REV	DATE	DESCRIPTION	DRN	CHK	APR
DRAWING TITLE					
컨실리언스센터 지하1층 전등설비 평면도					
APPROVED					
CHECKED1					
CHECKED2					
DRAWN					
PROJECT NO.					
SCALE					
A1	1/500	A3	1/1000	APPROVAL DATE	
DRAWING NO.				REV.	
E-21-0601					

3					
2					
1	12.01	설계/호칭 수정			
REV	DATE	DESCRIPTION	DRN	CHK	APR

DRAWING TITLE

컨실리언스센터 지상1층
전등설비 평면도

APPROVED

CHECKED1

CHECKED2

DRAWN


PROJECT NO.

SCALE
 A1 1/500 A3 1/1000

APPROVAL DATE


DRAWING NO. REV.

E-21-602

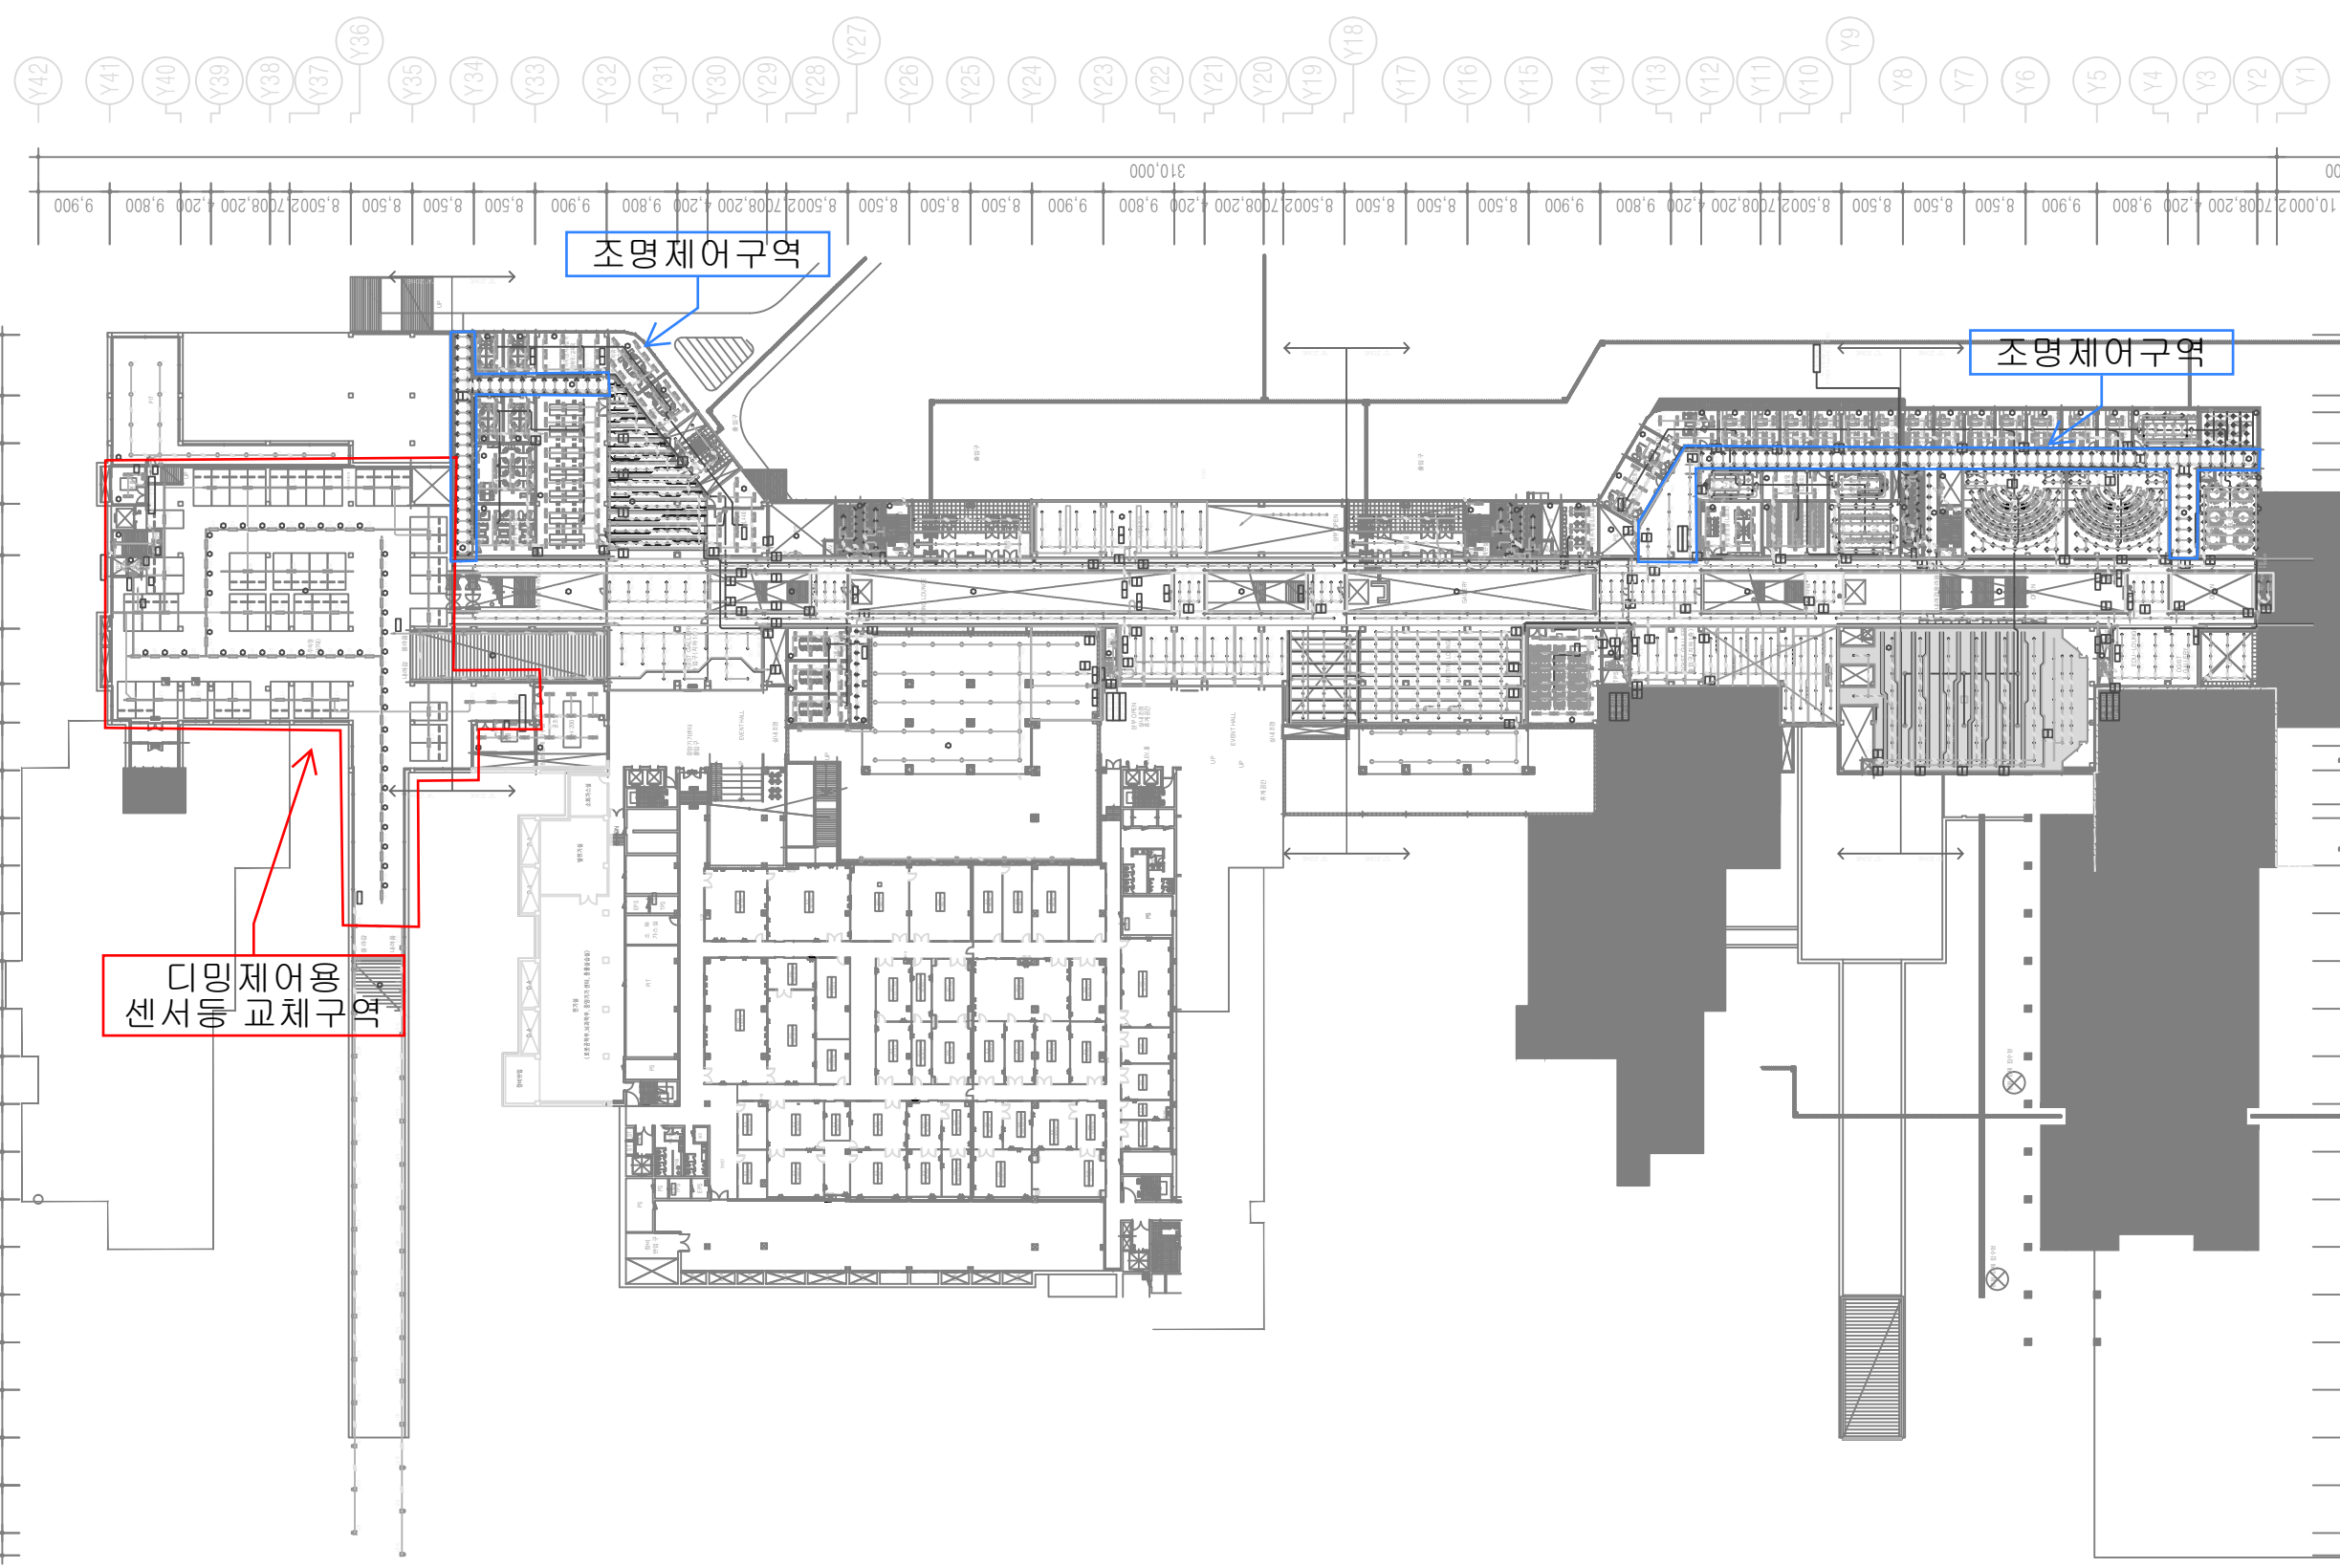

컨실리언스센터 지상1층 전등설비 평면도

축척 A1: 1/500, A3: 1/1000

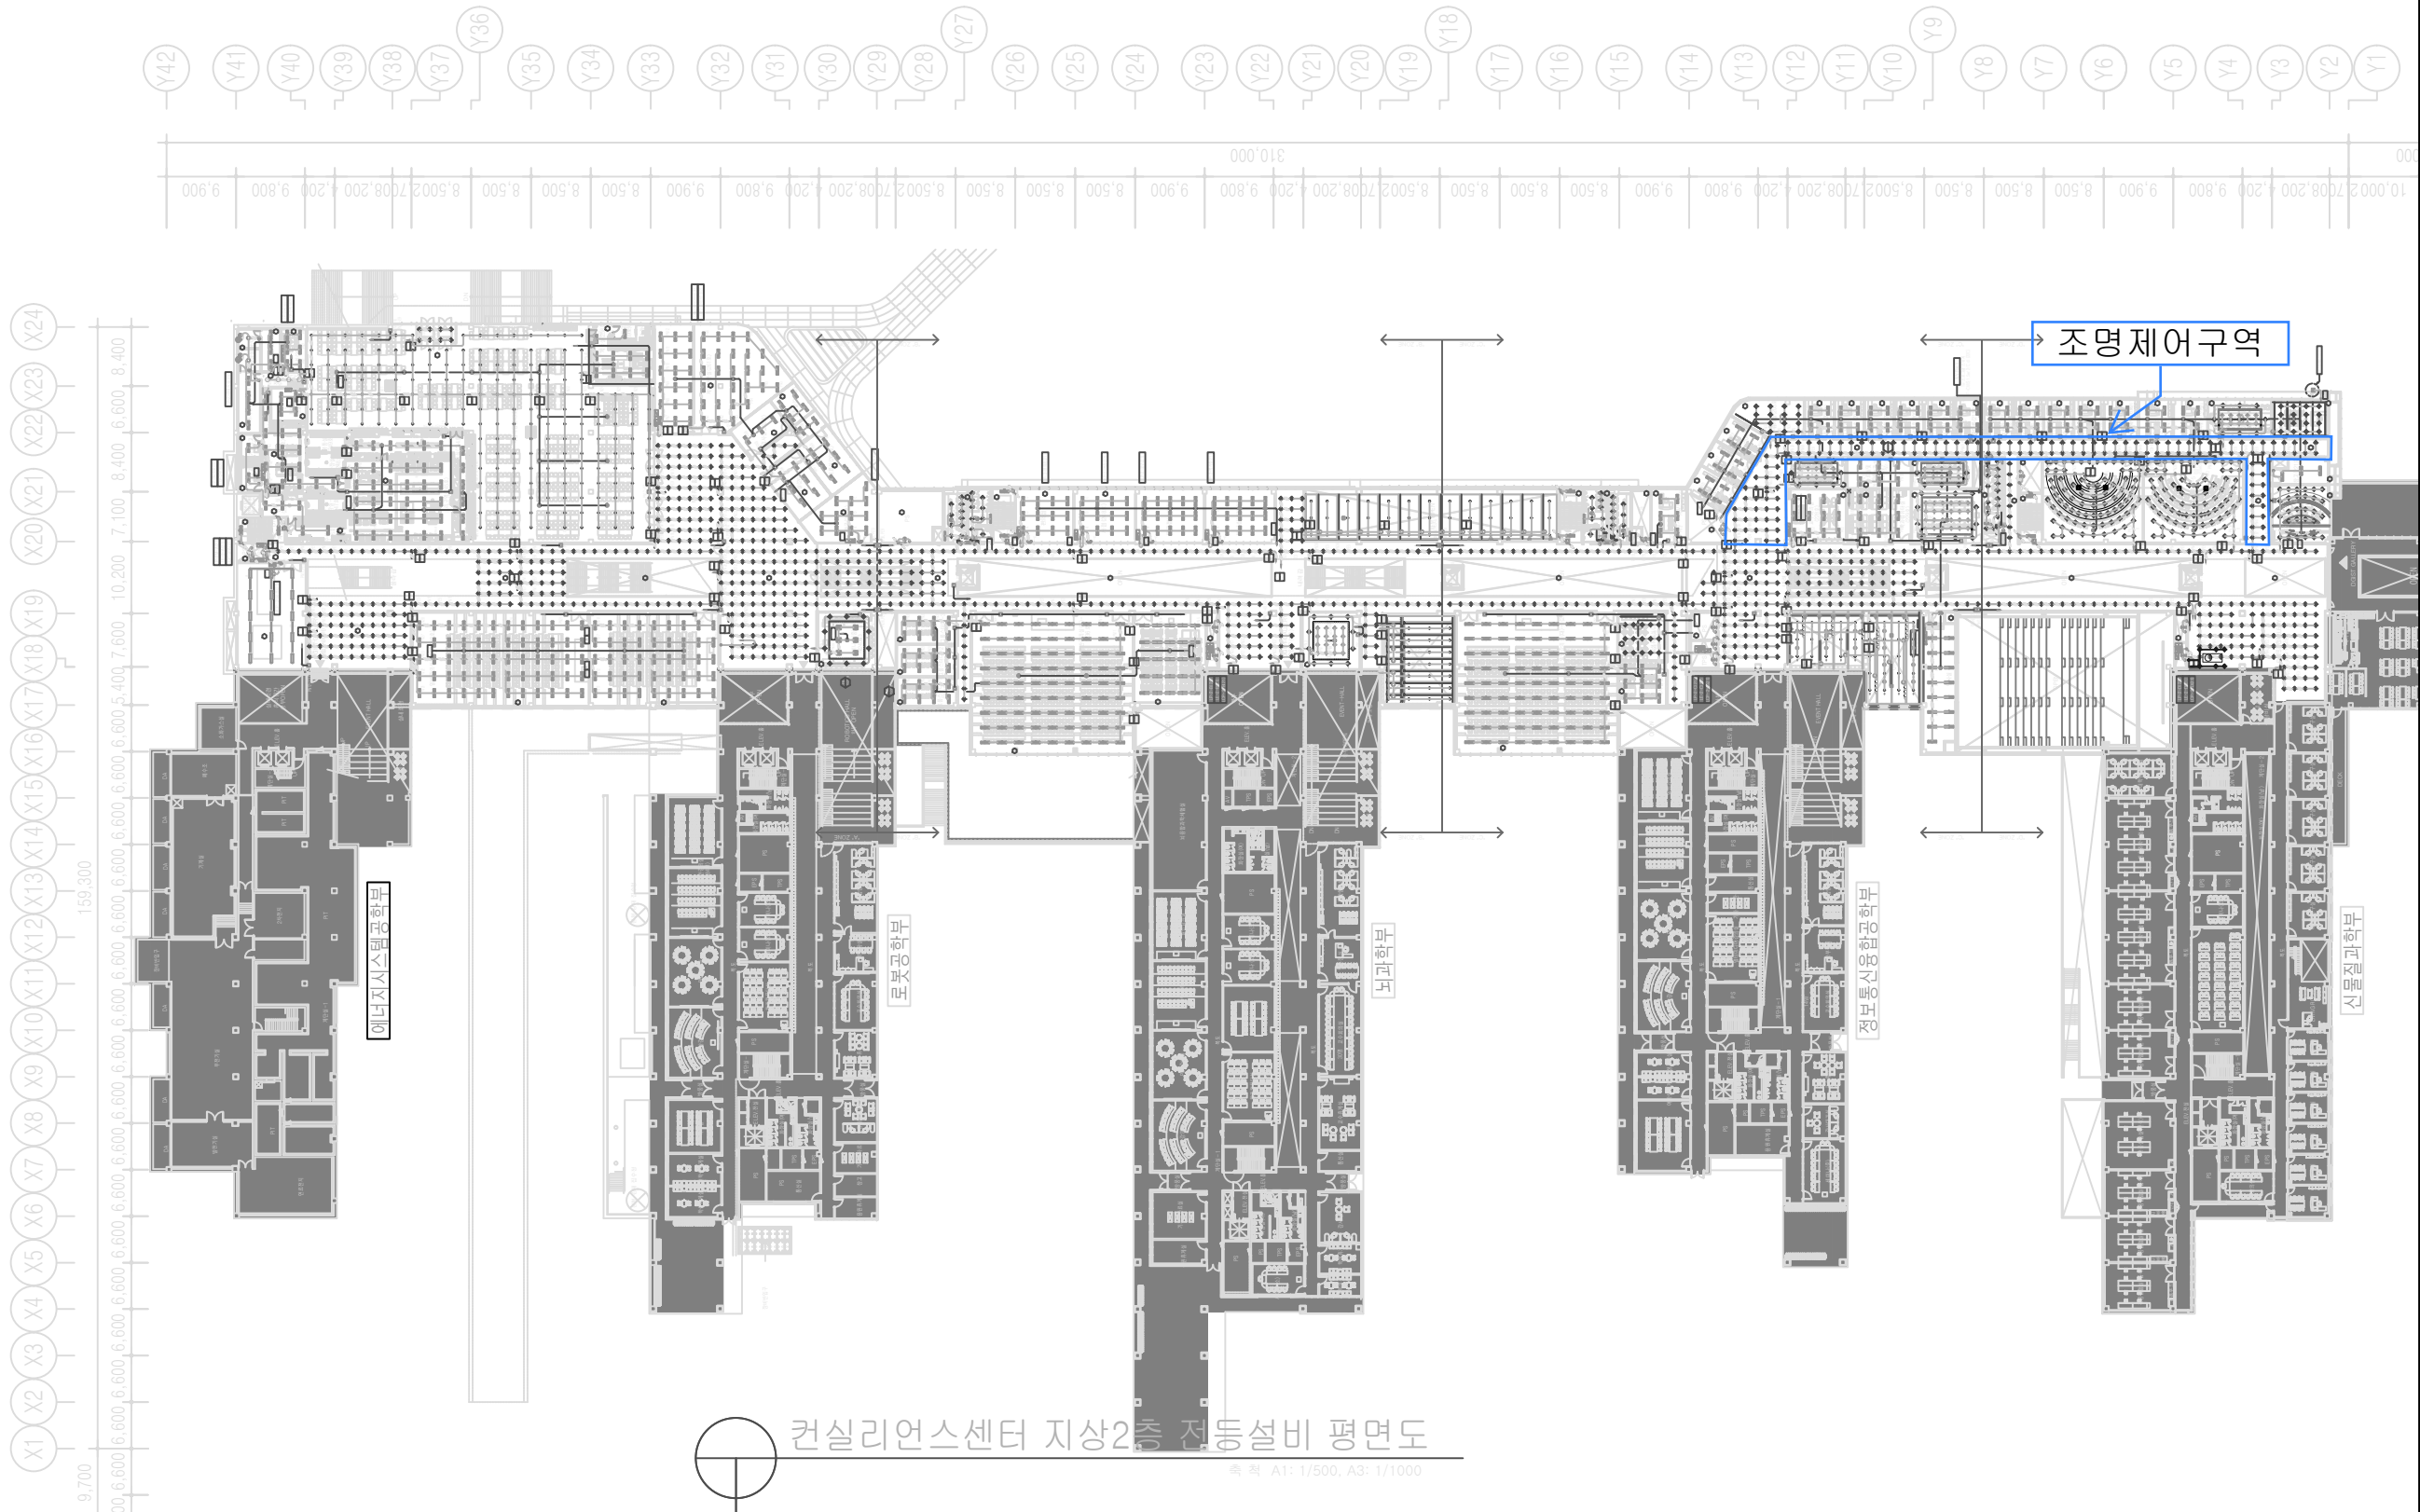

컨실리언스센터 지상2층 전등설비 평면도
 축척 A1: 1/500, A3: 1/1000


3					
2					
1	04.12.04	설계/호설 수정			
REV	DATE	DESCRIPTION	DRN	CHK	APR
DRAWING TITLE					
컨실리언스센터 지상2층 전등설비 평면도					
APPROVED					
CHECKED1					
CHECKED2					
DRAWN					
PROJECT NO.					
SCALE					
A1	A3	APPROVAL DATE			
1/500	1/1000				
DRAWING NO.				REV.	
E-21-0603					

학위과정시설 임대형민자사업(BTL)

Construction

Construction Management

NOTE

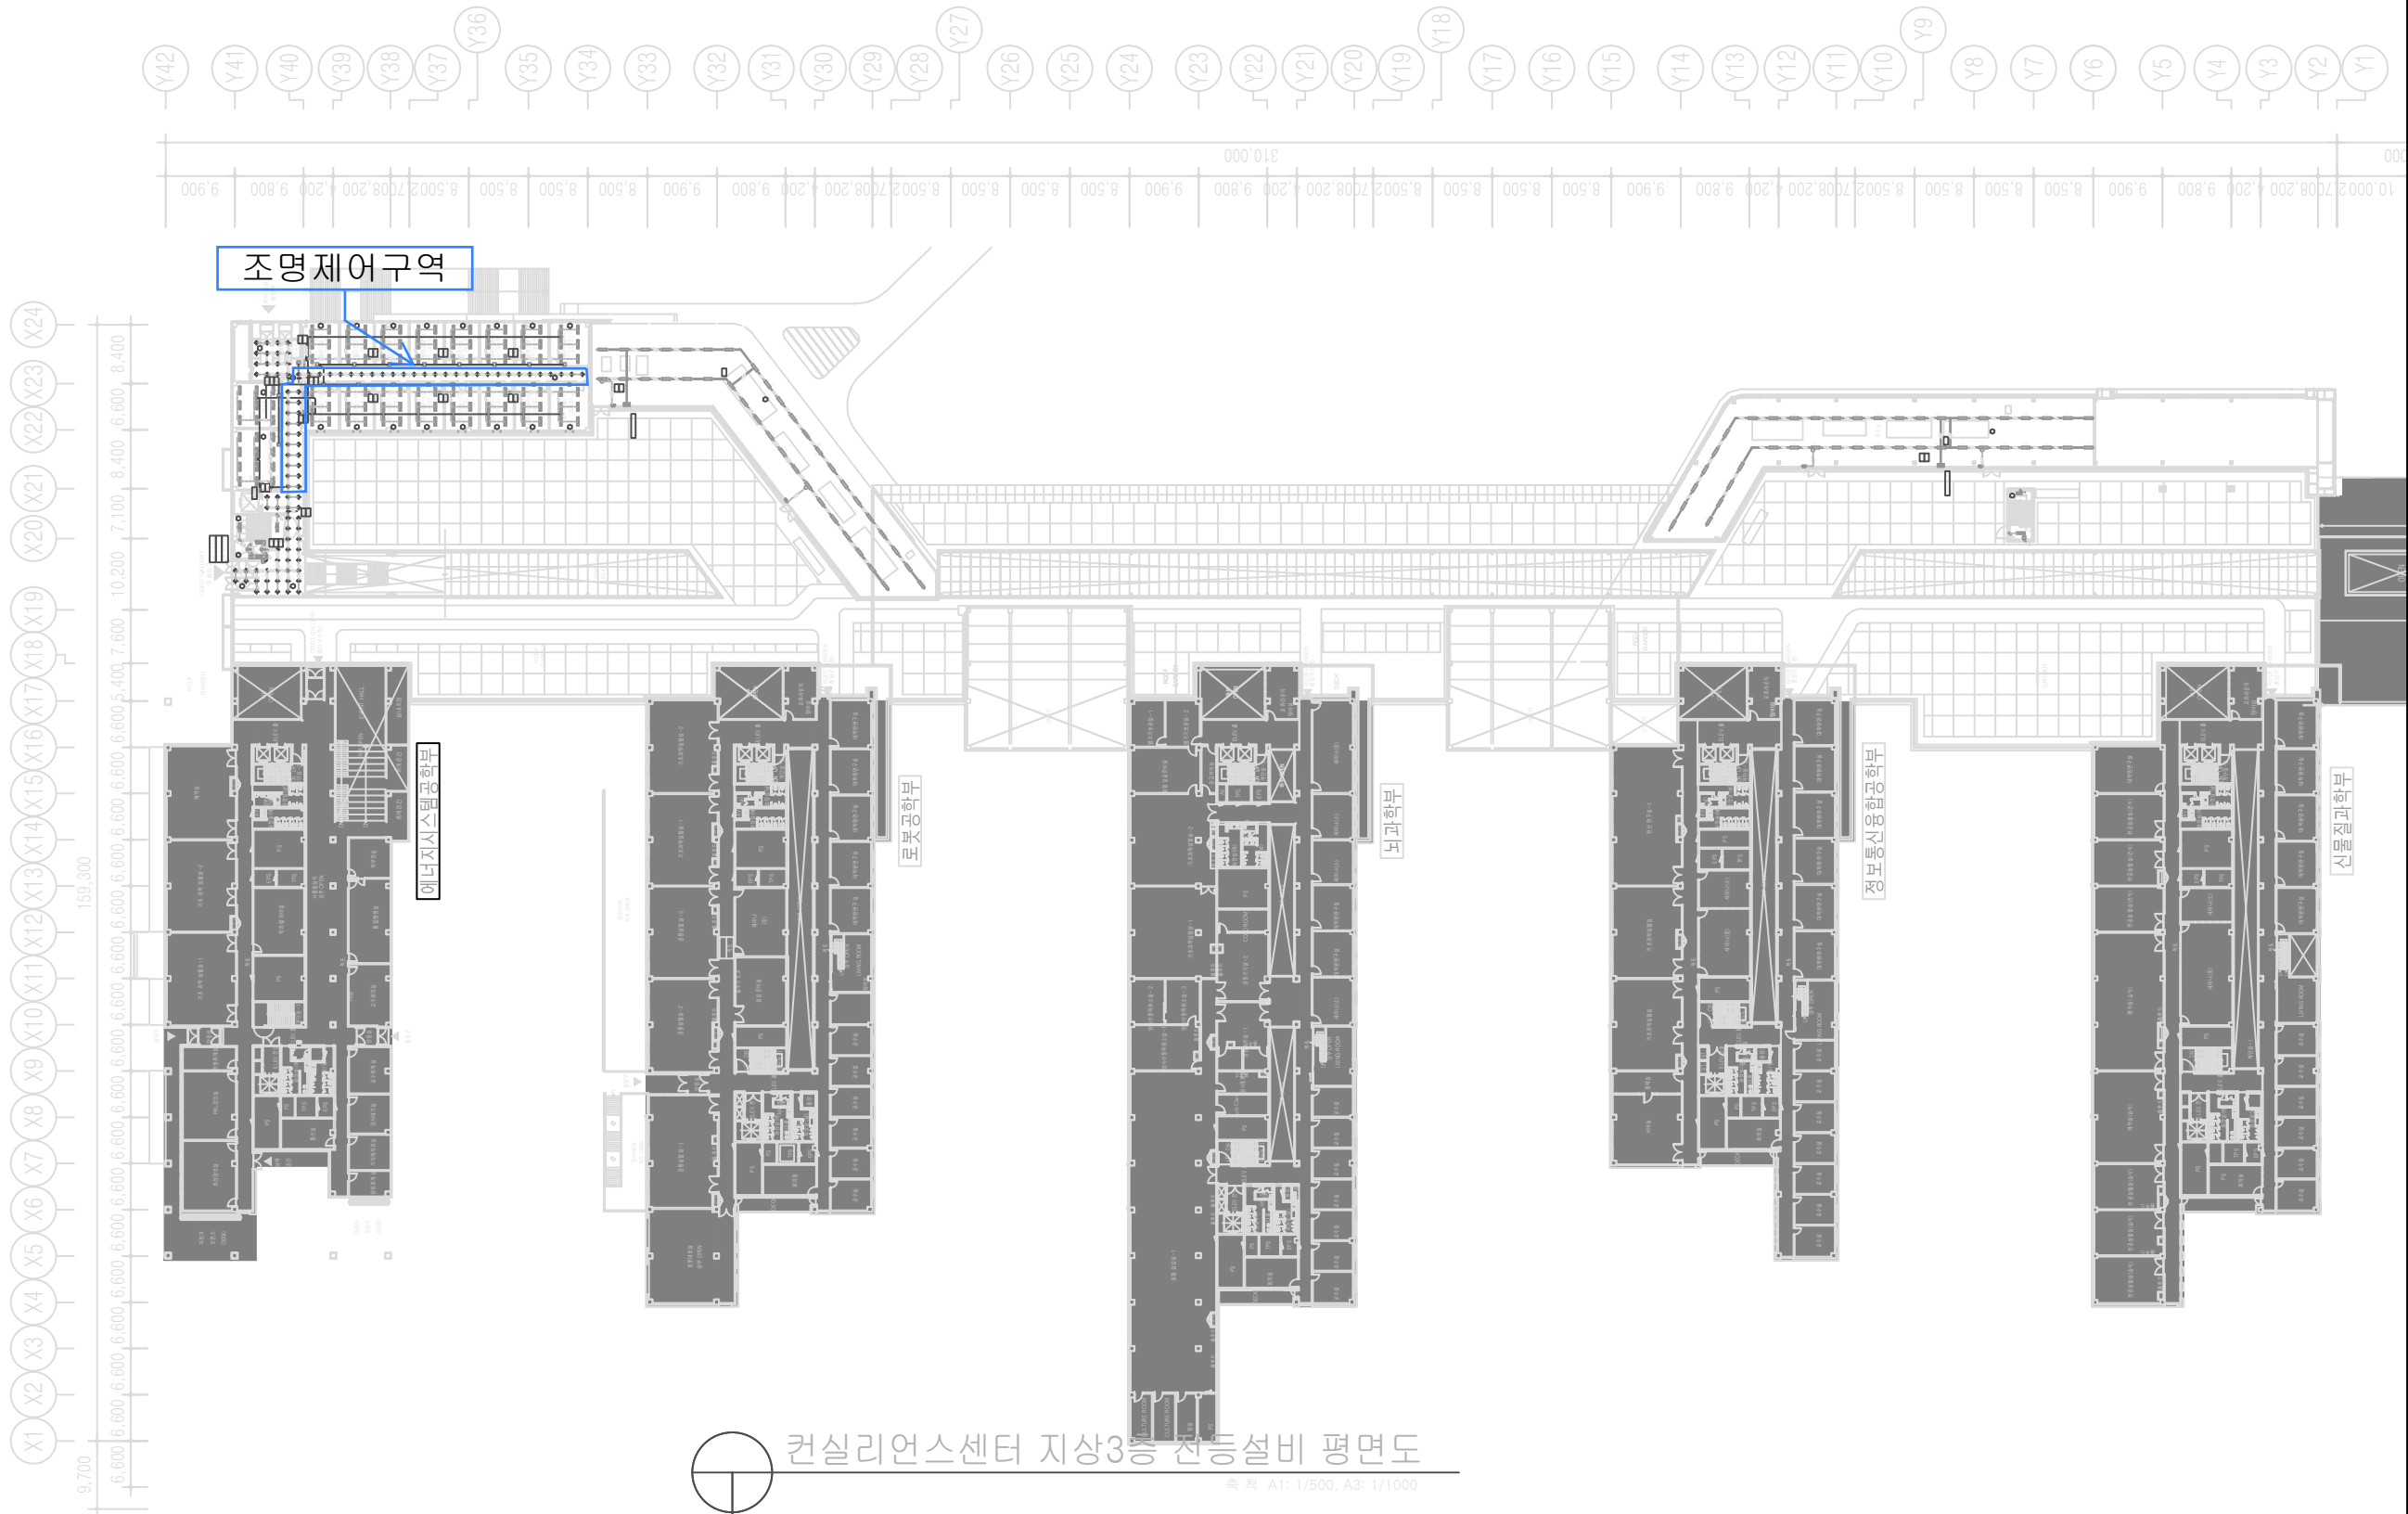

컨실리언스센터 지상3층 전등설비 평면도

축척 A1: 1/500, A3: 1/1000

3					
2					
1	12.01	설계/호칭 수정			
REV	DATE	DESCRIPTION	DRN	CHK	APR
DRAWING TITLE					
컨실리언스센터 지상3층 전등설비 평면도					
APPROVED					
CHECKED1					
CHECKED2					
DRAWN					
PROJECT NO.					
SCALE					
A1	A3	APPROVAL DATE			
1/500	1/1000				
DRAWING NO.					REV.
E-21-604					