


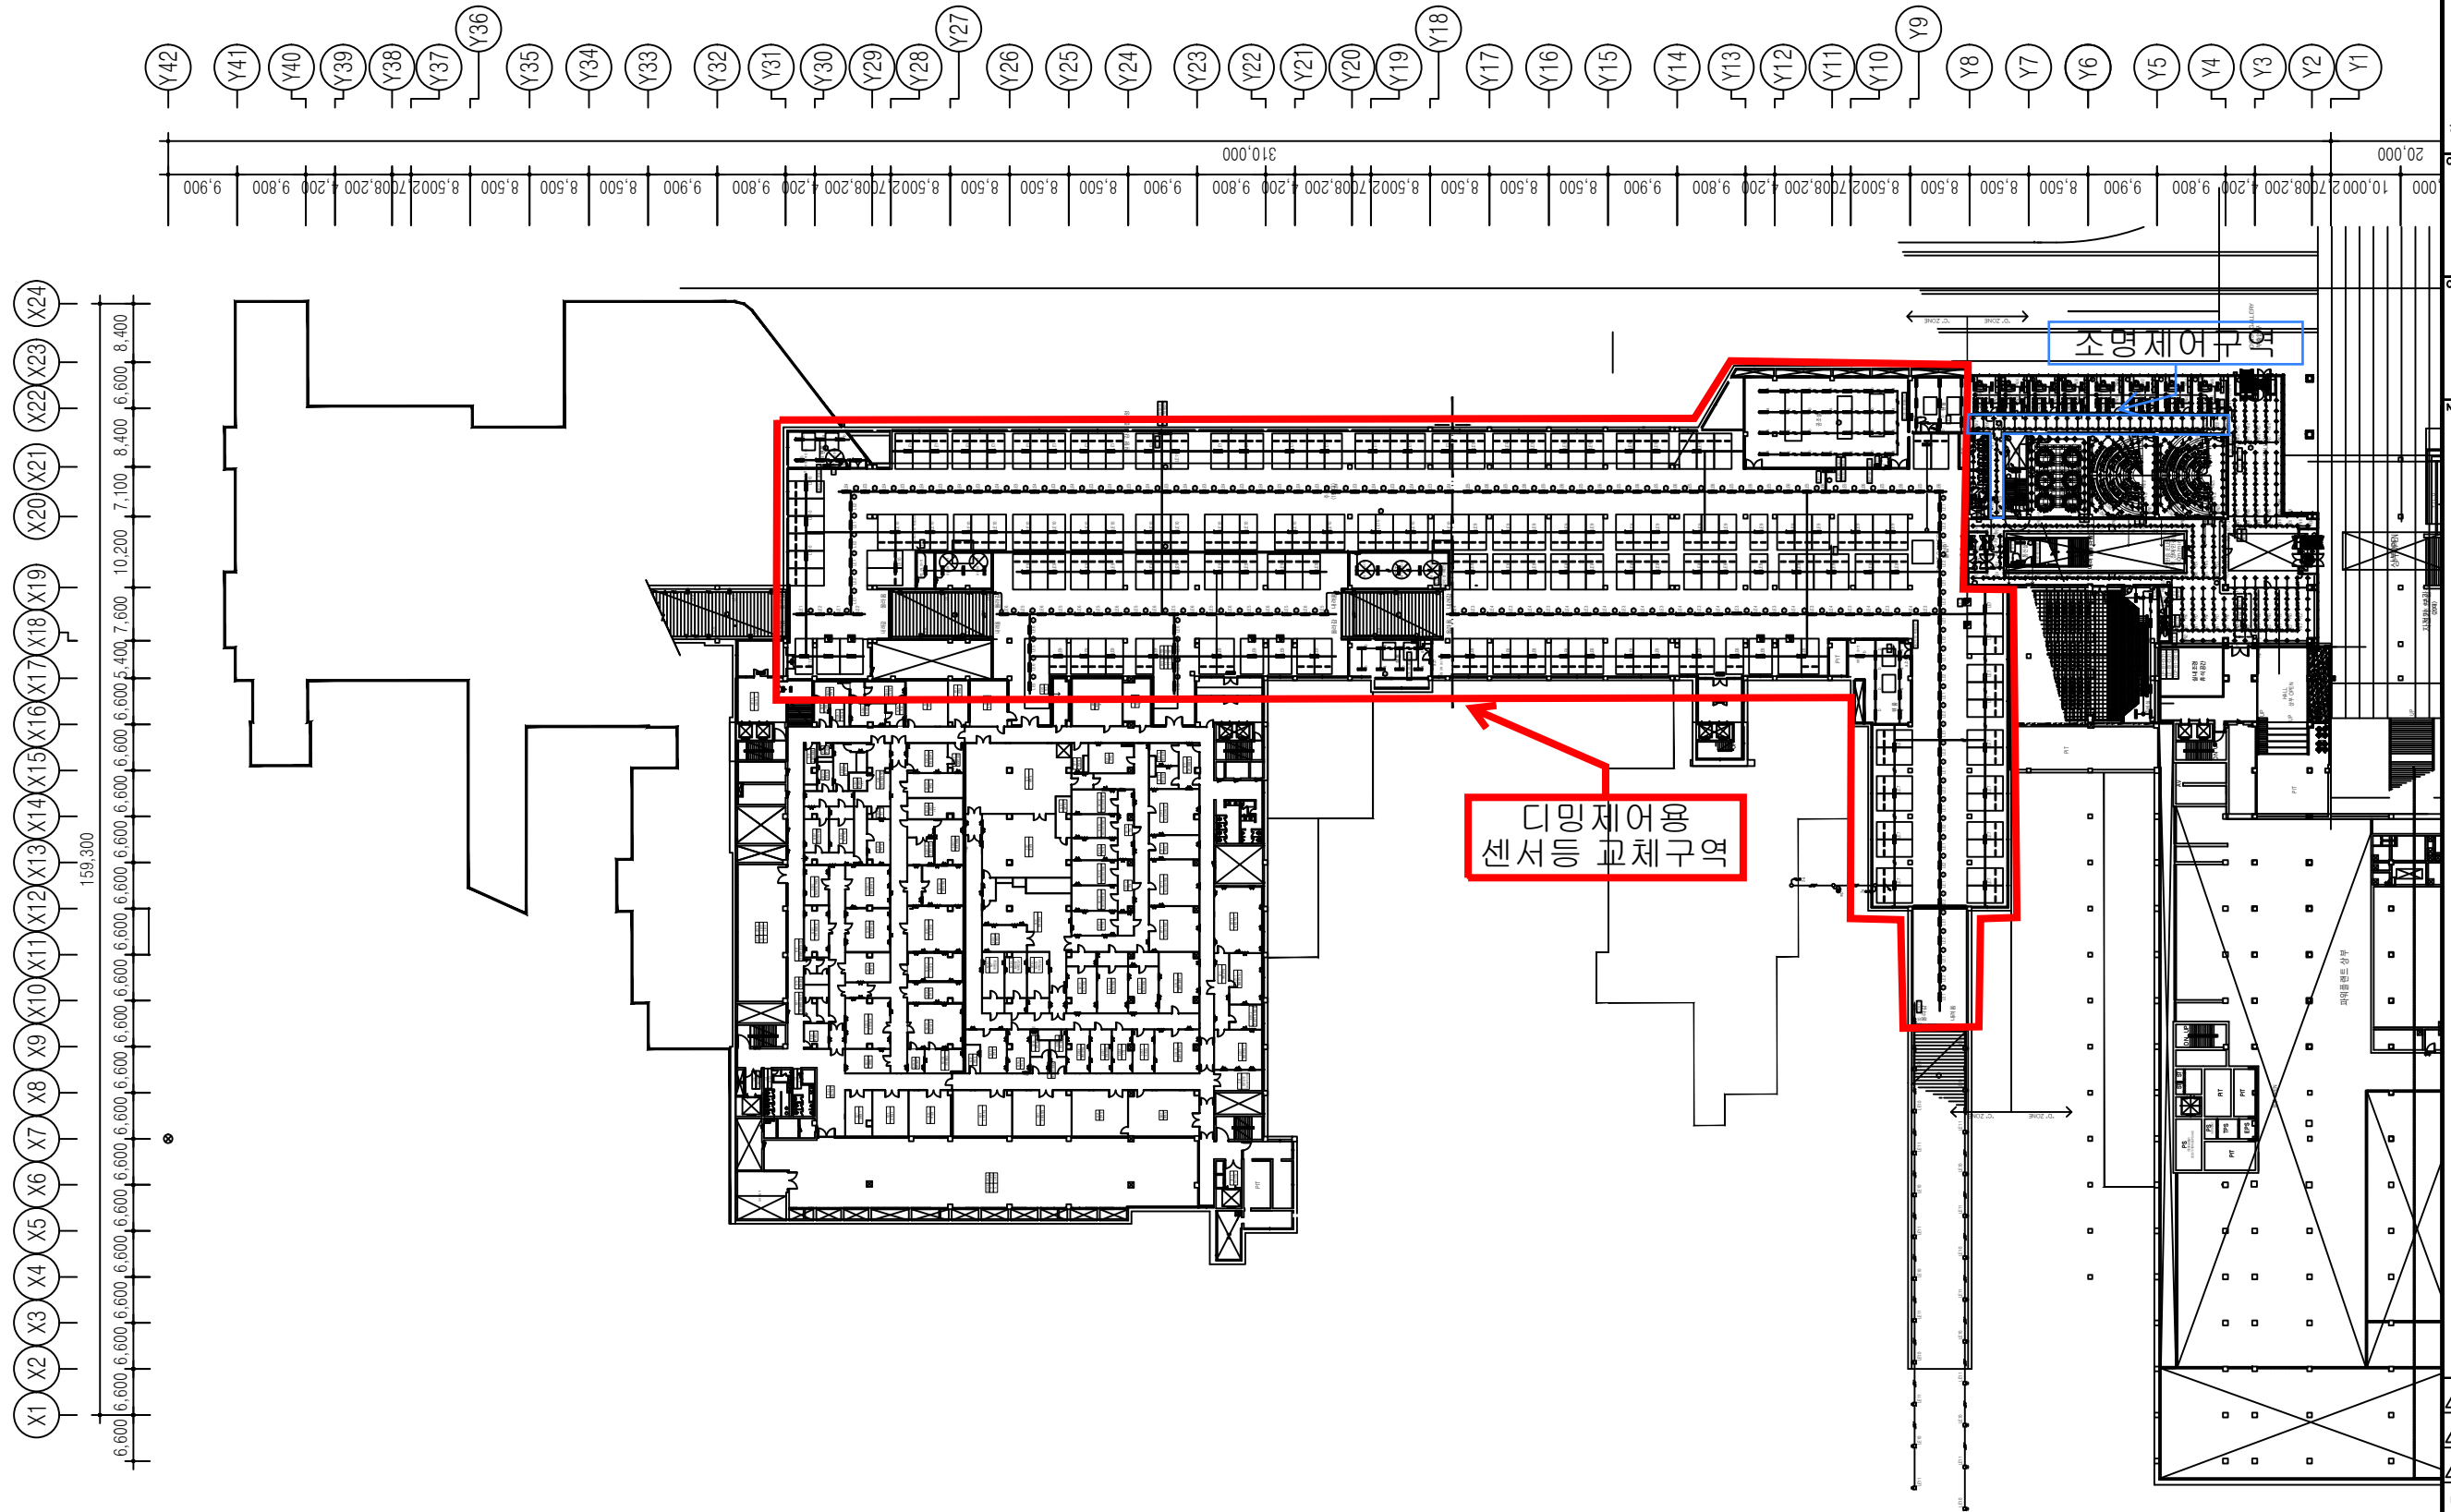

컨실리언스센터 지하1층 전등설비 평면도  
축척 A1: 1/500, A3: 1/1000

| 3                        |          |               |     |     |      |
|--------------------------|----------|---------------|-----|-----|------|
| 2                        |          |               |     |     |      |
| 1                        | 14.12.04 | 실명/호실 수정      |     |     |      |
| REV                      | DATE     | DESCRIPTION   | DRN | CHK | APR  |
| DRAWING TITLE            |          |               |     |     |      |
| 컨실리언스센터 지하1층<br>전등설비 평면도 |          |               |     |     |      |
| APPROVED                 |          |               |     |     |      |
| CHECKED1                 |          |               |     |     |      |
| CHECKED2                 |          |               |     |     |      |
| DRAWN                    |          |               |     |     |      |
| PROJECT NO.              |          |               |     |     |      |
| SCALE                    |          |               |     |     |      |
| A1                       | A3       | APPROVAL DATE |     |     |      |
| 1/500                    | 1/1000   |               |     |     |      |
| DRAWING NO.              |          |               |     |     | REV. |
| E-21-0601                |          |               |     |     |      |

| 3   |       |             |     |     |     |
|-----|-------|-------------|-----|-----|-----|
| 2   |       |             |     |     |     |
| 1   | 12.01 | 설계/호칭 수정    |     |     |     |
| REV | DATE  | DESCRIPTION | DRN | CHK | APR |

DRAWING TITLE  
 컨실리언스센터 지상1층  
 전등설비 평면도

APPROVED

CHECKED1


CHECKED2

DRAWN


PROJECT NO.

SCALE  
 A1 1/500 A3 1/1000  
 APPROVAL DATE

DRAWING NO. E-21-602 REV.

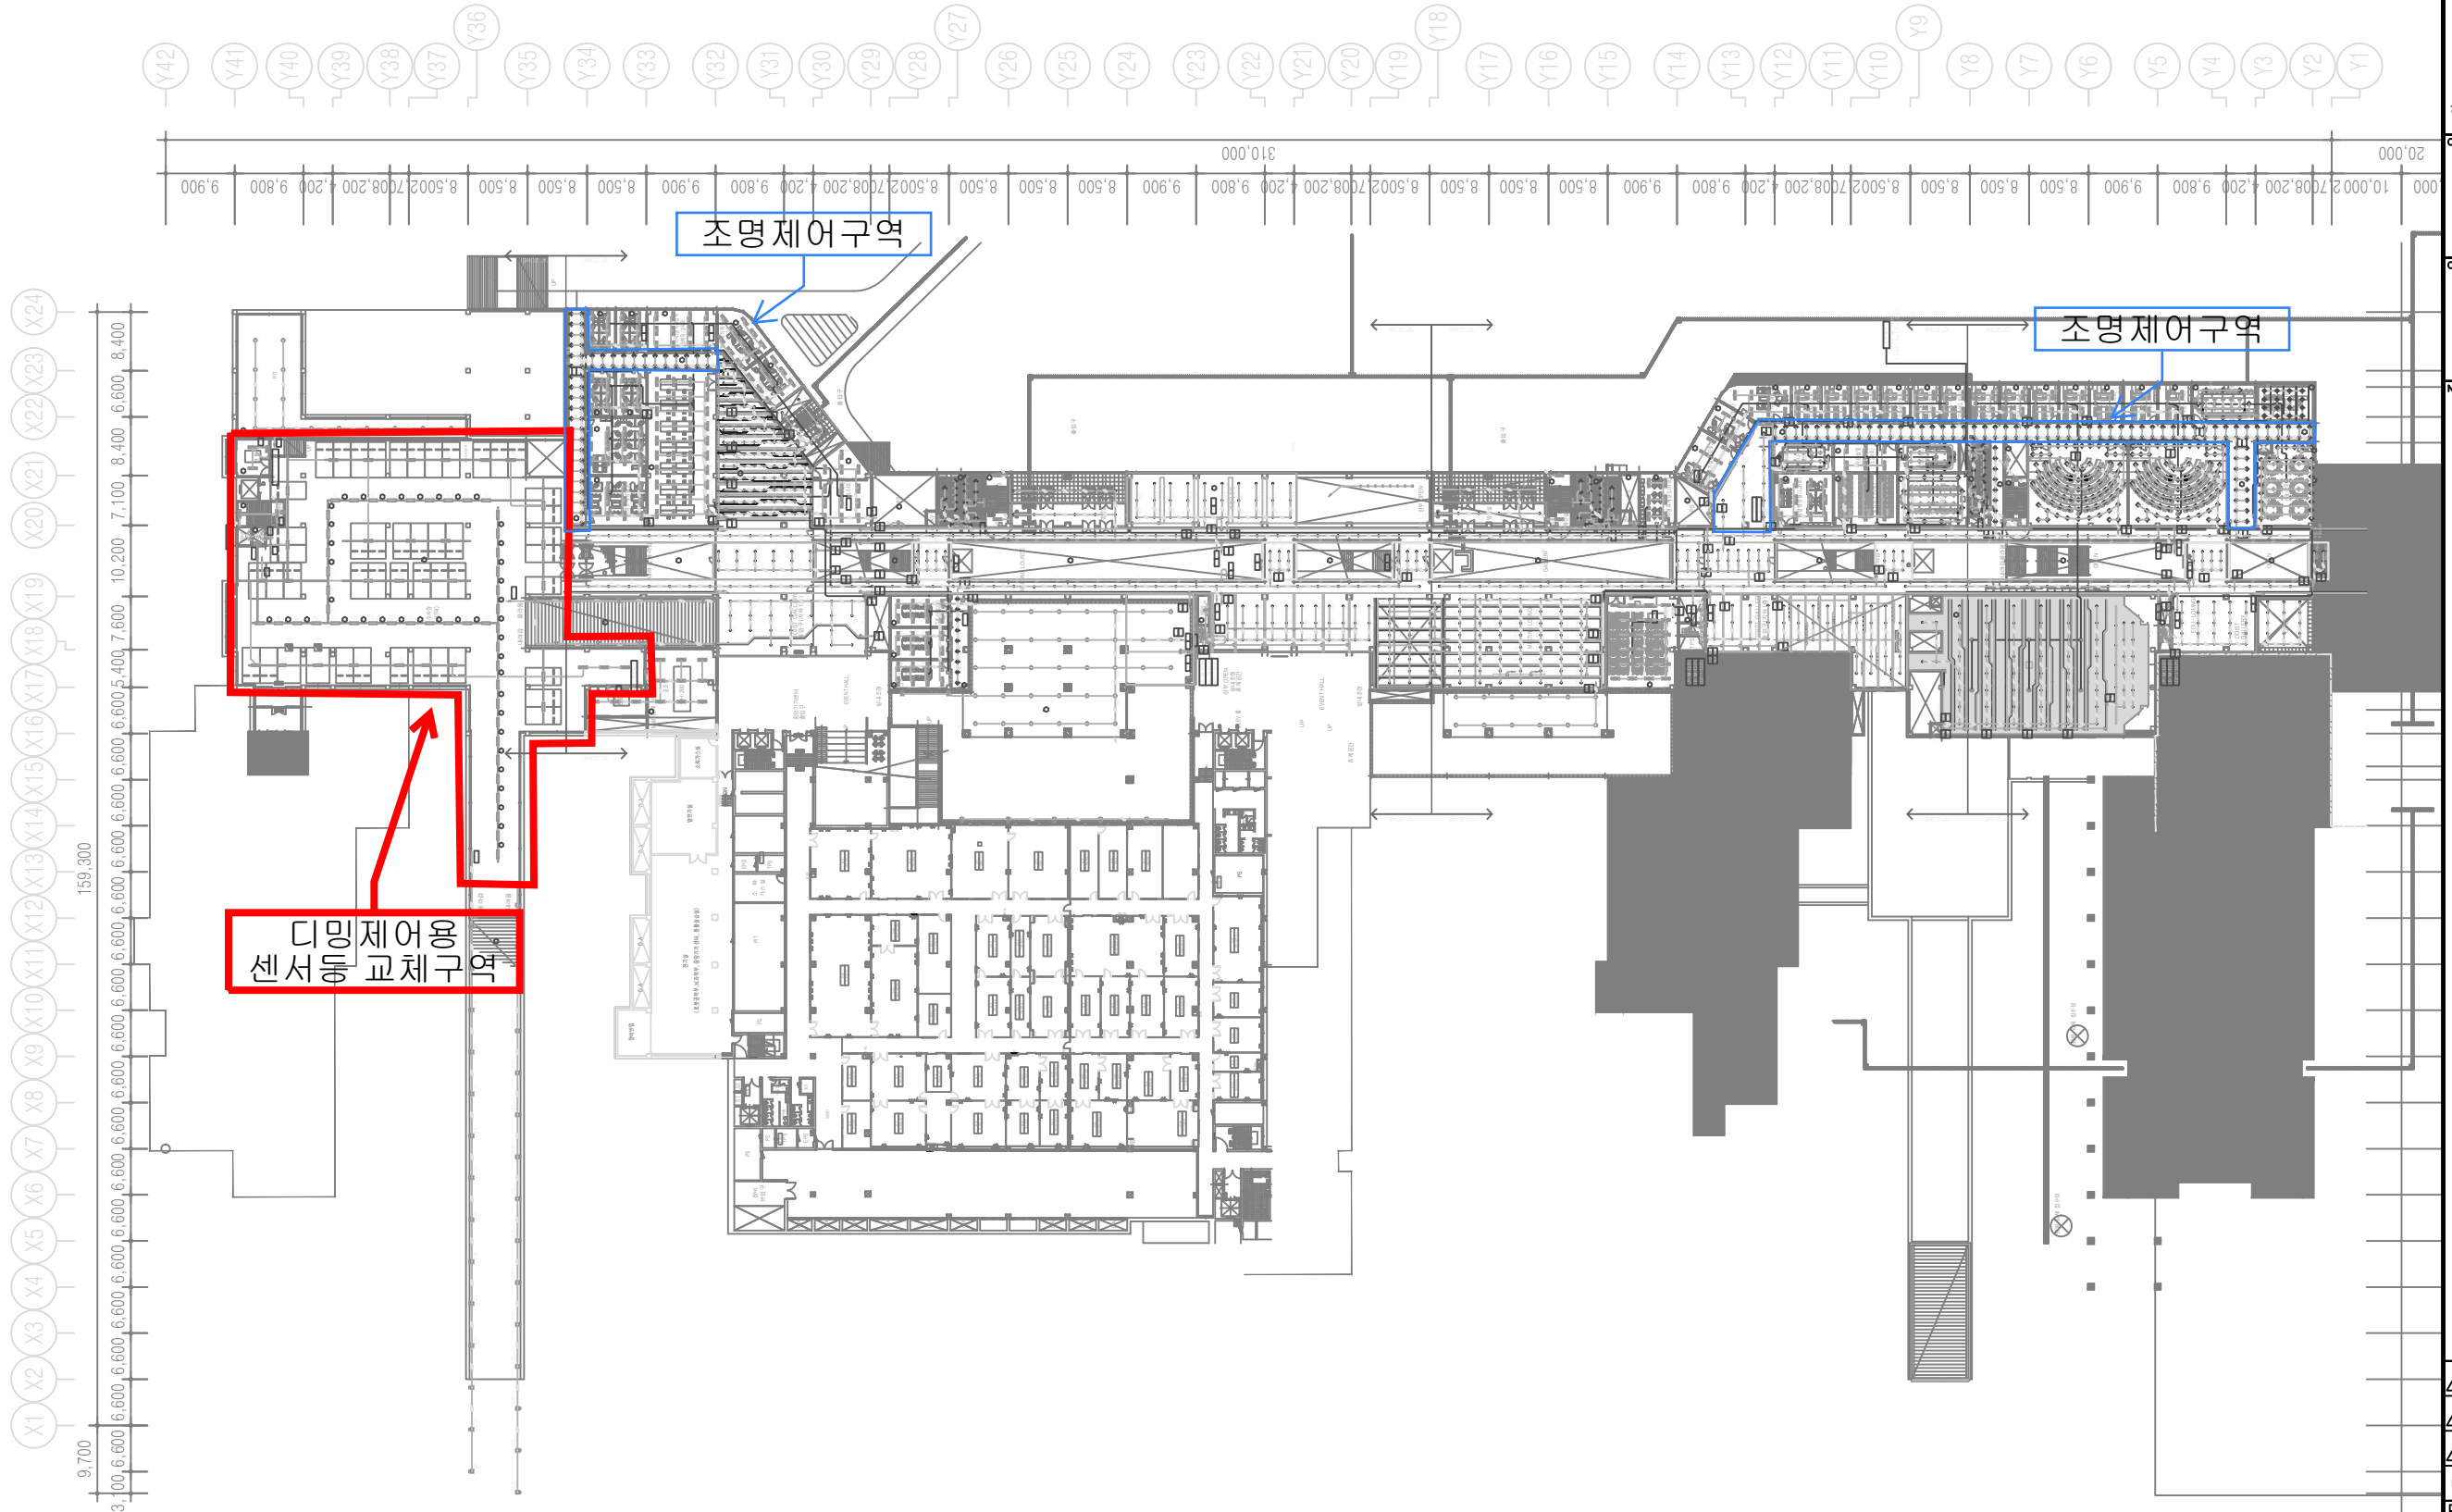


컨실리언스센터 지상1층 전등설비 평면도  
 축척 A1: 1/500, A3: 1/1000

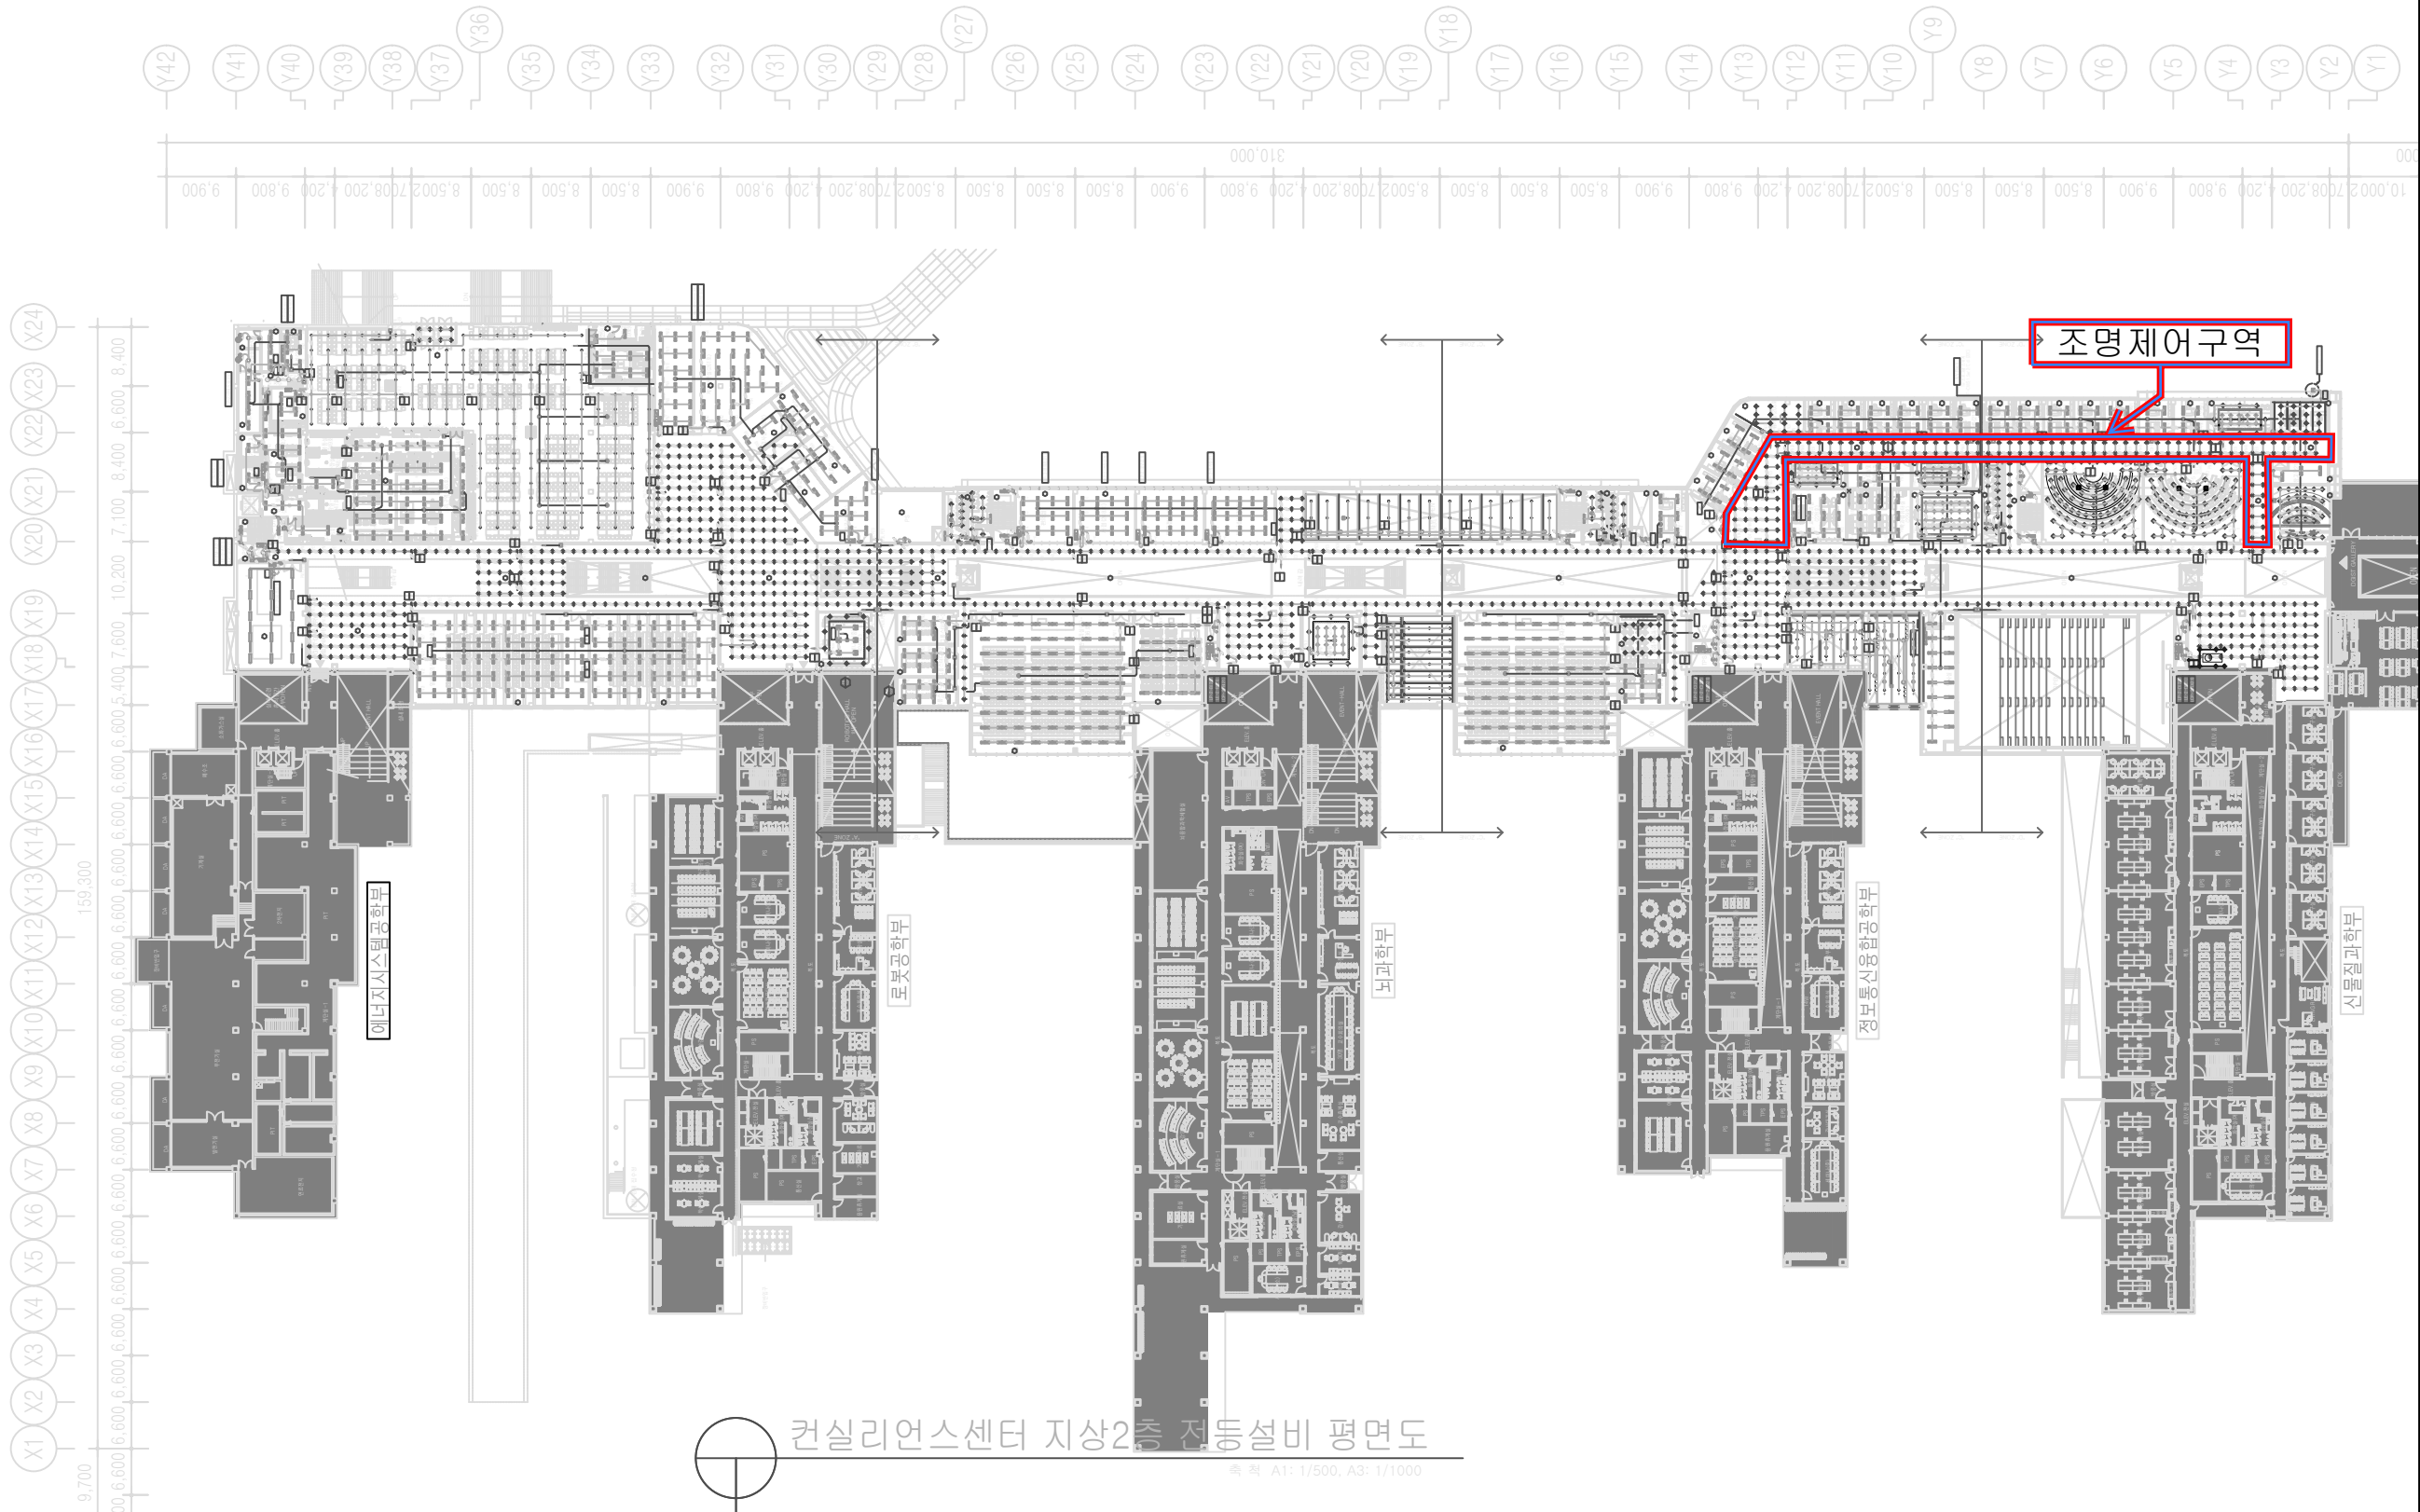

컨실리언스센터 지상2층 전등설비 평면도

축척 A1: 1/500, A3: 1/1000

| 3                        |       |             |        |               |     |
|--------------------------|-------|-------------|--------|---------------|-----|
| 2                        |       |             |        |               |     |
| 1                        | 12.01 | 설계/호칭 수정    |        |               |     |
| REV                      | DATE  | DESCRIPTION | DRN    | CHK           | APR |
| DRAWING TITLE            |       |             |        |               |     |
| 컨실리언스센터 지상2층<br>전등설비 평면도 |       |             |        |               |     |
| APPROVED                 |       |             |        |               |     |
| CHECKED1                 |       |             |        |               |     |
| CHECKED2                 |       |             |        |               |     |
| DRAWN                    |       |             |        |               |     |
| PROJECT NO.              |       |             |        |               |     |
| SCALE                    |       |             |        |               |     |
| A1                       | 1/500 | A3          | 1/1000 | APPROVAL DATE |     |
| DRAWING NO.              |       |             |        | REV.          |     |
| E-21-0603                |       |             |        |               |     |

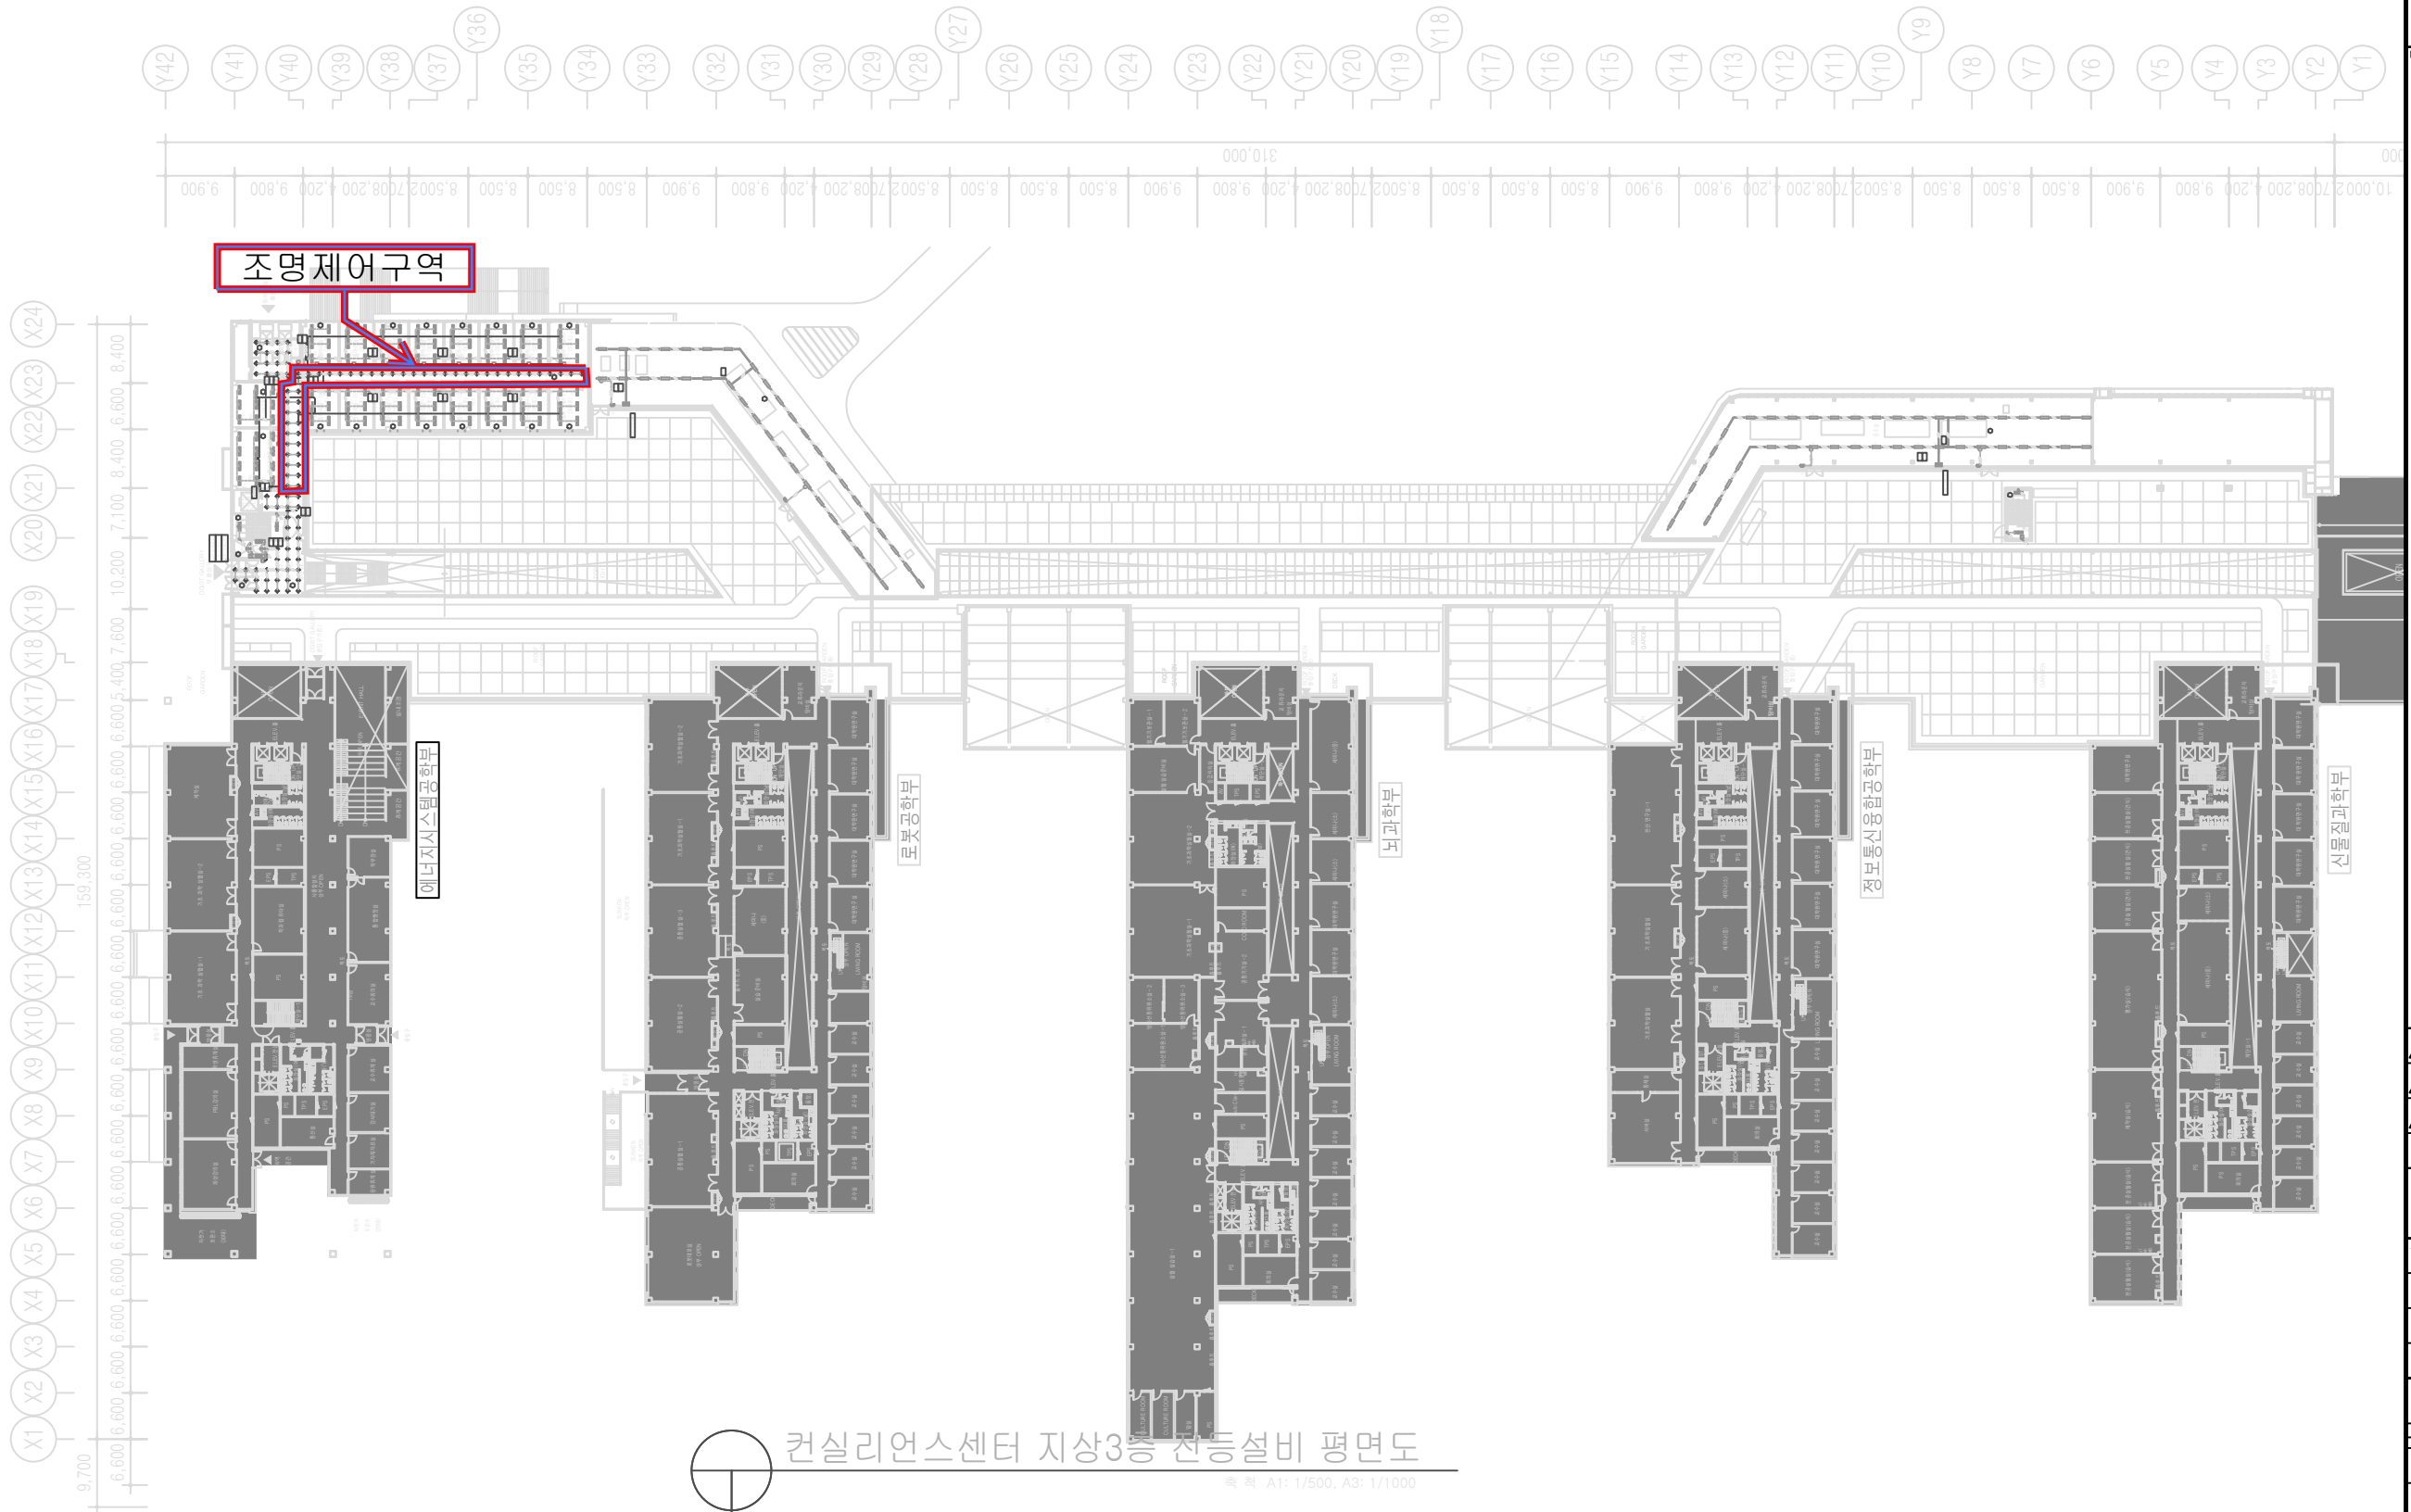

컨실리언스센터 지상3층 전등설비 평면도  
축척 A1: 1/500, A3: 1/1000

|                          |        |               |     |     |      |
|--------------------------|--------|---------------|-----|-----|------|
| 3                        |        |               |     |     |      |
| 2                        |        |               |     |     |      |
| 1                        | 12.01  | 설계/호설 수정      |     |     |      |
| REV                      | DATE   | DESCRIPTION   | DRN | CHK | APR  |
| DRAWING TITLE            |        |               |     |     |      |
| 컨실리언스센터 지상3층<br>전등설비 평면도 |        |               |     |     |      |
| APPROVED                 |        |               |     |     |      |
| CHECKED1                 |        |               |     |     |      |
| CHECKED2                 |        |               |     |     |      |
| DRAWN                    |        |               |     |     |      |
| PROJECT NO.              |        |               |     |     |      |
| SCALE                    |        |               |     |     |      |
| A1                       | A3     | APPROVAL DATE |     |     |      |
| 1/500                    | 1/1000 |               |     |     |      |
| DRAWING NO.              |        |               |     |     | REV. |
| E-21-604                 |        |               |     |     |      |