
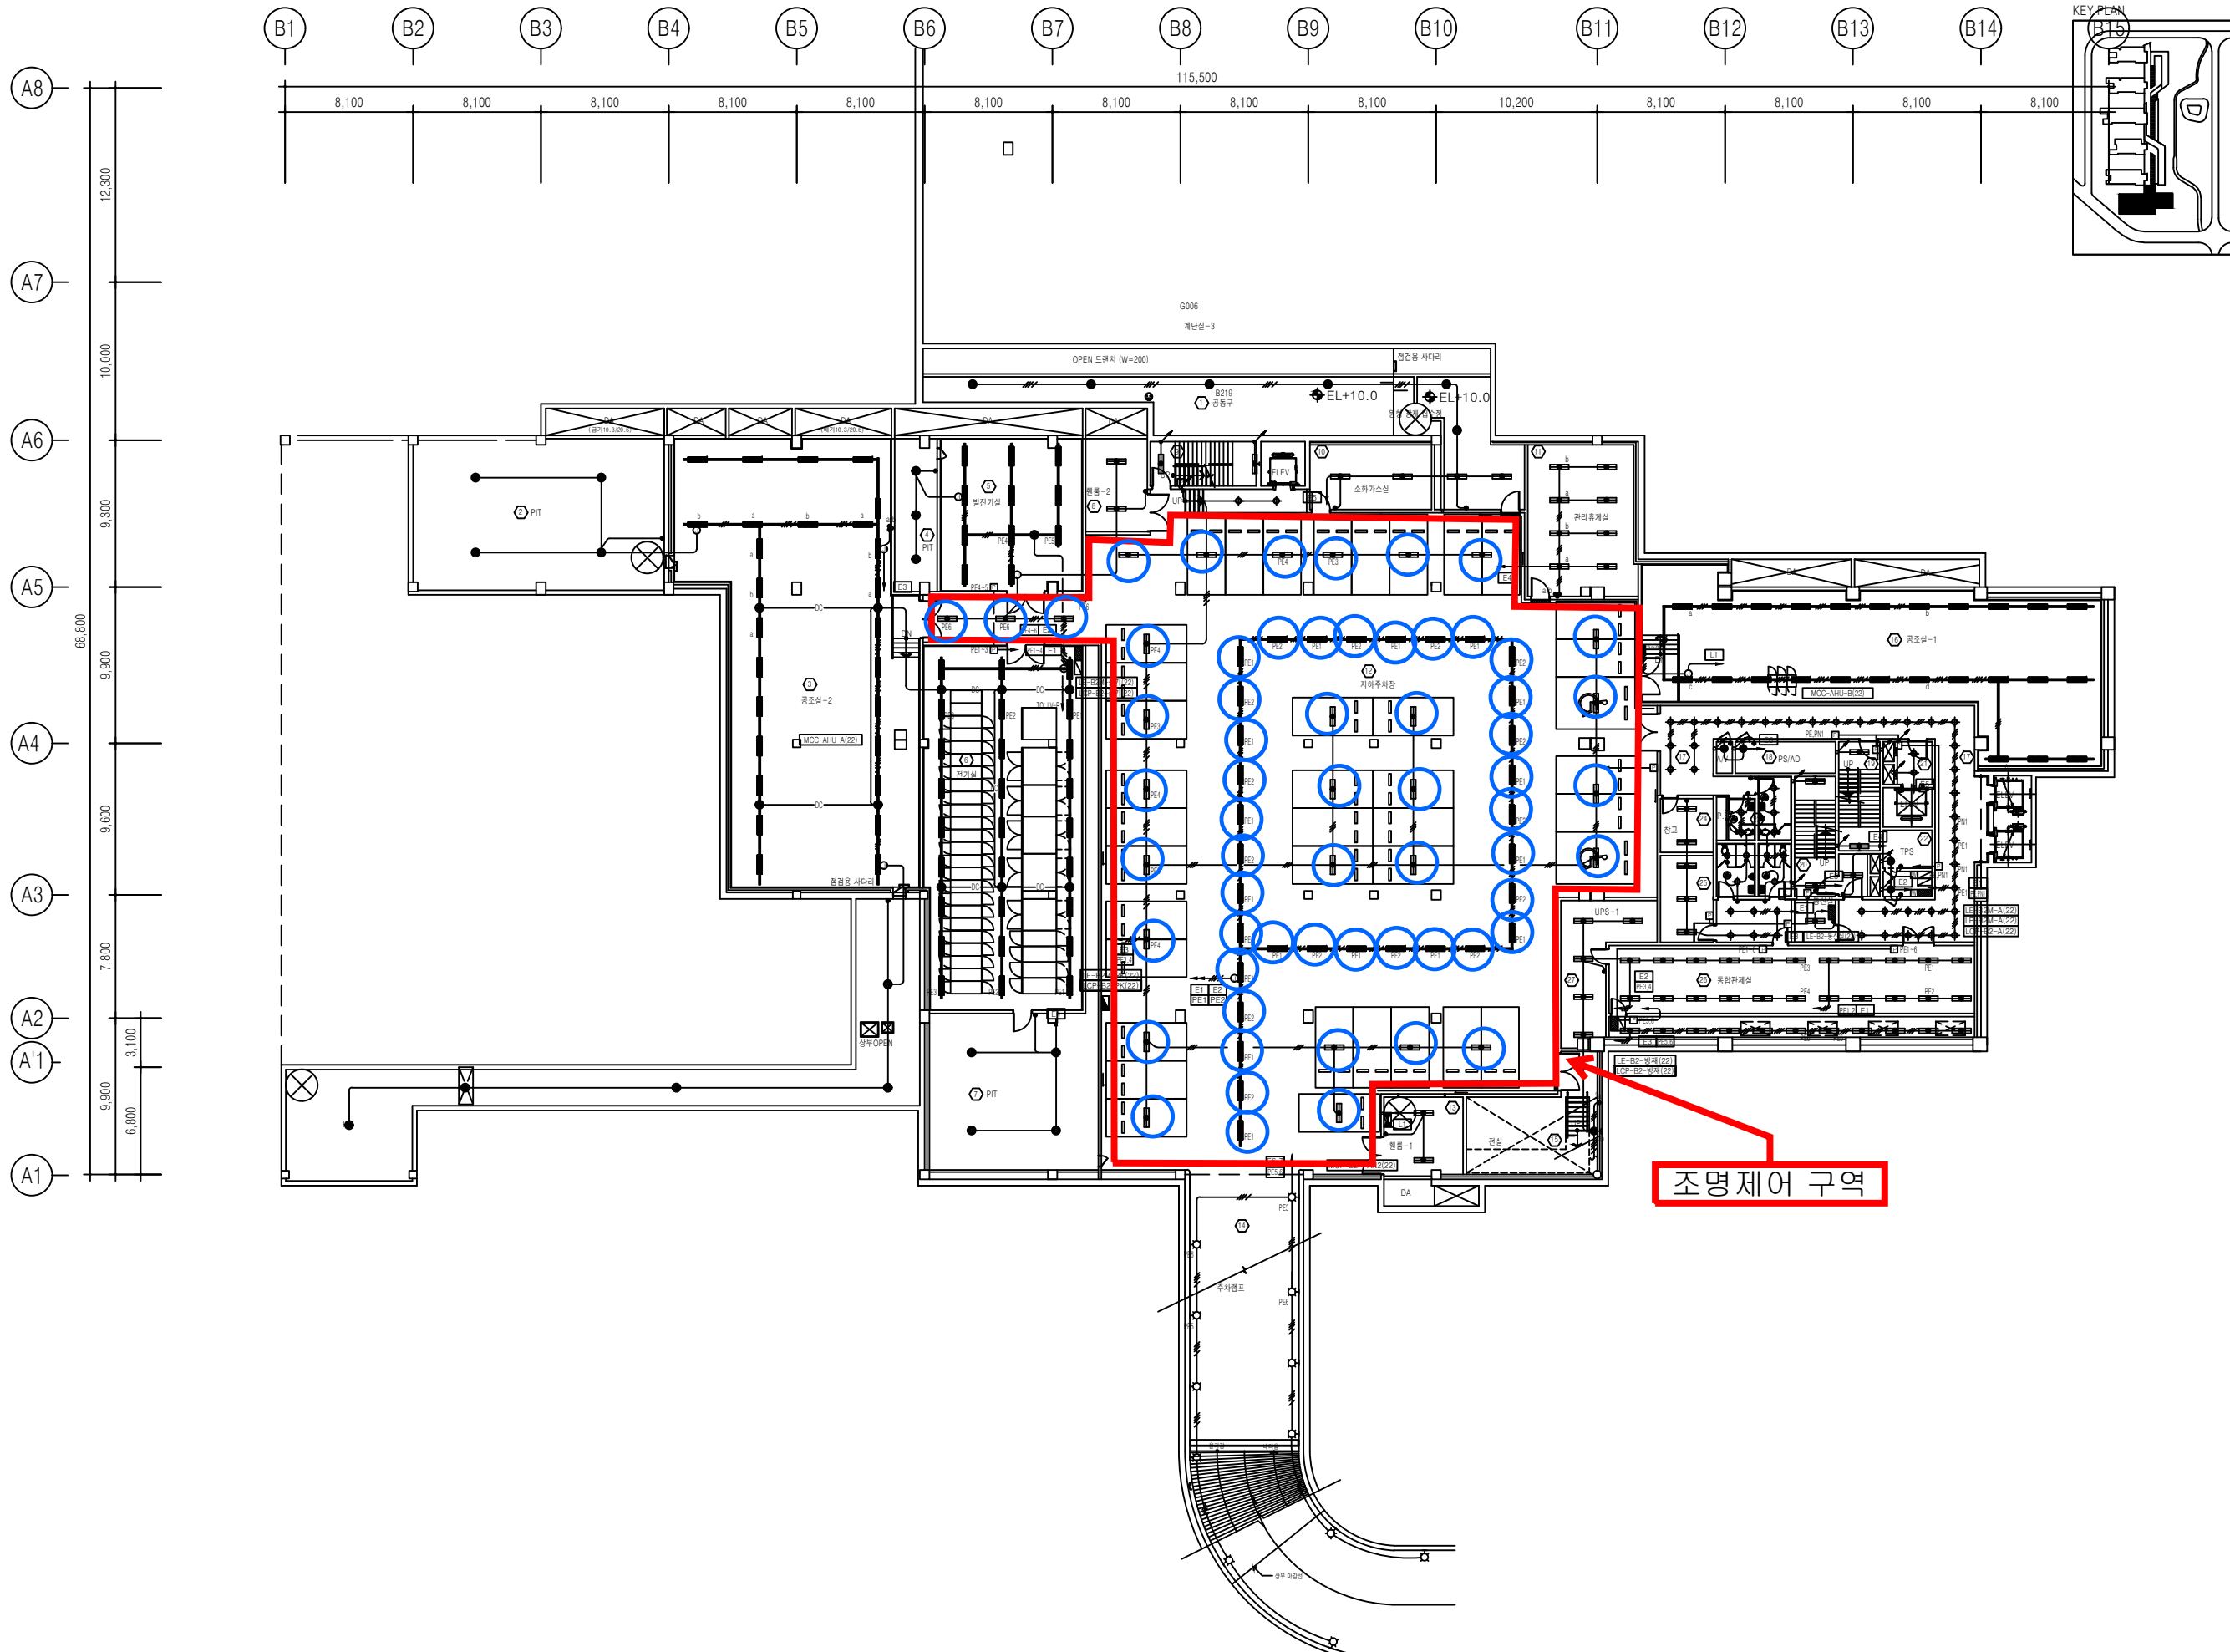


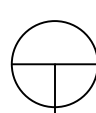


컨퍼런스 및 통합행정지원센터 지하1층 전등설비 평면도
 축척 A1: 1/200, A3: 1/400

3					
2					
1	14.12.08	실명/호실 수정			
REV	DATE	DESCRIPTION	DRN	CHK	APR

DRAWING TITLE
 컨퍼런스 및 통합행정지원센터
 지하1층 전등설비 평면도

APPROVED

CHECKED1

CHECKED2

DRAWN

PROJECT NO.

SCALE

APPROVAL DATE

1/200 1/400 2014.04

DRAWING NO.

E-22-0701

REV.