
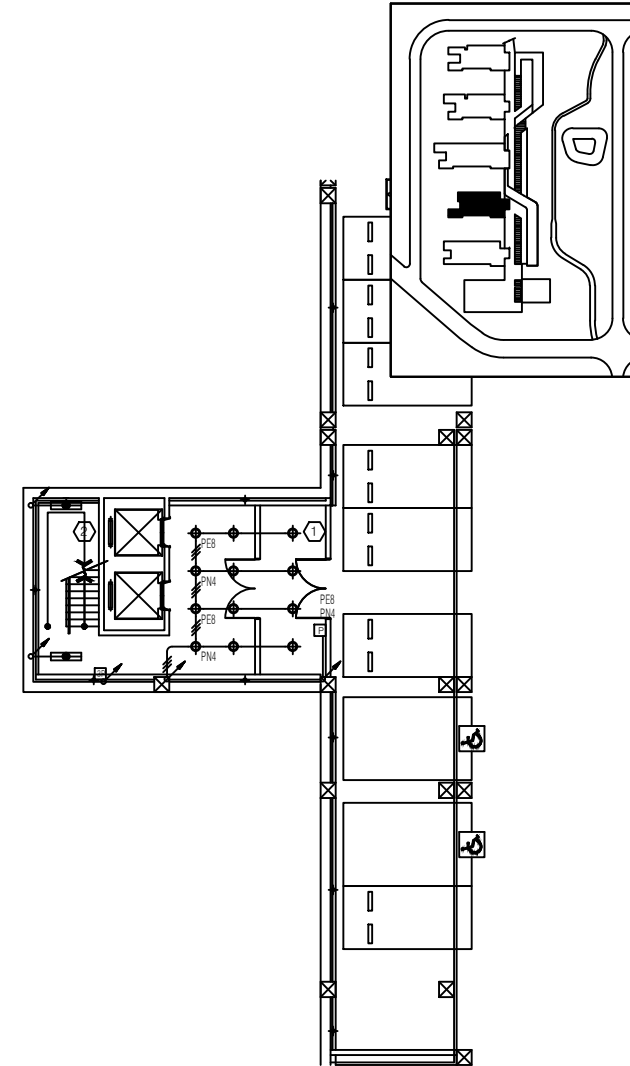
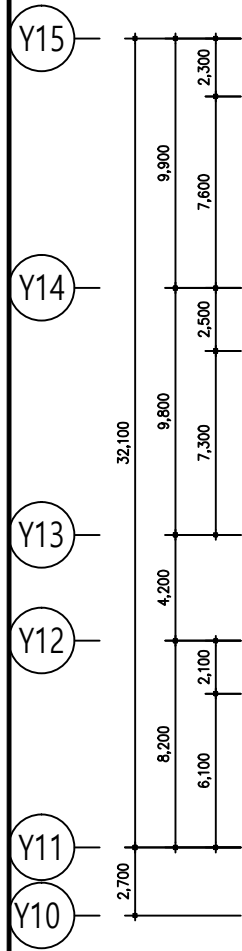


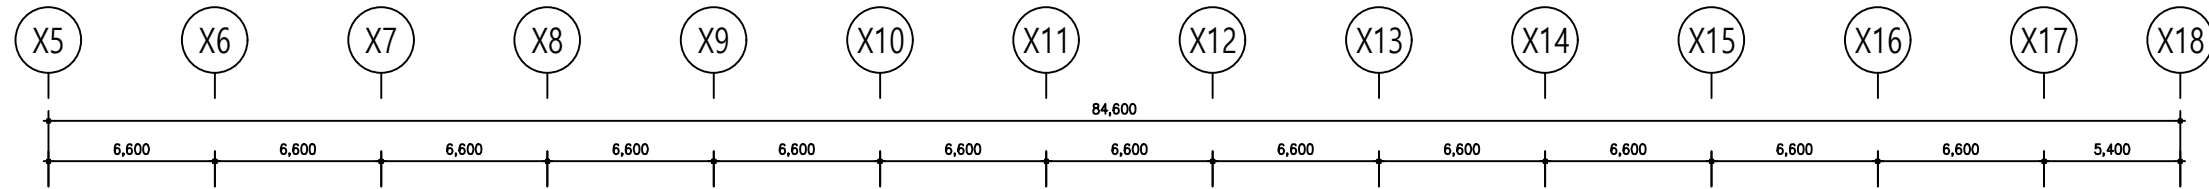

|     |          |             |     |     |     |
|-----|----------|-------------|-----|-----|-----|
| 3   |          |             |     |     |     |
| 2   |          |             |     |     |     |
| 1   | 14.11.19 | 실명/호실 수정    |     |     |     |
| REV | DATE     | DESCRIPTION | DRN | CHK | APR |

DRAWING TITLE

정보통신융합공학부  
지하1층 전등설비 평면도

APPROVED

CHECKED1


CHECKED2

DRAWN

PROJECT NO.

|                   |               |
|-------------------|---------------|
| SCALE             | APPROVAL DATE |
| A1 1/150 A3 1/300 | 2014.04       |






|             |      |
|-------------|------|
| DRAWING NO. | REV. |
| E-12-0701   |      |

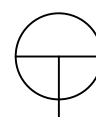

정보통신융합공학부 지하1층 전등설비 평면도

축척 A1: 1/150, A3: 1/300



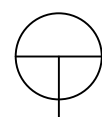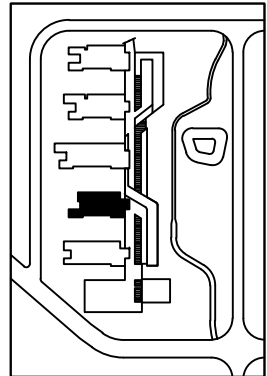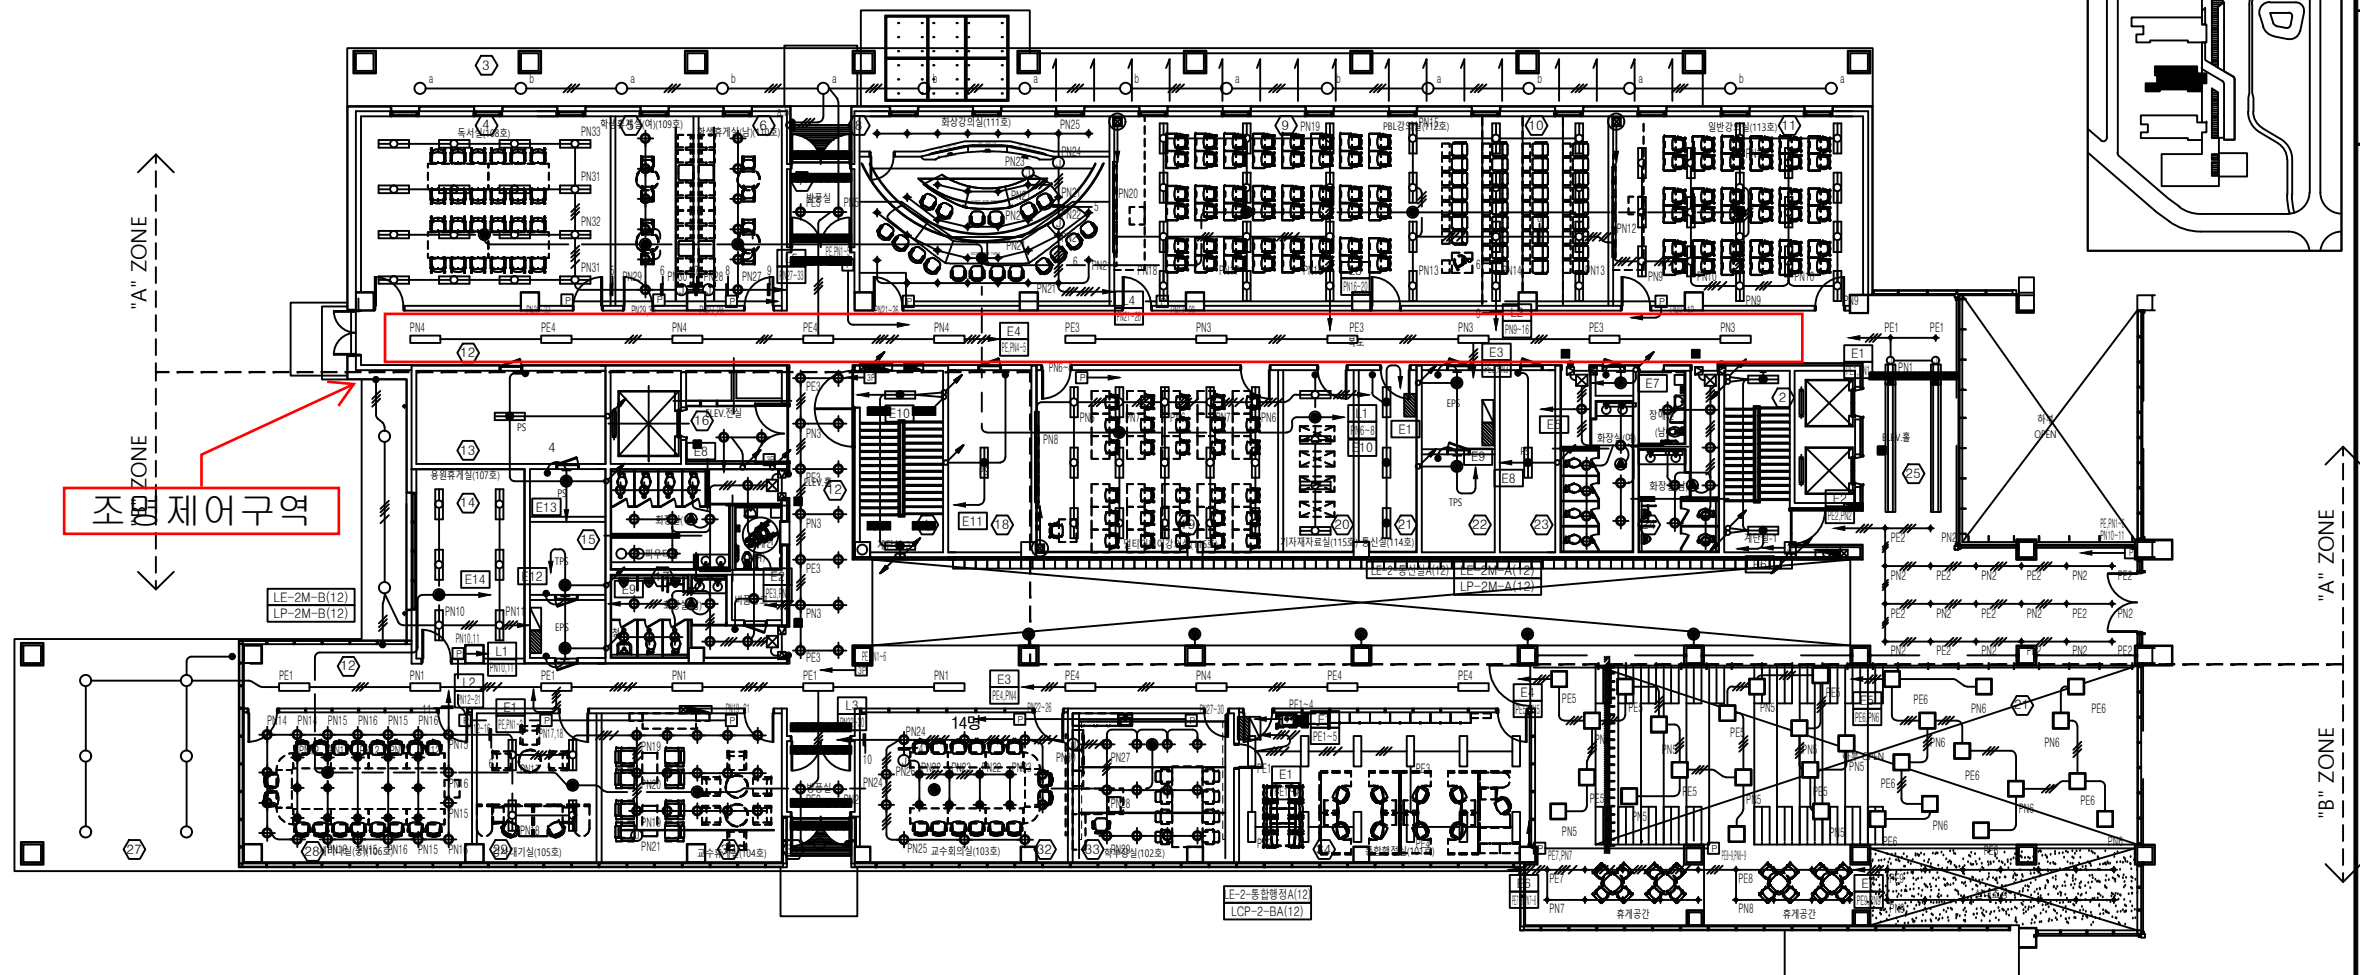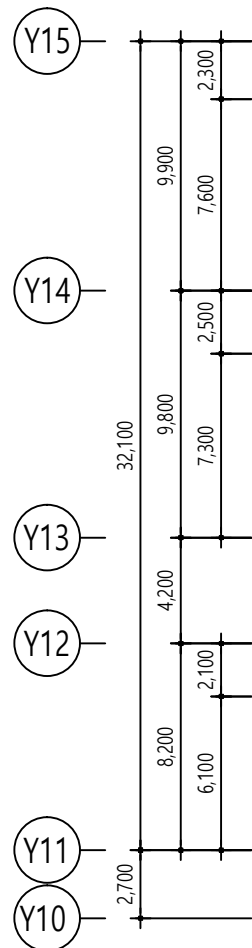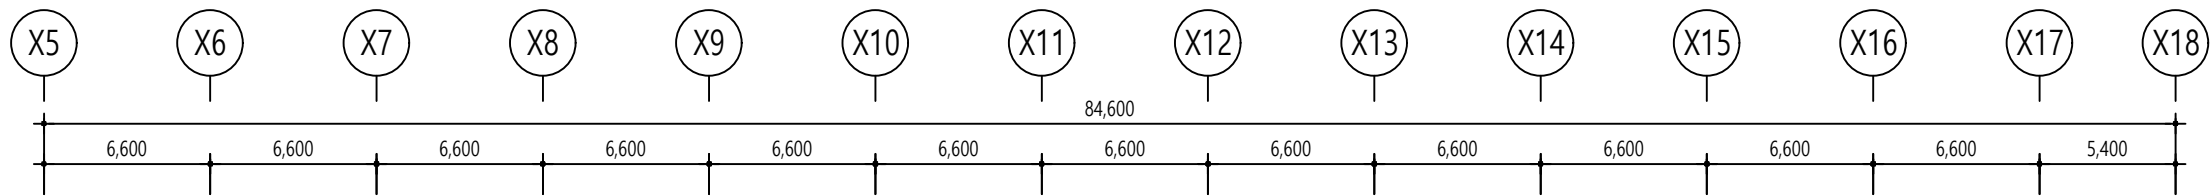

정보통신융합공학부 1층 전등설비 평면도

축척 A1: 1/150, A3: 1/300

| 3   |          |             |     |     |     |
|-----|----------|-------------|-----|-----|-----|
| 2   |          |             |     |     |     |
| 1   | 14.11.19 | 실명/호실 수정    |     |     |     |
| REV | DATE     | DESCRIPTION | DRN | CHK | APR |

DRAWING TITLE

정보통신융합공학부  
1층 전등설비 평면도

APPROVED

CHECKED1

CHECKED2

DRAWN

PROJECT NO.

SCALE

A1

1/150

A3

1/300






APPROVAL DATE

2014.04

DRAWING NO.

E-12-0703






REV.

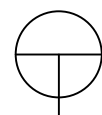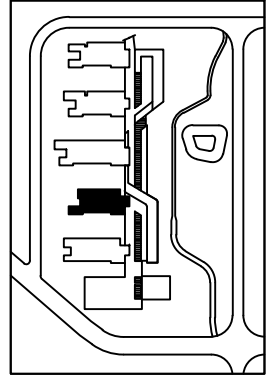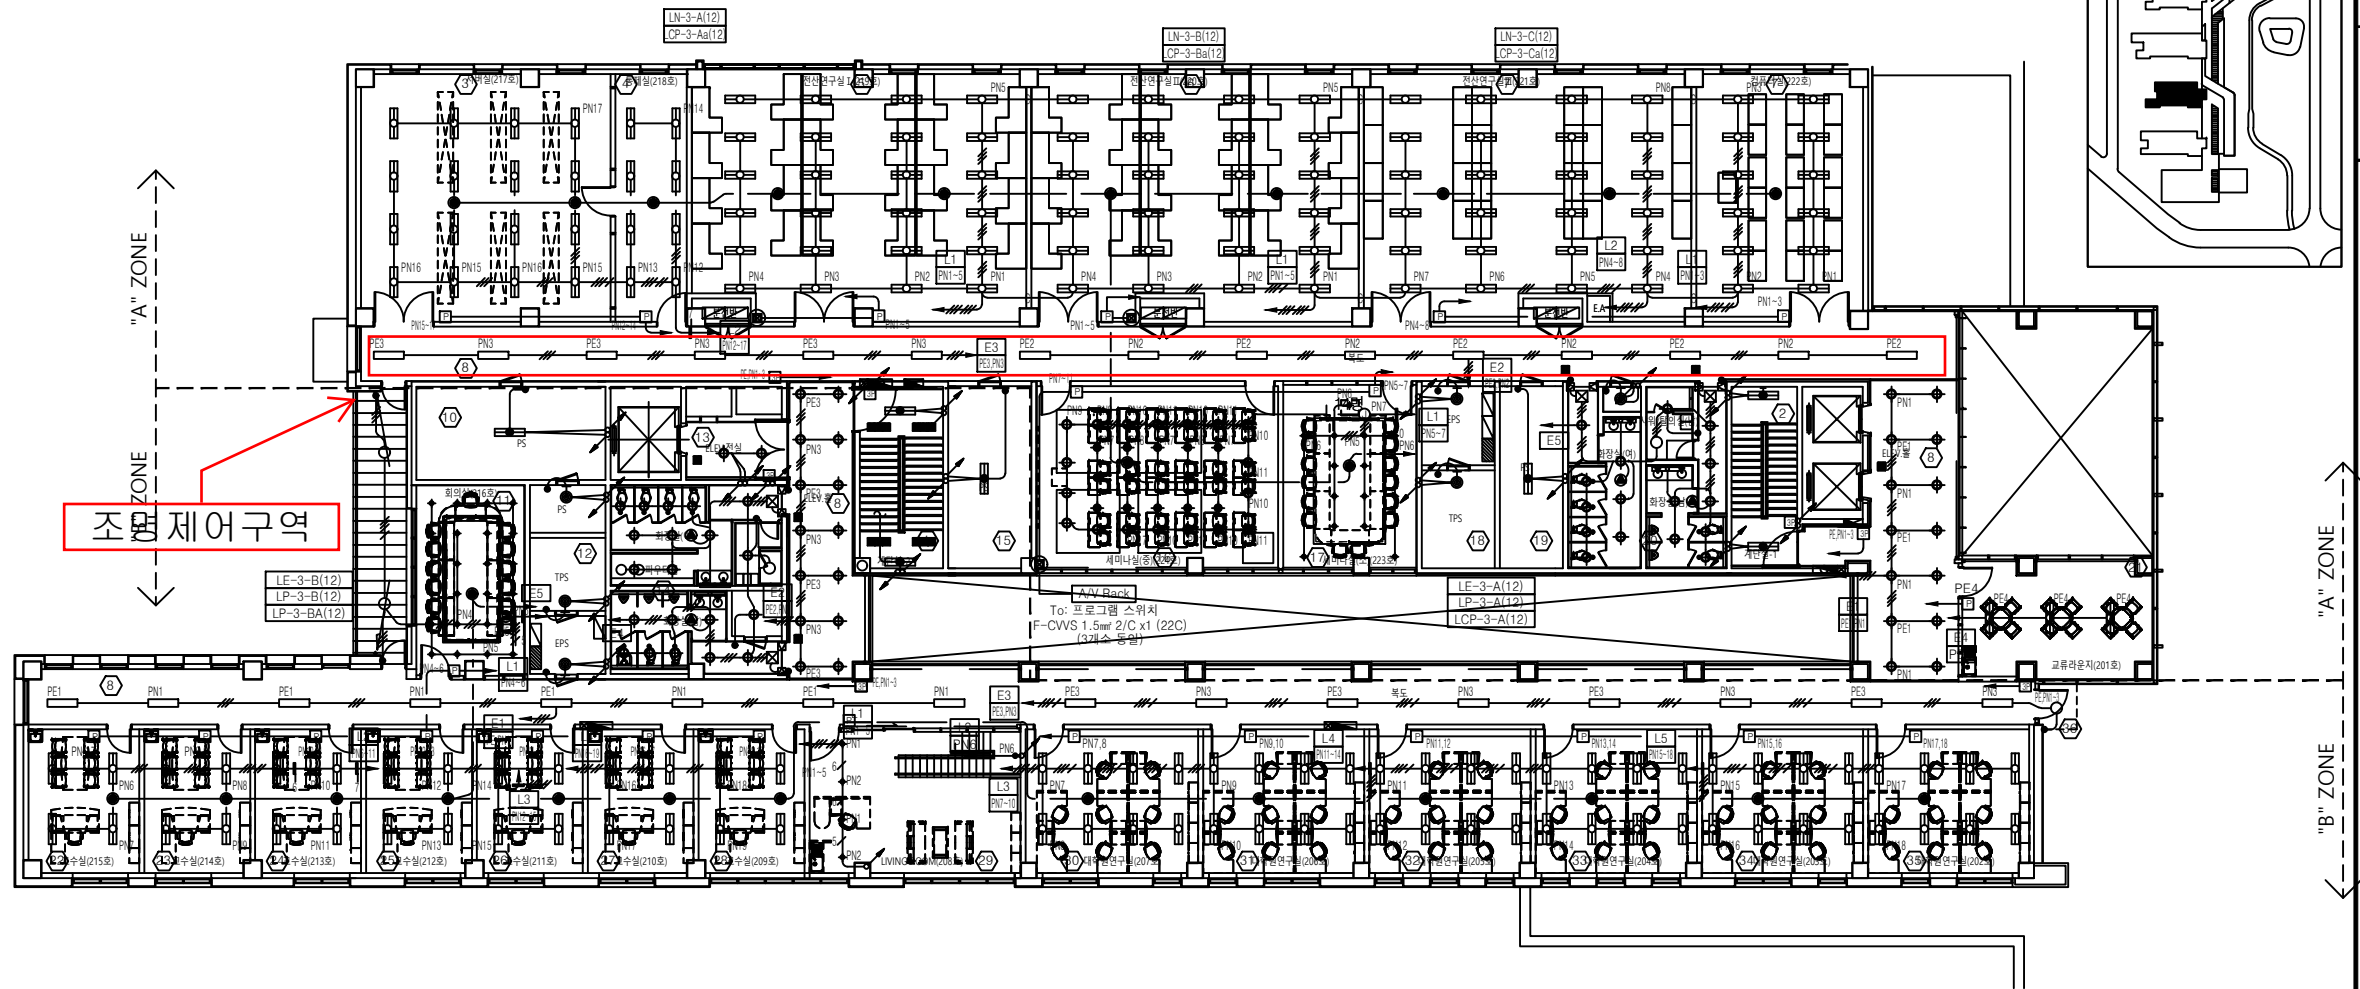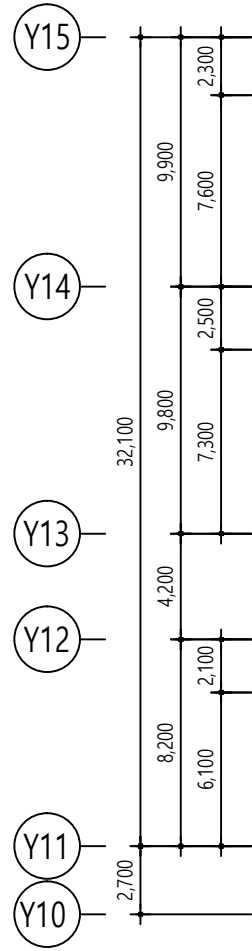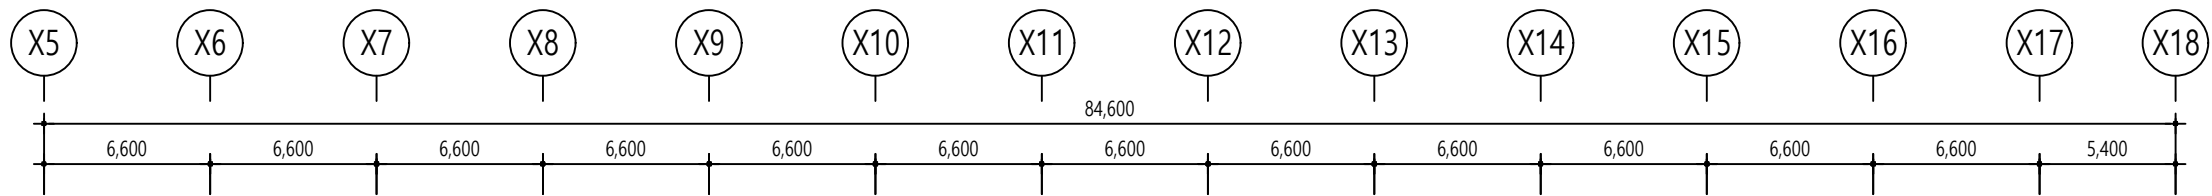

정보통신융합공학부 2층 전등설비 평면도

축척 A1: 1/150, A3: 1/300

| 3                        |          |             |               |         |      |
|--------------------------|----------|-------------|---------------|---------|------|
| 2                        |          |             |               |         |      |
| 1                        | 14.11.19 | 실명/호실 수정    |               |         |      |
| REV                      | DATE     | DESCRIPTION | DRN           | CHK     | APR  |
| DRAWING TITLE            |          |             |               |         |      |
| 정보통신융합공학부<br>2층 전등설비 평면도 |          |             |               |         |      |
| APPROVED                 |          |             |               |         |      |
| CHECKED1                 |          |             |               |         |      |
| CHECKED2                 |          |             |               |         |      |
| DRAWN                    |          |             |               |         |      |
| PROJECT NO.              |          |             |               |         |      |
| SCALE                    |          |             | APPROVAL DATE |         |      |
| A1                       | 1/150    | A3          | 1/300         | 2014.04 |      |
| DRAWING NO.              |          |             |               |         | REV. |
| E-12-0704                |          |             |               |         |      |

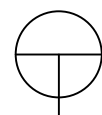
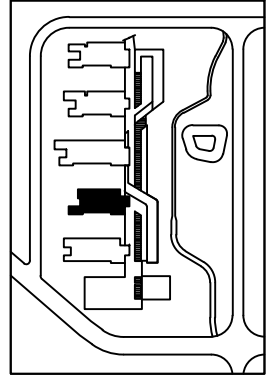
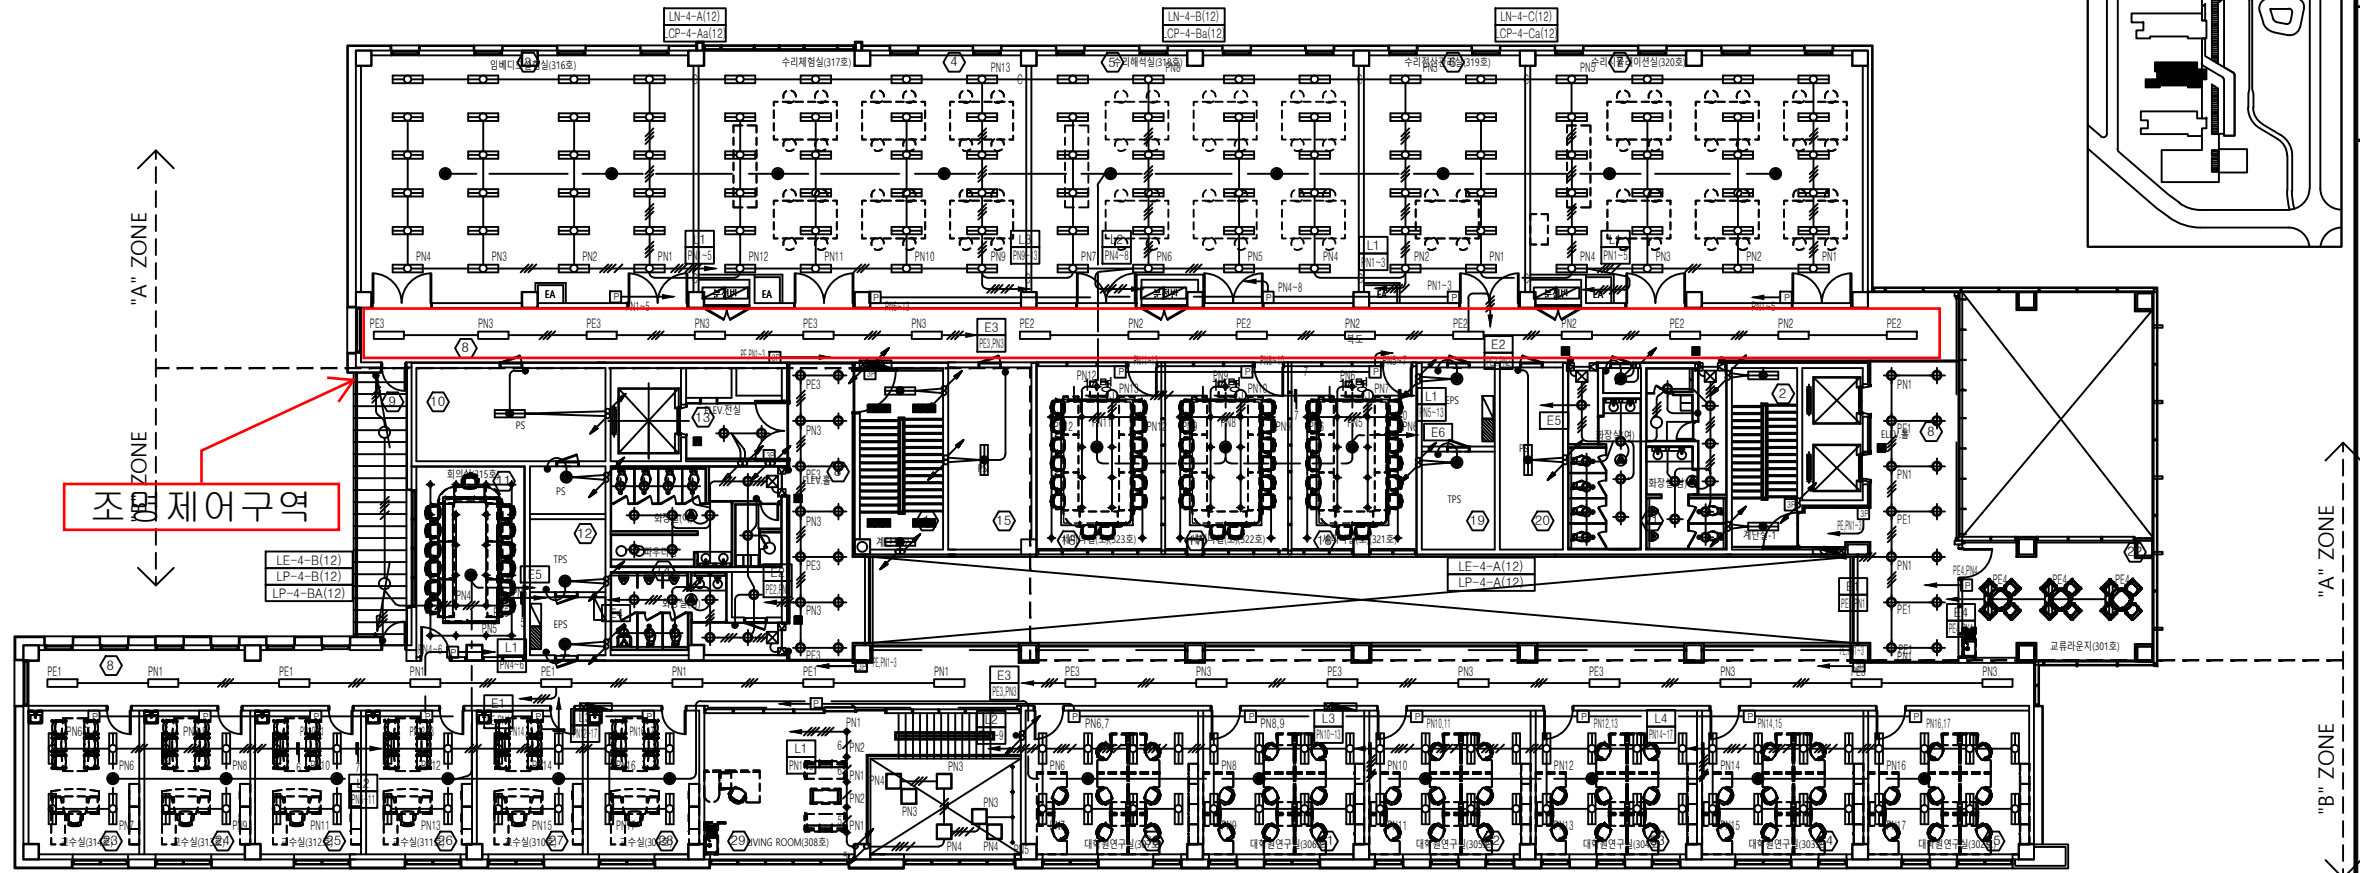
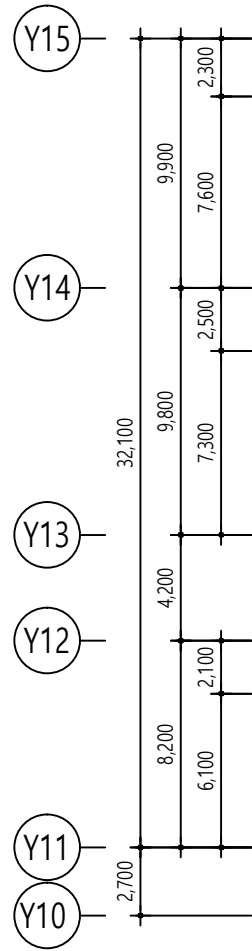
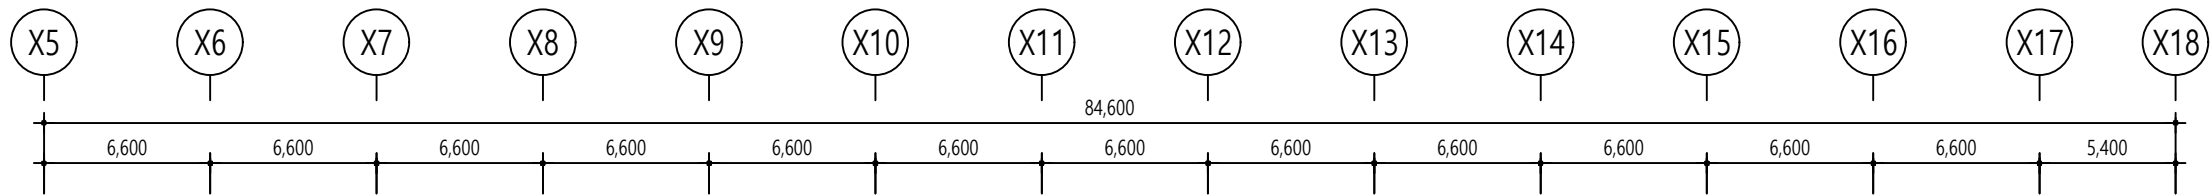


정보통신융합공학부 3층 전등설비 평면도

축척 A1: 1/150, A3: 1/300

| 3                        |          |             |               |         |      |
|--------------------------|----------|-------------|---------------|---------|------|
| 2                        |          |             |               |         |      |
| 1                        | 14.11.19 | 실명/호실 수정    |               |         |      |
| REV                      | DATE     | DESCRIPTION | DRN           | CHK     | APR  |
| DRAWING TITLE            |          |             |               |         |      |
| 정보통신융합공학부<br>3층 전등설비 평면도 |          |             |               |         |      |
| APPROVED                 |          |             |               |         |      |
| CHECKED1                 |          |             |               |         |      |
| CHECKED2                 |          |             |               |         |      |
| DRAWN                    |          |             |               |         |      |
| PROJECT NO.              |          |             |               |         |      |
| SCALE                    |          |             | APPROVAL DATE |         |      |
| A1                       | 1/150    | A3          | 1/300         | 2014.04 |      |
| DRAWING NO.              |          |             |               |         | REV. |
| E-12-0705                |          |             |               |         |      |








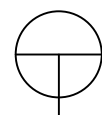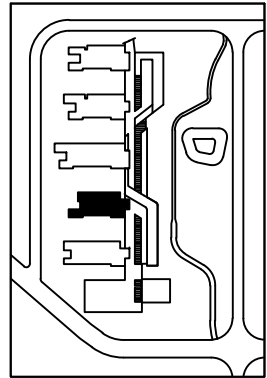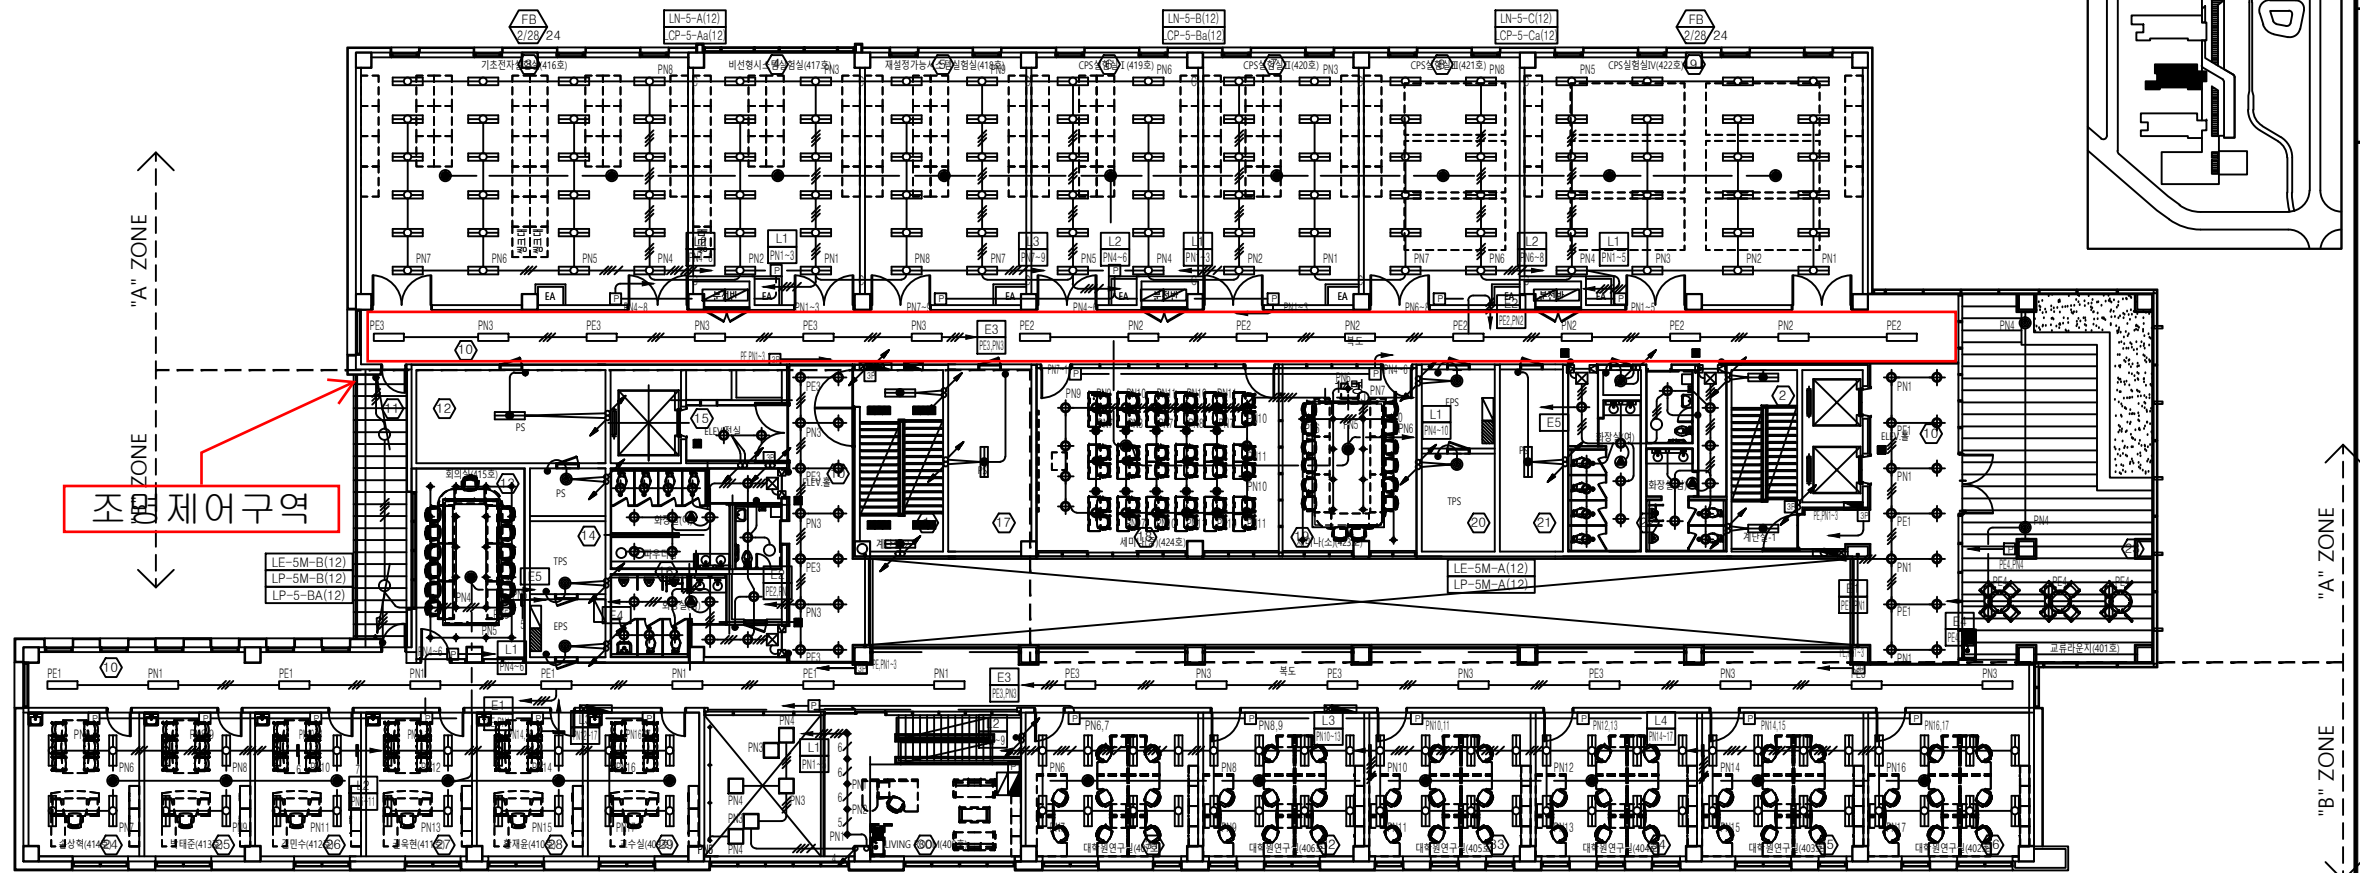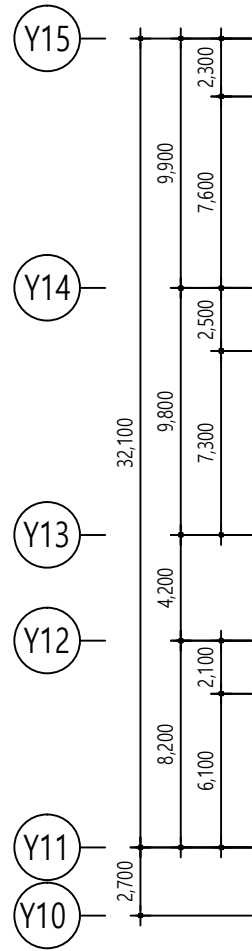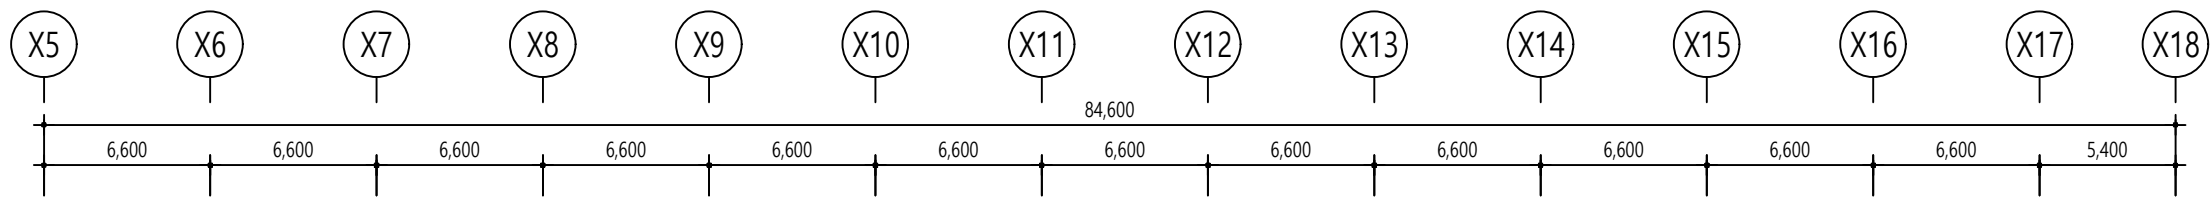

정보통신융합공학부 4층 전등설비 평면도

축척 A1: 1/150, A3: 1/300






| 3                        |          |             |               |         |      |
|--------------------------|----------|-------------|---------------|---------|------|
| 2                        |          |             |               |         |      |
| 1                        | 14.11.19 | 실명/호실 수정    |               |         |      |
| REV                      | DATE     | DESCRIPTION | DRN           | CHK     | APR  |
| DRAWING TITLE            |          |             |               |         |      |
| 정보통신융합공학부<br>4층 전등설비 평면도 |          |             |               |         |      |
| APPROVED                 |          |             |               |         |      |
| CHECKED1                 |          |             |               |         |      |
| CHECKED2                 |          |             |               |         |      |
| DRAWN                    |          |             |               |         |      |
| PROJECT NO.              |          |             |               |         |      |
| SCALE                    |          |             | APPROVAL DATE |         |      |
| A1                       | 1/150    | A3          | 1/300         | 2014.04 |      |
| DRAWING NO.              |          |             |               |         | REV. |
| E-12-0706                |          |             |               |         |      |

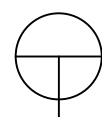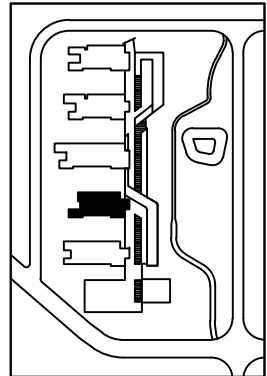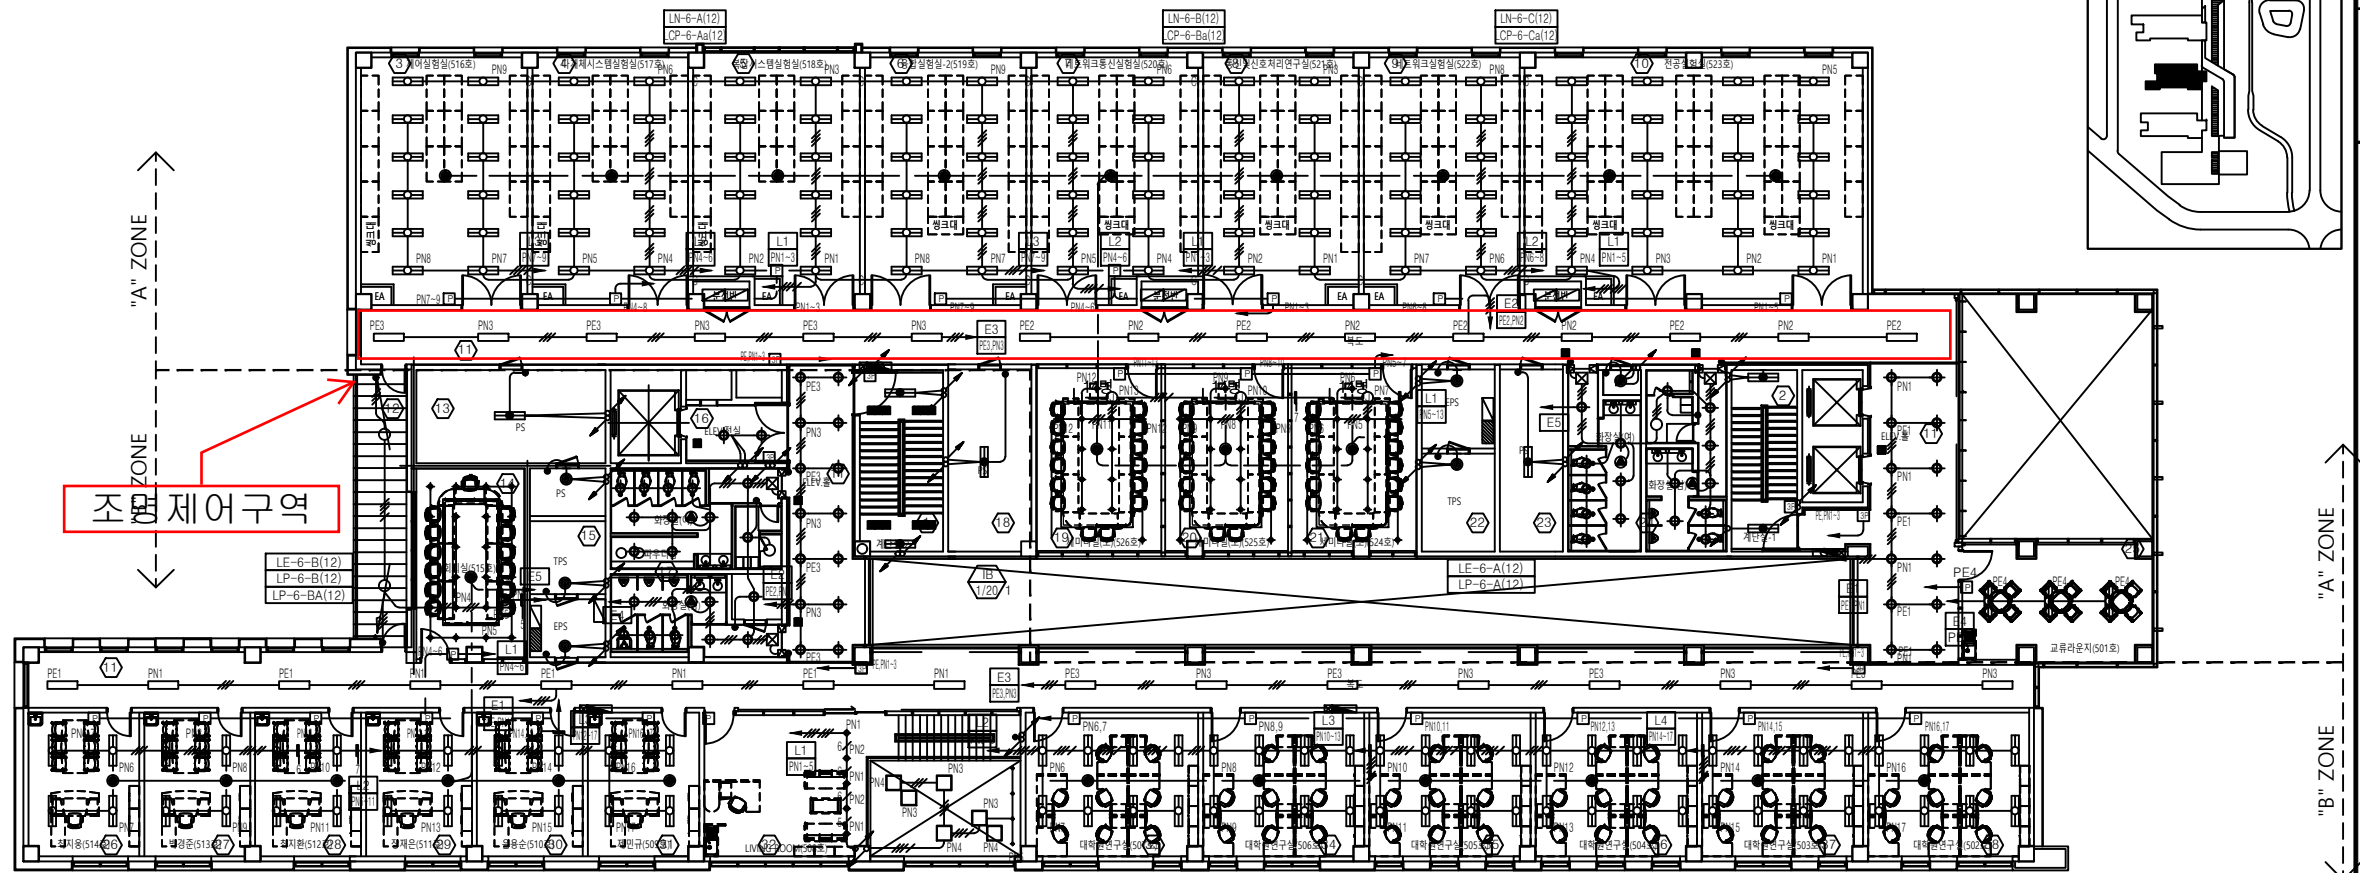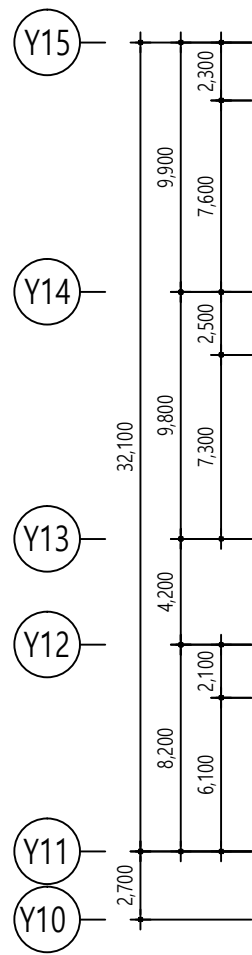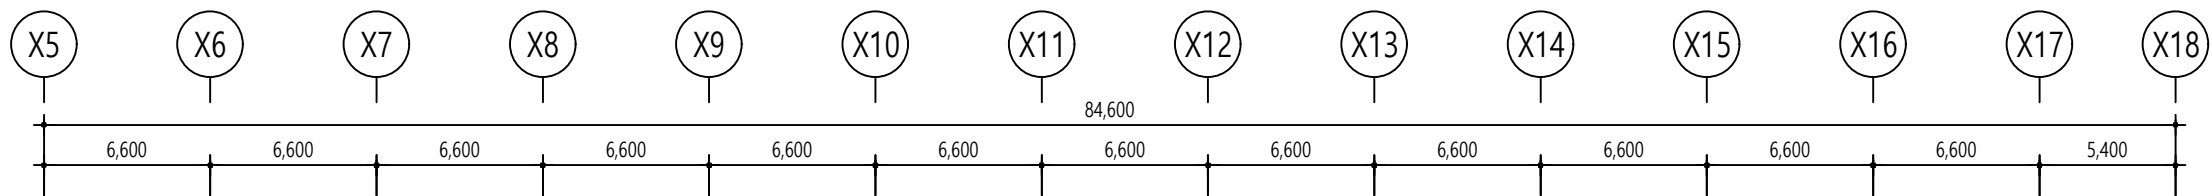

정보통신융합공학부 5층 전등설비 평면도

축척 A1: 1/150, A3: 1/300

| 3                        |          |             |               |         |      |
|--------------------------|----------|-------------|---------------|---------|------|
| 2                        |          |             |               |         |      |
| 1                        | 14.11.19 | 실명/호실 수정    |               |         |      |
| REV                      | DATE     | DESCRIPTION | DRN           | CHK     | APR  |
| DRAWING TITLE            |          |             |               |         |      |
| 정보통신융합공학부<br>5층 전등설비 평면도 |          |             |               |         |      |
| APPROVED                 |          |             |               |         |      |
| CHECKED1                 |          |             |               |         |      |
| CHECKED2                 |          |             |               |         |      |
| DRAWN                    |          |             |               |         |      |
| PROJECT NO.              |          |             |               |         |      |
| SCALE                    |          |             | APPROVAL DATE |         |      |
| A1                       | 1/150    | A3          | 1/300         | 2014.04 |      |
| DRAWING NO.              |          |             |               |         | REV. |
| E-12-0707                |          |             |               |         |      |

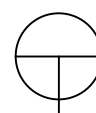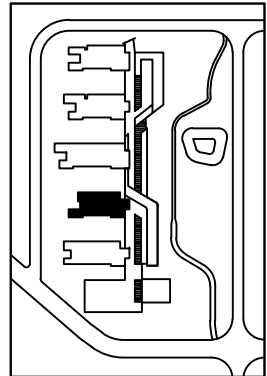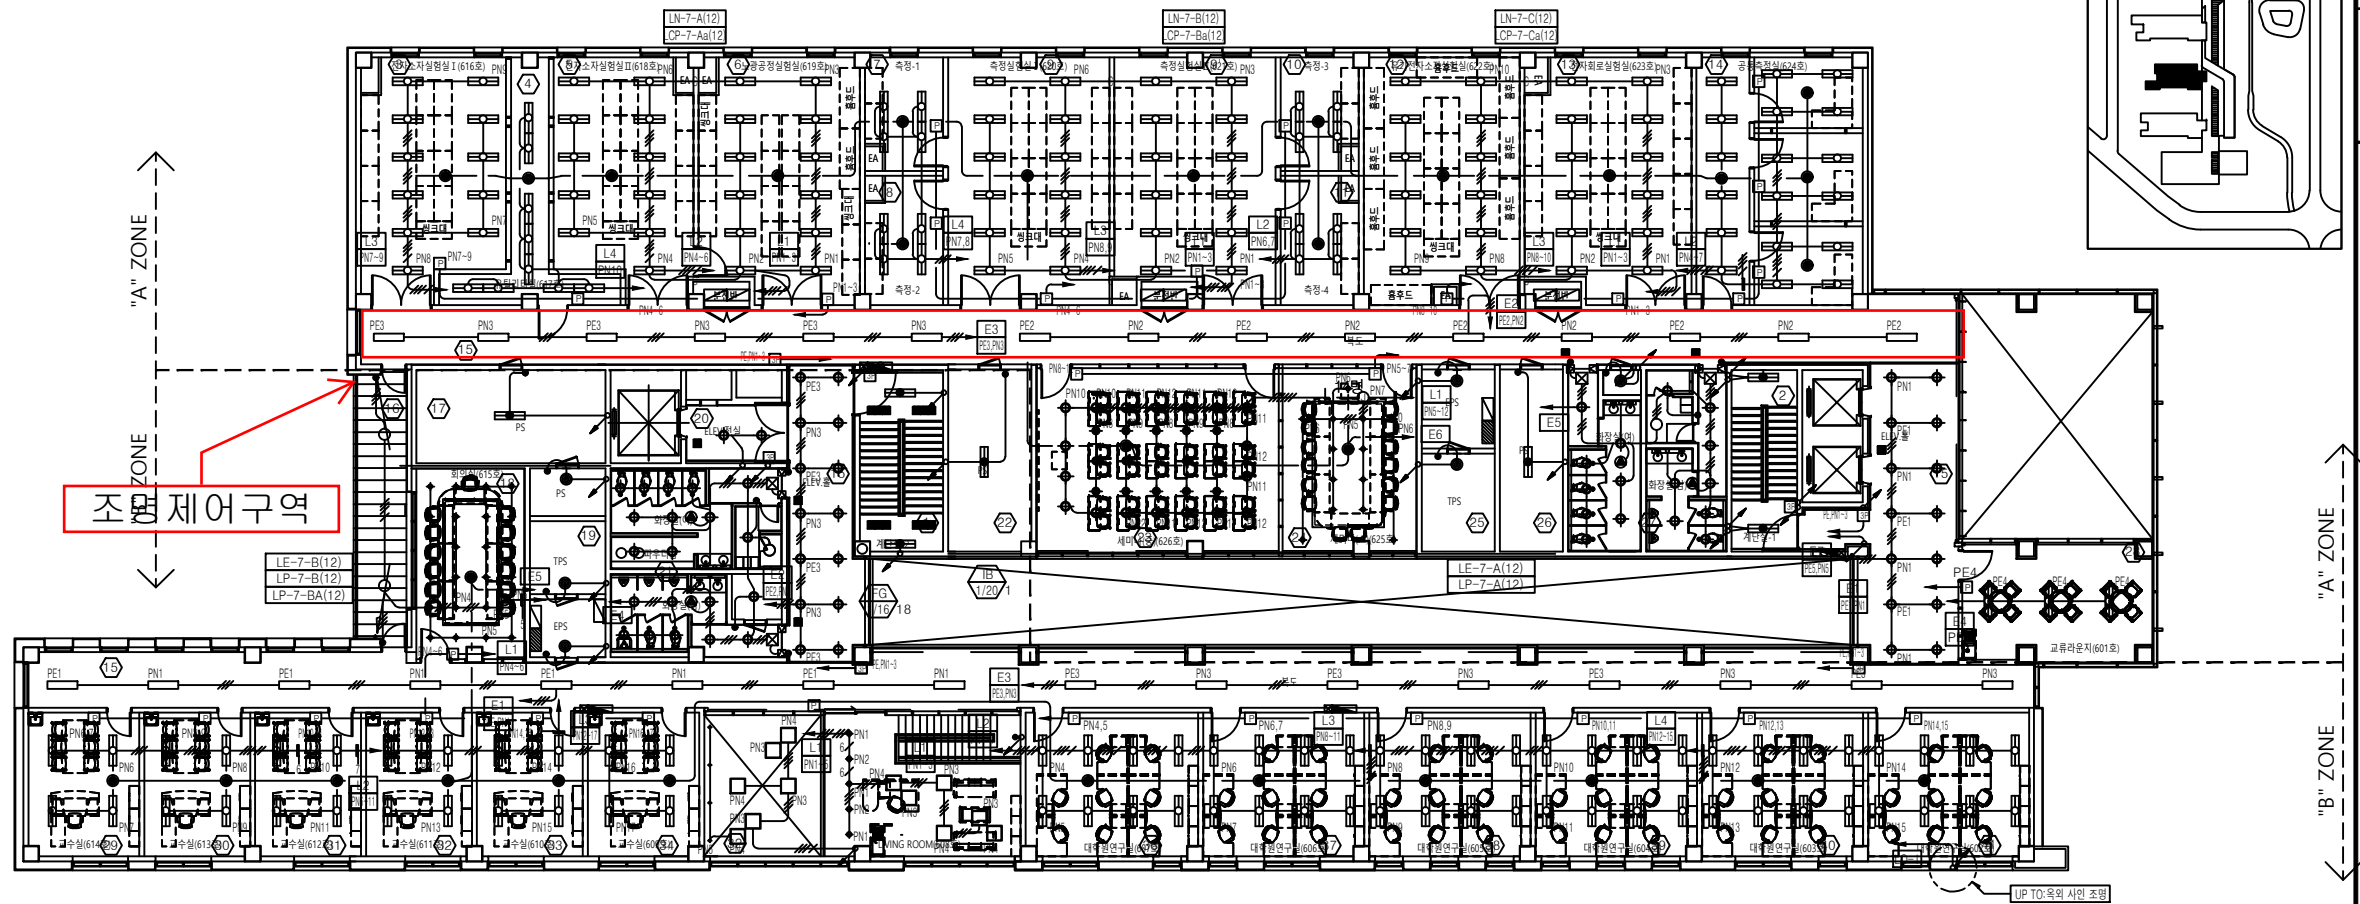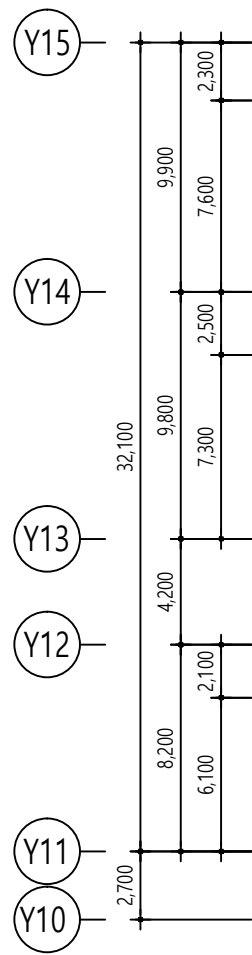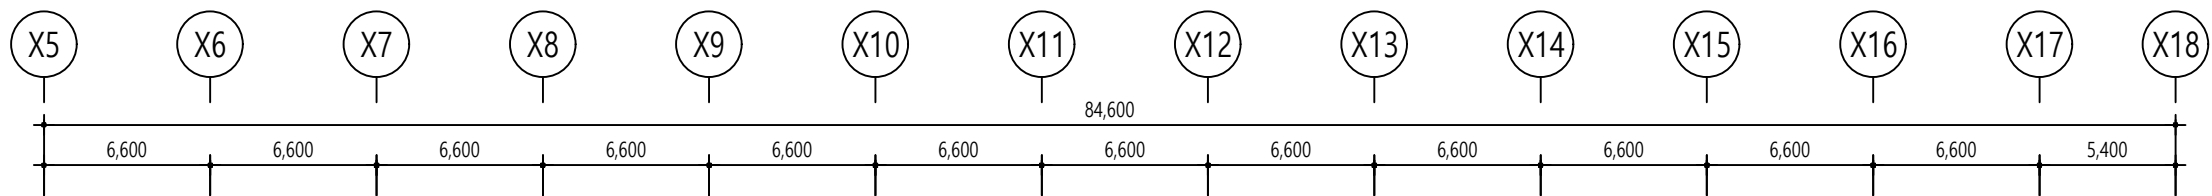

정보통신융합공학부 6층 전등설비 평면도

축척 A1: 1/150, A3: 1/300

| 3                        |          |             |               |         |      |
|--------------------------|----------|-------------|---------------|---------|------|
| 2                        |          |             |               |         |      |
| 1                        | 14.11.19 | 실명/호실 수정    |               |         |      |
| REV                      | DATE     | DESCRIPTION | DRN           | CHK     | APR  |
| DRAWING TITLE            |          |             |               |         |      |
| 정보통신융합공학부<br>6층 전등설비 평면도 |          |             |               |         |      |
| APPROVED                 |          |             |               |         |      |
| CHECKED1                 |          |             |               |         |      |
| CHECKED2                 |          |             |               |         |      |
| DRAWN                    |          |             |               |         |      |
| PROJECT NO.              |          |             |               |         |      |
| SCALE                    |          |             | APPROVAL DATE |         |      |
| A1                       | 1/150    | A3          | 1/300         | 2014.04 |      |
| DRAWING NO.              |          |             |               |         | REV. |
| E-12-0708                |          |             |               |         |      |



