
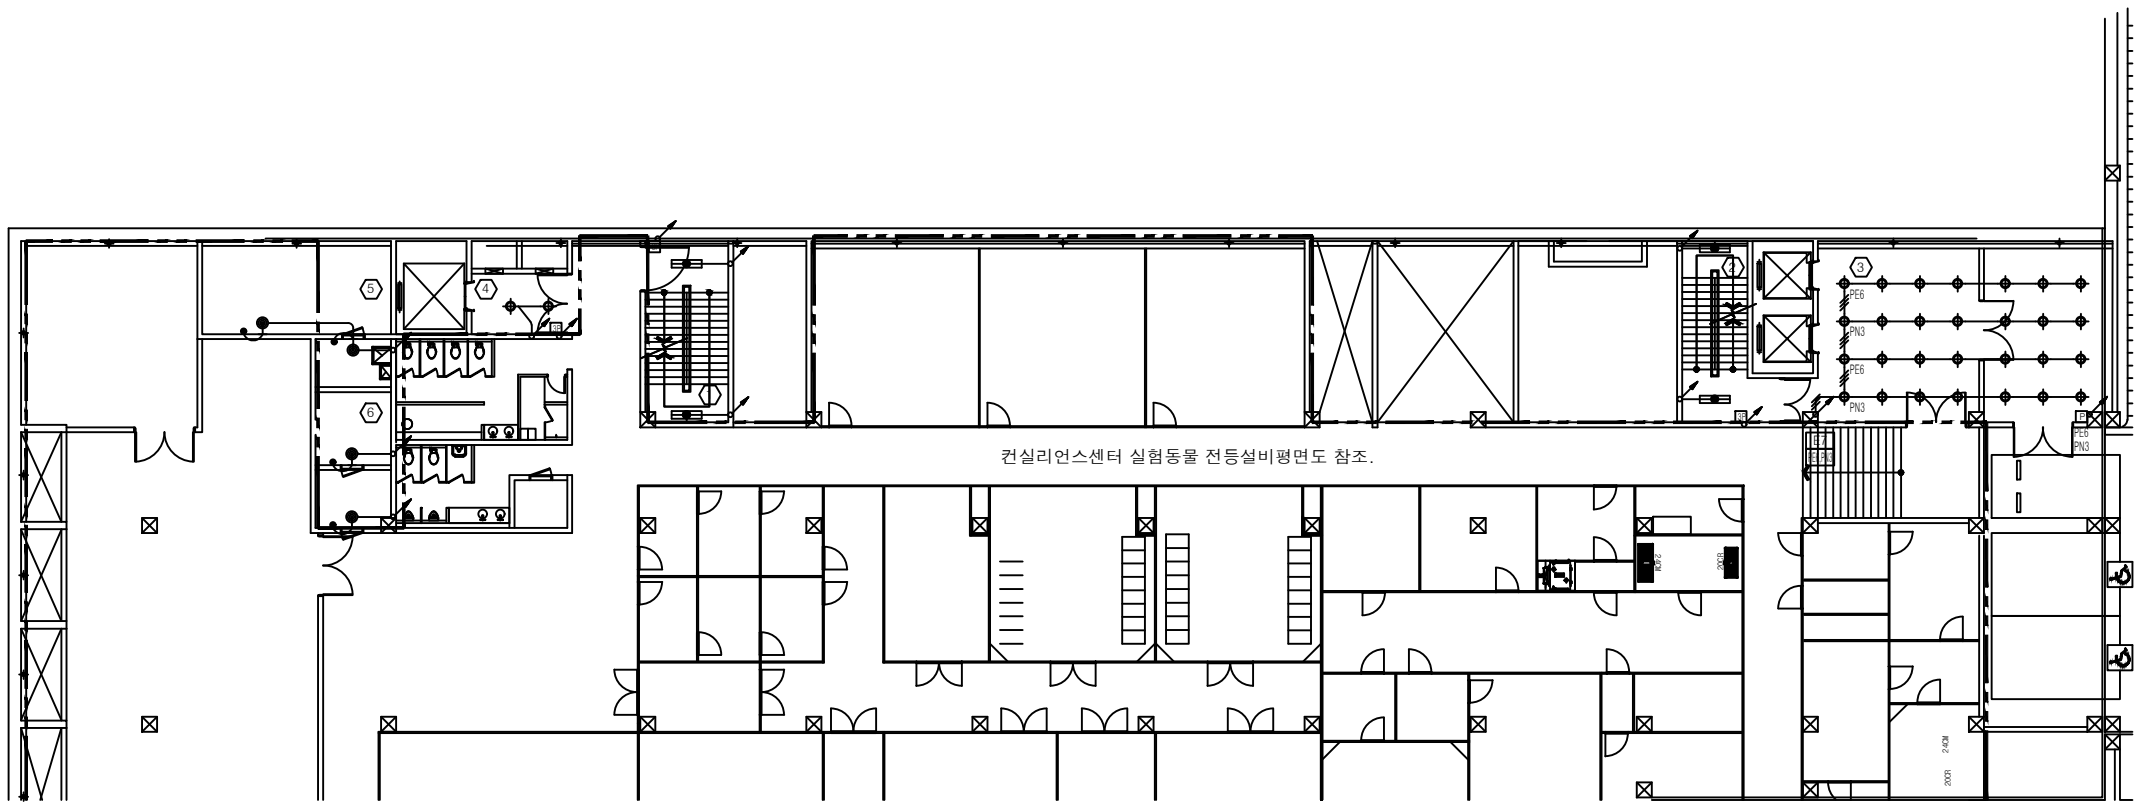
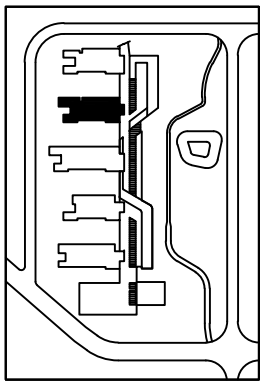
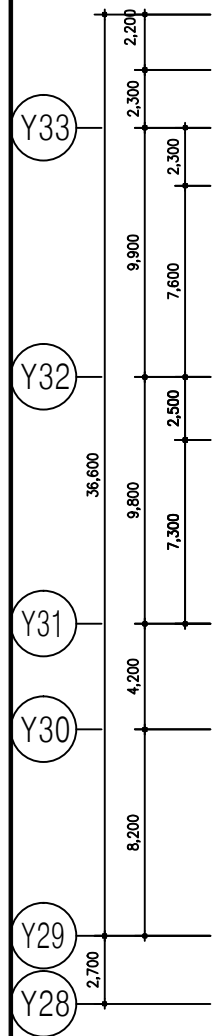


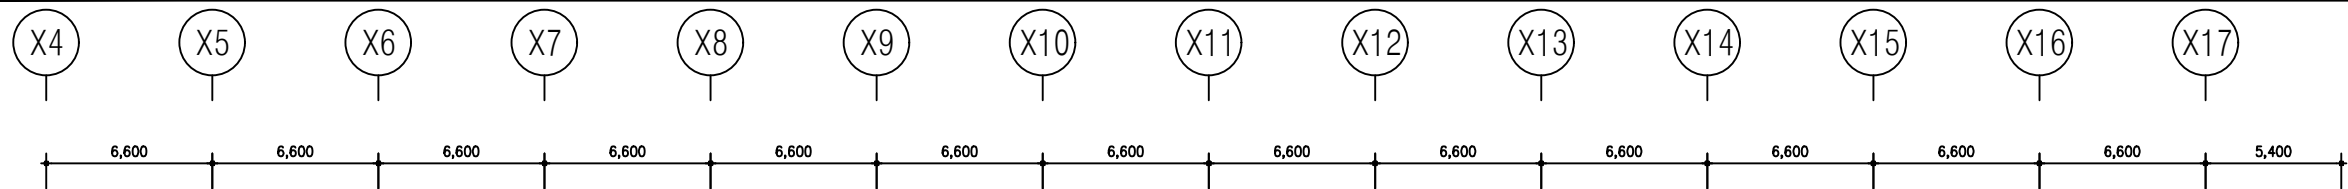

로봇공학부 지하 1층 전등설비 평면도  
축척 A1: 1/150, A3: 1/300

1. 실험실내의 전등설비용 공배관 설치.  
: EMPTY PIPE (CD 22C)

|     |          |             |     |     |     |
|-----|----------|-------------|-----|-----|-----|
| 3   |          |             |     |     |     |
| 2   |          |             |     |     |     |
| 1   | 14.11.18 | 실명/호실 수정    |     |     |     |
| REV | DATE     | DESCRIPTION | DRN | CHK | APR |

DRAWING TITLE

로봇공학부  
지하 1층 전등설비 평면도

APPROVED

CHECKED1

CHECKED2

DRAWN

PROJECT NO.

SCALE

A1 1/150 A3 1/300

APPROVAL DATE



2014.04

DRAWING NO.

E-14-0701



REV.



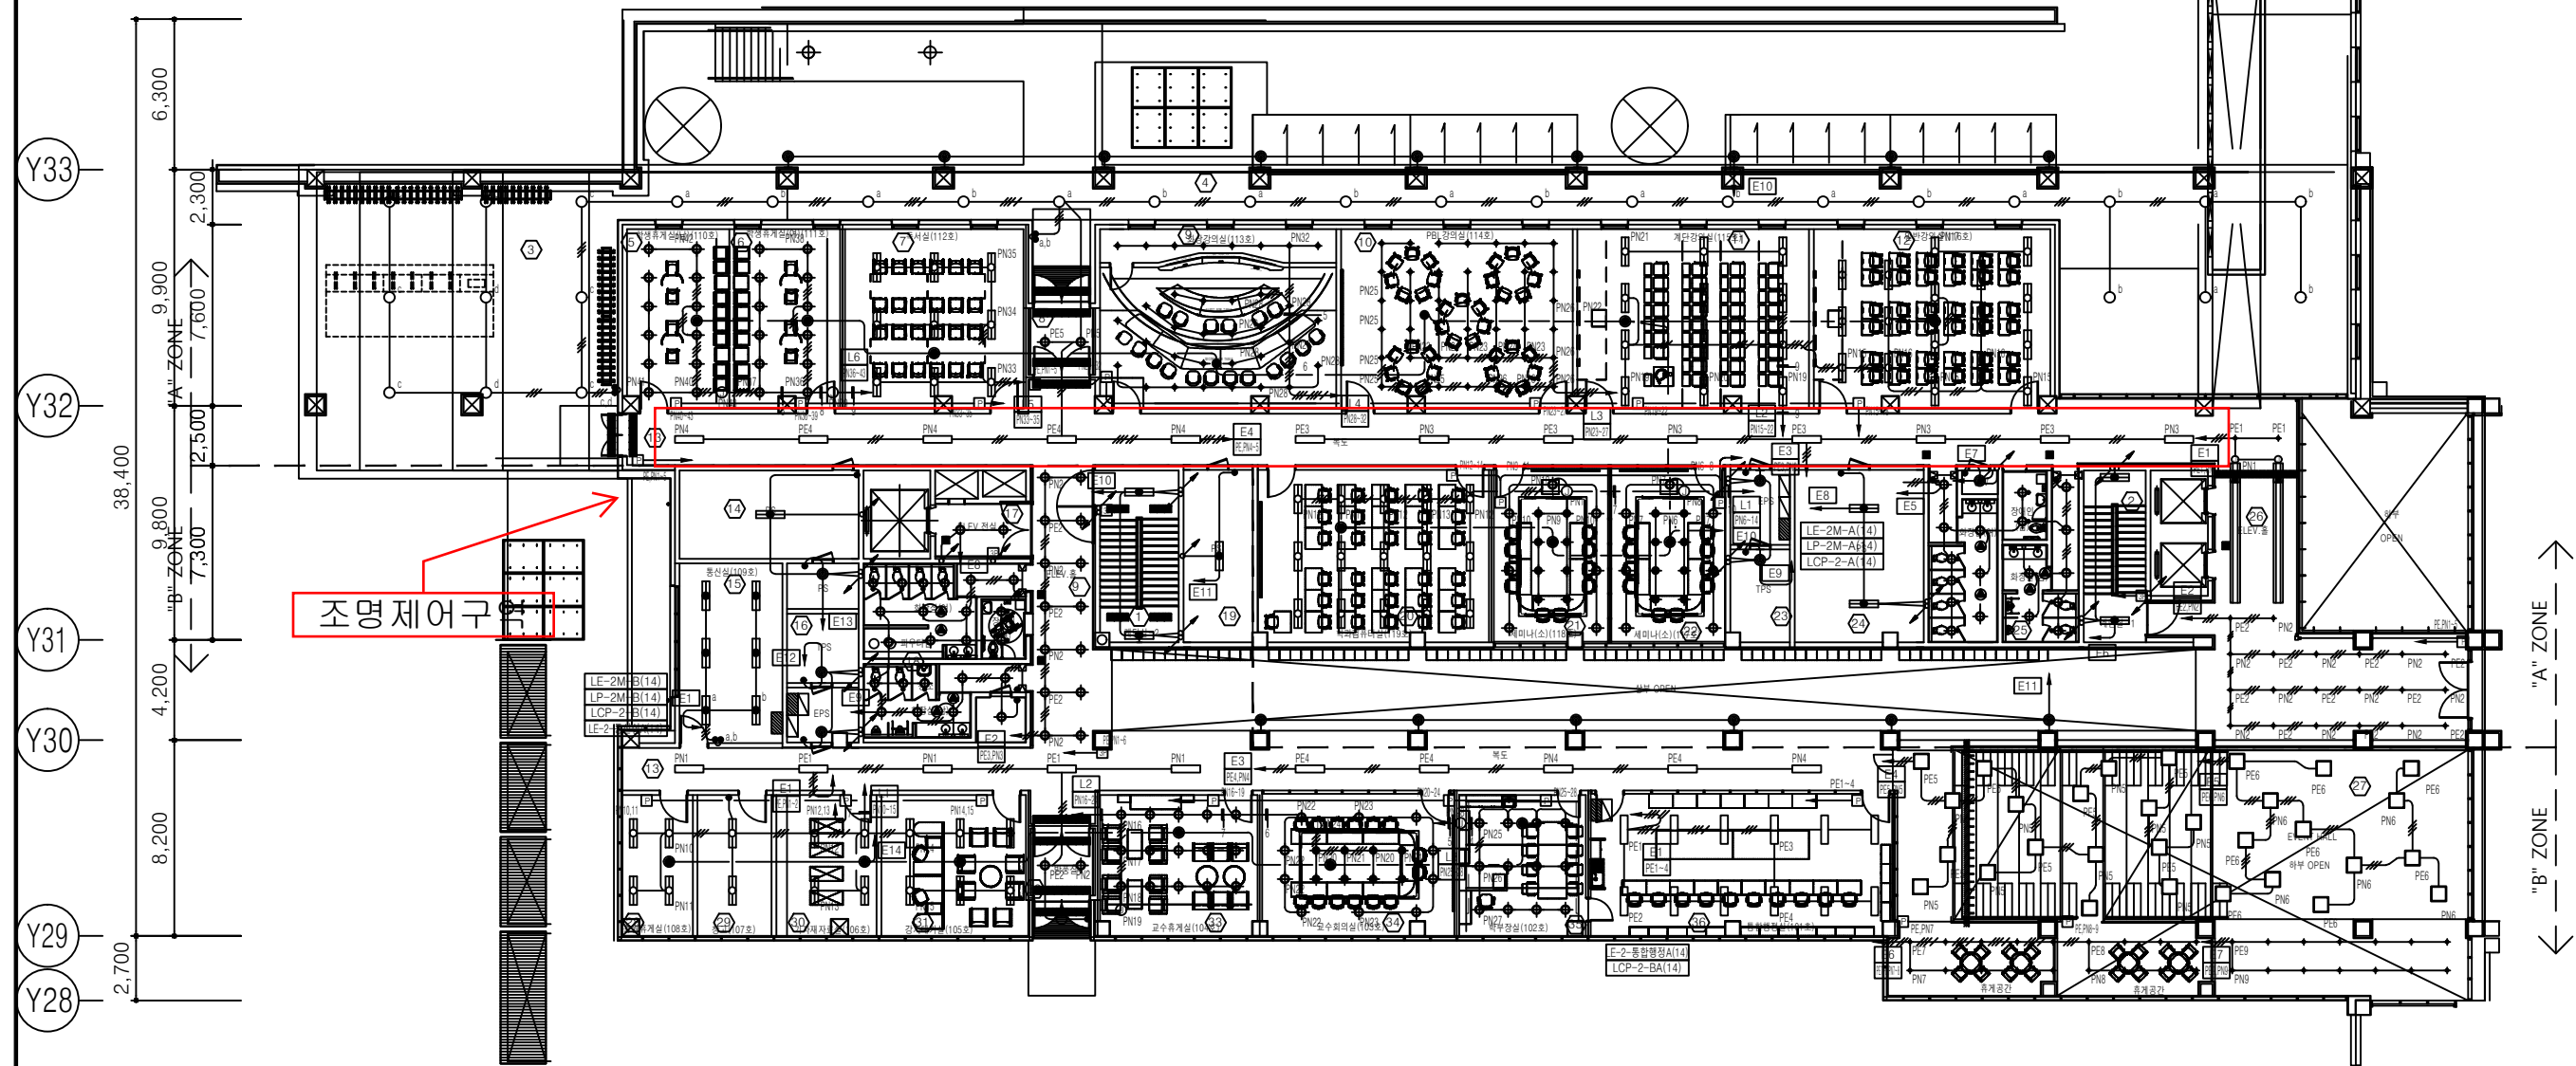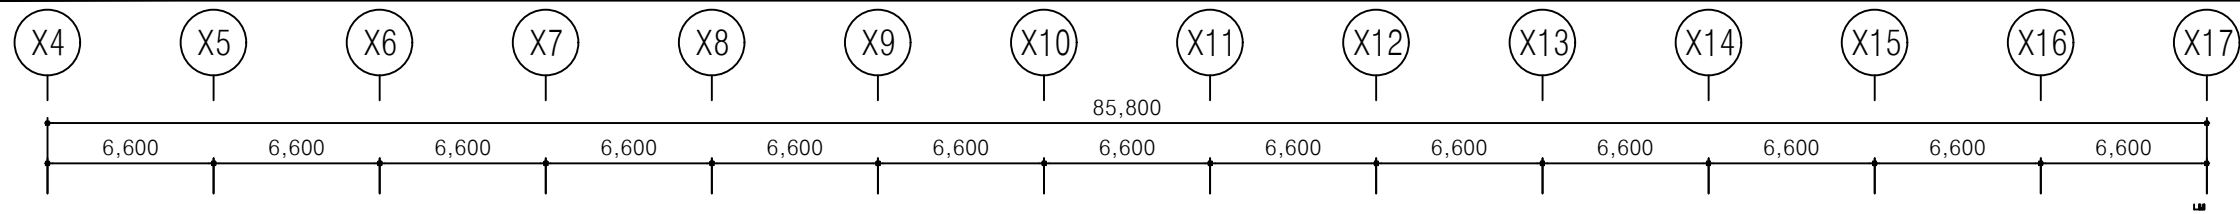

로봇공학부 1층 전등설비 평면도  
축척 A1: 1/150, A3: 1/300

| 3                    |          |               |     |     |      |
|----------------------|----------|---------------|-----|-----|------|
| 2                    |          |               |     |     |      |
| 1                    | 14.11.18 | 실명/호실 수정      |     |     |      |
| REV                  | DATE     | DESCRIPTION   | DRN | CHK | APR  |
| DRAWING TITLE        |          |               |     |     |      |
| 로봇공학부<br>1층 전등설비 평면도 |          |               |     |     |      |
| APPROVED             |          |               |     |     |      |
| CHECKED1             |          |               |     |     |      |
| CHECKED2             |          |               |     |     |      |
| DRAWN                |          |               |     |     |      |
| PROJECT NO.          |          |               |     |     |      |
| SCALE                |          |               |     |     |      |
| A1                   | A3       | APPROVAL DATE |     |     |      |
| 1/150                | 1/300    | 2014.04       |     |     |      |
| DRAWING NO.          |          |               |     |     | REV. |
| E-14-0703            |          |               |     |     |      |


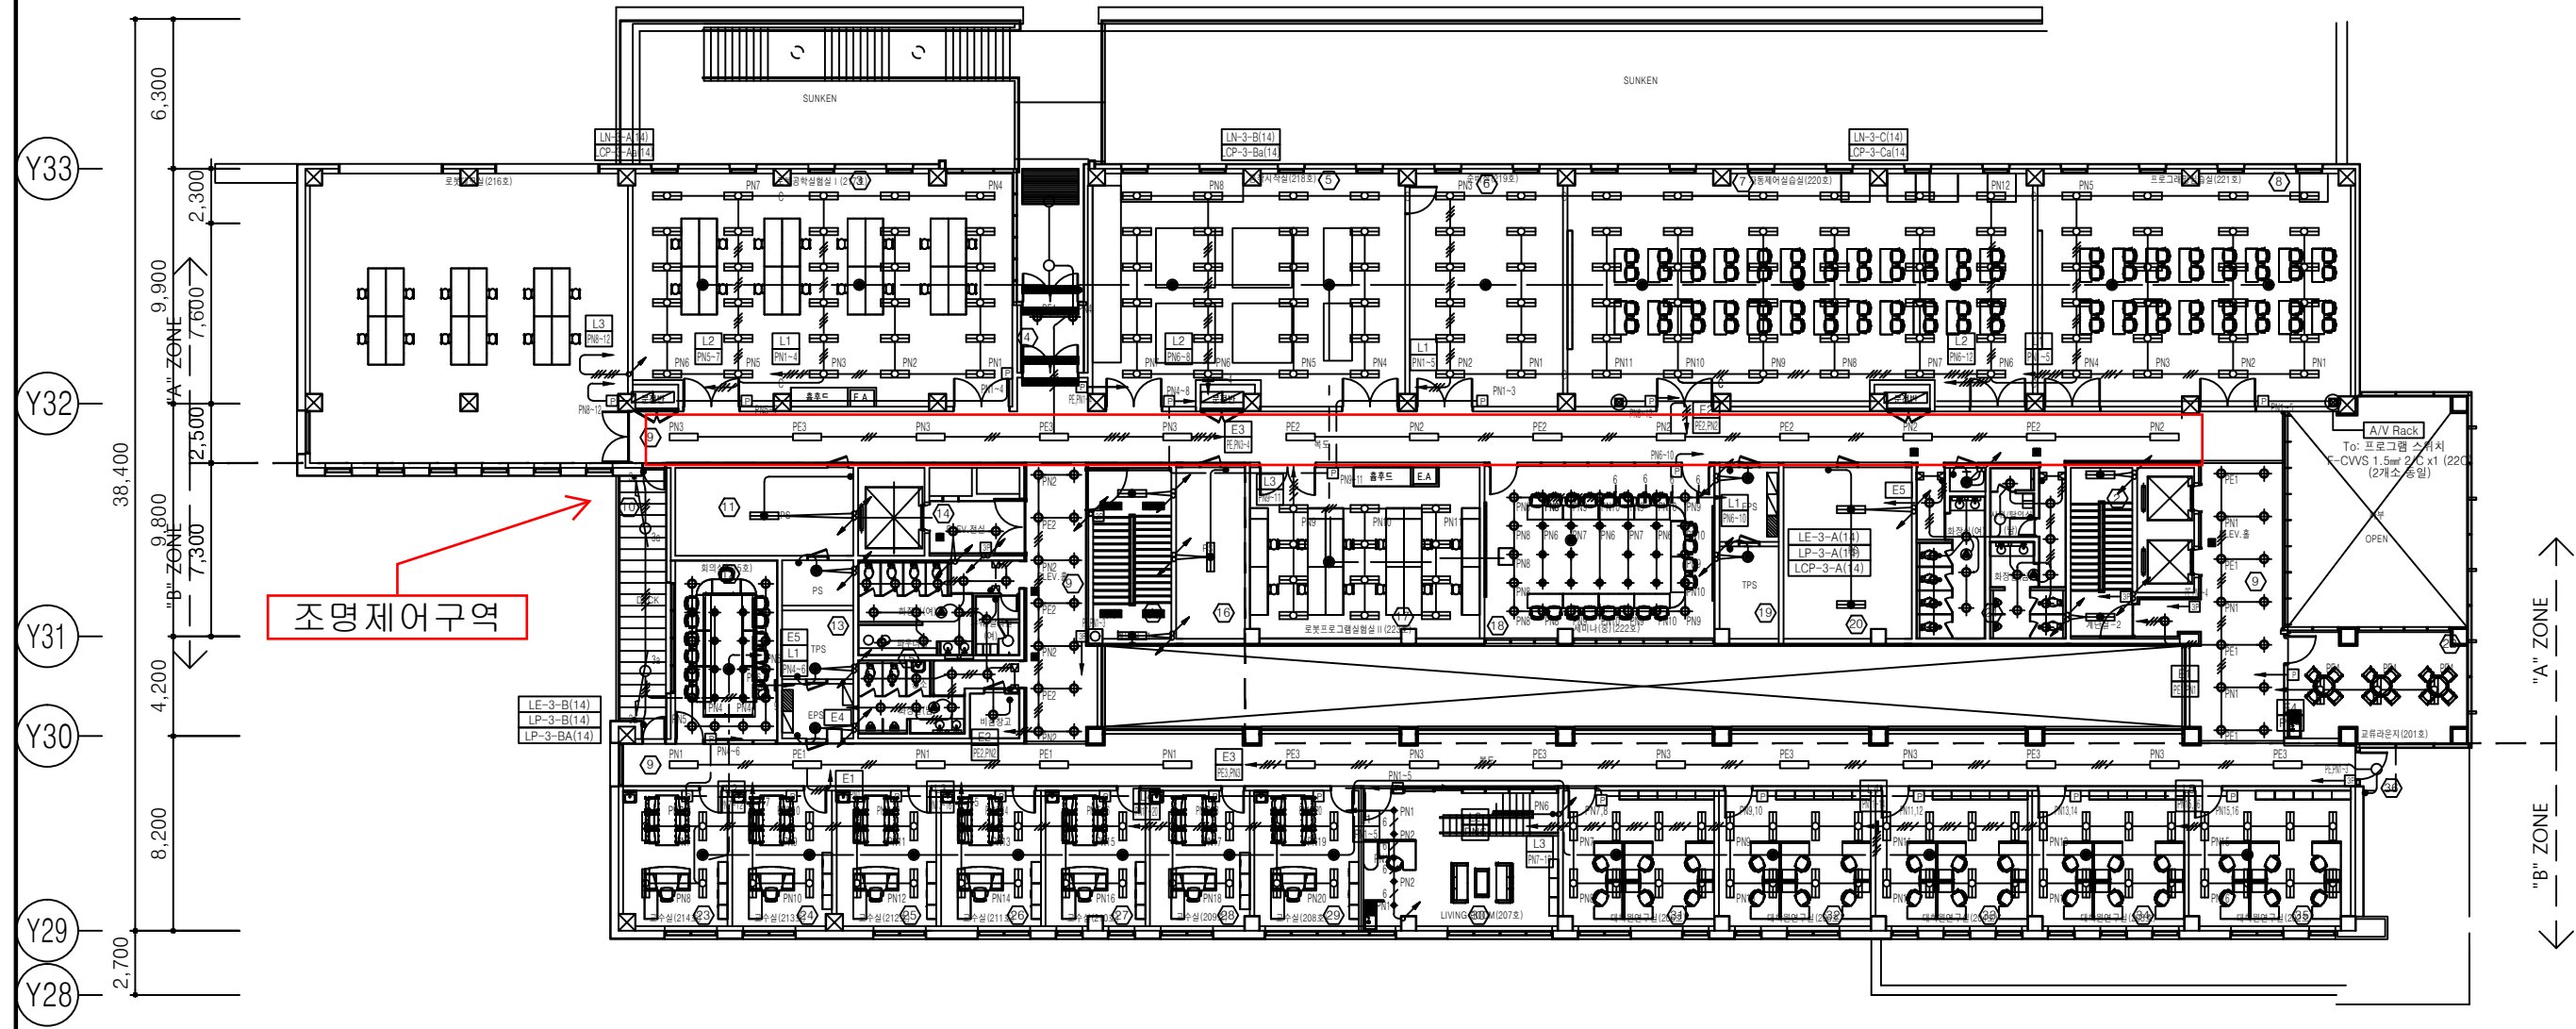
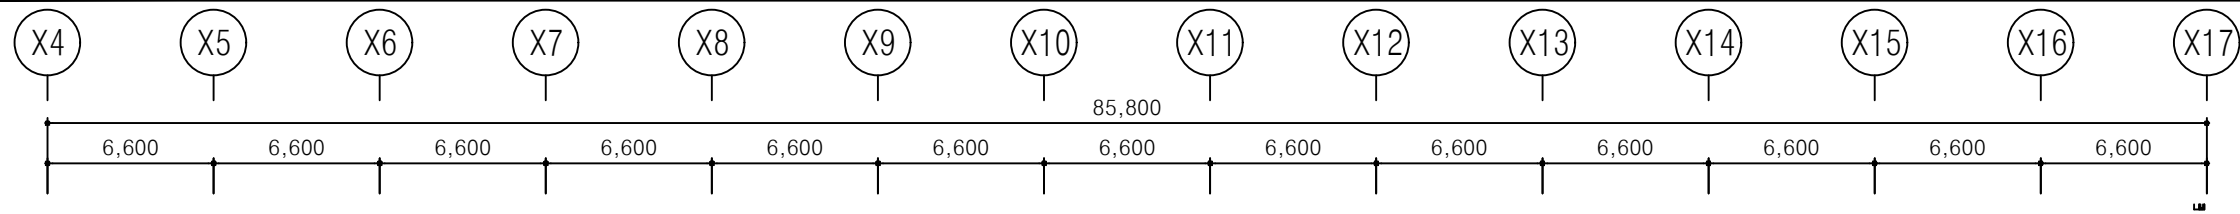


조명 제어구역

로봇공학부 2층 전등설비 평면도  
축척 A1: 1/150, A3: 1/300

| 3                    |          |               |     |     |      |
|----------------------|----------|---------------|-----|-----|------|
| 2                    |          |               |     |     |      |
| 1                    | 14.11.18 | 실명/호실 수정      |     |     |      |
| REV                  | DATE     | DESCRIPTION   | DRN | CHK | APR  |
| DRAWING TITLE        |          |               |     |     |      |
| 로봇공학부<br>2층 전등설비 평면도 |          |               |     |     |      |
| APPROVED             |          |               |     |     |      |
| CHECKED1             |          |               |     |     |      |
| CHECKED2             |          |               |     |     |      |
| DRAWN                |          |               |     |     |      |
| PROJECT NO.          |          |               |     |     |      |
| SCALE                |          |               |     |     |      |
| A1                   | A3       | APPROVAL DATE |     |     |      |
| 1/150                | 1/300    | 2014.04       |     |     |      |
| DRAWING NO.          |          |               |     |     | REV. |
| E-14-0704            |          |               |     |     |      |



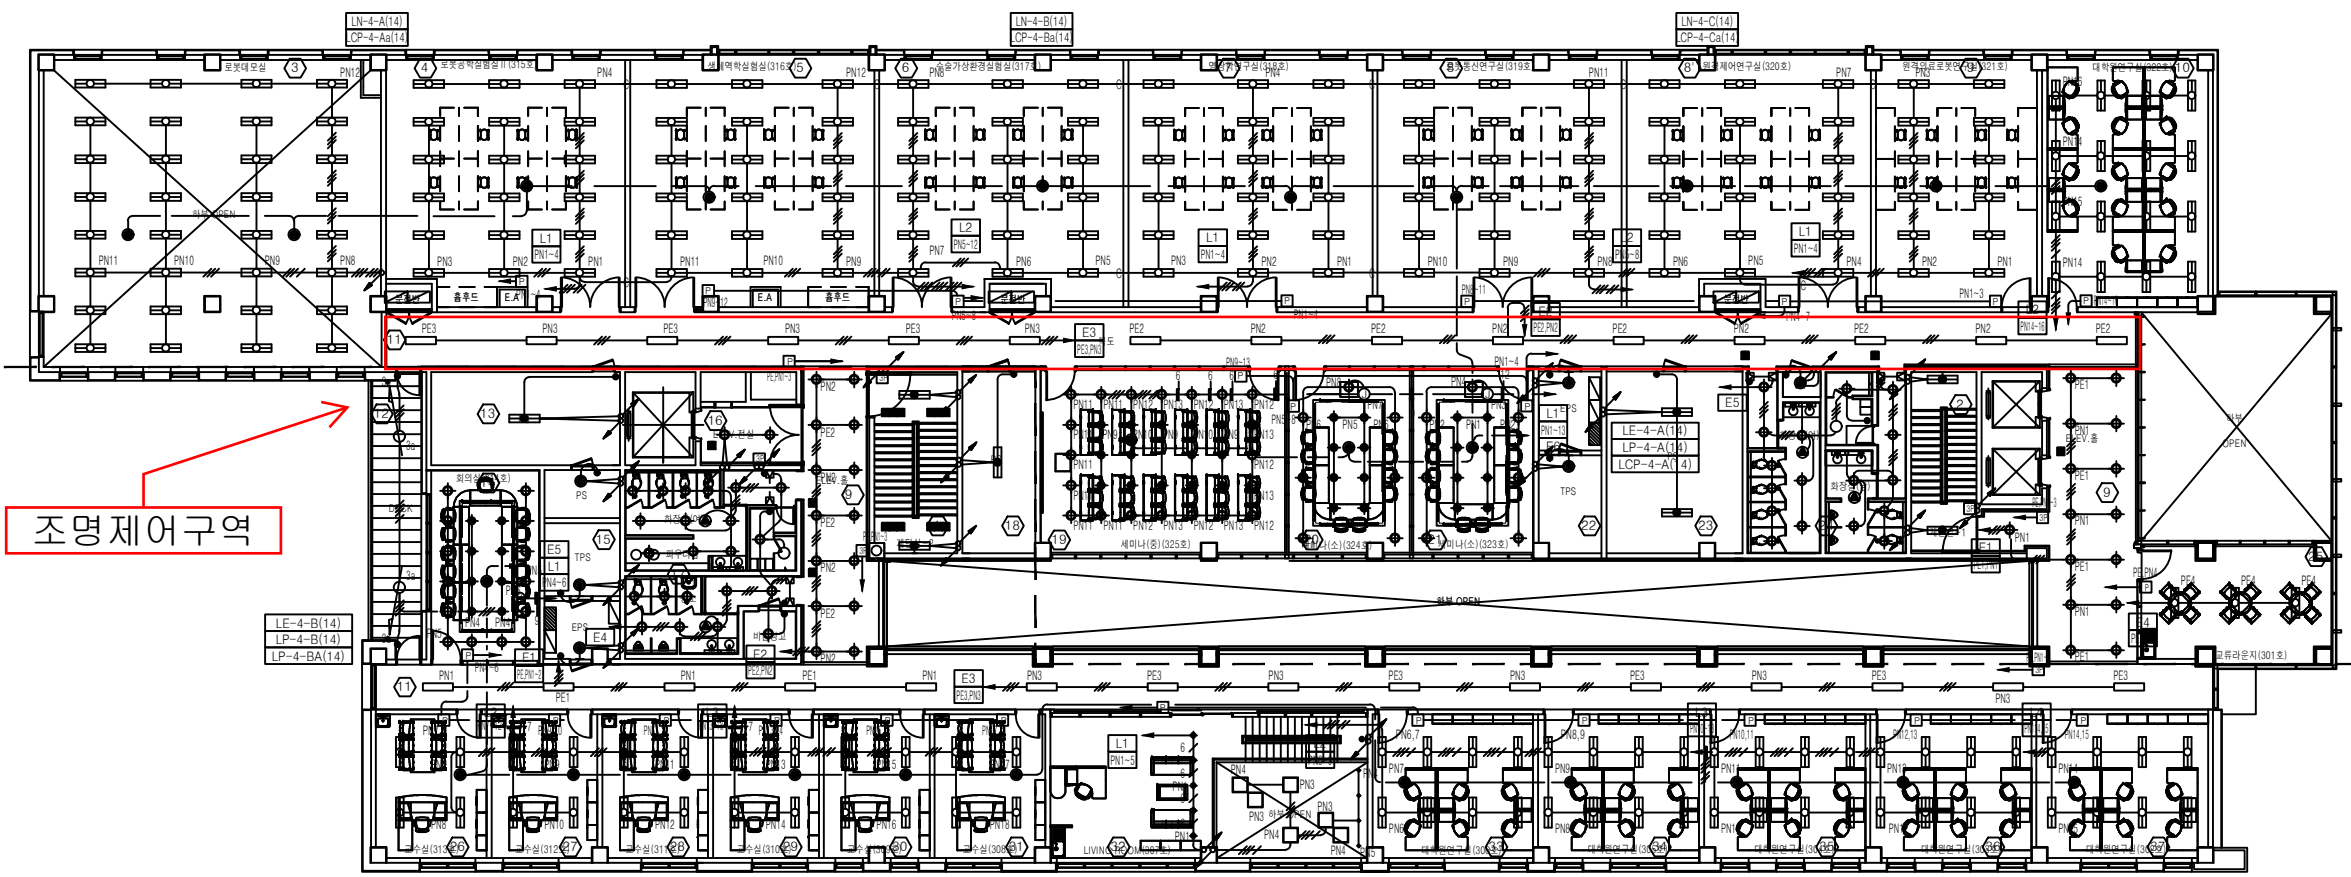
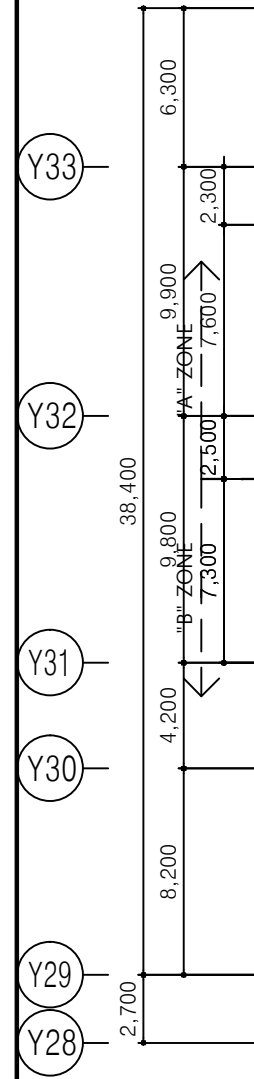
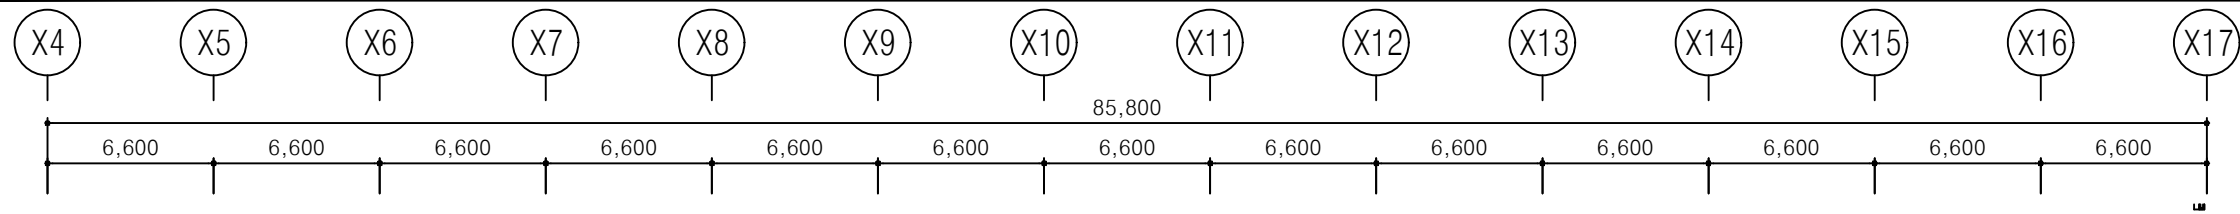


조명 제어구역

"A" ZONE  
"B" ZONE

로봇공학부 3층 전등설비 평면도  
축척 A1: 1/150, A3: 1/300

| 3                    |          |             |               |      |     |
|----------------------|----------|-------------|---------------|------|-----|
| 2                    |          |             |               |      |     |
| 1                    | 14.11.18 | 실명/호실 수정    |               |      |     |
| REV                  | DATE     | DESCRIPTION | DRN           | CHK  | APR |
| DRAWING TITLE        |          |             |               |      |     |
| 로봇공학부<br>3층 전등설비 평면도 |          |             |               |      |     |
| APPROVED             |          |             |               |      |     |
| CHECKED1             |          |             |               |      |     |
| CHECKED2             |          |             |               |      |     |
| DRAWN                |          |             |               |      |     |
| PROJECT NO.          |          |             |               |      |     |
| SCALE                |          |             | APPROVAL DATE |      |     |
| A1                   | A3       |             | 2014.04       |      |     |
| 1/150                | 1/300    |             |               |      |     |
| DRAWING NO.          |          |             |               | REV. |     |
| E-14-0705            |          |             |               | 01   |     |

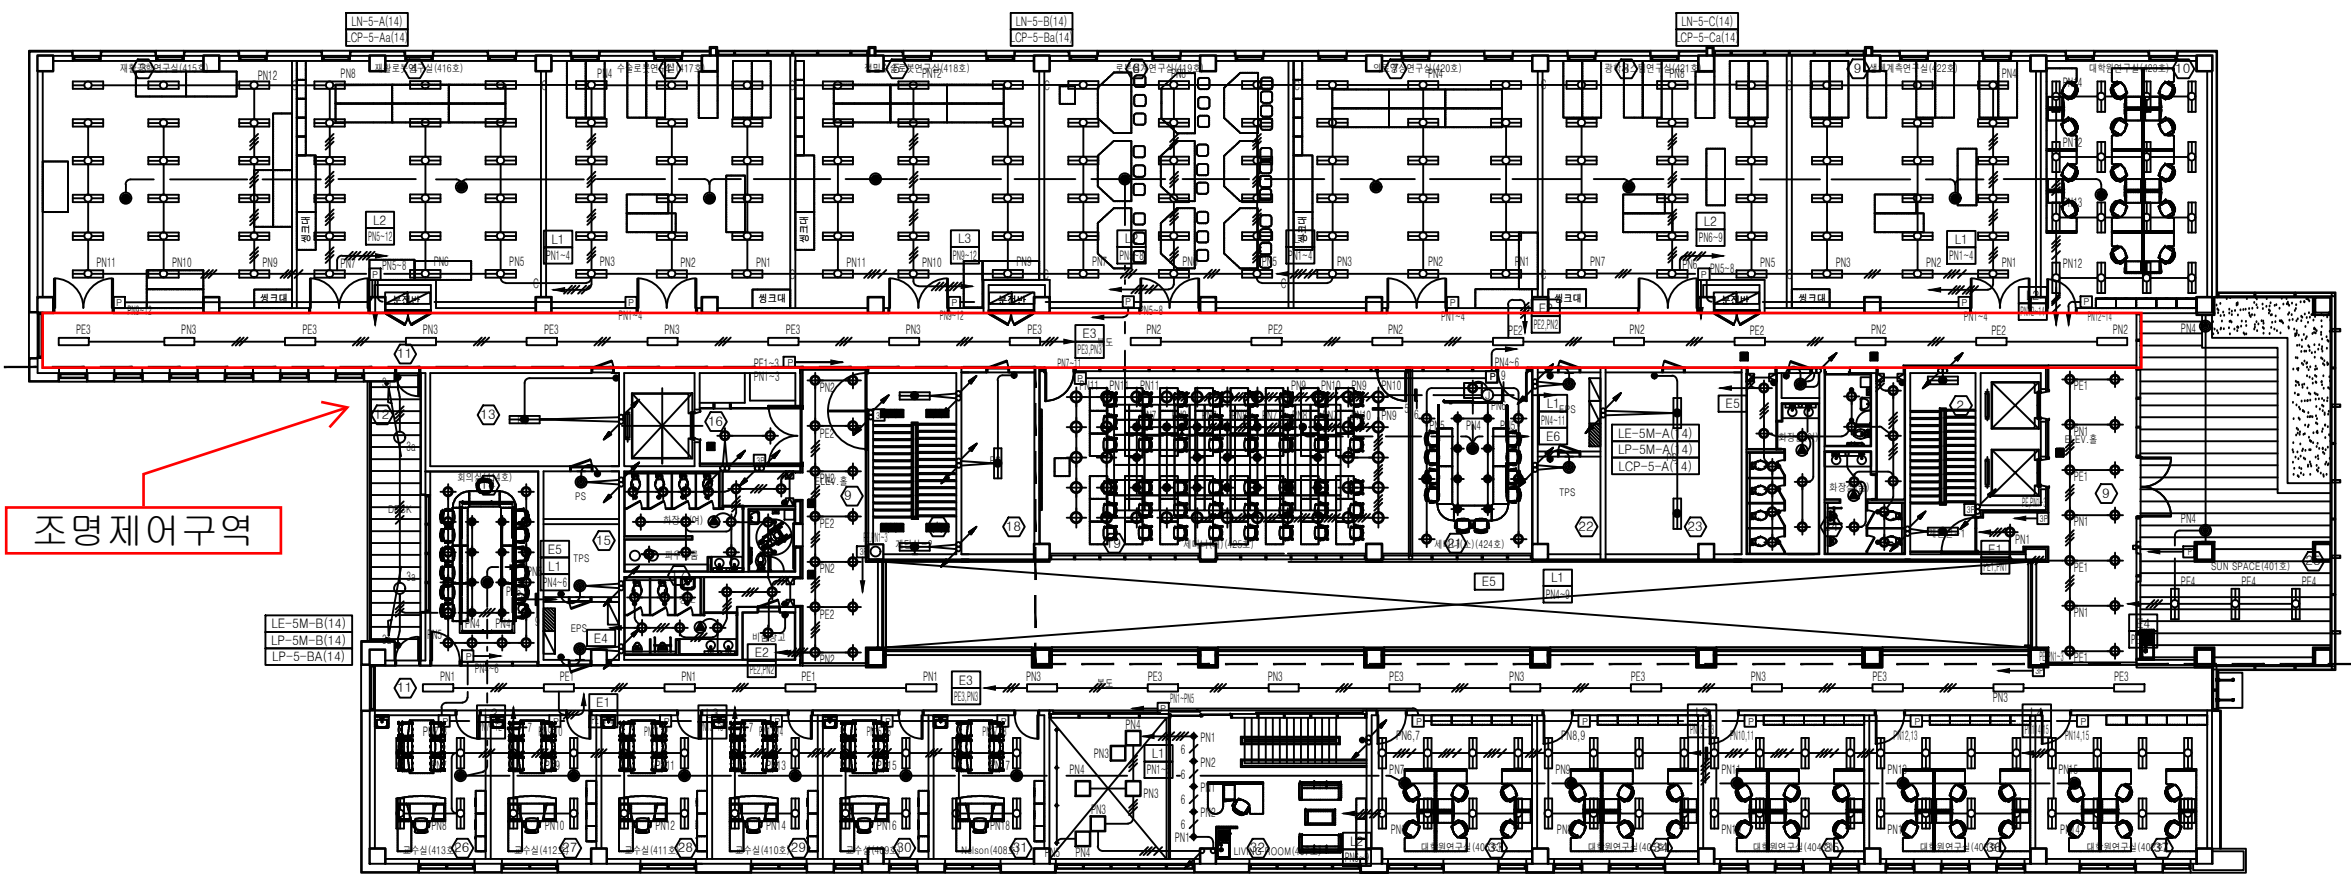
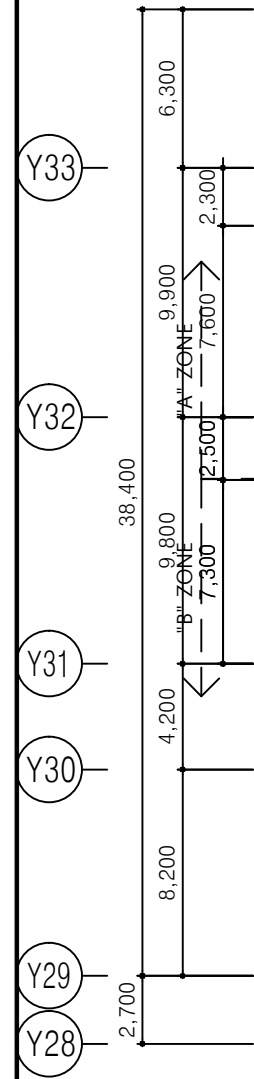
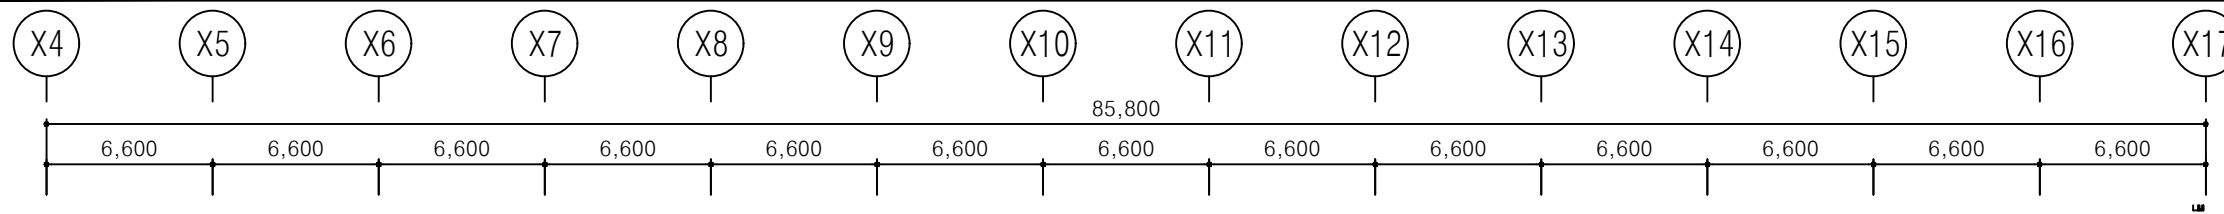


조명 제어구역

"A" ZONE  
"B" ZONE

로봇공학부 4층 전등설비 평면도  
축척 A1: 1/150, A3: 1/300

| 3                    |          |               |     |     |      |
|----------------------|----------|---------------|-----|-----|------|
| 2                    |          |               |     |     |      |
| 1                    | 14.11.18 | 설명/호설 수정      |     |     |      |
| REV                  | DATE     | DESCRIPTION   | DRN | CHK | APR  |
| DRAWING TITLE        |          |               |     |     |      |
| 로봇공학부<br>4층 전등설비 평면도 |          |               |     |     |      |
| APPROVED             |          |               |     |     |      |
| CHECKED1             |          |               |     |     |      |
| CHECKED2             |          |               |     |     |      |
| DRAWN                |          |               |     |     |      |
| PROJECT NO.          |          |               |     |     |      |
| SCALE                |          | APPROVAL DATE |     |     |      |
| A1                   | A3       | 2014.04       |     |     |      |
| 1/150                | 1/300    |               |     |     |      |
| DRAWING NO.          |          |               |     |     | REV. |
| E-14-0706            |          |               |     |     |      |

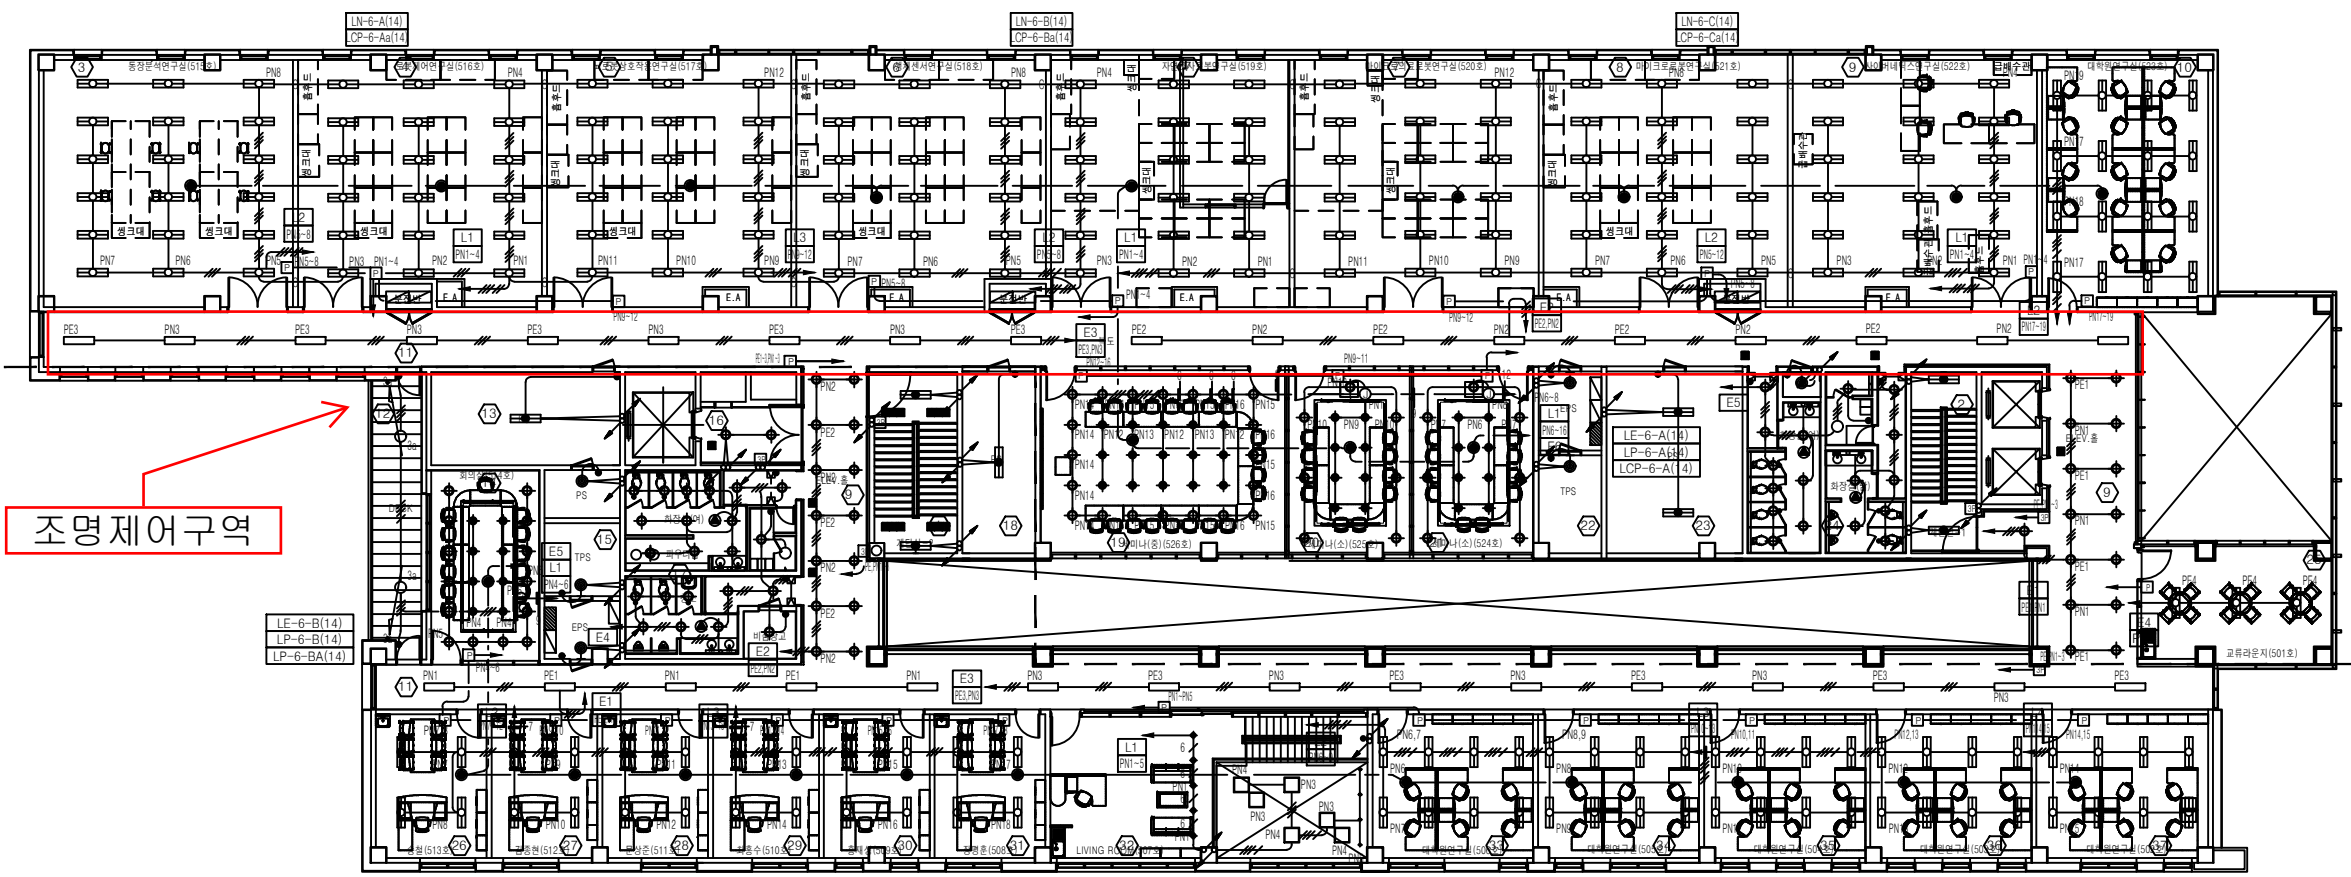
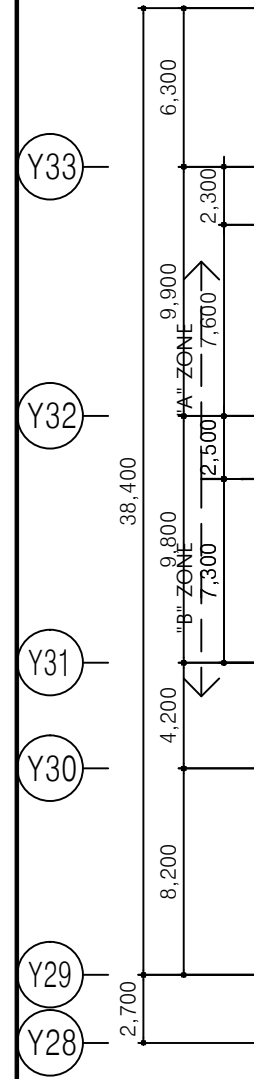
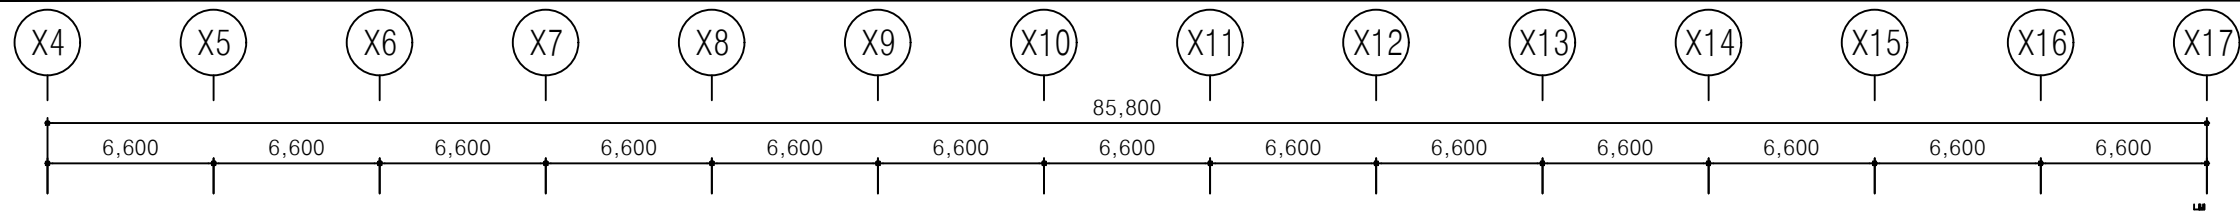


조명 제어구역

"A" ZONE  
"B" ZONE

로봇공학부 5층 전등설비 평면도  
축척 A1: 1/150, A3: 1/300

| 3                    |          |               |     |     |      |
|----------------------|----------|---------------|-----|-----|------|
| 2                    |          |               |     |     |      |
| 1                    | 14.11.18 | 실명/호실 수정      |     |     |      |
| REV                  | DATE     | DESCRIPTION   | DRN | CHK | APR  |
| DRAWING TITLE        |          |               |     |     |      |
| 로봇공학부<br>5층 전등설비 평면도 |          |               |     |     |      |
| APPROVED             |          |               |     |     |      |
| CHECKED1             |          |               |     |     |      |
| CHECKED2             |          |               |     |     |      |
| DRAWN                |          |               |     |     |      |
| PROJECT NO.          |          |               |     |     |      |
| SCALE                |          |               |     |     |      |
| A1                   | A3       | APPROVAL DATE |     |     |      |
| 1/150                | 1/300    | 2014.04       |     |     |      |
| DRAWING NO.          |          |               |     |     | REV. |
| E-14-0707            |          |               |     |     |      |


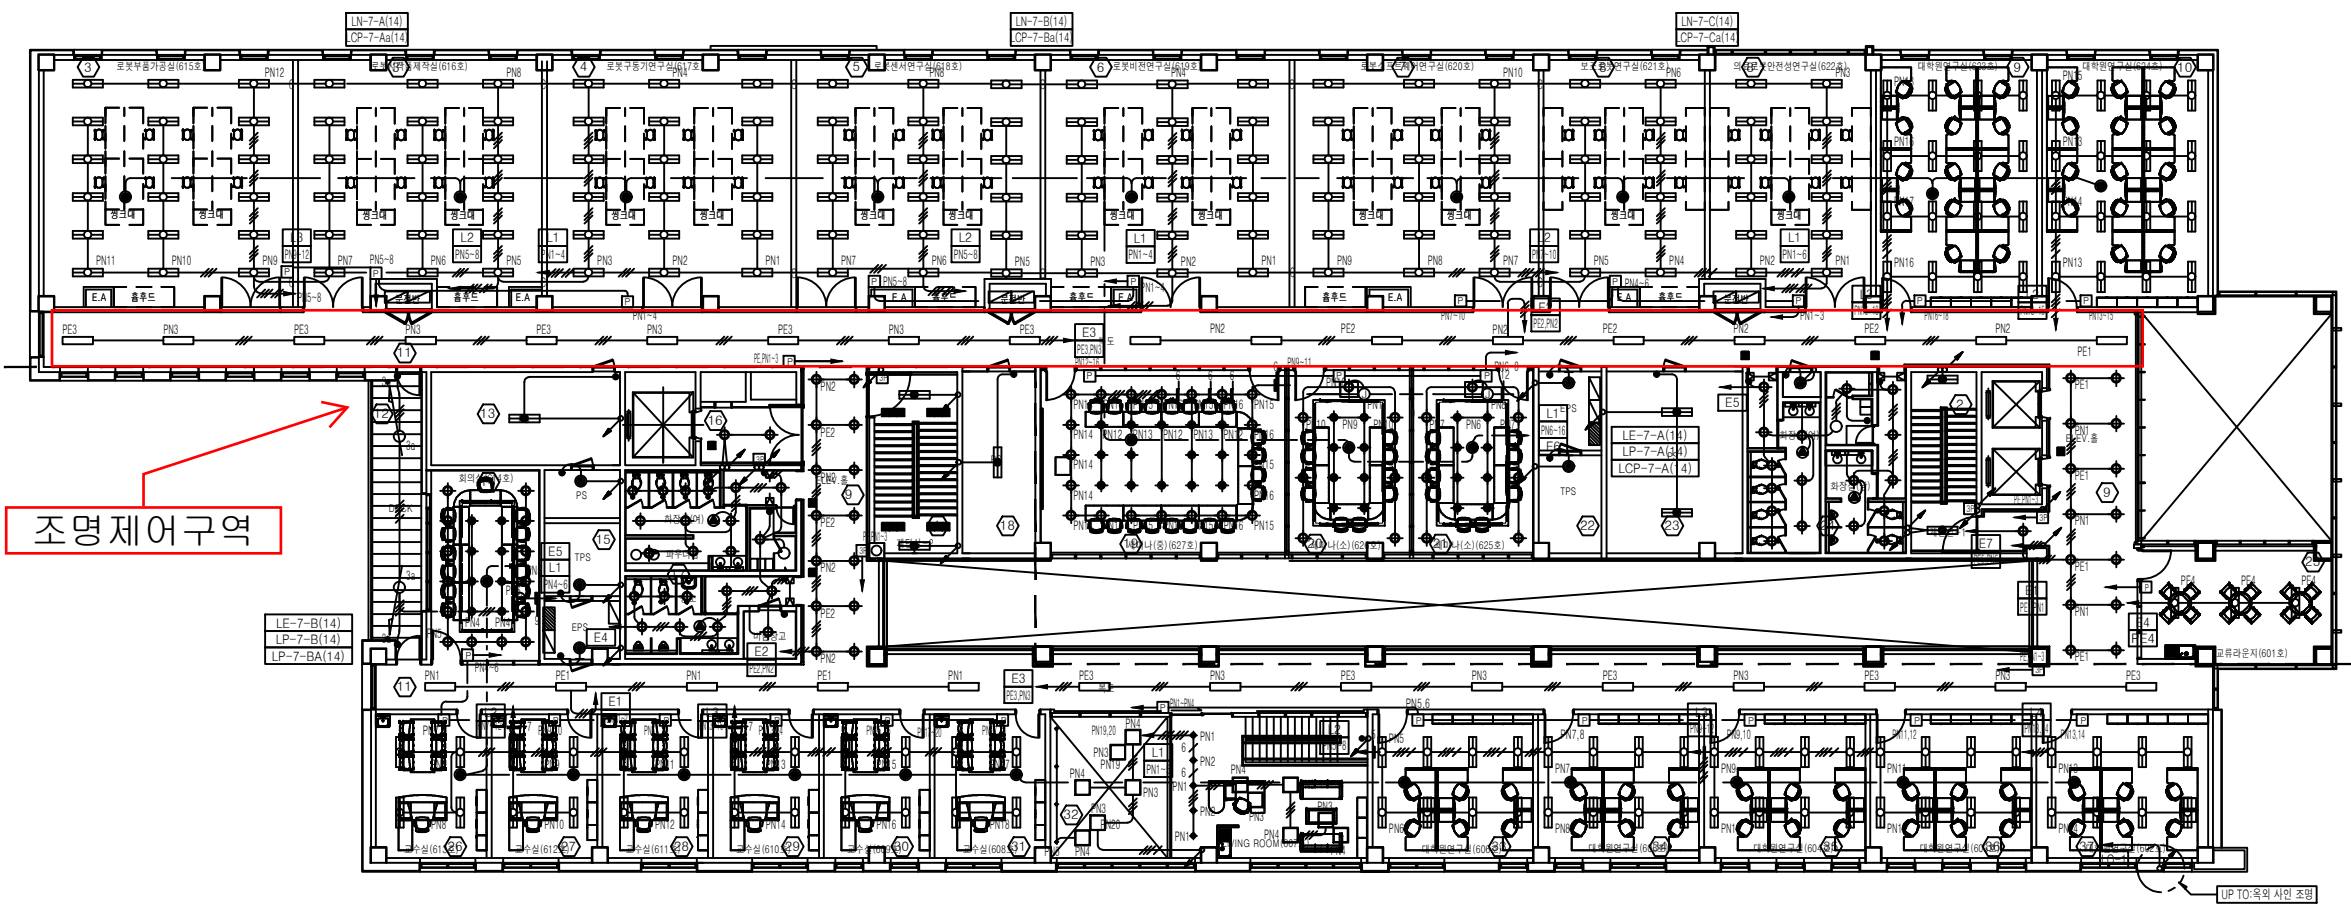
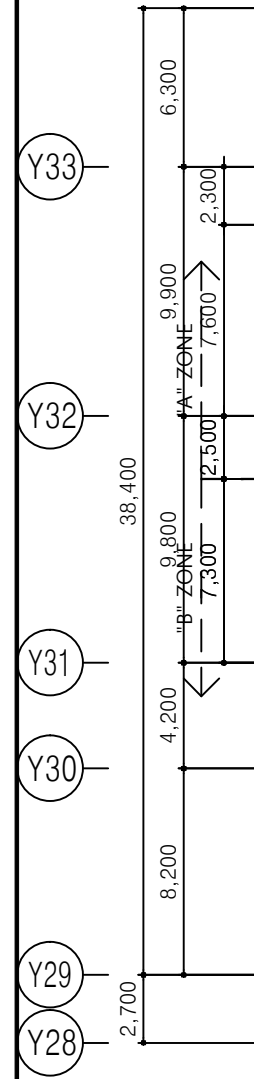
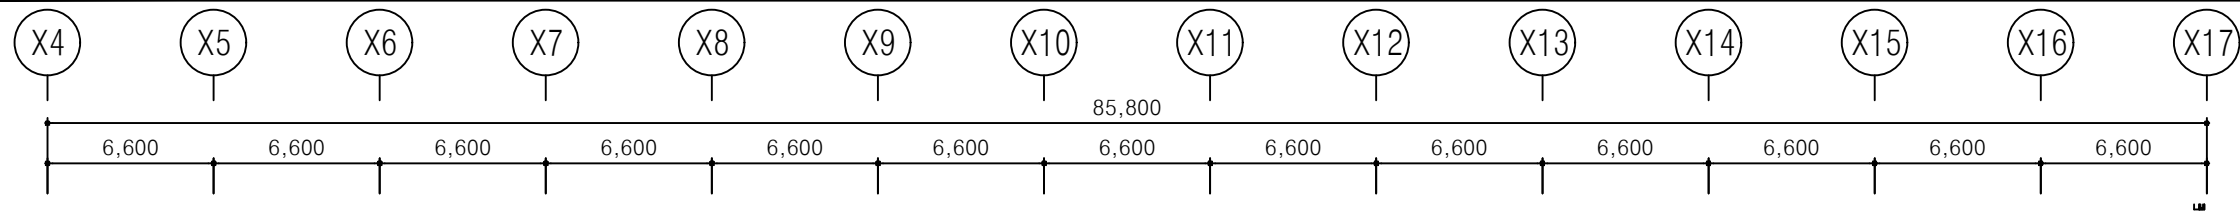


"A" ZONE  
"B" ZONE

로봇공학부 6층 전등설비 평면도  
축척 A1: 1/150, A3: 1/300

| 3                    |          |               |     |     |      |
|----------------------|----------|---------------|-----|-----|------|
| 2                    |          |               |     |     |      |
| 1                    | 14.11.18 | 실명/호실 수정      |     |     |      |
| REV                  | DATE     | DESCRIPTION   | DRN | CHK | APR  |
| DRAWING TITLE        |          |               |     |     |      |
| 로봇공학부<br>6층 전등설비 평면도 |          |               |     |     |      |
| APPROVED             |          |               |     |     |      |
| CHECKED1             |          |               |     |     |      |
| CHECKED2             |          |               |     |     |      |
| DRAWN                |          |               |     |     |      |
| PROJECT NO.          |          |               |     |     |      |
| SCALE                |          |               |     |     |      |
| A1                   | A3       | APPROVAL DATE |     |     |      |
| 1/150                | 1/300    | 2014.04       |     |     |      |
| DRAWING NO.          |          |               |     |     | REV. |
| E-14-0708            |          |               |     |     |      |



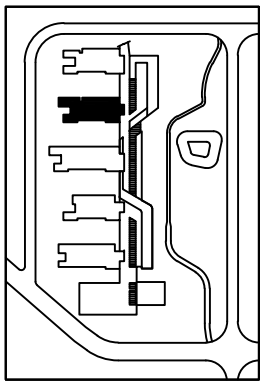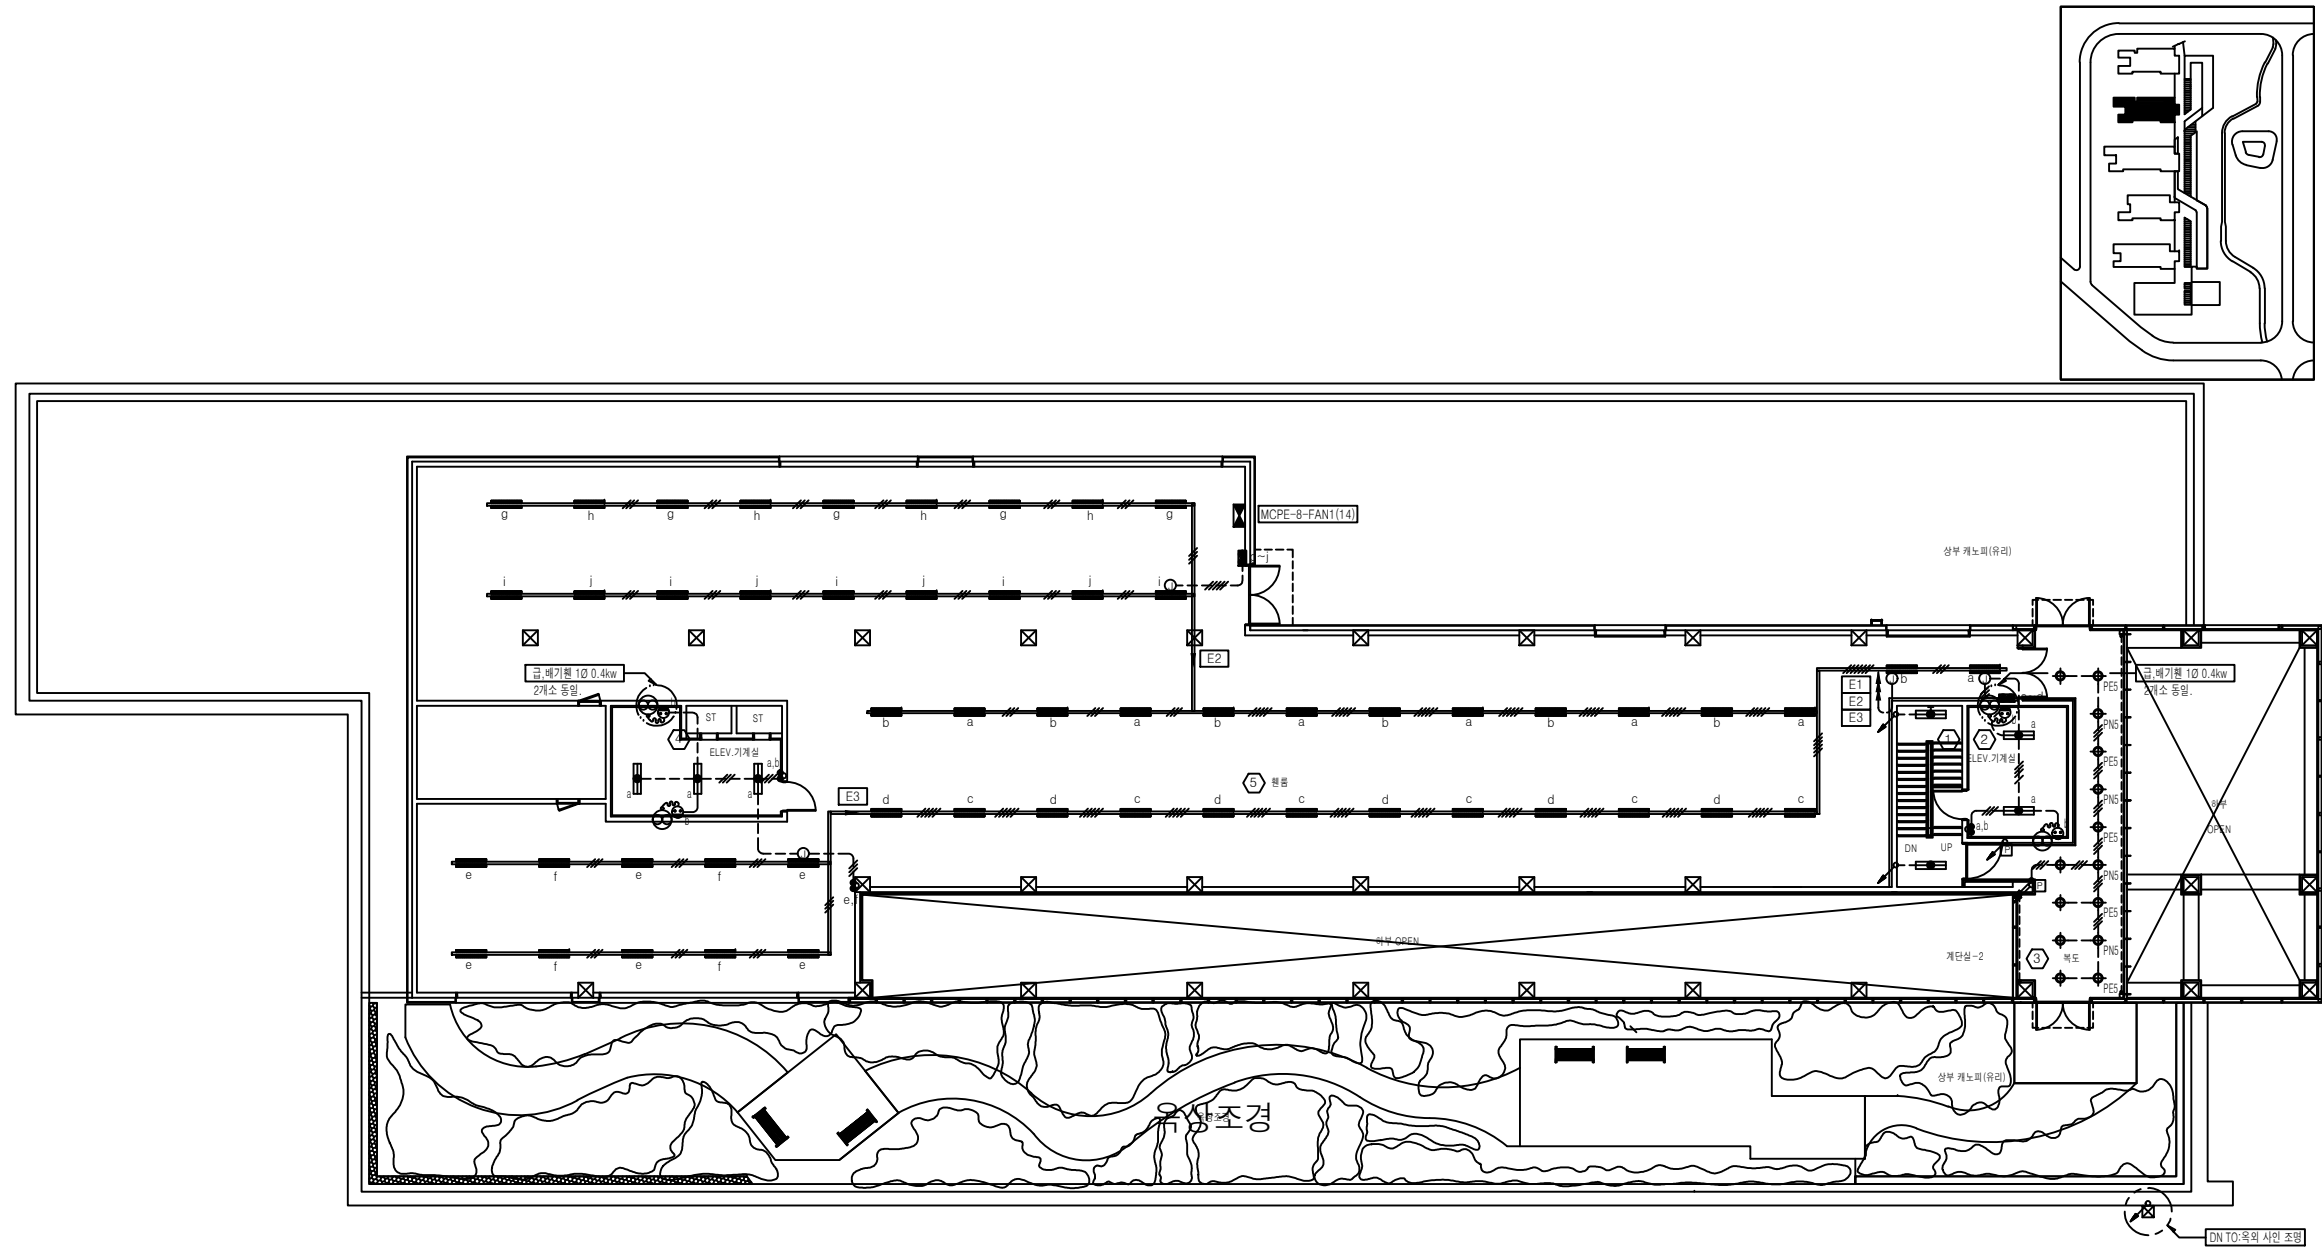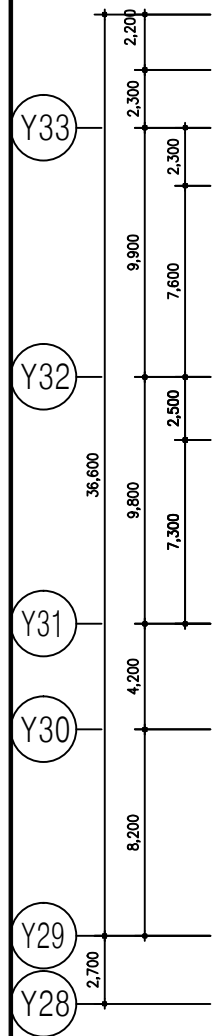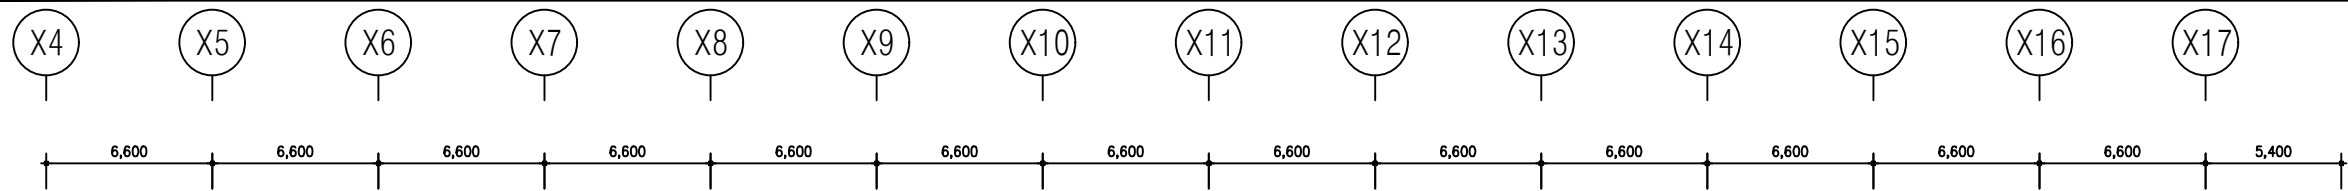

|     |          |             |     |     |     |
|-----|----------|-------------|-----|-----|-----|
| 3   |          |             |     |     |     |
| 2   |          |             |     |     |     |
| 1   | 14.11.18 | 실명/호실 수정    |     |     |     |
| REV | DATE     | DESCRIPTION | DRN | CHK | APR |

DRAWING TITLE

로봇공학부  
7층 전등설비 평면도

APPROVED

CHECKED1

CHECKED2

DRAWN

PROJECT NO.

|       |       |               |
|-------|-------|---------------|
| SCALE | A3    | APPROVAL DATE |
| 1/150 | 1/300 | 2014.04       |

|             |      |
|-------------|------|
| DRAWING NO. | REV. |
| E-14-0709   |      |

로봇공학부 7층 전등설비 평면도  
축척 A1: 1/150, A3: 1/300